




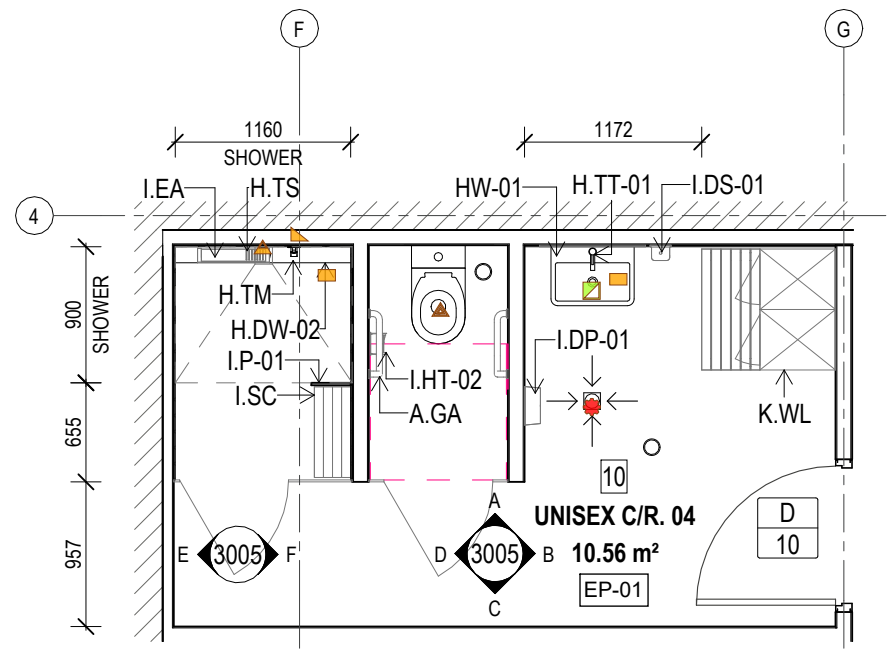


1 PLAN ROOM LAYOUT - UNISEX C/R.04
Scale: 1: 50

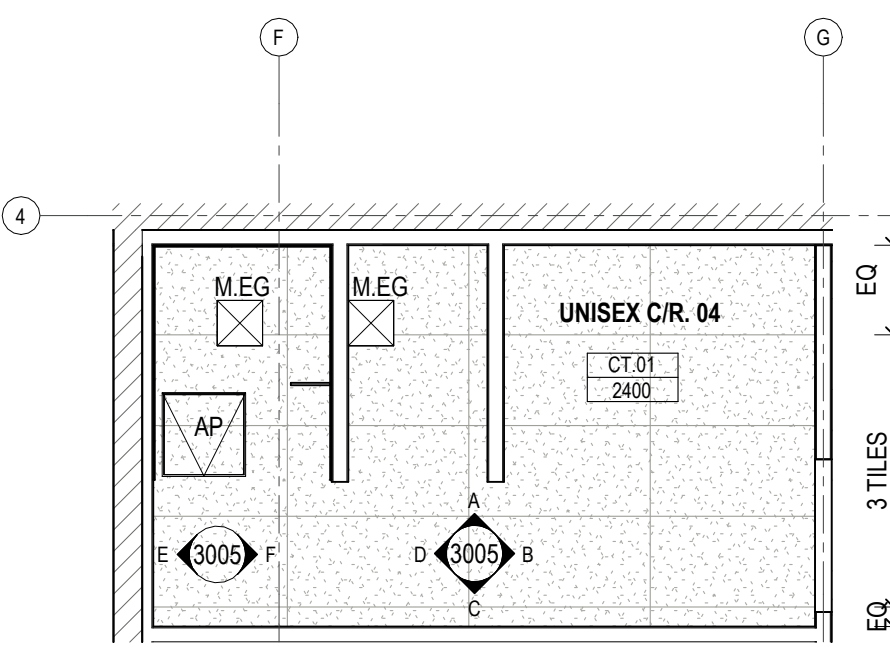


2 REFLECTED CEILING PLAN UNISEX C/R.04
Scale: 1: 50

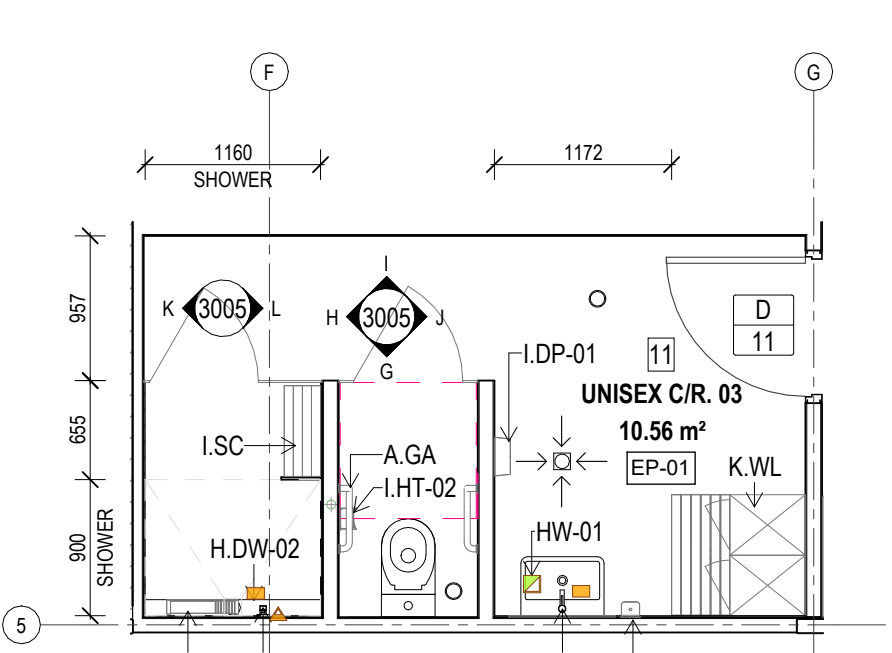


3 PLAN UNISEX C/R.03
Scale: 1: 50

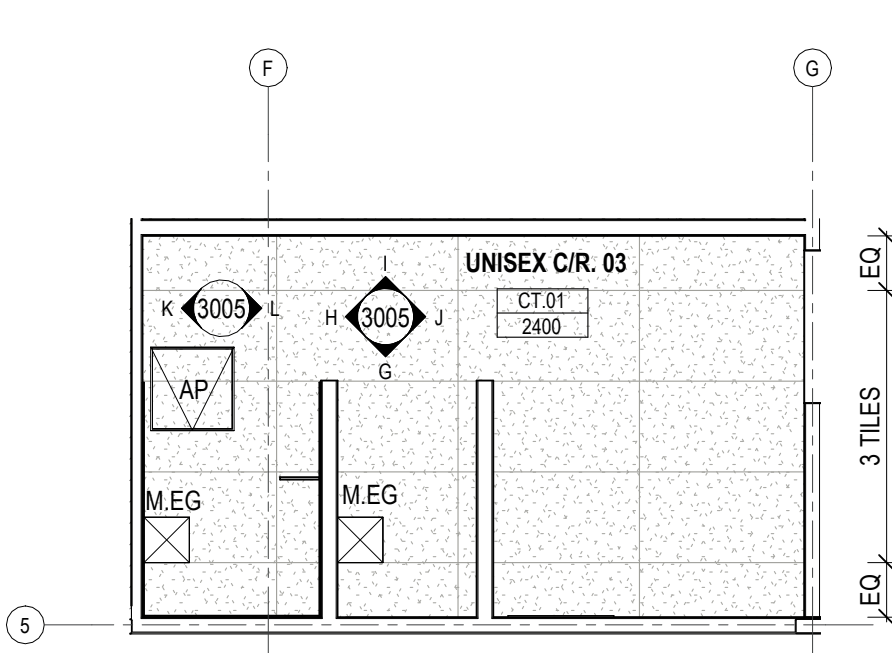


4 REFLECTED CEILING PLAN UNISEX C/R.03
Scale: 1: 50

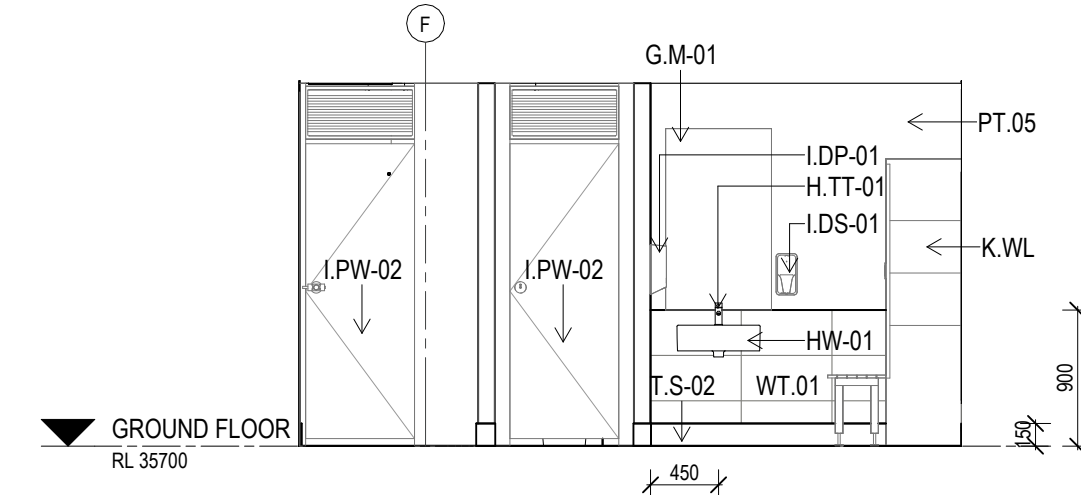


A ELEVATION UNISEX C/R.04
Scale: 1: 50

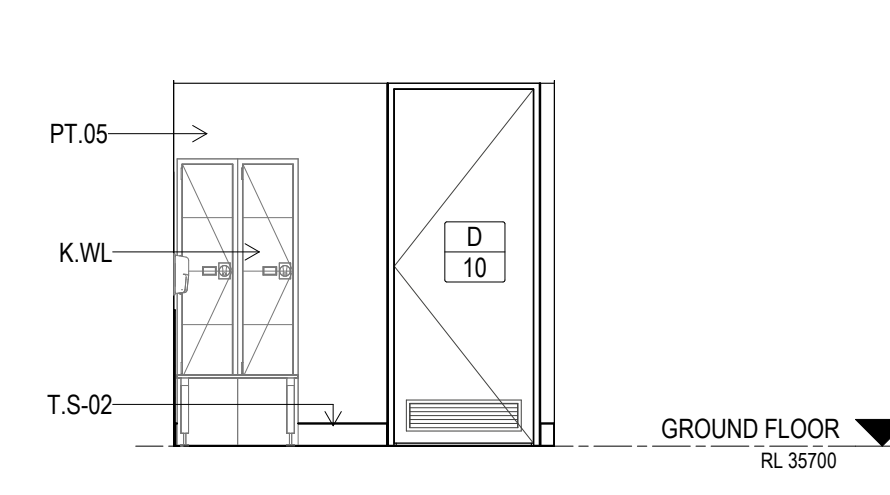


B ELEVATION UNISEX C/R.04
Scale: 1: 50

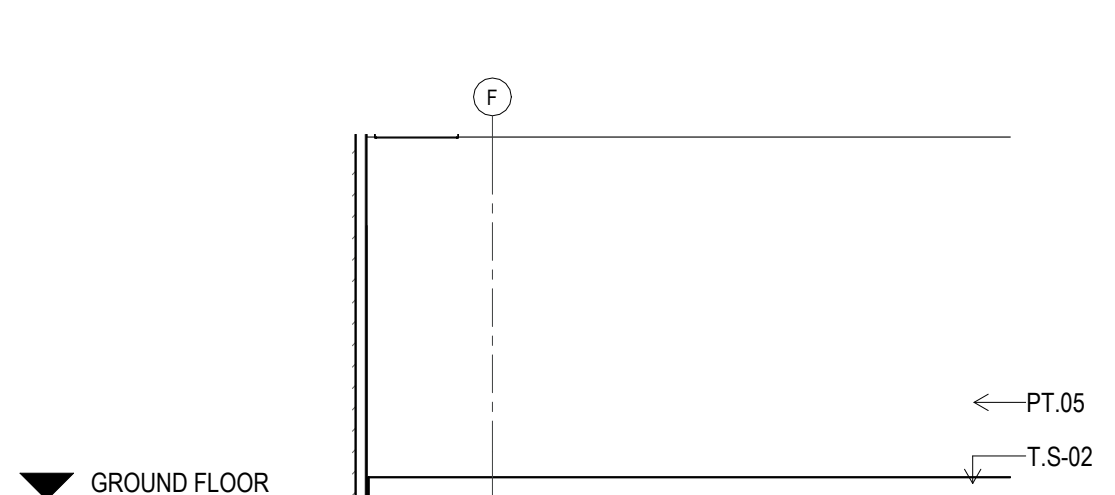


I ELEVATION UNISEX C/R.03
Scale: 1: 50

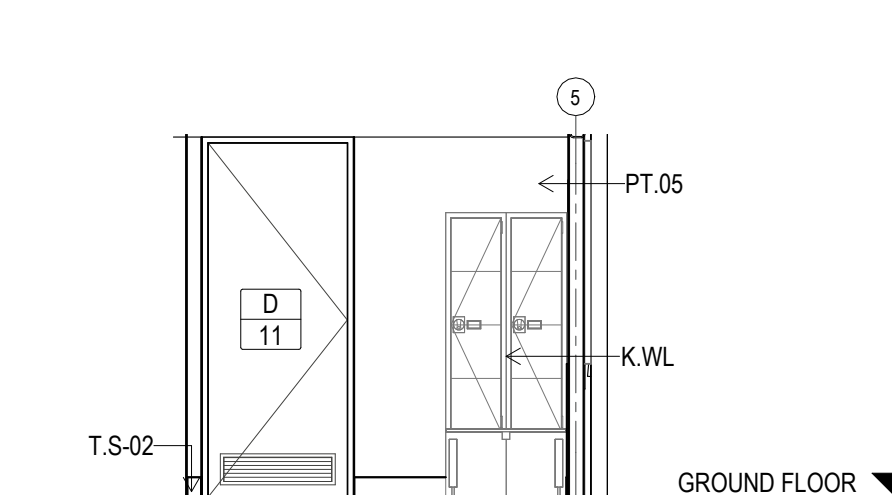


J ELEVATION UNISEX C/R.03
Scale: 1: 50

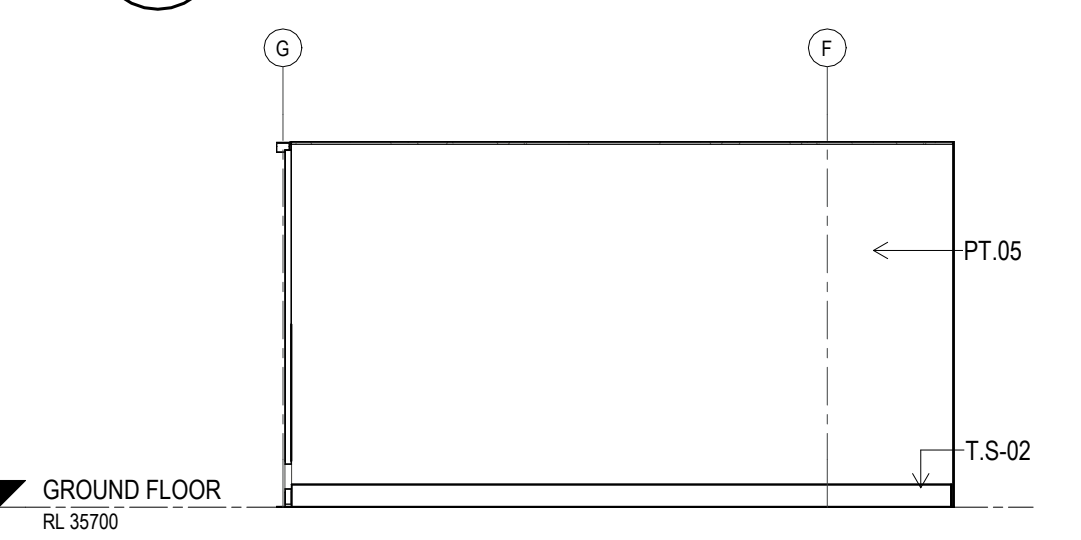


C ELEVATION UNISEX C/R.04
Scale: 1: 50

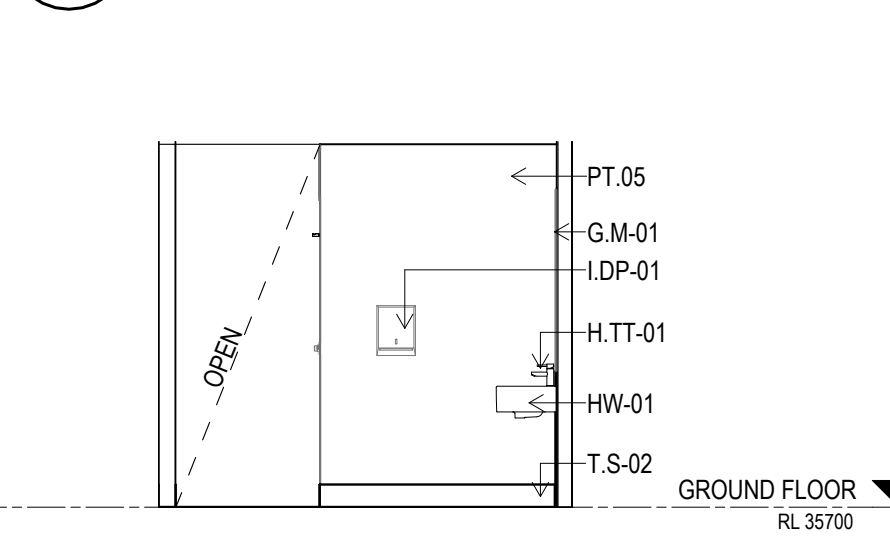


D ELEVATION UNISEX C/R.04
Scale: 1: 50

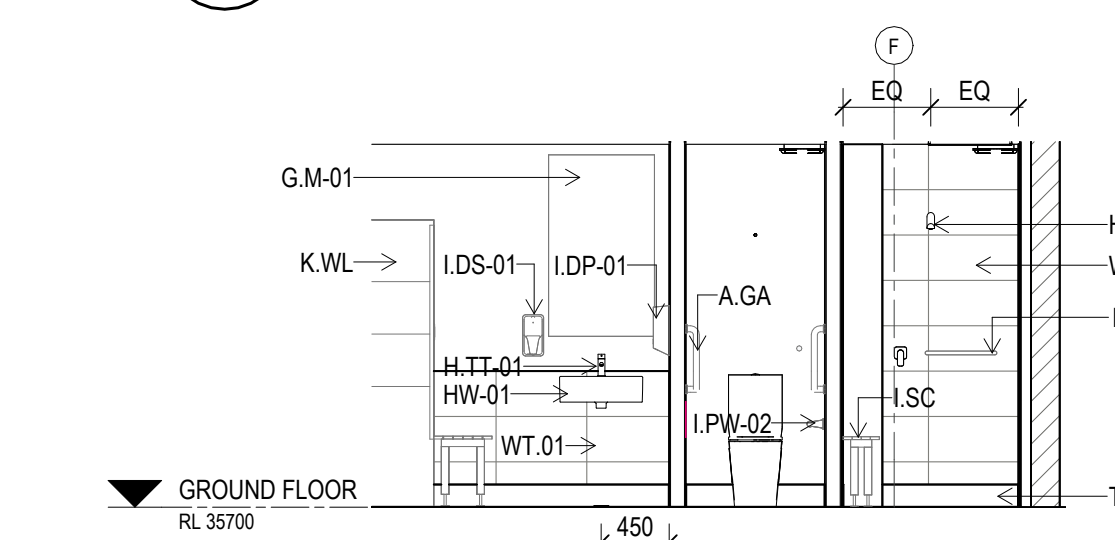


G ELEVATION UNISEX C/R.03
Scale: 1: 50

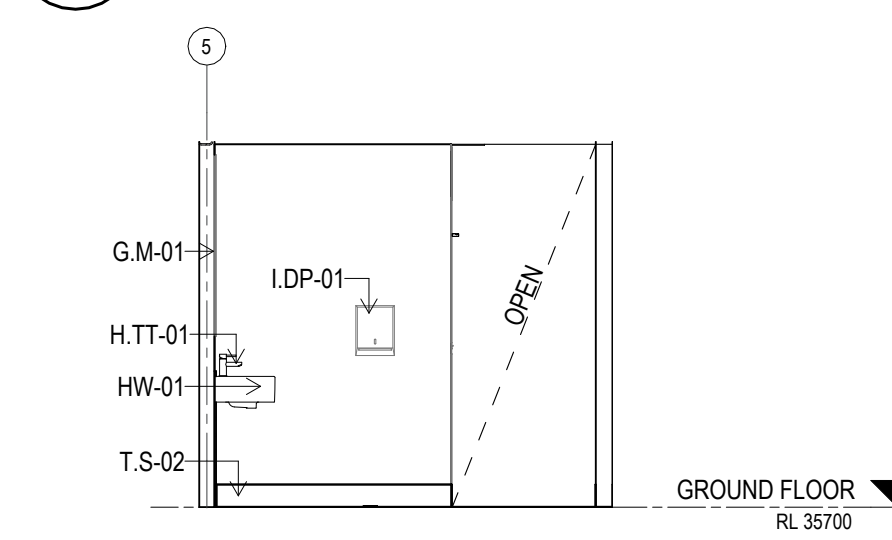


H ELEVATION UNISEX C/R.03
Scale: 1: 50

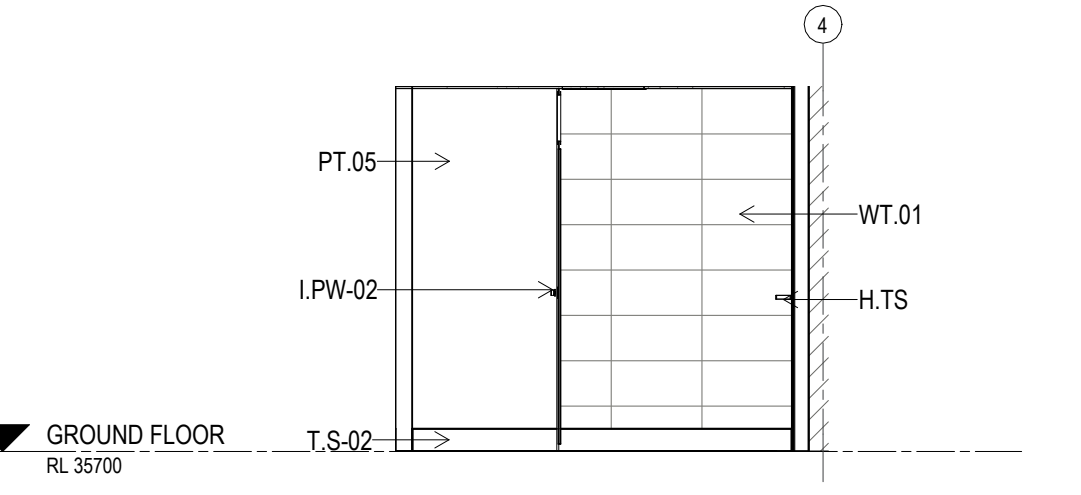


E ELEVATION UNISEX C/R.04
Scale: 1: 50

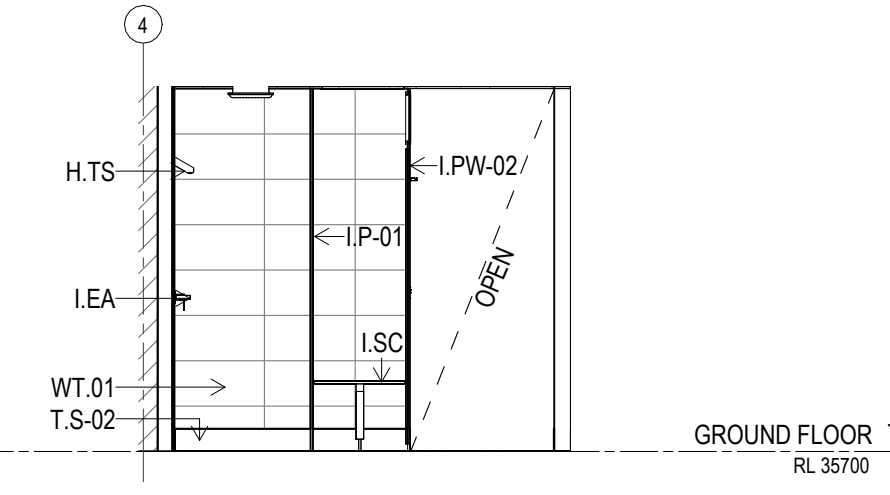


F ELEVATION UNISEX C/R.04
Scale: 1: 50

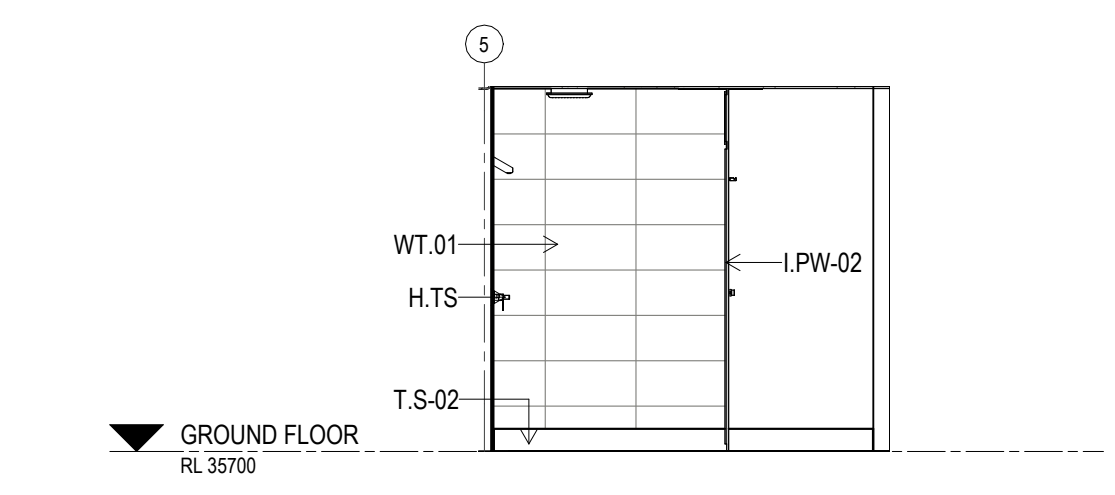


K ELEVATION UNISEX C/R.03
Scale: 1: 50

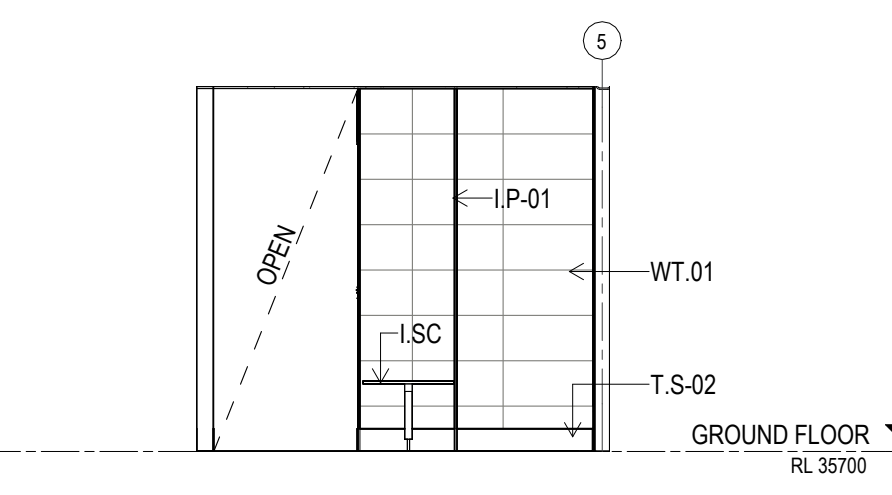


L ELEVATION UNISEX C/R.03
Scale: 1: 50

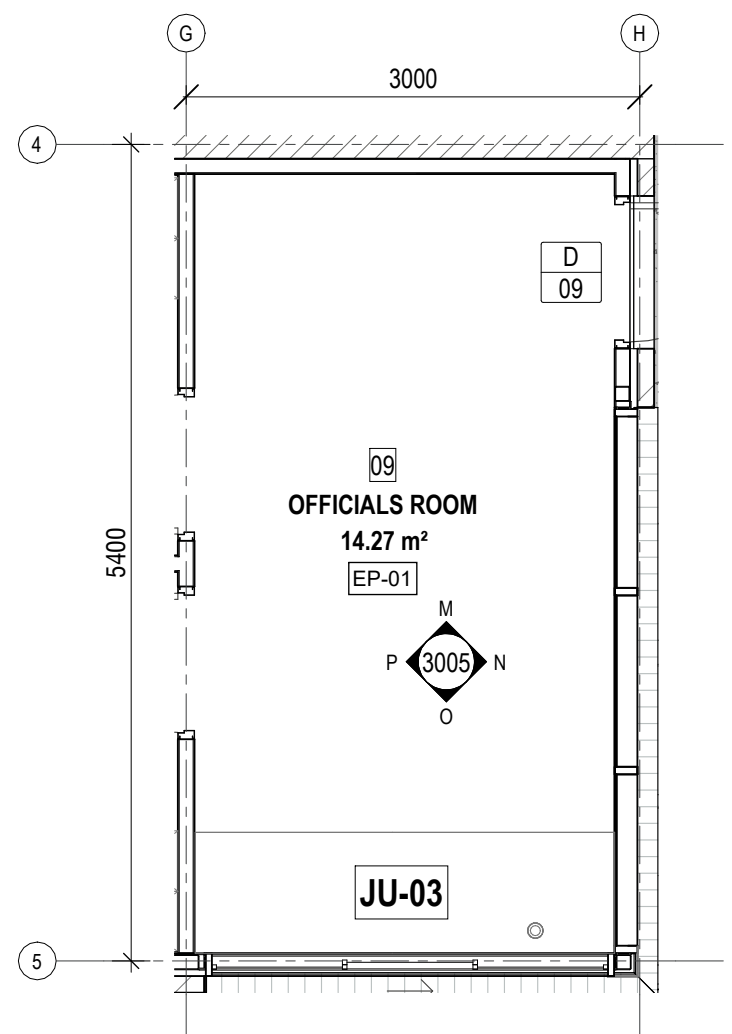


5 PLAN ROOM LAYOUT - OFFICIALS ROOM
Scale: 1: 50

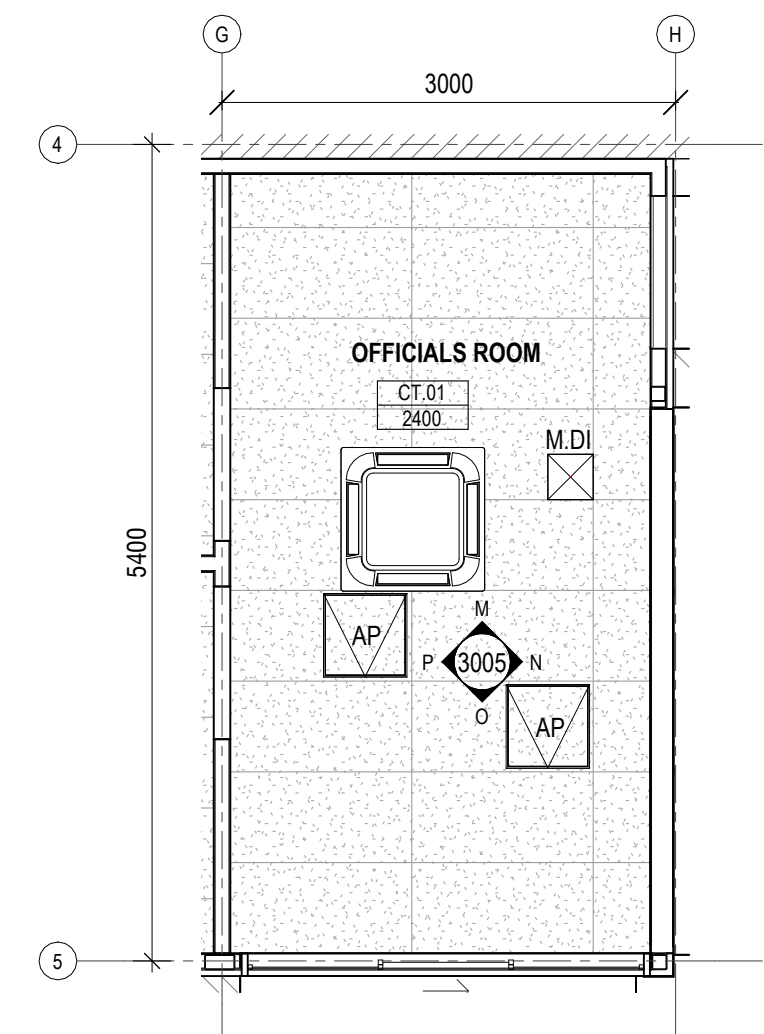


6 REFLECTED CEILING PLAN OFFICIALS ROOM
Scale: 1: 50

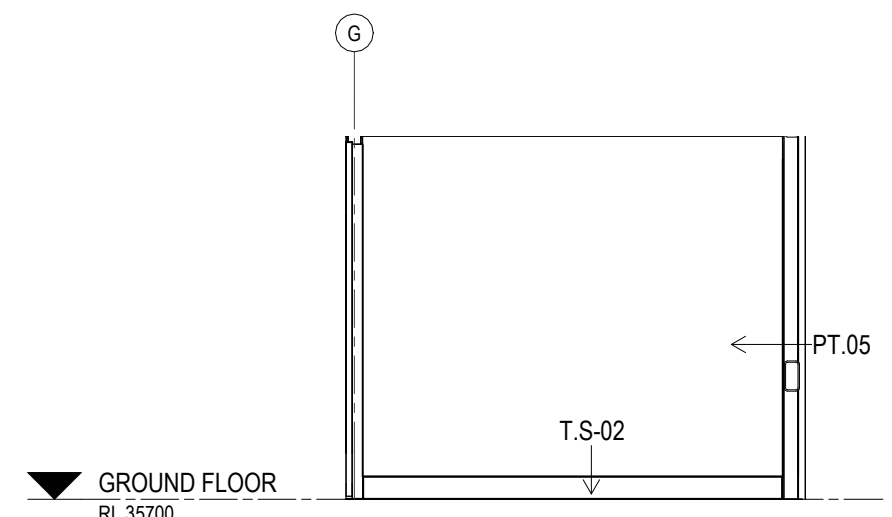


M ELEVATION OFFICIALS ROOM
Scale: 1: 50

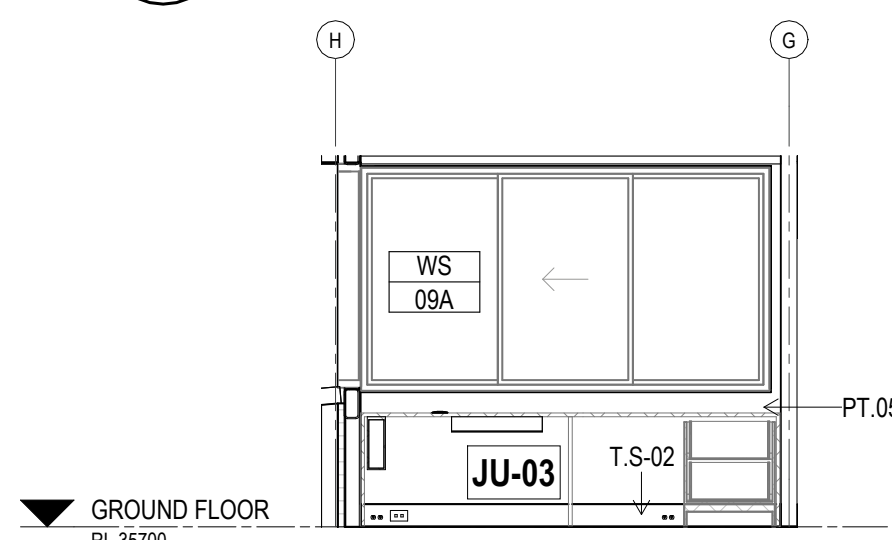

O ELEVATION OFFICIALS ROOM
Scale: 1: 50

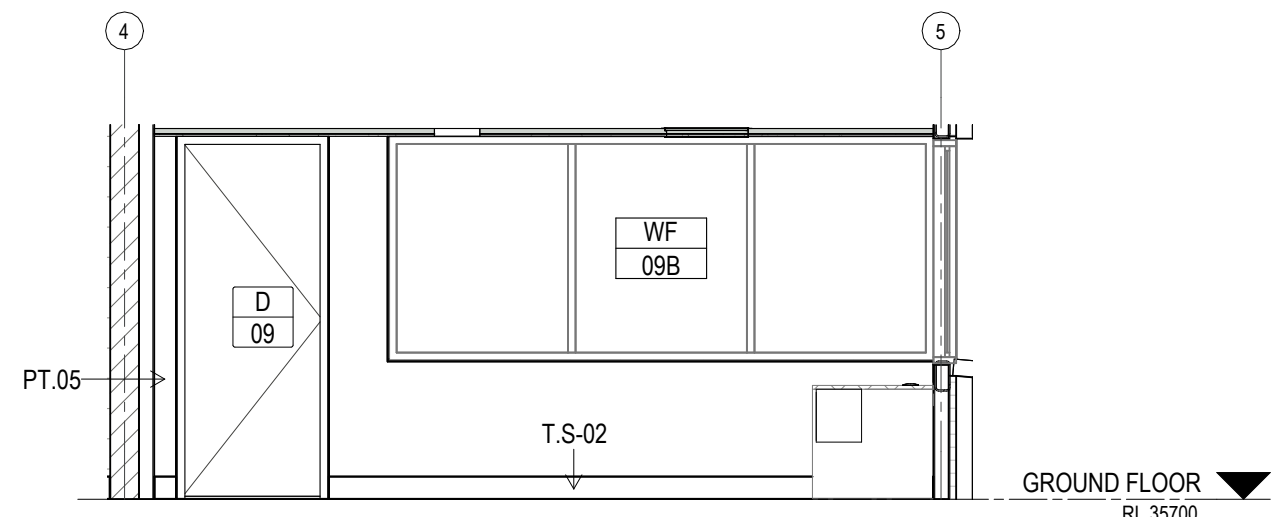


N ELEVATION OFFICIALS ROOM
Scale: 1: 50

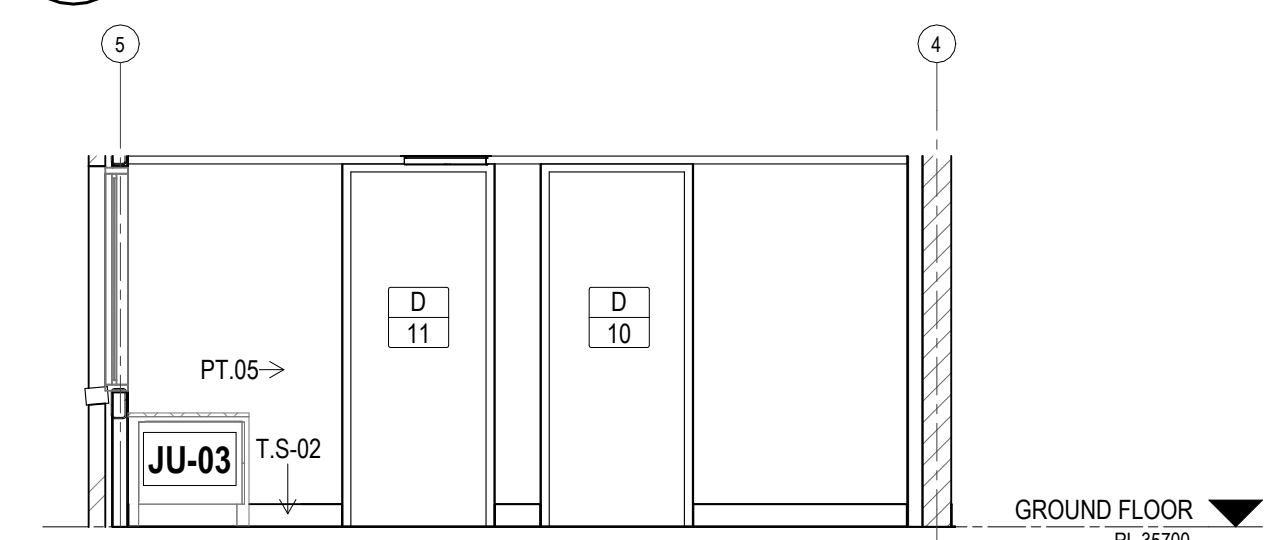

P ELEVATION OFFICIALS ROOM
Scale: 1: 50

• These designs and plans are the copyright of MODE DESIGN Corp. Pty Ltd and cannot be reproduced without written permission.
• Verify all dimensions on site prior to commencement of work.
• DO NOT scale off these drawings.
• Report any discrepancies to the architect before carrying out any work.

AMENDMENTS				
REV	DESCRIPTION	AUTH	CHK	DATE
T1	ISSUE FOR TENDER	DW	GB	18/06/26

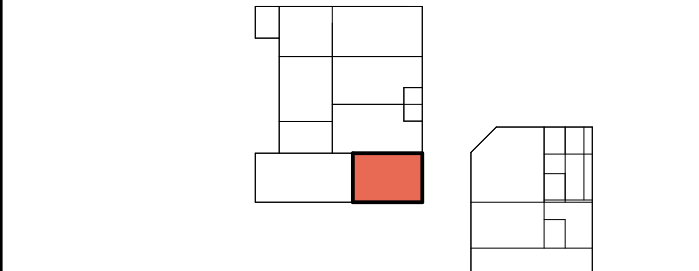

NOTE:
- REFER TO AR-NBC-0010 FOR CODE LIST.

ROOM LAYOUT NOTES
SUBMIT SHOP DRAWINGS OF ALL JOINERY ITEMS FOR REVIEW PRIOR FABRICATION
REFER TO TYPICAL FIXTURE HEIGHT SETOUT FOR FIXTURE MOUNTING
HEIGHTS - ALL FIXTURE SETOUTS ARE NOMINAL - INSTALL TO MANUFACTURER'S DETAILS
REFER TO INTERNAL FINISHES SCHEDULE FOR ALL FINISHES INTERNAL
REFER TO FF&E SCHEDULE FOR ALL FIXTURES, FITTINGS AND EQUIPMENT SPECIFICATIONS
ALLOW FOR NOGGINS AND FRAMING TO SUPPORT ALL WALL-MOUNTED INSTALLATIONS
ALL CUBICLE DOORS TO INCLUDE PRIVACY INDICATOR LOCKSETS
REFER FF&E SCHEDULE FOR TYPE SPECIFICATION

FURNITURE & EQUIPMENT
ALL JOINERY, EQUIPMENT AND LOOSE FURNITURE SHOWN DASHED GREY ARE INDICATIVE ONLY AND TO BE PROVIDED BY OTHERS
REFER TO JOINERY SHEET (AR-4310) FOR DETAILS ON JU-01 & JU-02

NOTE:
• TYPICAL SHOWER FALL TO BE 1:80 - 1:80
• TYPICAL KITCHEN FALL TO BE 1:80 - 1:100
• TYPICAL PWD SHOWER FALL TO BE 1:80 - 1:80
• TYPICAL PWD SHOWER FALL TO BE 1:80 - 1:100

NOM. REG. Architect: Rhonan O'Brien QLD 2350 NSW 7176 VIC 16162
TAS 1216 NZ 4712, Peter Bertram QLD 2333 WA 2143 NT AR1213
STATUS
ISSUED FOR TENDER
0m 0.5 1 1.5 2 2.5
NORTH

BRISBANE
mode
Plaza Level, Mosaic
826 Ann St
Fortitude Valley QLD 4006
T +61 7 3253 9900
bne@modedesign.com.au
ABN: 65 112 807 931

Rockhampton
Regional Council

CLIENT
SPORTENG™

PROJECT
ROCKHAMPTON NETBALL
CENTRE (STAGE 1) -
NETBALL CLUBHOUSE
554-700 YAAMBA ROAD, NORMAN GARDEN - 4701
DRAWING TITLE
ROOM LAYOUT -
OFC.ROOM, C/R.03, C/R.04

DRAWN DW	CHECKED SM
ISSUE 17/06/2026 2:42:21 PM	SCALE @ A1 As indicated
PROJECT No 24523	STAGE IFT
DRAWING No AR-NBC-3005	REVISION T1