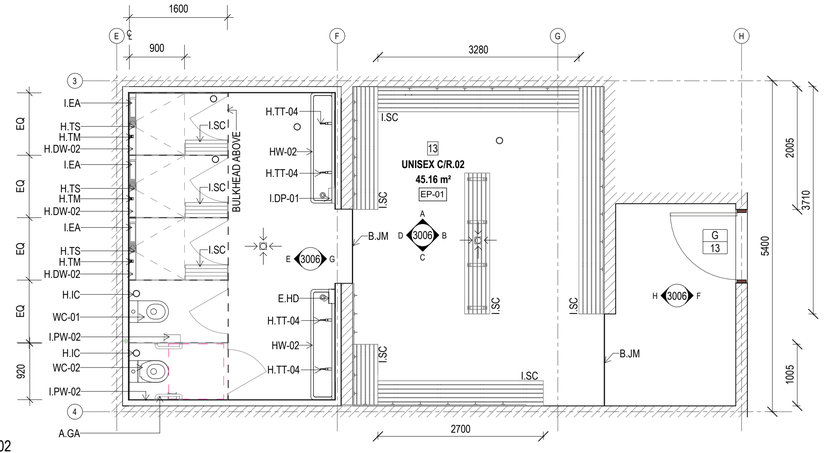

1 PLAN UNISEX C/R.02
Scale: 1 : 50

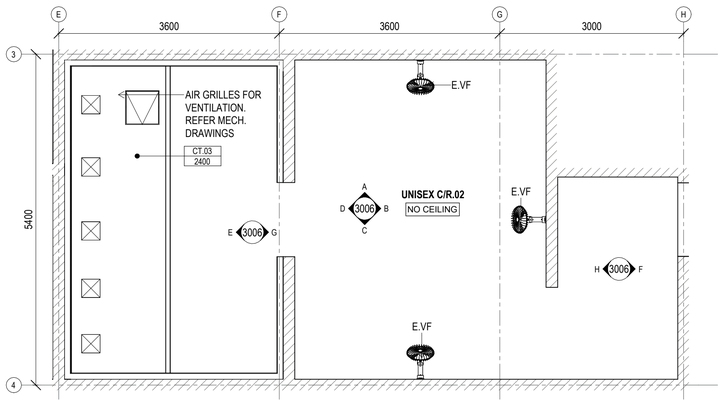

2 REFLECTED CEILING PLAN UNISEX C/R.02
Scale: 1 : 50

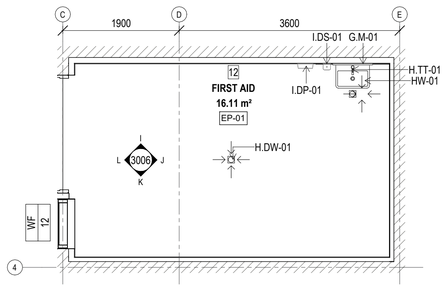

3 PLAN FIRST AID
Scale: 1 : 50

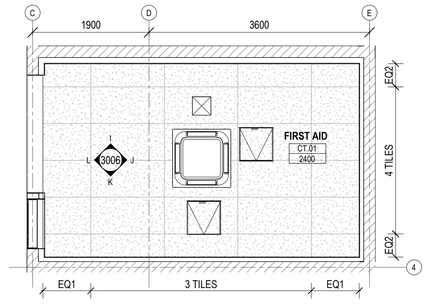

4 REFLECTED CEILING PLAN FIRST AID
Scale: 1 : 50

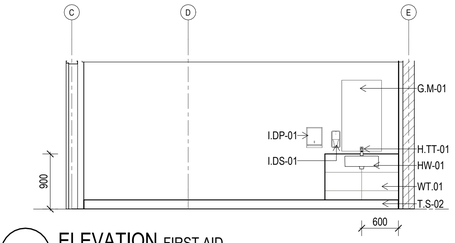

I ELEVATION FIRST AID
Scale: 1 : 50

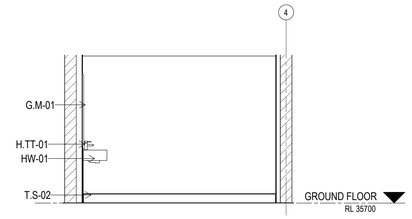

J ELEVATION FIRST AID
Scale: 1 : 50

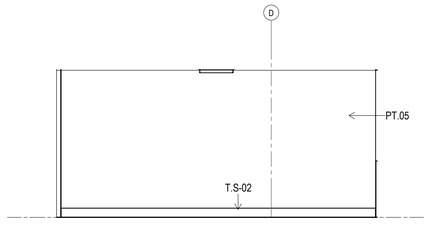

K ELEVATION FIRST AID
Scale: 1 : 50

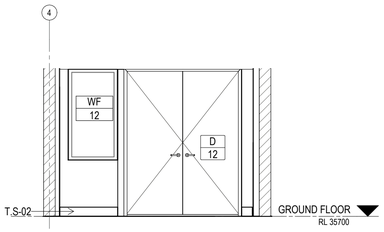

L ELEVATION FIRST AID
Scale: 1 : 50

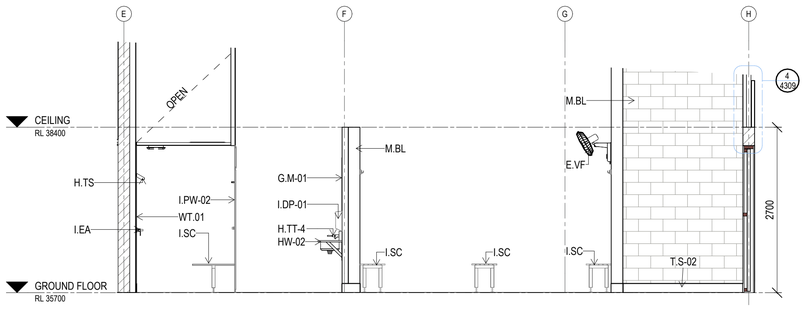

A ELEVATION UNISEX C/R.02
Scale: 1 : 50

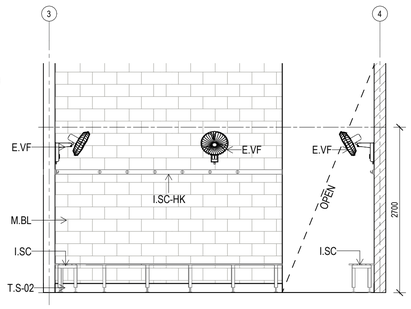

B ELEVATION UNISEX C/R.02
Scale: 1 : 50

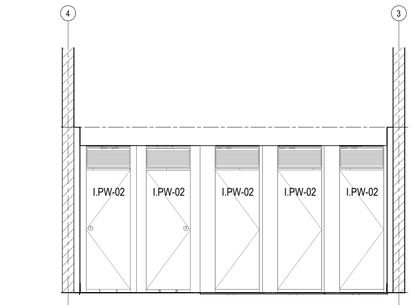

E ELEVATION UNISEX C/R.02
Scale: 1 : 50

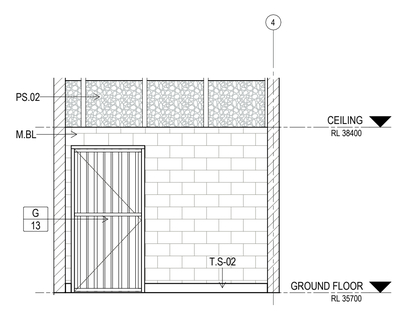

F ELEVATION UNISEX C/R.02
Scale: 1 : 50

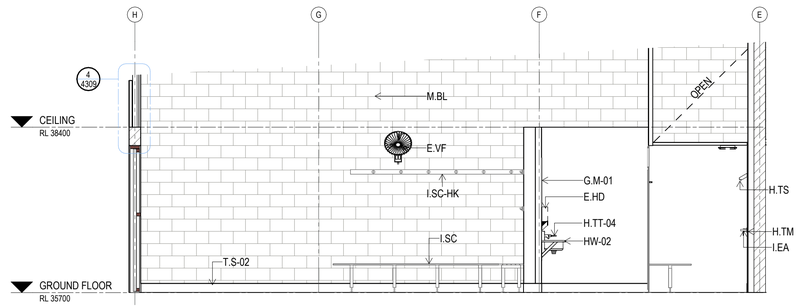

C ELEVATION UNISEX C/R.02
Scale: 1 : 50

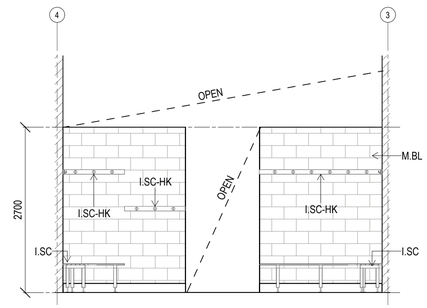

D ELEVATION UNISEX C/R.02
Scale: 1 : 50

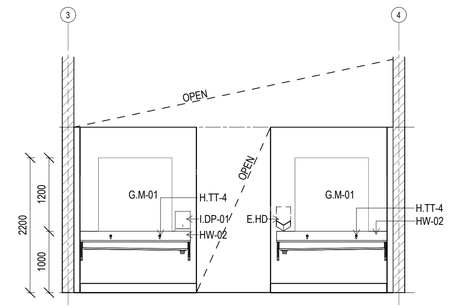

G ELEVATION UNISEX C/R.02
Scale: 1 : 50

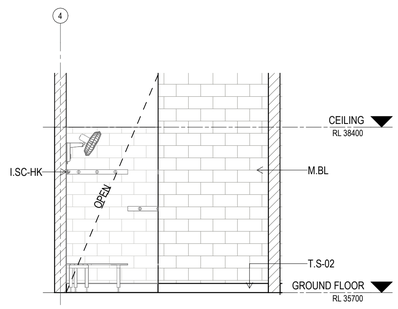

H ELEVATION UNISEX C/R.02
Scale: 1 : 50

- These designs and plans are the copyright of MODE DESIGN Corp. Pty Ltd and cannot be reproduced without written permission.
- Verify all dimensions on site prior to commencement of work.
- DO NOT scale off these drawings.
- Report any discrepancies to the architect before carrying out any work.

AMENDMENTS

REV	DESCRIPTION	AUTH	CHK	DATE
T1	ISSUE FOR TENDER	DW	GB	18/06/26

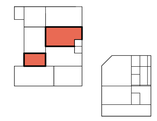

NOTE:
- REFER TO AR-NBC-0010 FOR CODE LIST.

ROOM LAYOUT NOTES

SUBMIT SHOP DRAWINGS OF ALL JOINERY ITEMS FOR REVIEW PRIOR FABRICATION

REFER TO TYPICAL FIXTURE HEIGHT SETOUT FOR FIXTURE MOUNTING HEIGHTS - ALL FIXTURE SETOUTS ARE NOMINAL - INSTALL TO MANUFACTURER'S DETAILS

REFER TO **INTERNAL FINISHES SCHEDULE** FOR ALL FINISHES INTERNAL

REFER TO **FF&E SCHEDULE** FOR ALL FIXTURES, FITTINGS AND EQUIPMENT SPECIFICATIONS

ALLOW FOR NOGGINS AND FRAMING TO SUPPORT ALL WALL-MOUNTED INSTALLATIONS

ALL CUBICLE DOORS TO INCLUDE PRIVACY INDICATOR LOCKSETS
REFER FF&E SCHEDULE FOR TYPE SPECIFICATION

FURNITURE & EQUIPMENT

ALL JOINERY, EQUIPMENT AND LOOSE FURNITURE SHOWN DASHED GREY ARE INDICATIVE ONLY AND TO BE PROVIDED BY OTHERS

REFER TO JOINERY SHEET (AR-4310) FOR DETAILS ON JU-01 & JU-02

FALL TO FLOOR WASTE

NOTE:
- TYPICAL SHOWER FALL TO BE 1:60 - 1:80
- TYPICAL KITCHEN FALL TO BE 1:80 - 1:100
- TYPICAL PWD SHOWER FALL TO BE 1:60 - 1:80
- TYPICAL PWD SHOWER FALL TO BE 1:80 - 1:100

NOM. REG. Architect: Rhonan O'Brien QLD 2350 NSW 7176 VIC 16182 TAS 1216 NZ 4712, Peter Bertram QLD 2333 WA 2143 NT AR1213

STATUS
ISSUED FOR TENDER

NORTH

0m 0.5 1 1.5 2 2.5

BRISBANE
mode
Plaza Level, Mosaic
826 Ann St
Fortitude Valley QLD 4006
T +61 7 3253 9900
bne@modedesign.com.au
ABN: 65 112 807 931

Rockhampton Regional Council

CLIENT
SPORTENG™

PROJECT
ROCKHAMPTON NETBALL CENTRE (STAGE 1) - NETBALL CLUBHOUSE
554-700 YAAMBA ROAD, NORMAN GARDEN - 4701

DRAWING TITLE
ROOM LAYOUT - UNISEX C.R.02 / FIRST AID

DRAWN	CHECKED
DW	SM
ISSUE	SCALE @ A1
17/06/2026 2:42:24 PM	As indicated

PROJECT No	STAGE	DRAWING No	REVISION
24523	IFT	AR- NBC- 3006	T1