


• These designs and plans are the copyright of MODE DESIGN Corp. Pty Ltd and cannot be reproduced without written permission.
• Verify all dimensions on site prior to commencement of work.
• DO NOT scale off these drawings.
• Report any discrepancies to the architect before carrying out any work.

AMENDMENTS					
REV	DESCRIPTION	AUTH	CHK	DATE	
T1	ISSUE FOR TENDER	DW	GB	18/06/26	

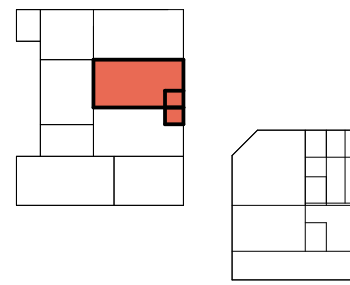

NOTE:
- REFER TO AR-NBC-0010 FOR CODE LIST.


ROOM LAYOUT NOTES

SUBMIT SHOP DRAWINGS OF ALL JOINERY ITEMS FOR REVIEW PRIOR FABRICATION
REFER TO TYPICAL FIXTURE HEIGHT SETOUT FOR FIXTURE MOUNTING HEIGHTS- ALL FIXTURE SETOUTS ARE NOMINAL - INSTALL TO MANUFACTURER'S DETAILS
REFER TO INTERNAL FINISHES SCHEDULE FOR ALL FINISHES INTERNAL
REFER TO FF&E SCHEDULE FOR ALL FIXTURES, FITTINGS AND EQUIPMENT SPECIFICATIONS
ALLOW FOR NOGGINS AND FRAMING TO SUPPORT ALL WALL-MOUNTED INSTALLATIONS
ALL CUBICLE DOORS TO INCLUDE PRIVACY INDICATOR LOCKSETS
REFER FF&E SCHEDULE FOR TYPE SPECIFICATION

FURNITURE & EQUIPMENT

ALL JOINERY, EQUIPMENT AND LOOSE FURNITURE SHOWN DASHED GREY ARE INDICATIVE ONLY AND TO BE PROVIDED BY OTHERS


REFER TO JOINERY SHEET (AR-4310) FOR DETAILS ON JU-01 & JU-02

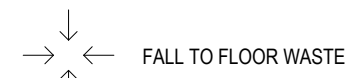

NOTE:
• TYPICAL SHOWER FALL TO BE 1:80 - 1:80
• TYPICAL KITCHEN FALL TO BE 1:80 - 1:100
• TYPICAL PWD SHOWER FALL TO BE 1:80 - 1:80
• TYPICAL PWD SHOWER FALL TO BE 1:80 - 1:100

NOM. REG. Architect: Rhonan O'Brien QLD 2350 NSW 7176 VIC 16162
TAS 1216 NZ 4712, Peter Bertram QLD 2333 WA 2143 NT AR1213

STATUS
ISSUED FOR TENDER

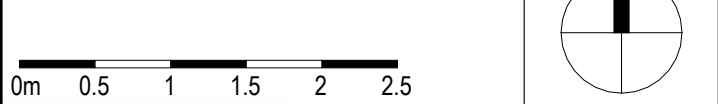


BRISBANE
mode
Plaza Level, Mosaic
826 Ann St
Fortitude Valley QLD 4006
T +61 7 3253 9900
bne@modedesign.com.au
ABN: 65 112 807 931




CLIENT
SPORTENG™

PROJECT
ROCKHAMPTON NETBALL CENTRE (STAGE 1) - NETBALL CLUBHOUSE
554-700 YAAMBA ROAD, NORMAN GARDEN - 4701
DRAWING TITLE
ROOM LAYOUT - UNISEX C.R.01 / SERVICES 2 / CLEANER


DRAWN AG	CHECKED SM	REVISION	
ISSUE 17/06/2026 2:42:27 PM	SCALE @ A1 As indicated	AR-NBC-3007	T1
PROJECT No 24523	DRAWING No IFT		

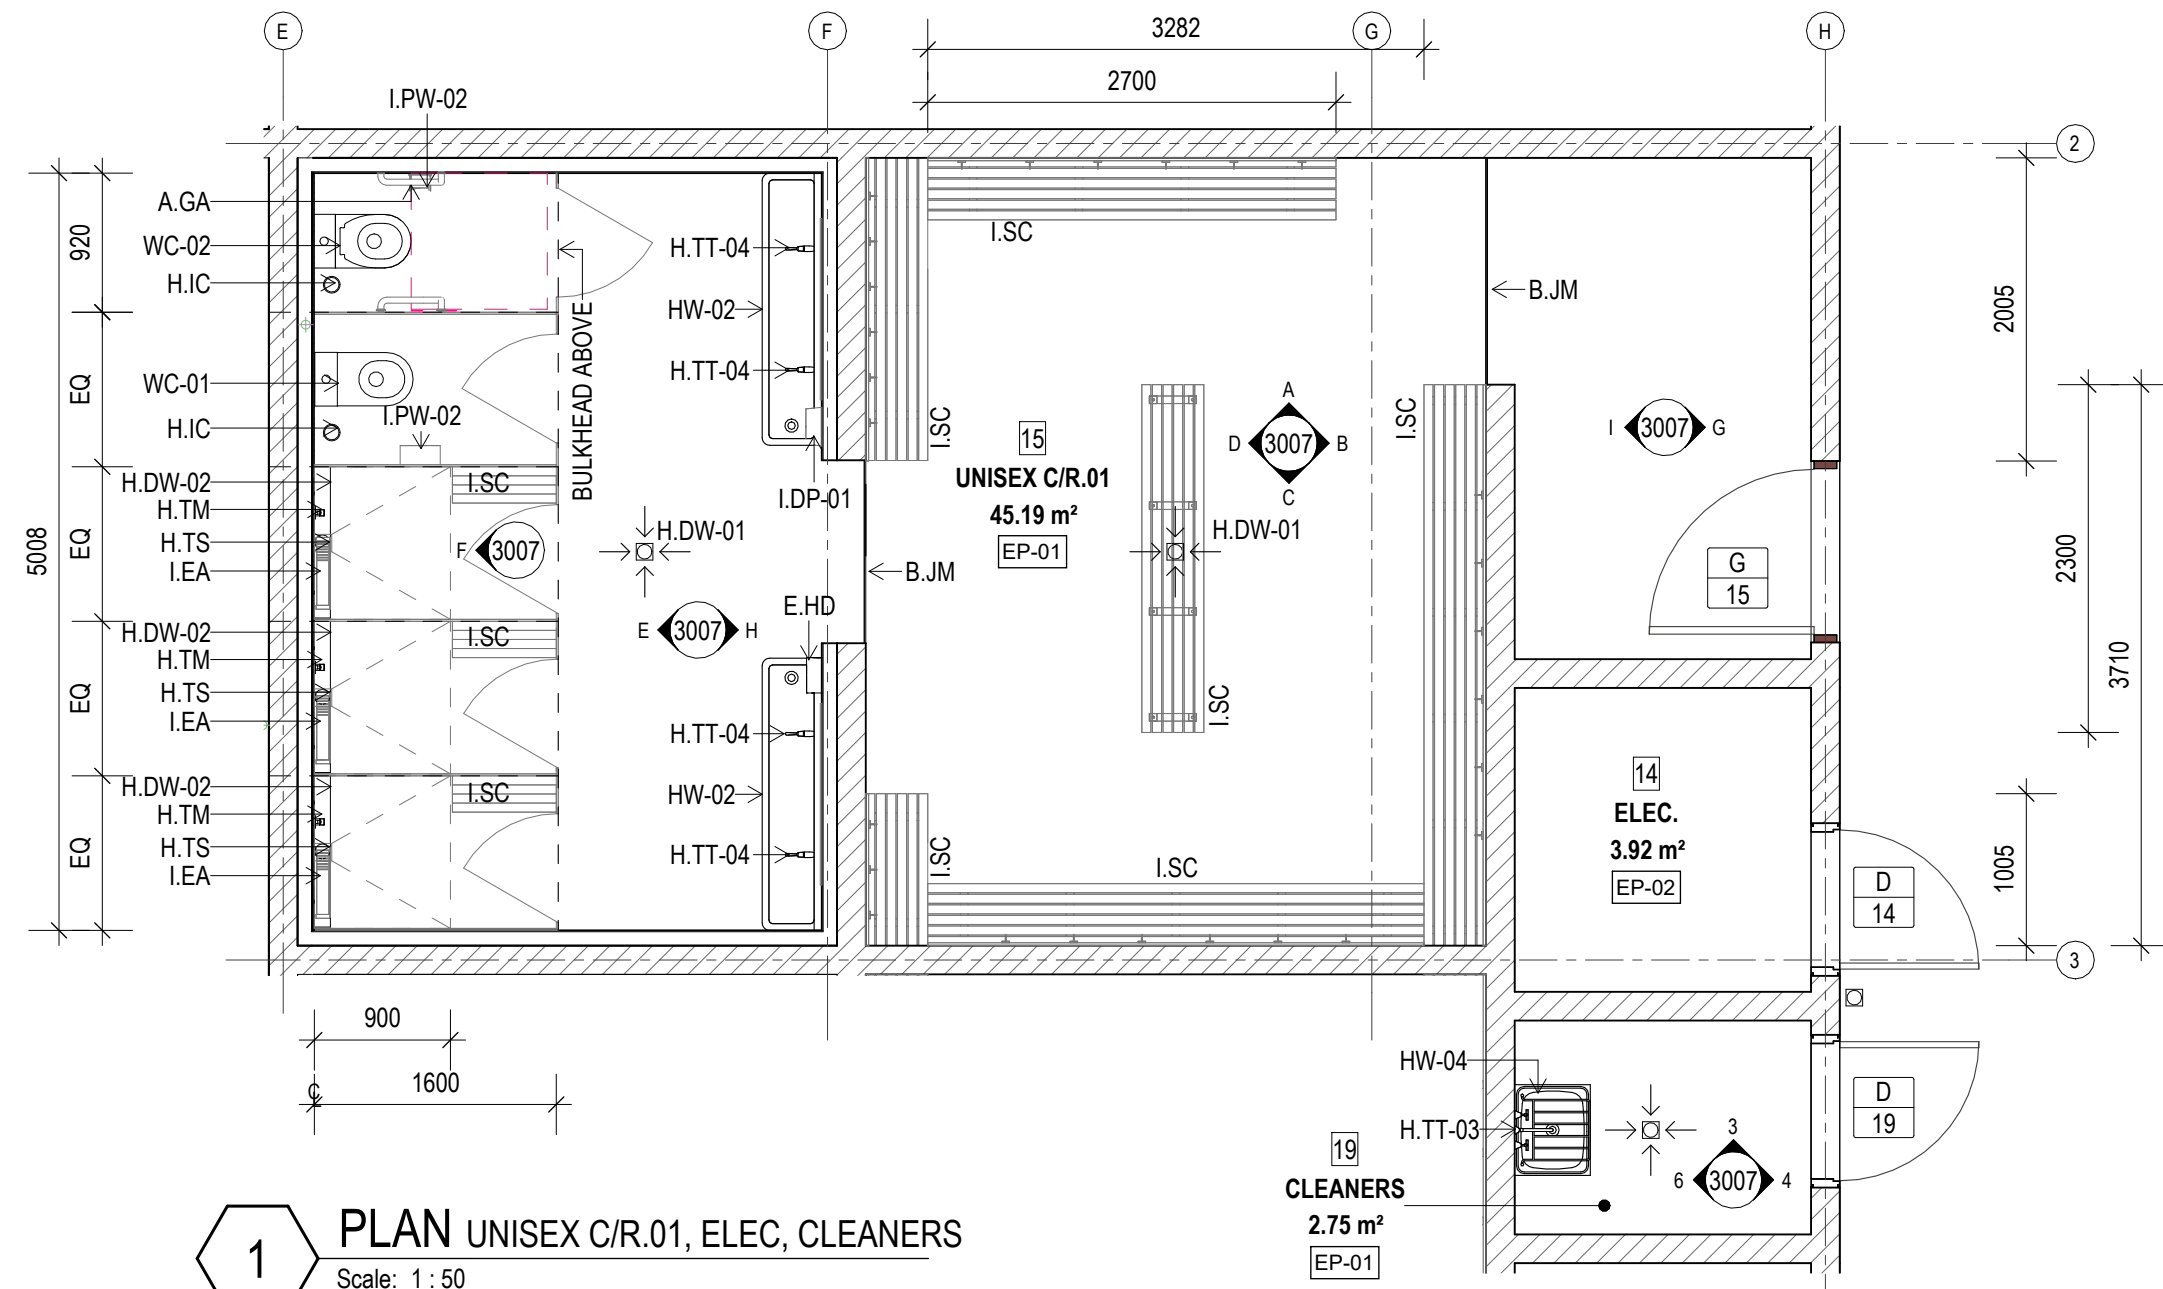


1 PLAN UNISEX C/R.01, ELEC, CLEANERS
Scale: 1 : 50

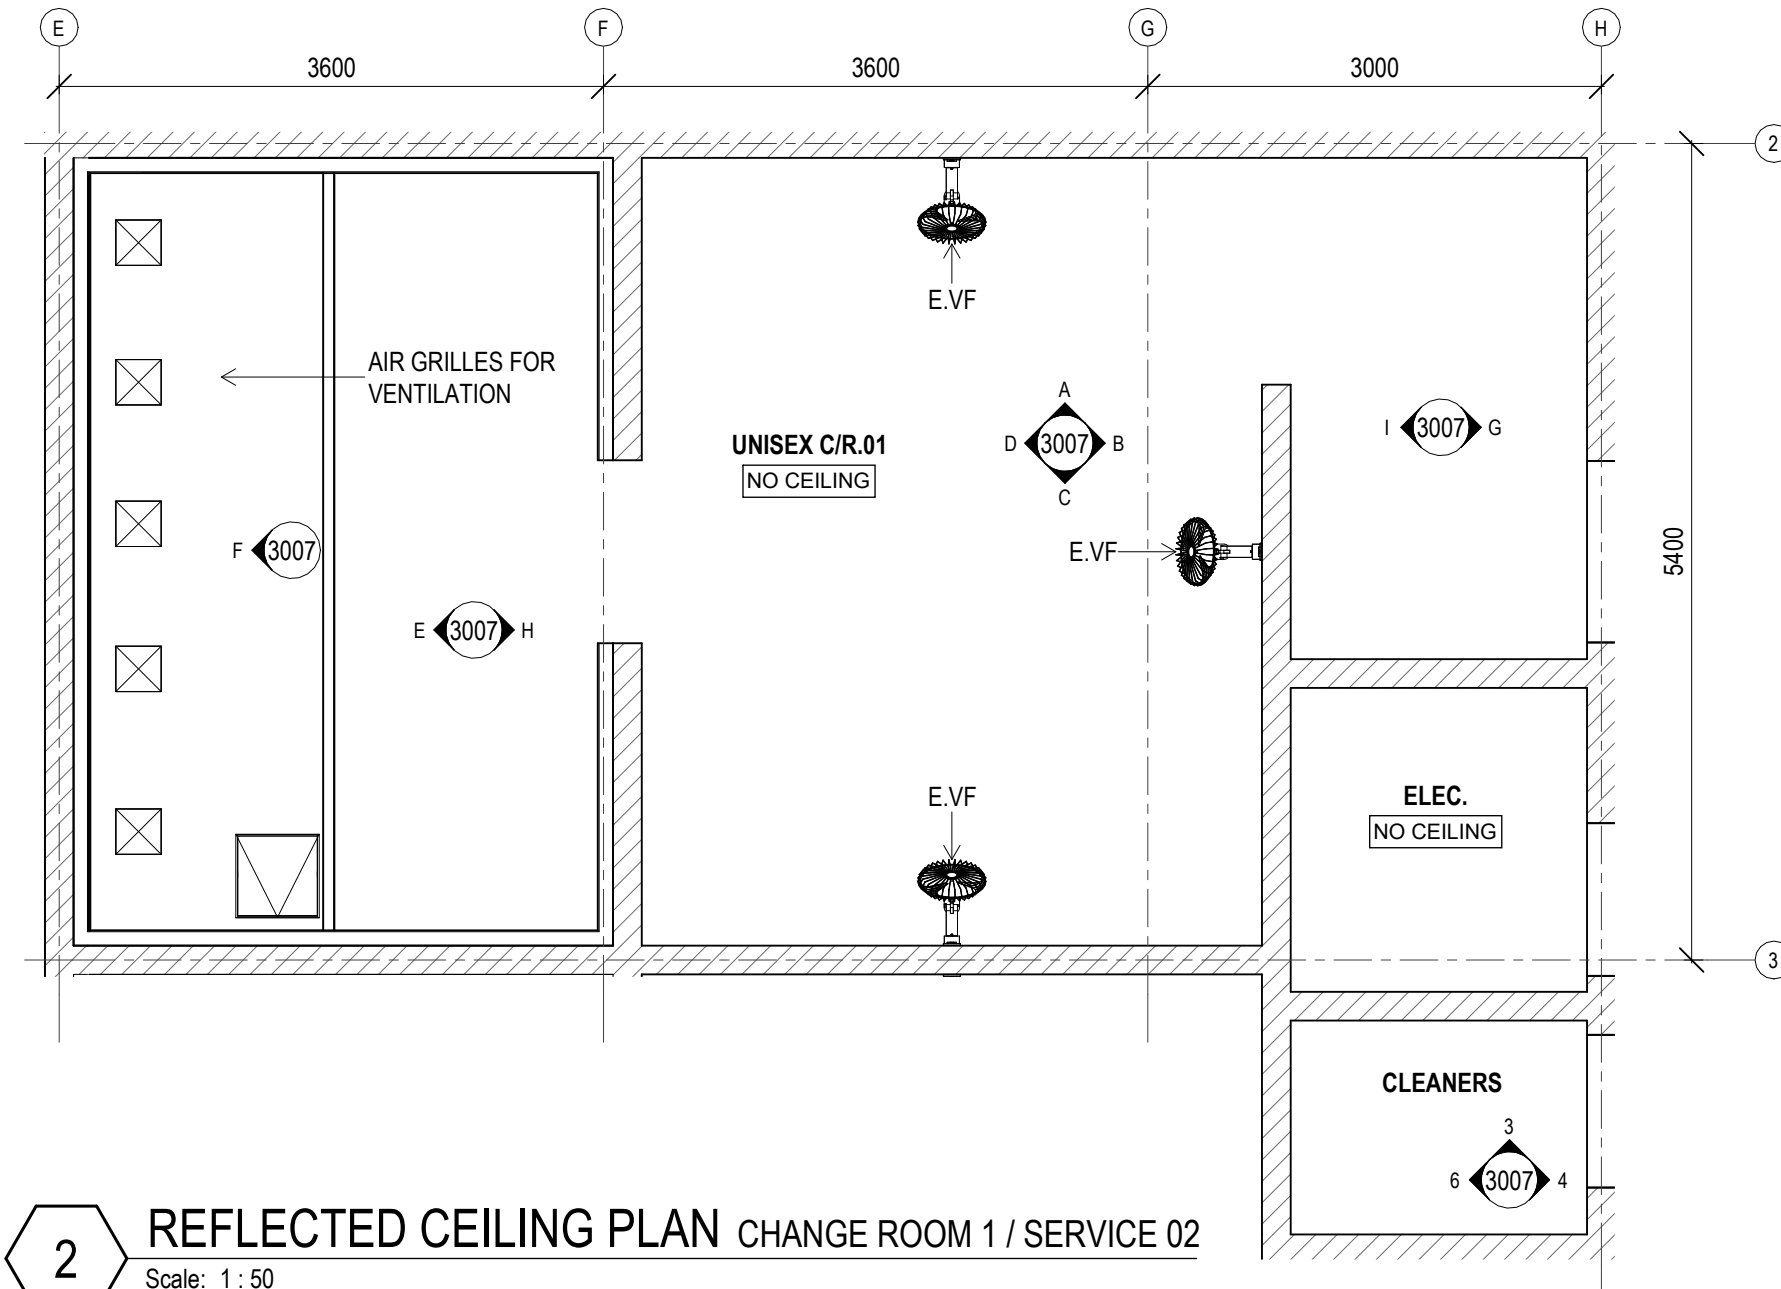


2 REFLECTED CEILING PLAN CHANGE ROOM 1 / SERVICE 02
Scale: 1 : 50

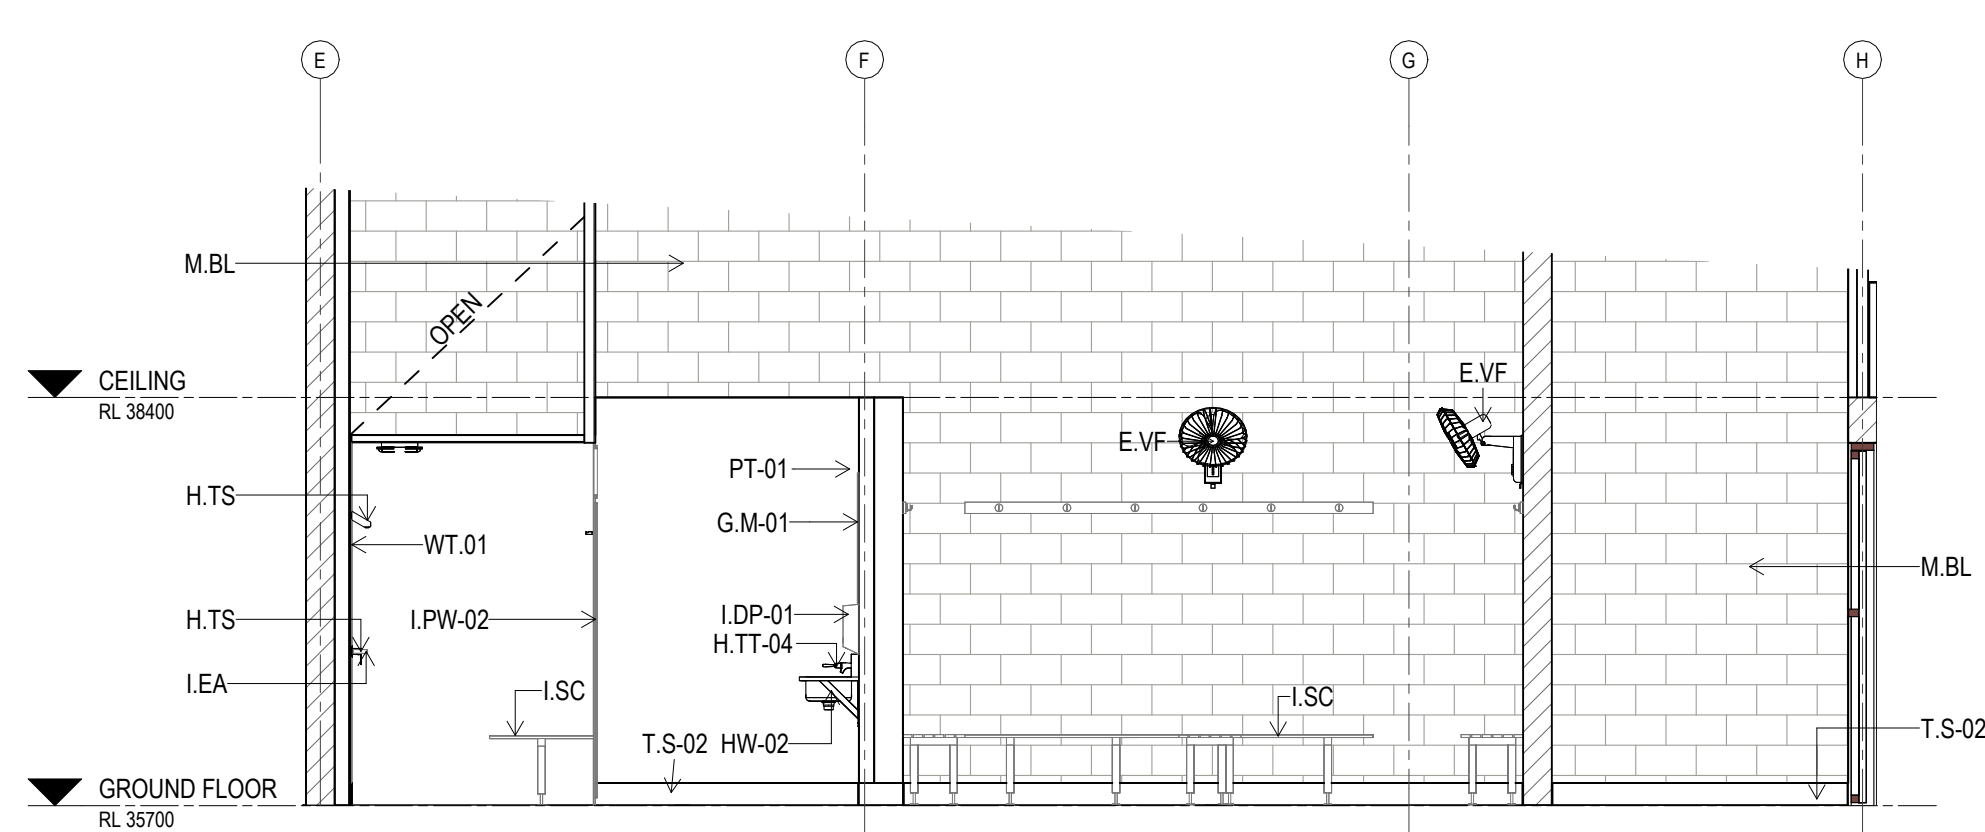


A ELEVATION CHANGE ROOM 1
Scale: 1 : 50

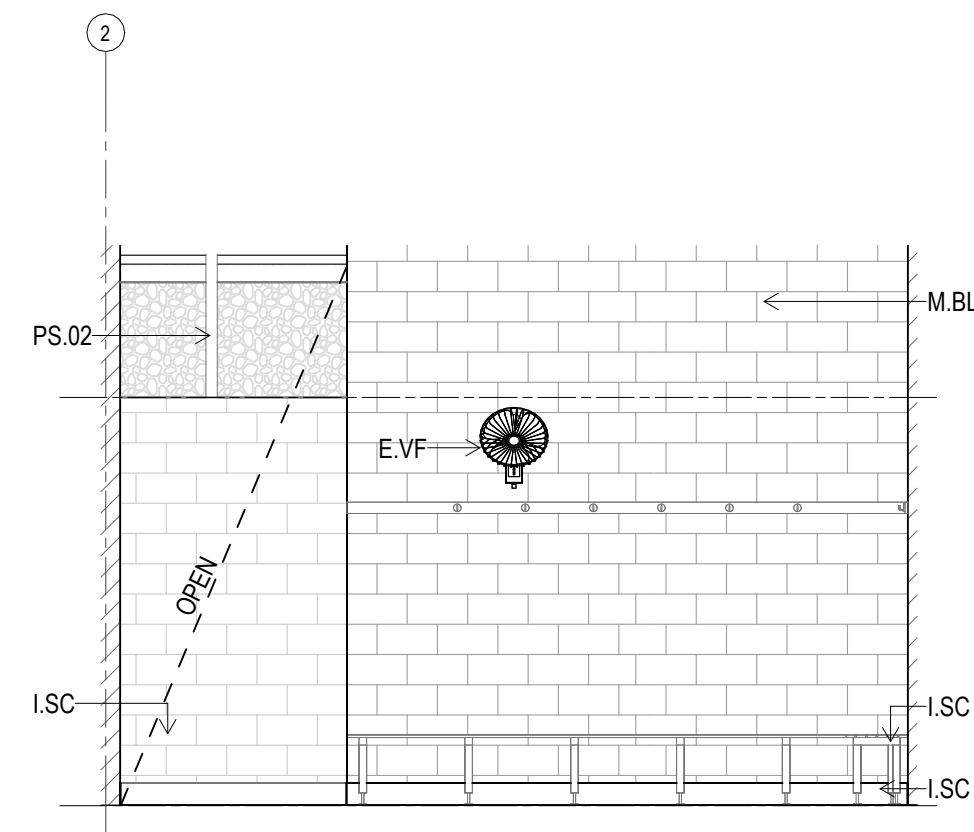


B ELEVATION CHANGE ROOM 1
Scale: 1 : 50

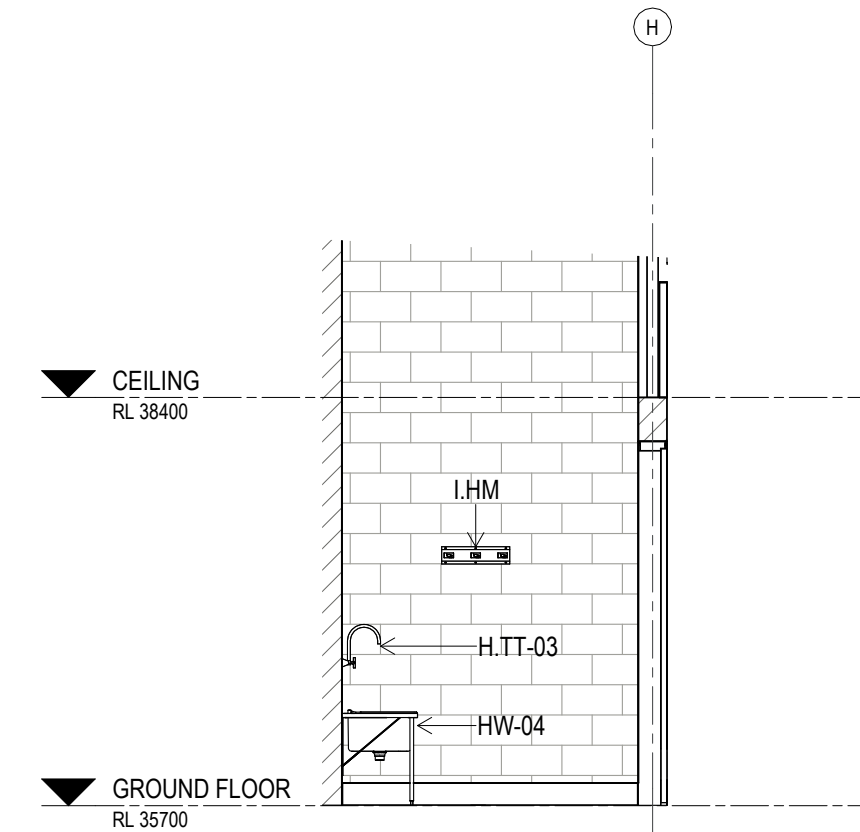


3 ELEVATION CLEANERS
Scale: 1 : 50

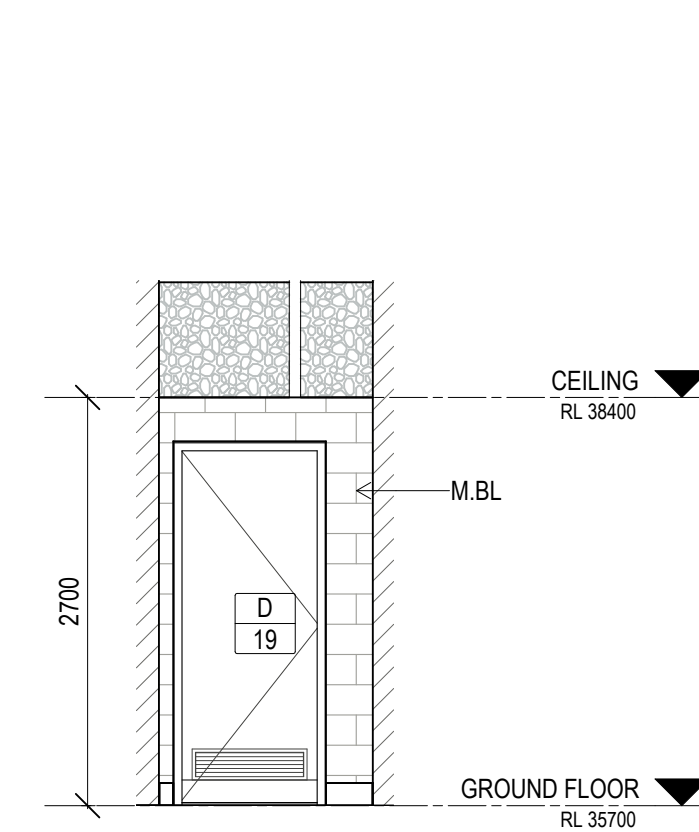


4 ELEVATION CLEANERS
Scale: 1 : 50

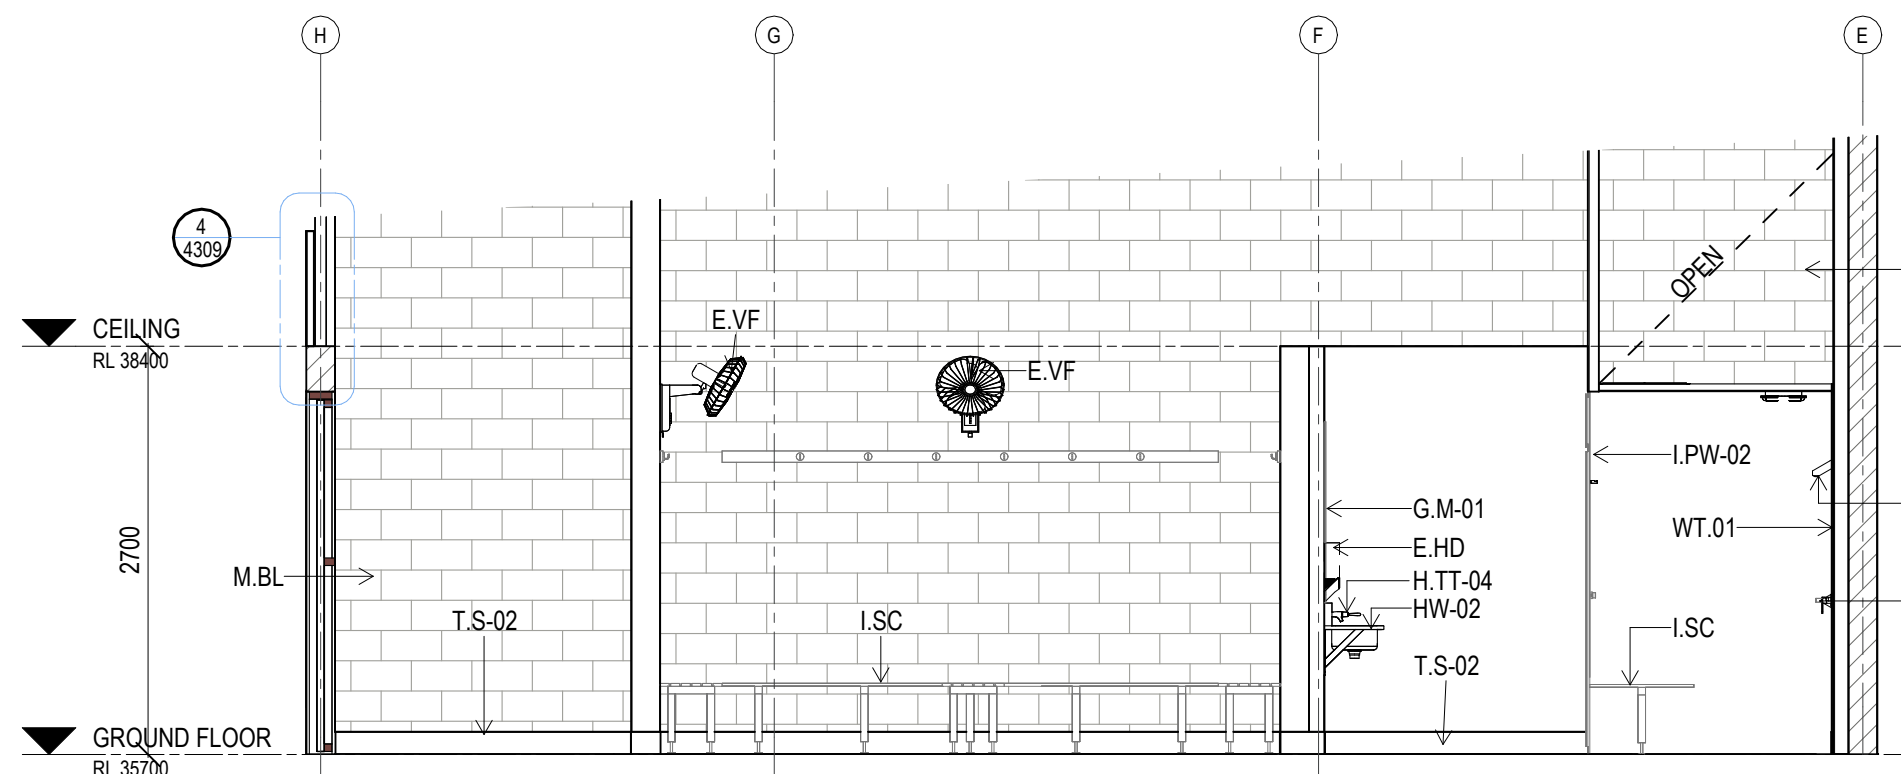


C ELEVATION CHANGE ROOM 1
Scale: 1 : 50

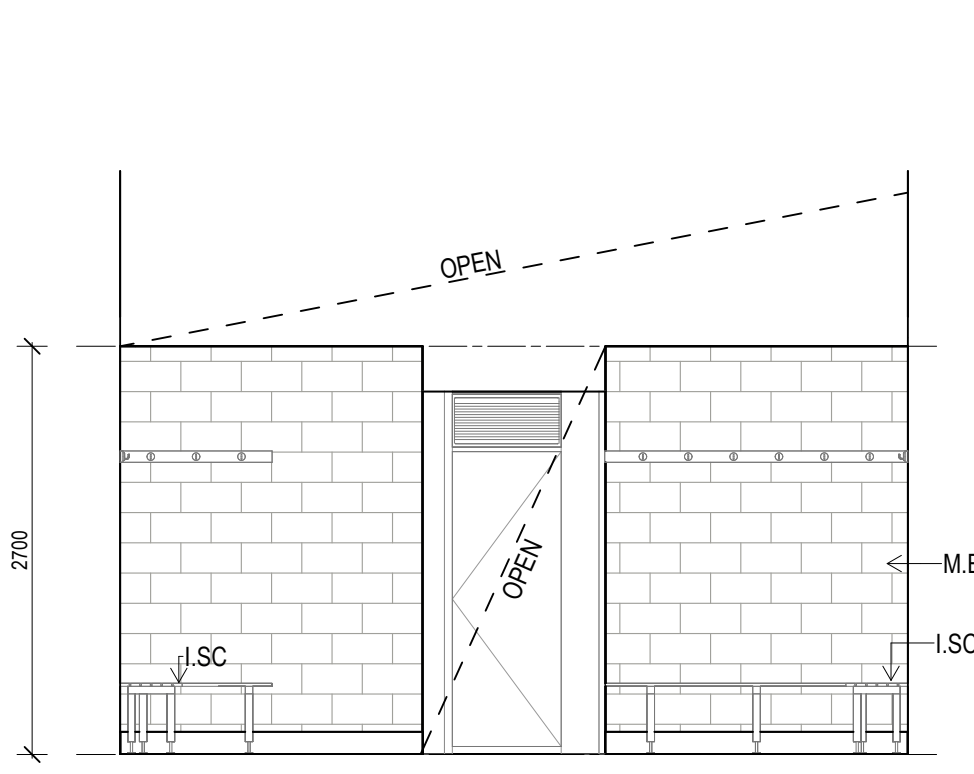


D ELEVATION CHANGE ROOM 1
Scale: 1 : 50

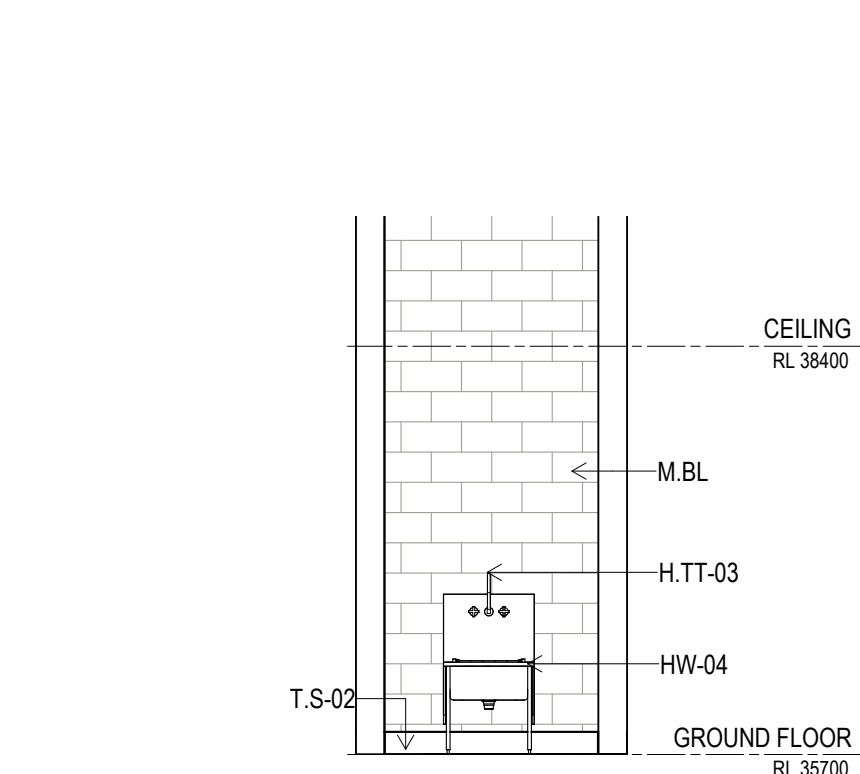


6 ELEVATION CLEANERS
Scale: 1 : 50

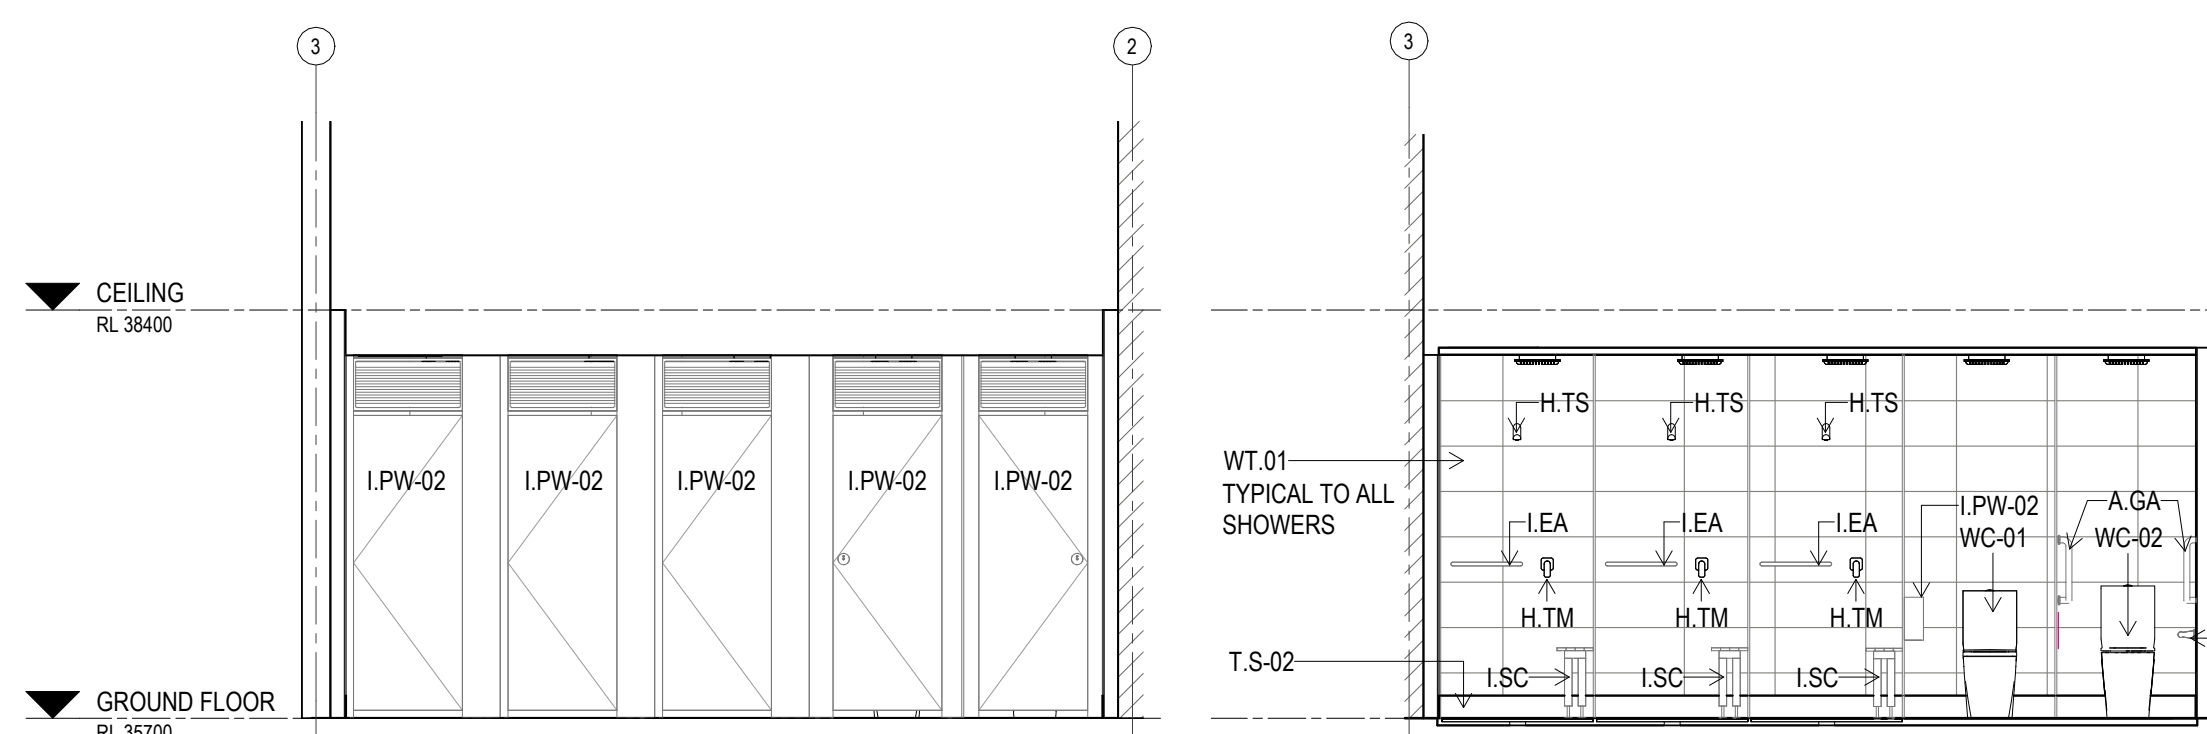


E ELEVATION CHANGE ROOM 1
Scale: 1 : 50

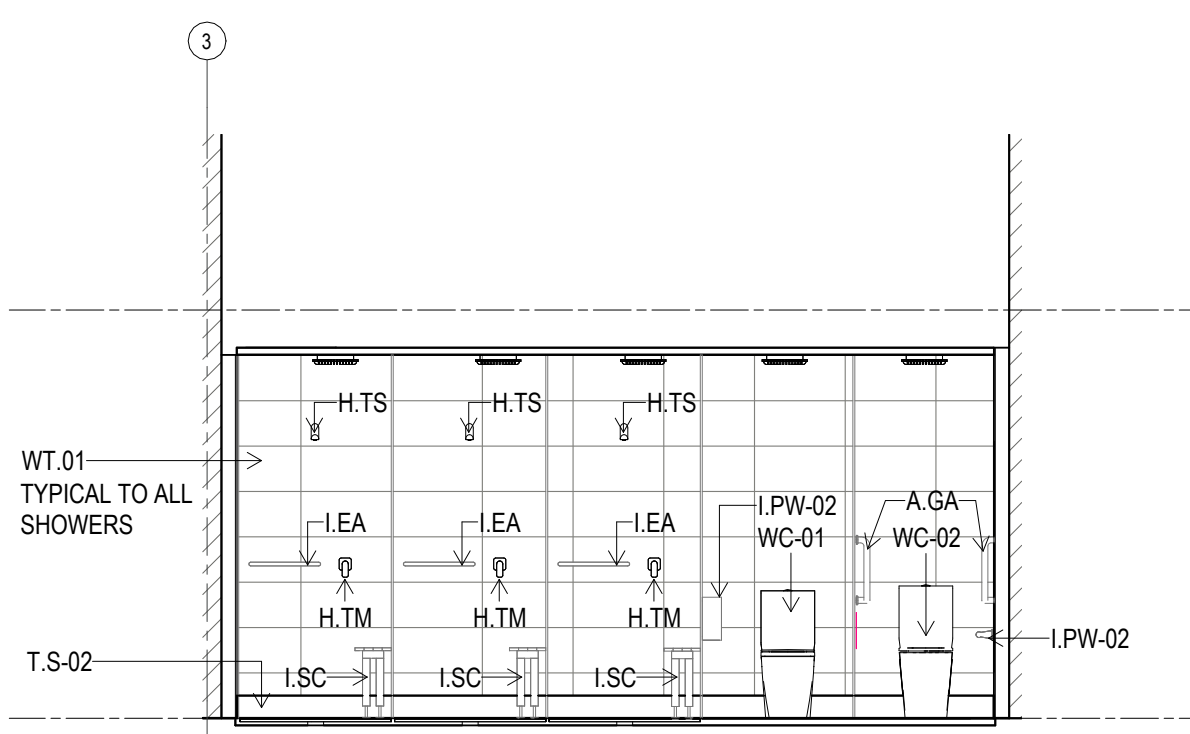


F ELEVATION CHANGE ROOM 1
Scale: 1 : 50

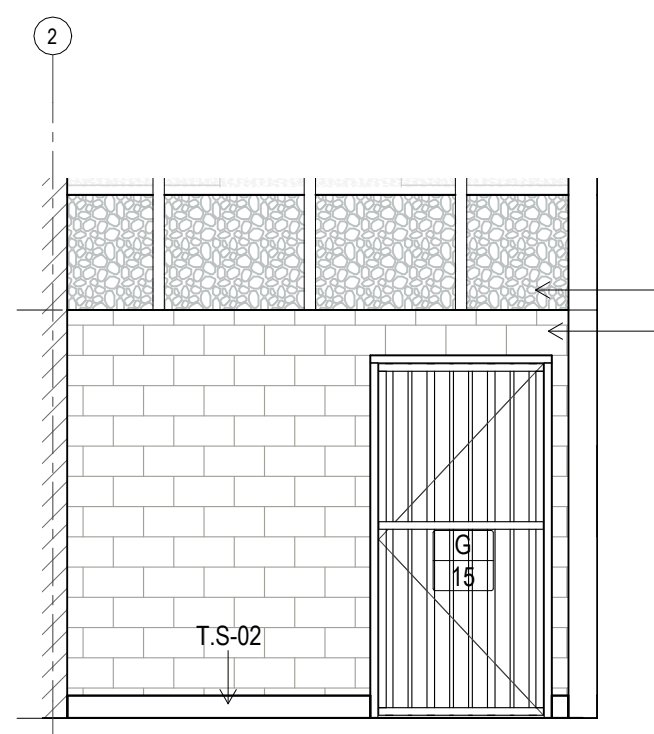

G ELEVATION CHANGE ROOM 1
Scale: 1 : 50

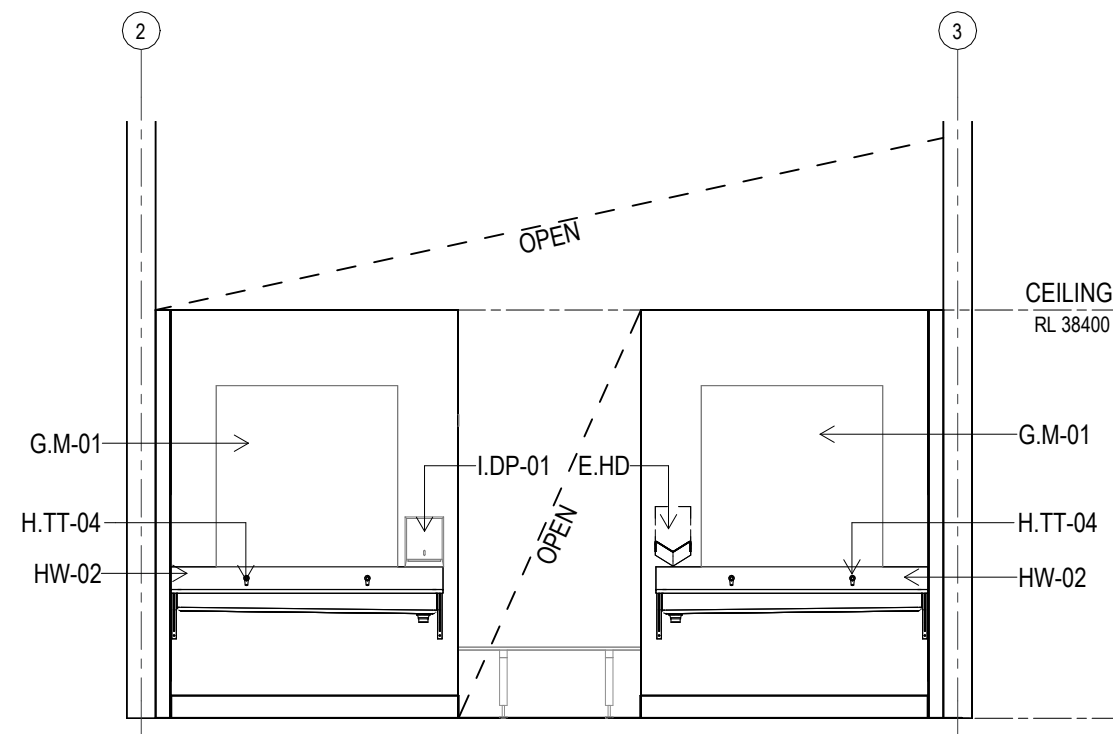

H ELEVATION CHANGE ROOM 1
Scale: 1 : 50

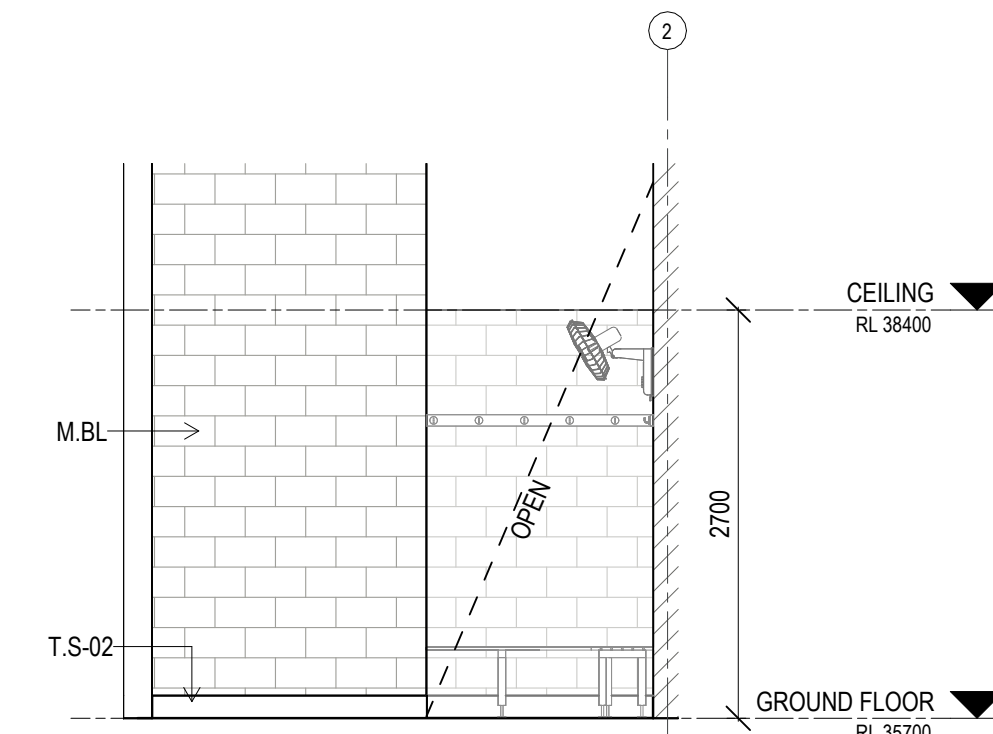

I ELEVATION CHANGE ROOM 1
Scale: 1 : 50