




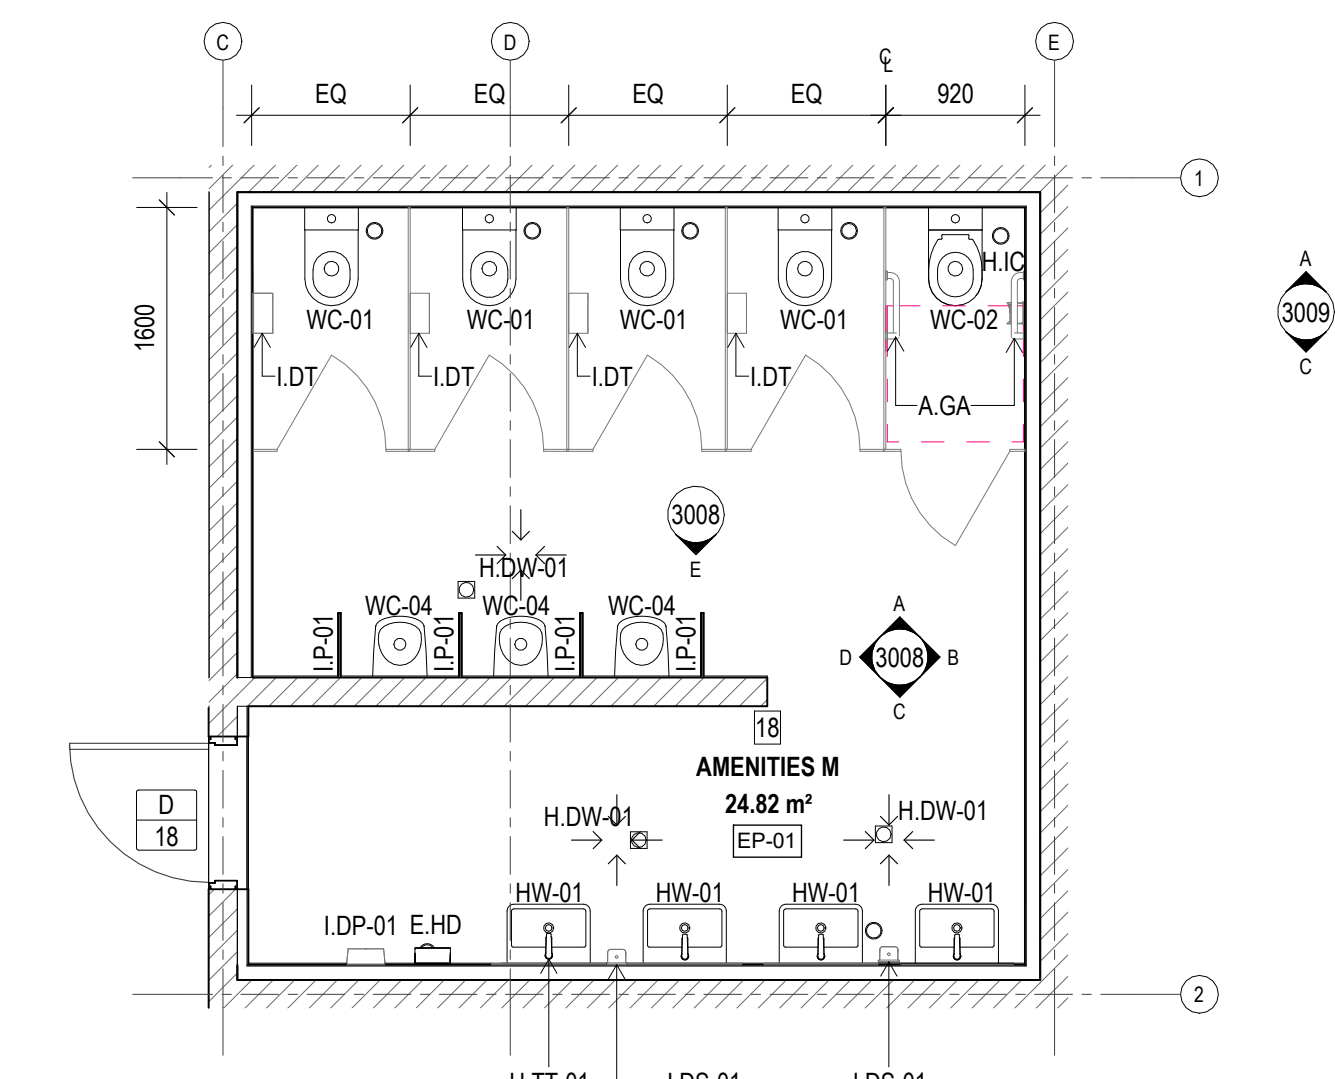


1 PLAN AMENITIES M
Scale: 1:50

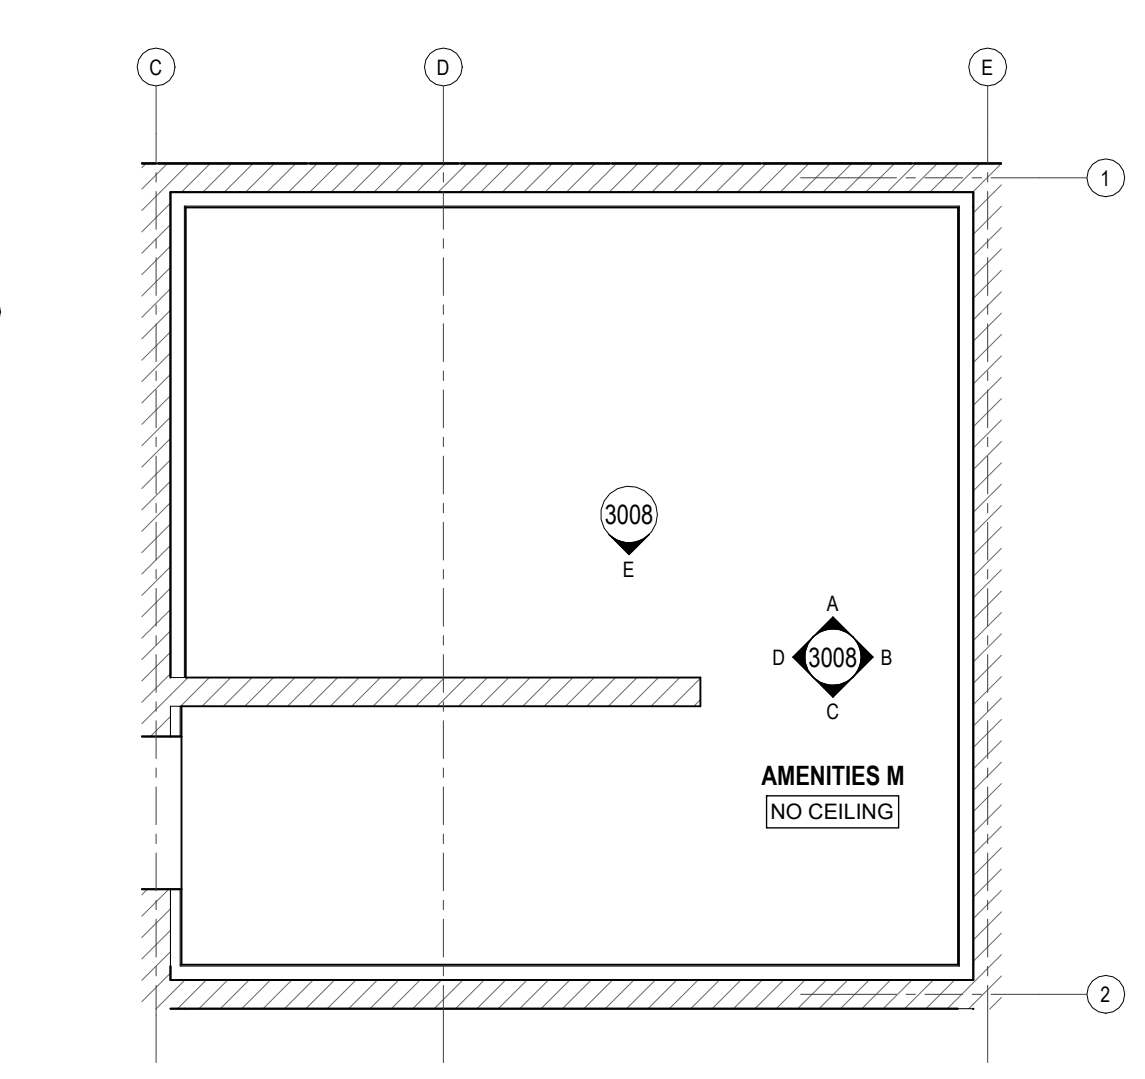


2 REFLECTED CEILING PLAN AMENITIES M
Scale: 1:50

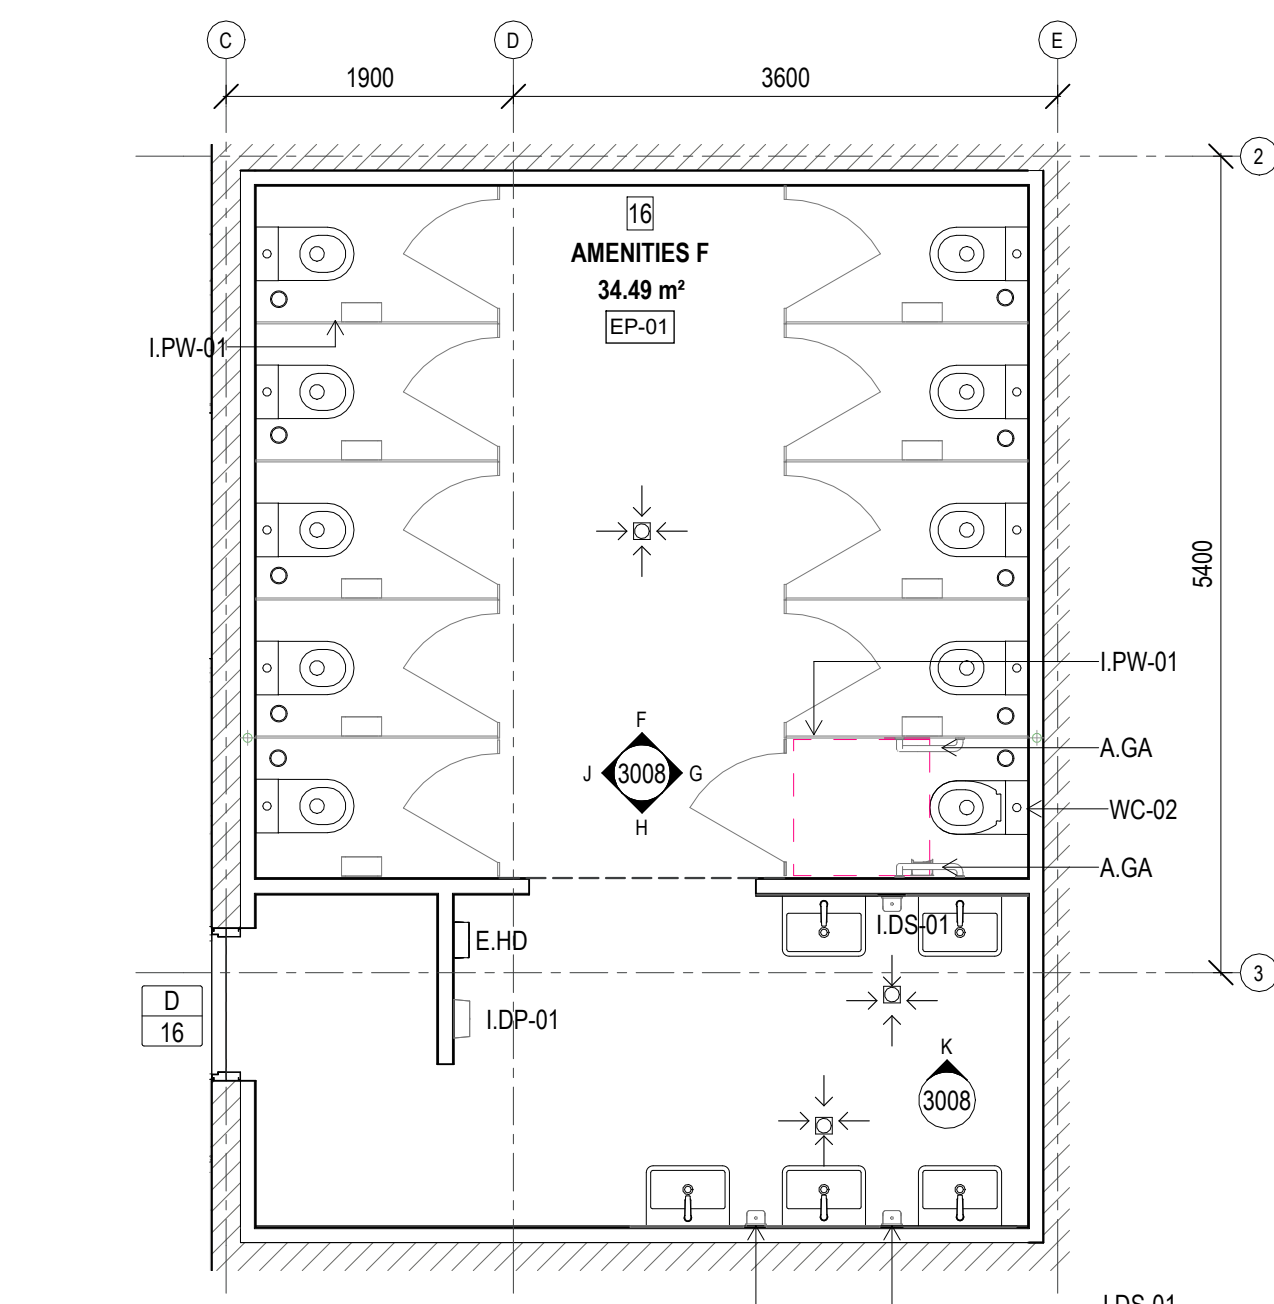


3 PLAN AMENITIES F
Scale: 1:50

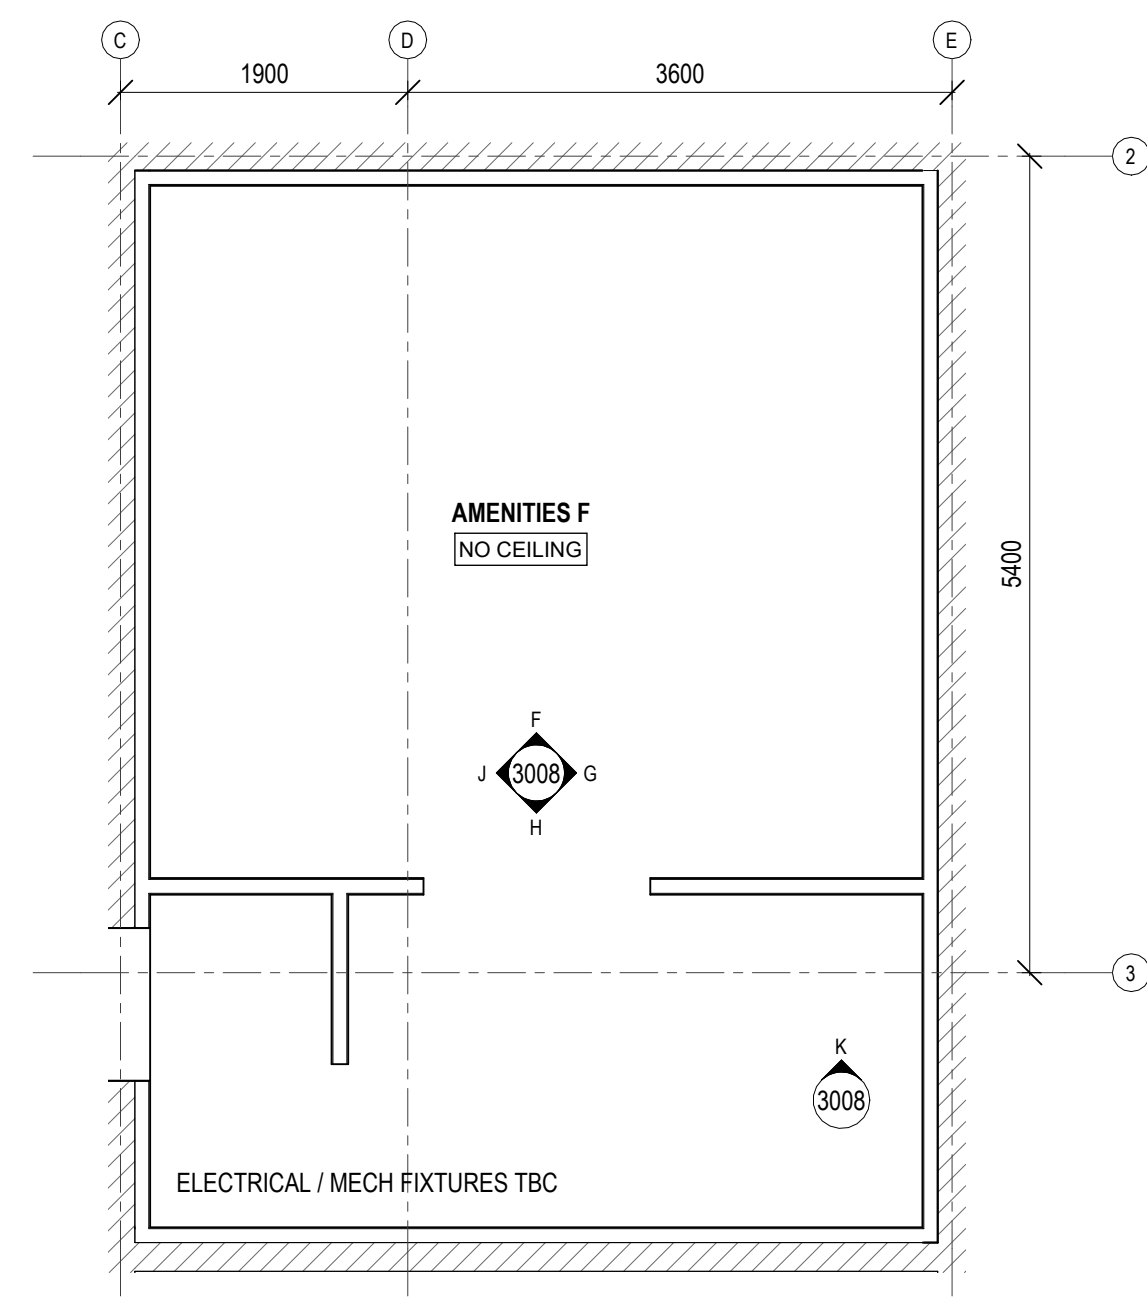


4 REFLECTED CEILING PLAN AMENITIES F
Scale: 1:50

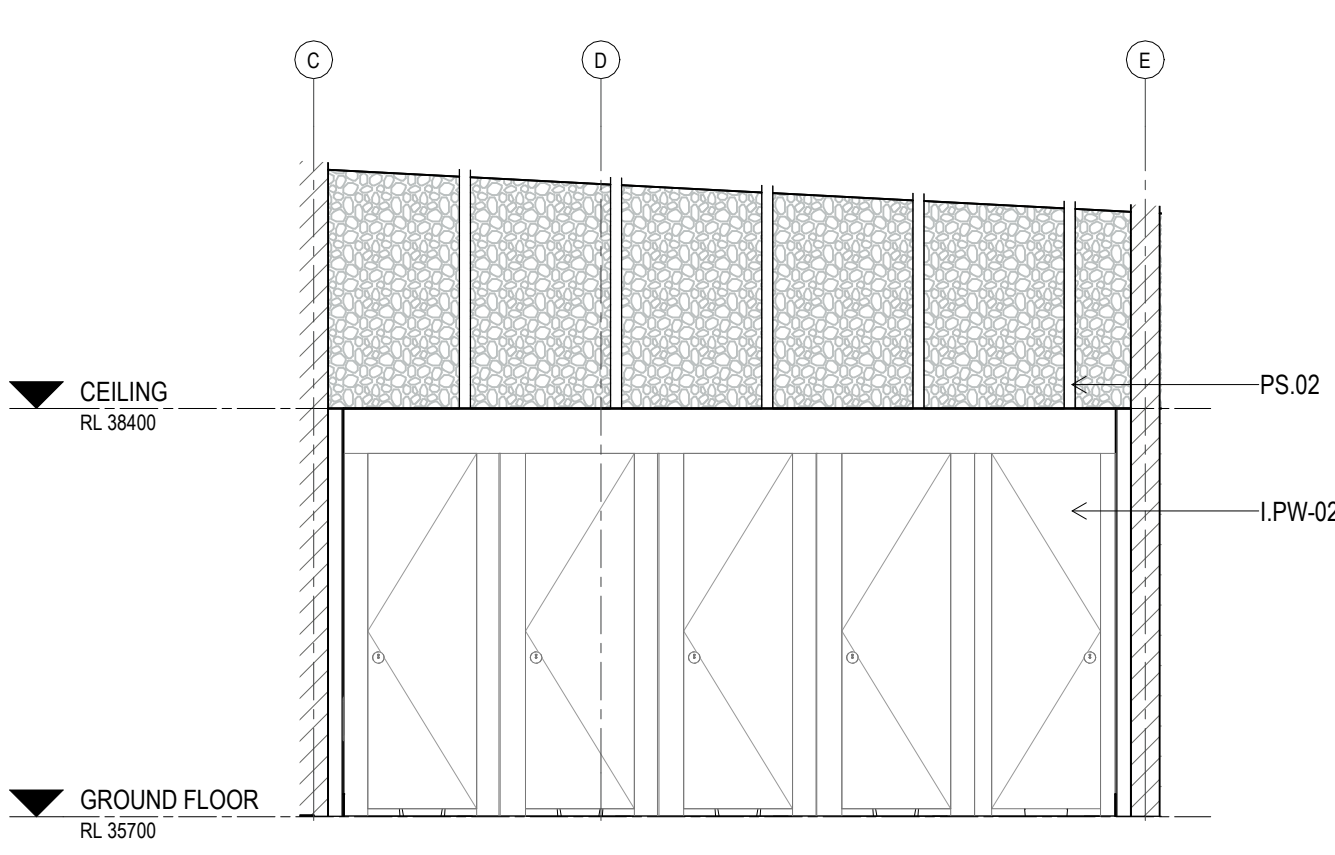


A ELEVATION AMENITIES M
Scale: 1:50

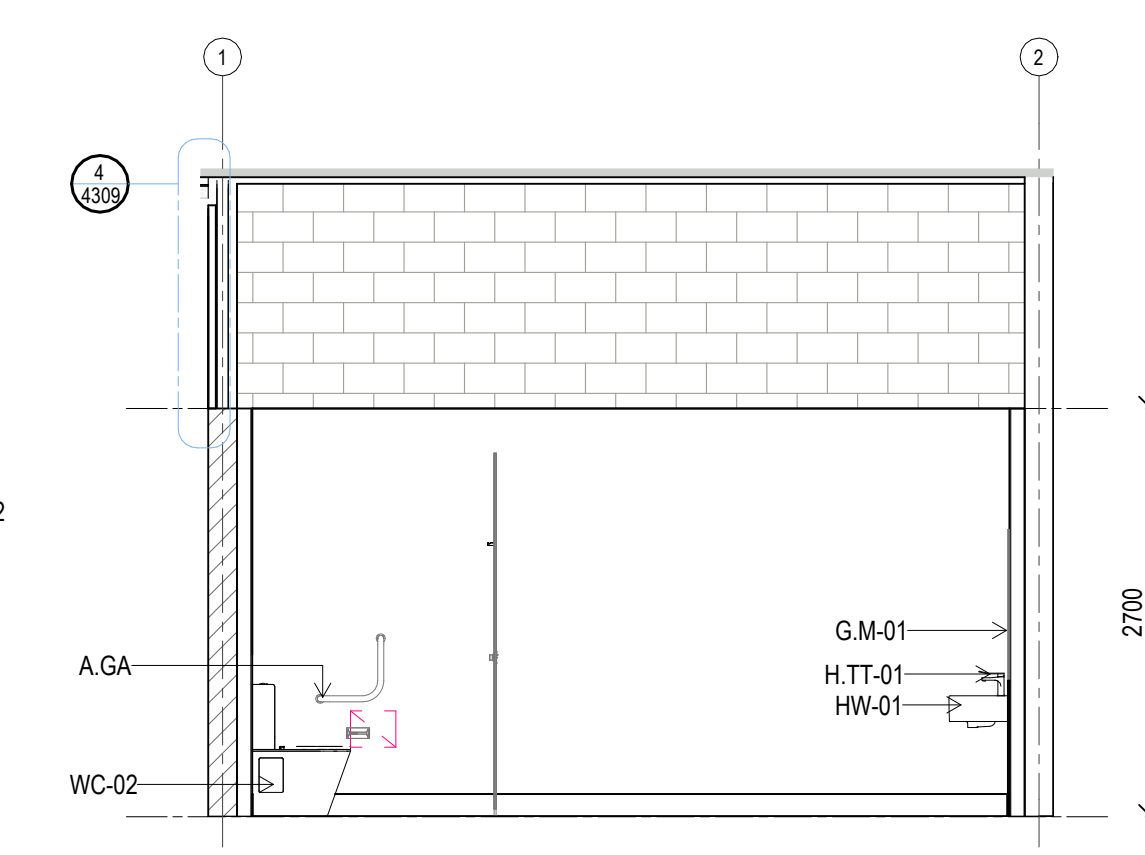


B ELEVATION AMENITIES M
Scale: 1:50

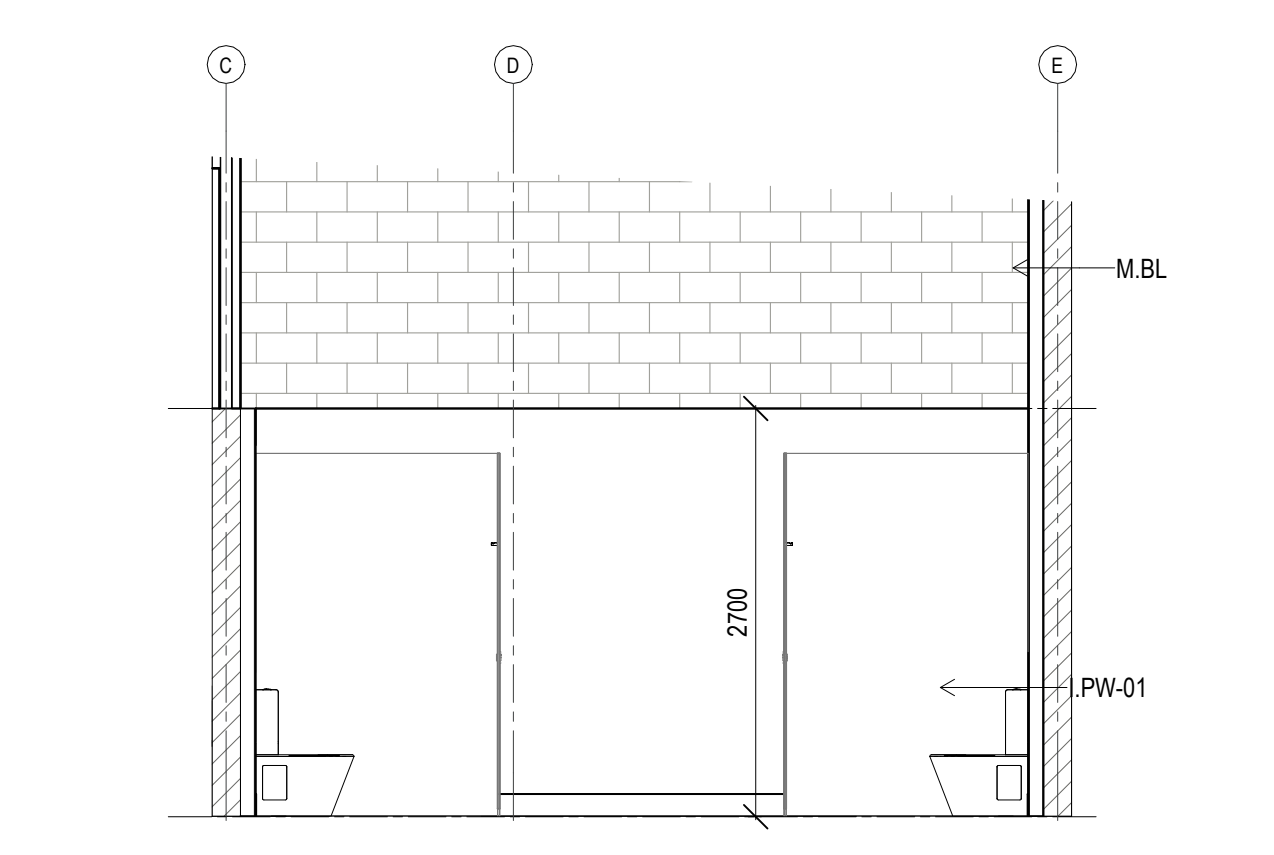


F ELEVATION AMENITIES F
Scale: 1:50

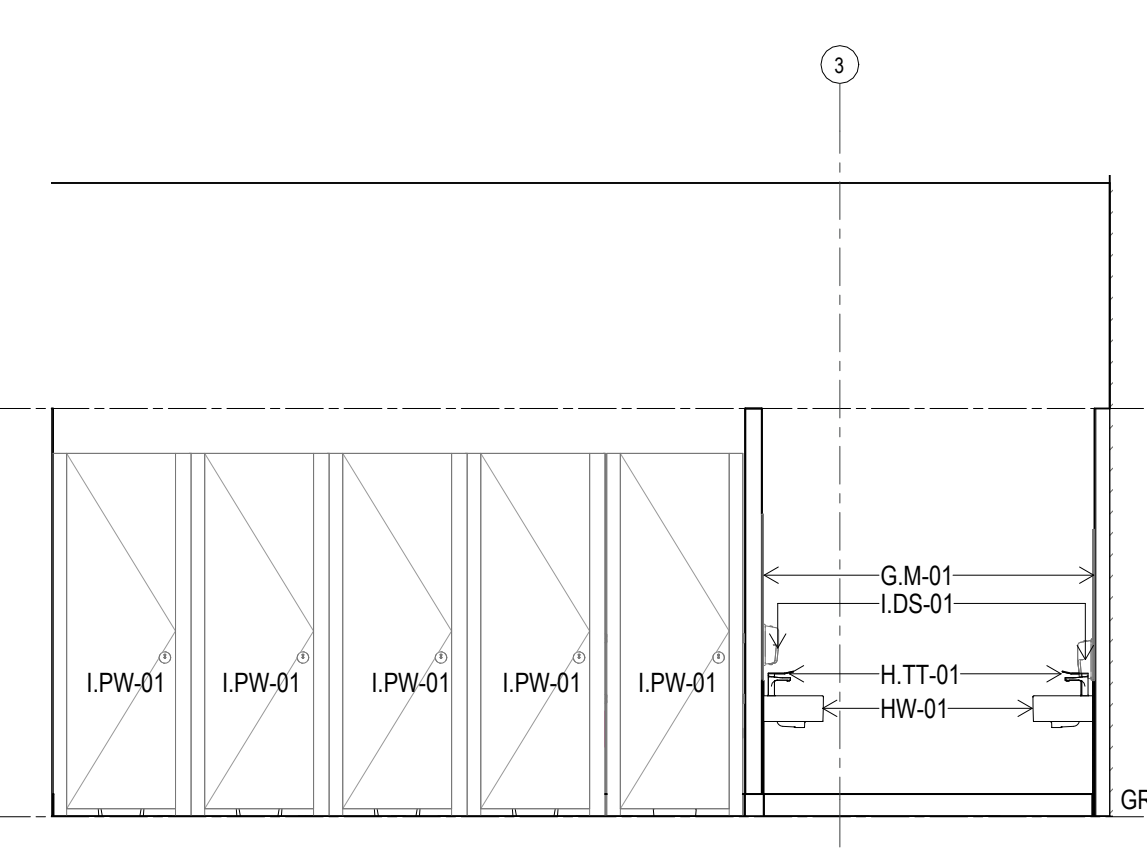


G ELEVATION AMENITIES F
Scale: 1:50

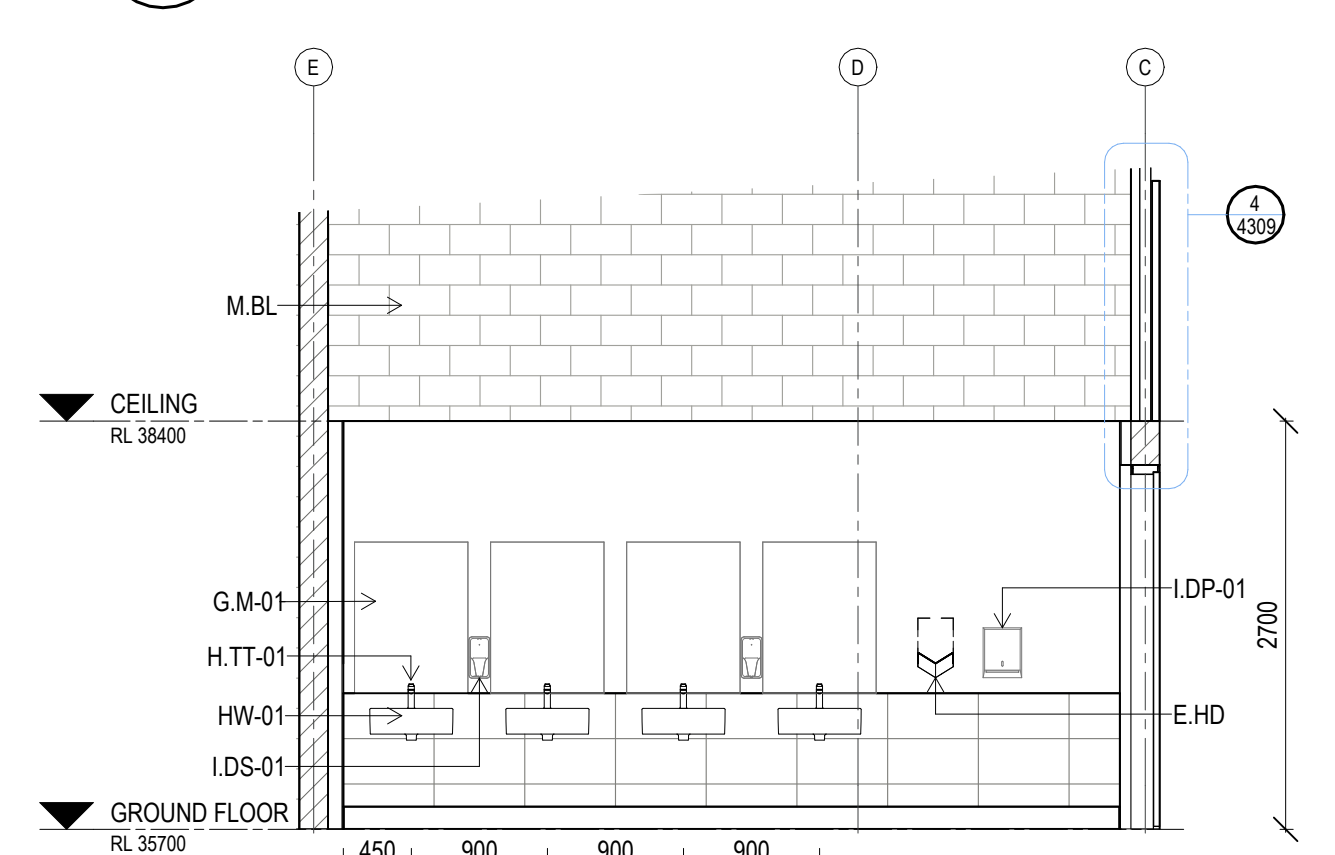


C ELEVATION AMENITIES M
Scale: 1:50

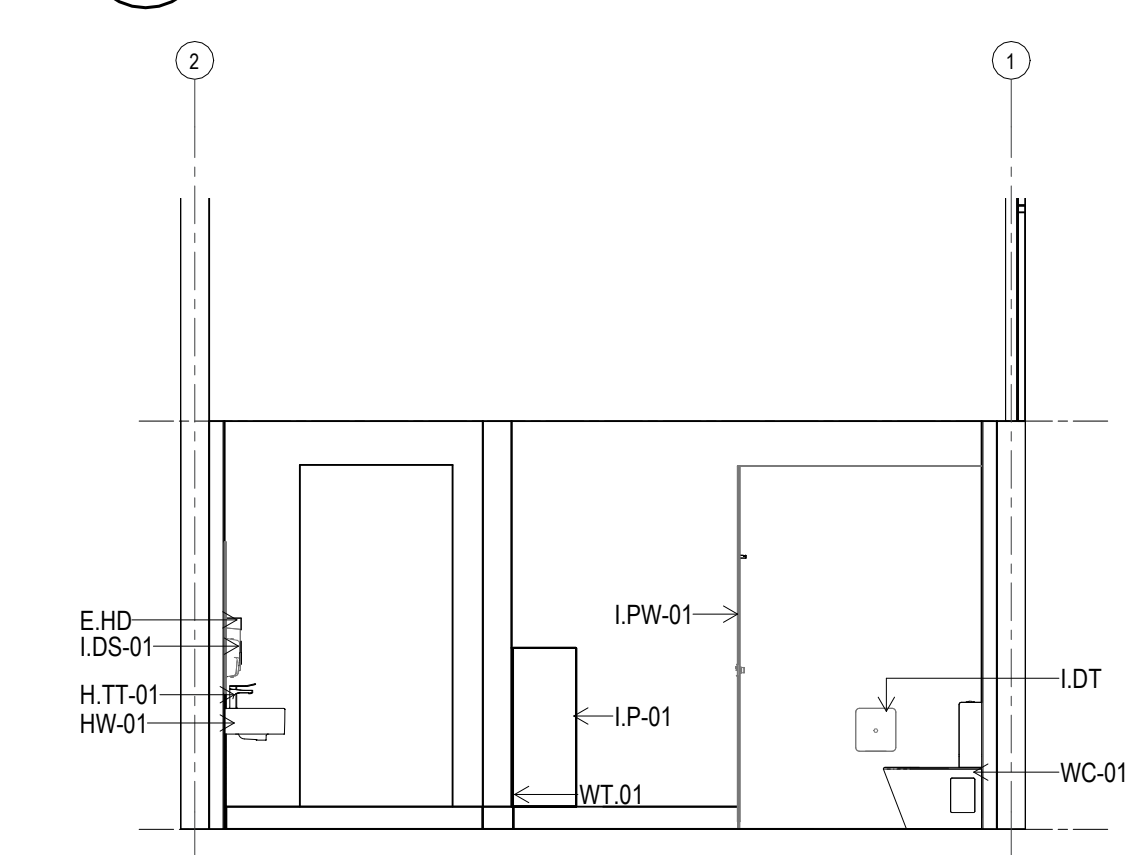


D ELEVATION AMENITIES M
Scale: 1:50

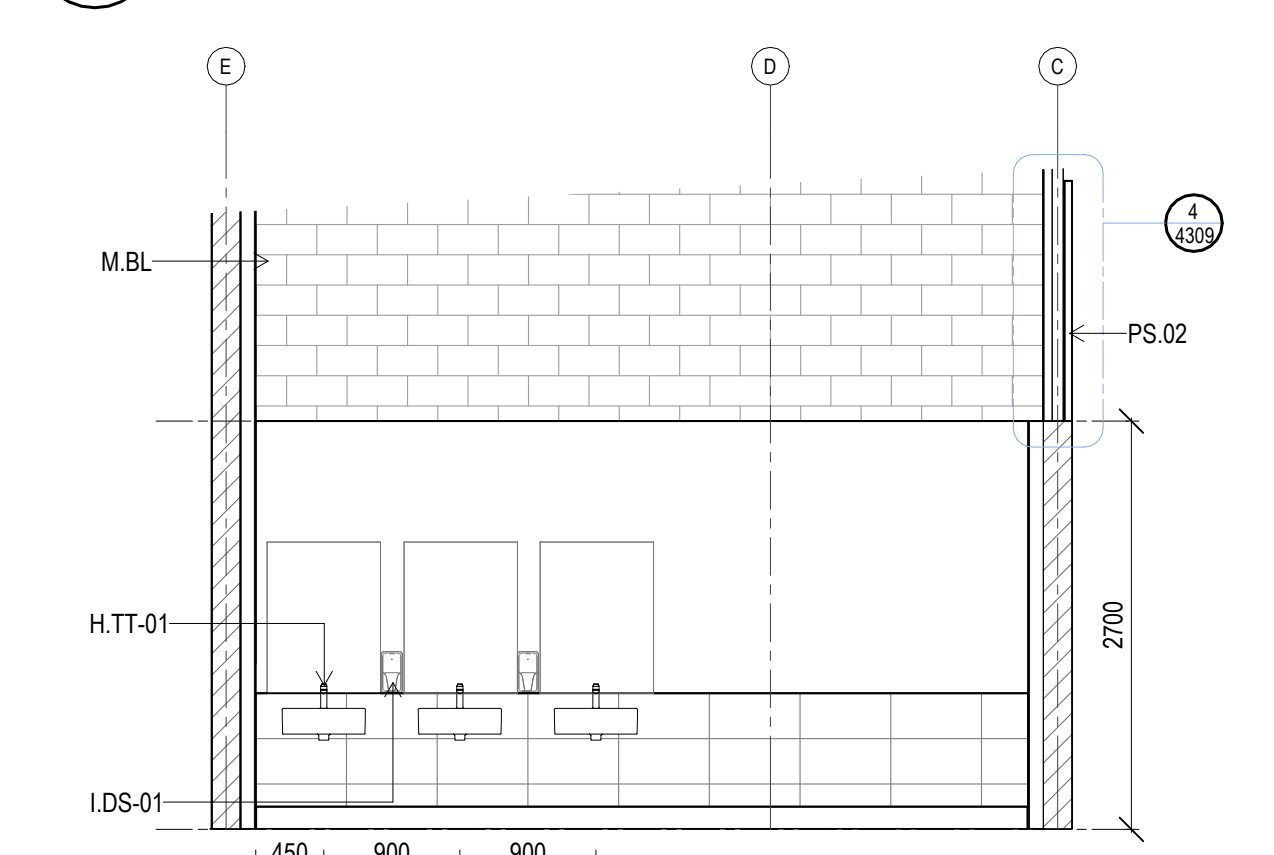


H ELEVATION AMENITIES F
Scale: 1:50

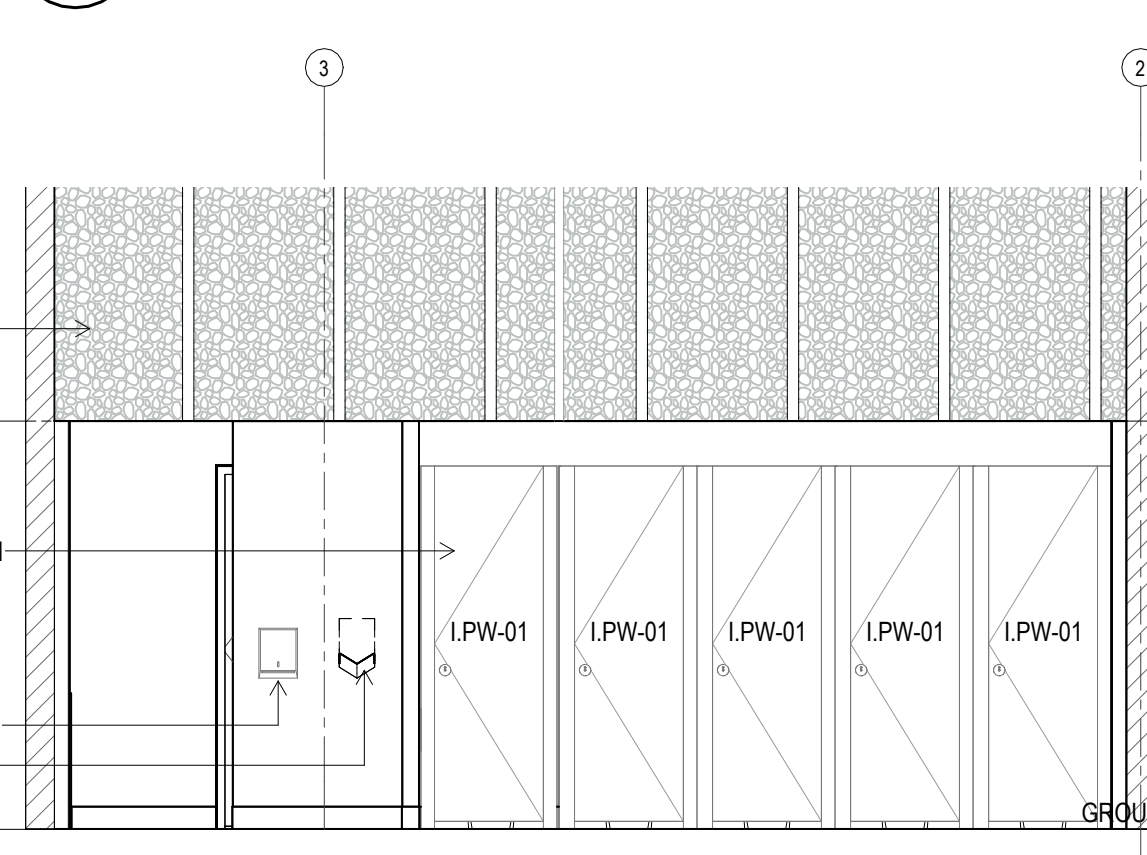


J ELEVATION AMENITIES F
Scale: 1:50

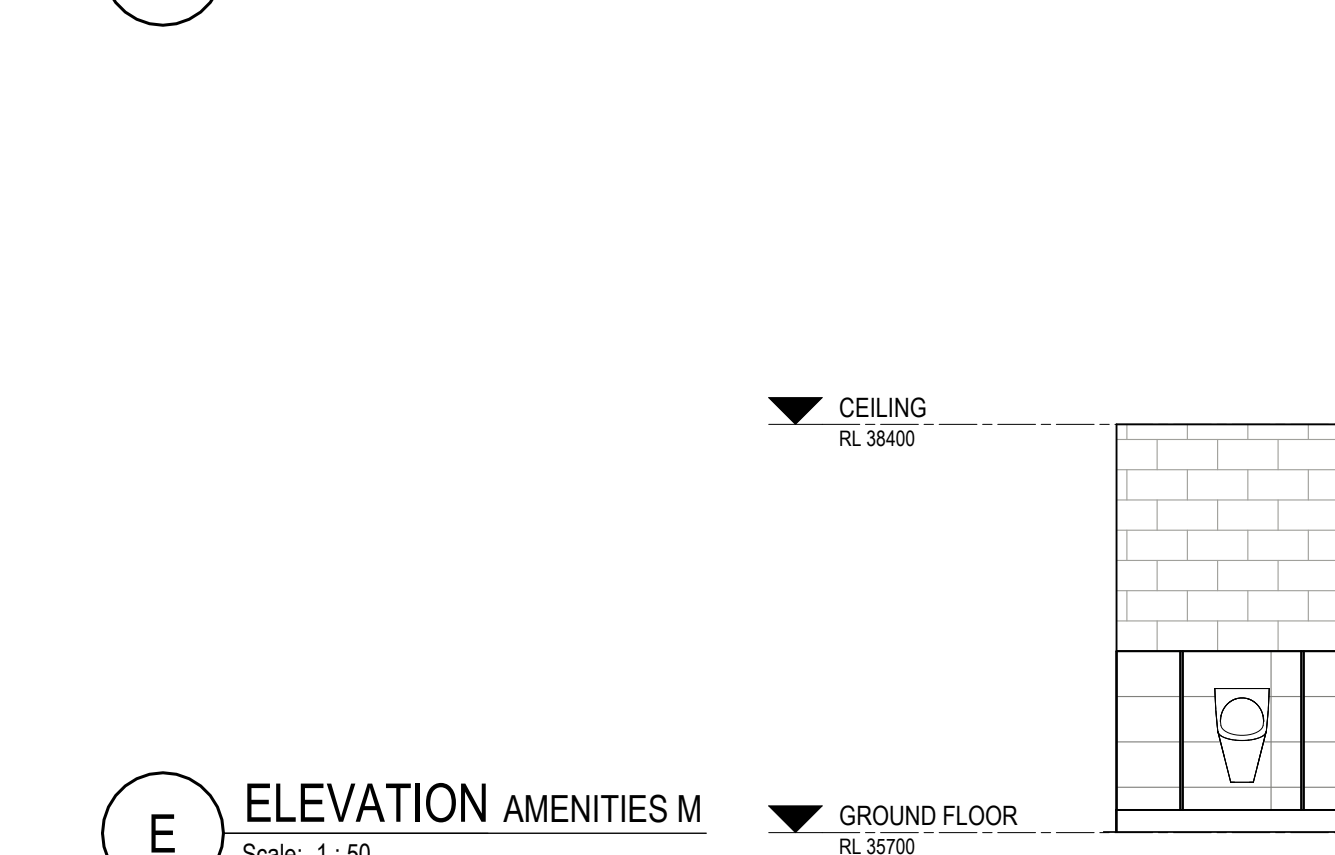

E ELEVATION AMENITIES M
Scale: 1:50

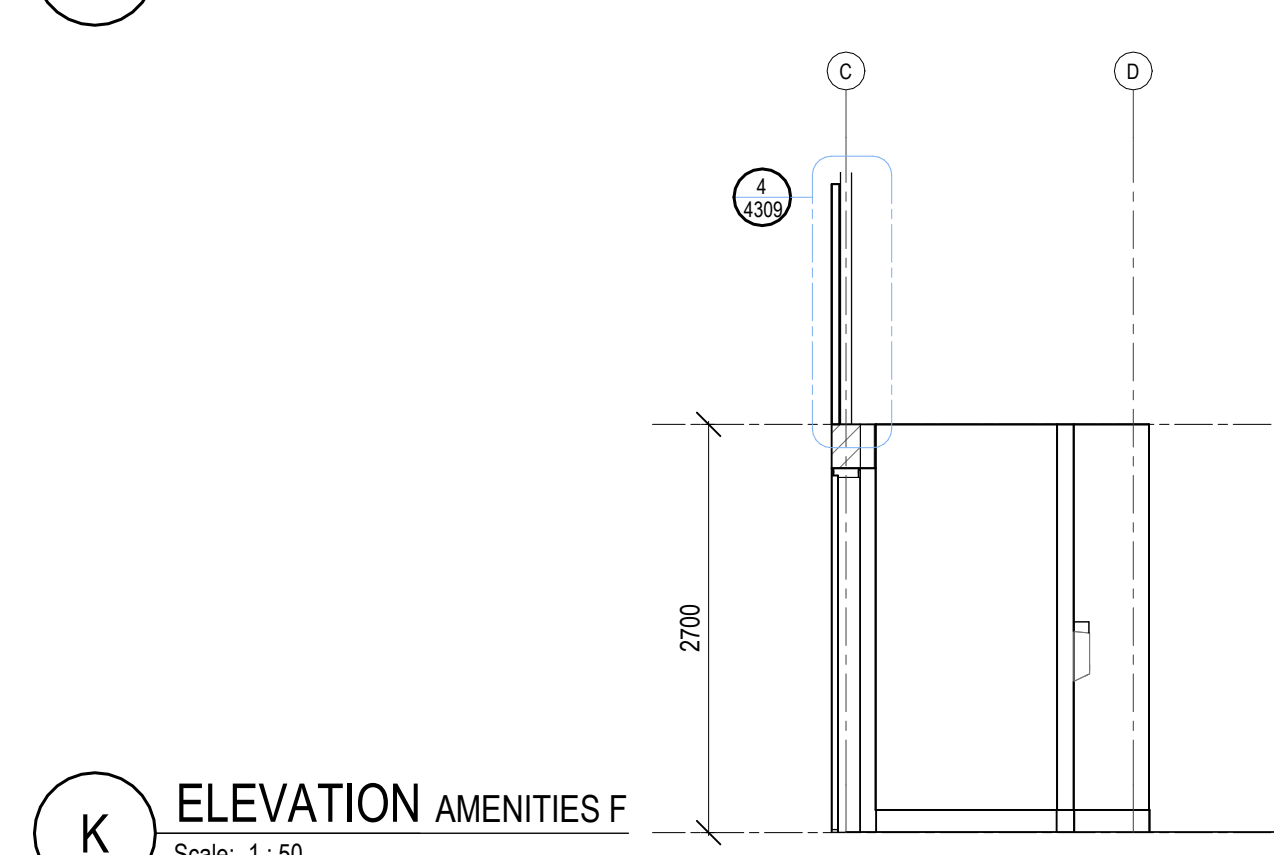

K ELEVATION AMENITIES F
Scale: 1:50

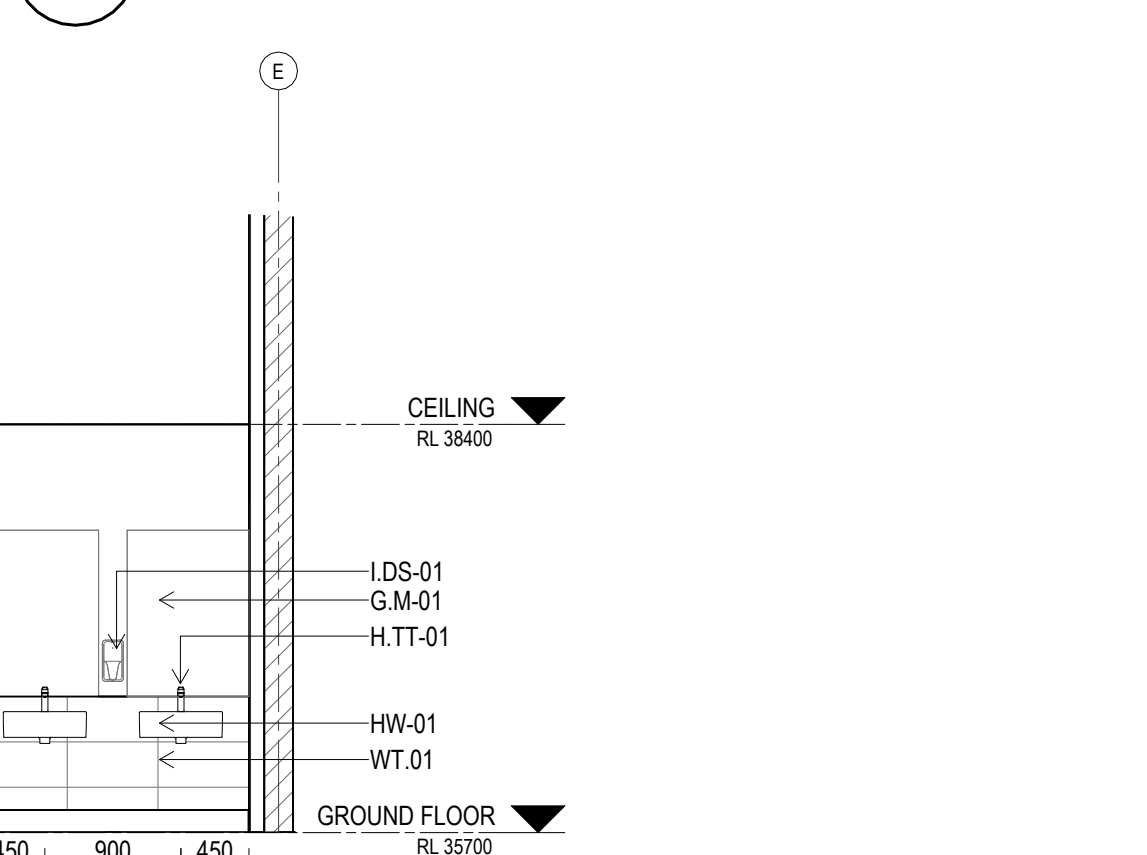

J ELEVATION AMENITIES F
Scale: 1:50

These designs and plans are the copyright of MODE DESIGN Corp. Pty Ltd and cannot be reproduced without written permission.

- Verify all dimensions on site prior to commencement of work.
- DO NOT scale off these drawings.
- Report any discrepancies to the architect before carrying out any work.

AMENDMENTS				
REV	DESCRIPTION	AUTH	CHK	DATE
T1	ISSUE FOR TENDER	DW	GB	18/06/26

NOTE:
- REFER TO AR-NBC-0010 FOR CODE LIST.

ROOM LAYOUT NOTES

SUBMIT SHOP DRAWINGS OF ALL JOINERY ITEMS FOR REVIEW PRIOR FABRICATION

REFER TO TYPICAL FIXTURE HEIGHT SETOUT FOR FIXTURE MOUNTING HEIGHTS - ALL FIXTURE SETOUTS ARE NOMINAL - INSTALL TO MANUFACTURER'S DETAILS

REFER TO INTERNAL FINISHES SCHEDULE FOR ALL FINISHES INTERNAL

REFER TO FF&E SCHEDULE FOR ALL FIXTURES, FITTINGS AND EQUIPMENT SPECIFICATIONS

ALLOW FOR NOGGINS AND FRAMING TO SUPPORT ALL WALL-MOUNTED INSTALLATIONS

ALL CUBICLE DOORS TO INCLUDE PRIVACY INDICATOR LOCKSETS

REFER FF&E SCHEDULE FOR TYPE SPECIFICATION

FURNITURE & EQUIPMENT

ALL JOINERY, EQUIPMENT AND LOOSE FURNITURE SHOWN DASHED GREY ARE INDICATIVE ONLY AND TO BE PROVIDED BY OTHERS

REFER TO JOINERY SHEET (AR-4310) FOR DETAILS ON JU-01 & JU-02

NOTE:

- TYPICAL SHOWER FALL TO BE 1:80 - 1:80
- TYPICAL KITCHEN FALL TO BE 1:80 - 1:100
- TYPICAL PWD SHOWER FALL TO BE 1:80 - 1:80
- TYPICAL PWD SHOWER FALL TO BE 1:80 - 1:100

NOM. REG. Architect: Rhonan O'Brien QLD 2350 NSW 7176 VIC 16182 TAS 1216 NZ 4712, Peter Bertram QLD 2333 WA 2143 NT AR1213

STATUS
ISSUED FOR TENDER

0m 0.5 1 1.5 2 2.5

BRISBANE

mode

Plaza Level, Mosaic
826 Ann St
Fortitude Valley QLD 4006
T +61 7 3253 9900
bne@modedesign.com.au
ABN: 65 112 807 931

Rockhampton Regional Council

CLIENT
SPORTENG™

PROJECT
ROCKHAMPTON NETBALL CENTRE (STAGE 1) - NETBALL CLUBHOUSE
554-700 YAAMBA ROAD, NORMAN GARDEN - 4701

DRAWING TITLE
ROOM LAYOUT - AMENITIES M / AMENITIES F

DRAWN	CHKD
DW	SM
ISSUE	SCALE @ A1
17/06/2026 2:42:30 PM	As indicated
PROJECT No	STAGE
24523	IFT
DRAWING No	REVISION
AR-NBC-3008	T1