

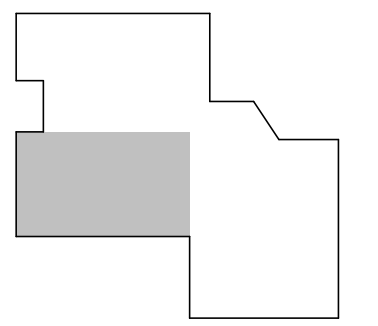


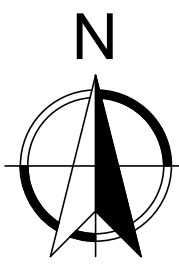

KEYPLAN

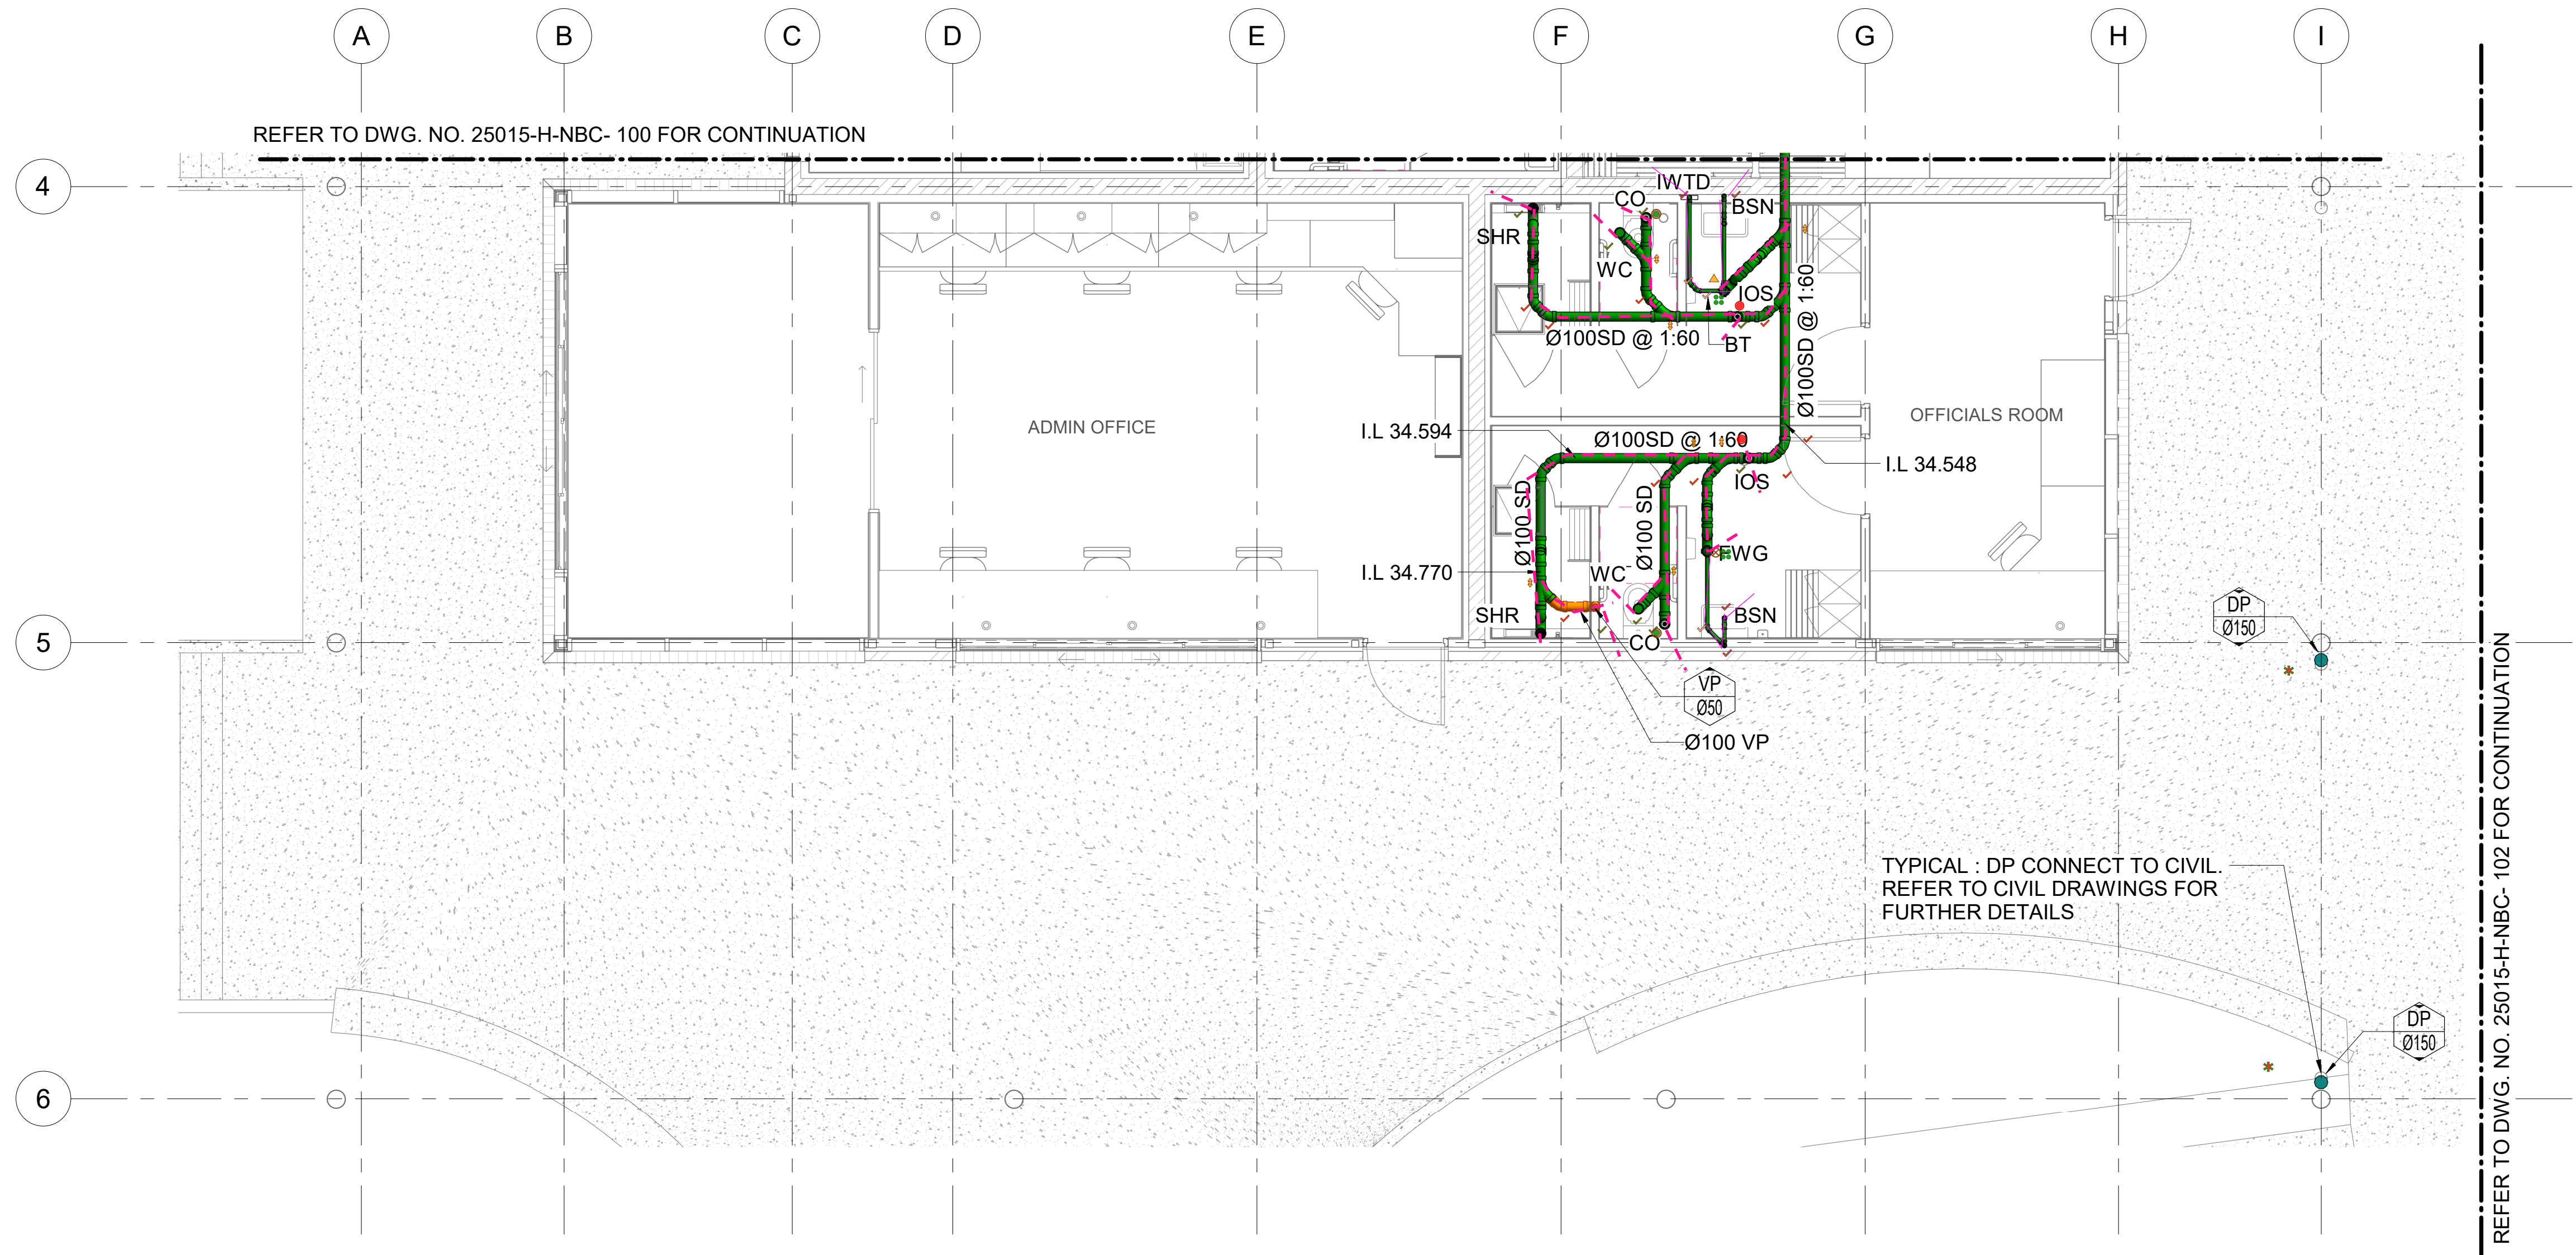

GROUND FLOOR SANITARY PLUMBING LAYOUT - PART 2
1 : 50

0 1 1 2 2 3 3 4 4 5 5m
SCALE 1:50 AT A1 SHEET | 1:100 AT A3 SHEET

ALL DIMENSIONS SHOWN IN MM. DO NOT SCALE FROM DRAWINGS.
DIMENSIONS TAKE PRECEDENCE. IF IN DOUBT REFER TO HK SOLUTIONS.

T1	ISSUE FOR TENDER	17.06.2026	MC	HKS	 ENGINEERING PROJECT MANAGEMENT DARWIN, GEELONG, CAIRNS, TOWNSVILLE, PERTH, BALLARAT admin@hksolutions.com.au www.hksolutions.com.au
REV.	DESCRIPTION	DATE	INT.	COMPANY	Conditions of use. This document may only be used by Harris Kmon Solutions clients for the purpose for which it was prepared and must not be used by any other person or for any other purpose.
REVISIONS					

SPORTENG™

DRAWN	AL
CHECKED	MC
DESIGNED	MC
CHECKED	LM
APPROVED	

THIS DRAWING MUST
NOT BE USED FOR
CONSTRUCTION UNLESS
SIGNED AS APPROVED

STAGE 1	
ROCKHAMPTON SPORTS PRECINCT - NETBALL CLUBHOUSE	
554-700 YAAMBA ROAD, NORMAN GARDEN - 4701	
GROUND FLOOR SANITARY PLUMBING LAYOUT - PART 2	

PAGE No	PROJECT No - DRAWING No	DISCIPLINE	REV.	SHEET SIZE
05 of 10	25015-H-NBC-101	HYDRAULIC	T1	A1

FOR TENDER

DRAWINGS TO BE PRINTED IN COLOUR