
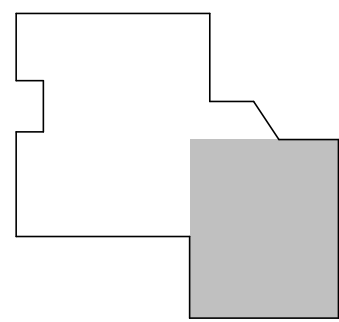


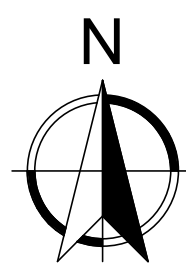

KEYPLAN

FLEXIBLE JOINT AS PER AS/NZS 3500.2, APPENDIX G CLASSIFICATION H1. REFER TO DRAWING NO. H300 FOR DETAILS.

Ø50 TW FOR DRINKING FOUNTAIN

Ø50 TD FOR RPZD DRAIN

Ø50 TD FOR ICE MAKER

Ø50 TW FOR COFFE MACHINE

PROVIDE IWTD FOR MECHANICAL CONDENSATE DRAIN (TYPICAL)

REFER TO DWG. NO. 25015-H-NBC-101 FOR CONTINUATION

J

K

L

M

N

3

4

5

6

7

Ø100SD @ 1:60

I.L. 34.769

Ø110 TW

Ø110 TW

IOW

I.L. 34.040

TO BINWASH. FOR CONTINUATION
REFER TO SITE DRAWING 25015-H003

DP
Ø150

FOR CONTINUATION REFER TO
SITE DRAWING 25015-H003

Ø100 VP TO ABOVE ROOF. VP TO TERMINATE
300mm ABOVE THE ROOF SHEET

1500 LITRES GIT VIKING PANELT.M
INGROUND, OR EQUALLY APPROVED

DP
Ø150

Ø50 TD FOR RPZD DRAIN

Ø50 TD FOR HWS SAFETY TRAY


RHEEM
HEAVY DUTY ELECTRIC - INDOOR/OUTDOOR -
315L - 3 x 3.6kW 500L \ FIRST HOUR DELIVERY
@ 50oC RISE MODEL 61331507
OR EQUALLY APPROVED
COMPLETE WITH SAFETY TRAY AS PER THE
AS3500 WITH PTR VALVE TO RUN TO OUTLET
OF THE TRAY AND HAVE AN AIR GAP
BETWEEN TRAY OUTLET AND PTR VALVE
RELEASED PIPE.

DP
Ø150

DP
Ø150

TYPICAL : DP CONNECT TO CIVIL.
REFER TO CIVIL DRAWINGS FOR
FURTHER DETAILS

DP
Ø150

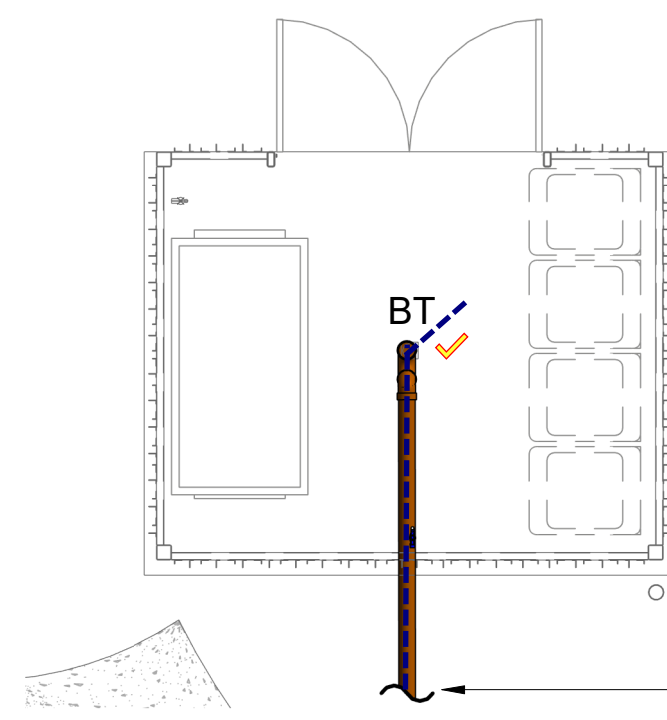

FOR CONTINUATION
REFER TO SITE DRAWING
25015-H003

NBC BINWASH SANITARY LAYOUT

1 : 50

0 1 1 2 2 3 3 4 4 5 5m
SCALE 1:50 AT A1 SHEET | 1:100 AT A3 SHEET

ALL DIMENSIONS SHOWN IN MM. DO NOT SCALE FROM DRAWINGS.
DIMENSIONS TAKE PRECEDENCE. IF IN DOUBT REFER TO HK SOLUTIONS.

GROUND FLOOR SANITARY PLUMBING LAYOUT - PART PLAN 3

1 : 50

FOR TENDER



ENGINEERING
PROJECT MANAGEMENT
DARWIN, GEELONG,
CAIRNS, TOWNSVILLE,
PERTH, BALLARAT
admin@hksolutions.com.au
www.hksolutions.com.au

Conditions of use. This document may only be used by
Harris Kmon Solutions clients for the purpose for which
it was prepared and must not be used by any other
person or for any other purpose.

SPORTENG™

DRAWN AL
CHECKED MC
DESIGNED MC
CHECKED LM
APPROVED

THIS DRAWING MUST
NOT BE USED FOR
CONSTRUCTION UNLESS
SIGNED AS APPROVED

STAGE 1

ROCKHAMPTON SPORTS PRECINCT - NETBALL CLUBHOUSE
554-700 YAAMBA ROAD, NORMAN GARDEN - 4701

GROUND FLOOR SANITARY PLUMBING LAYOUT - PART 3

PAGE No	PROJECT No - DRAWING No	DISCIPLINE	REV.	SHEET SIZE
06 of 10	25015-H-NBC-102	HYDRAULIC	T1	A1

DRAWINGS TO BE PRINTED IN COLOUR