
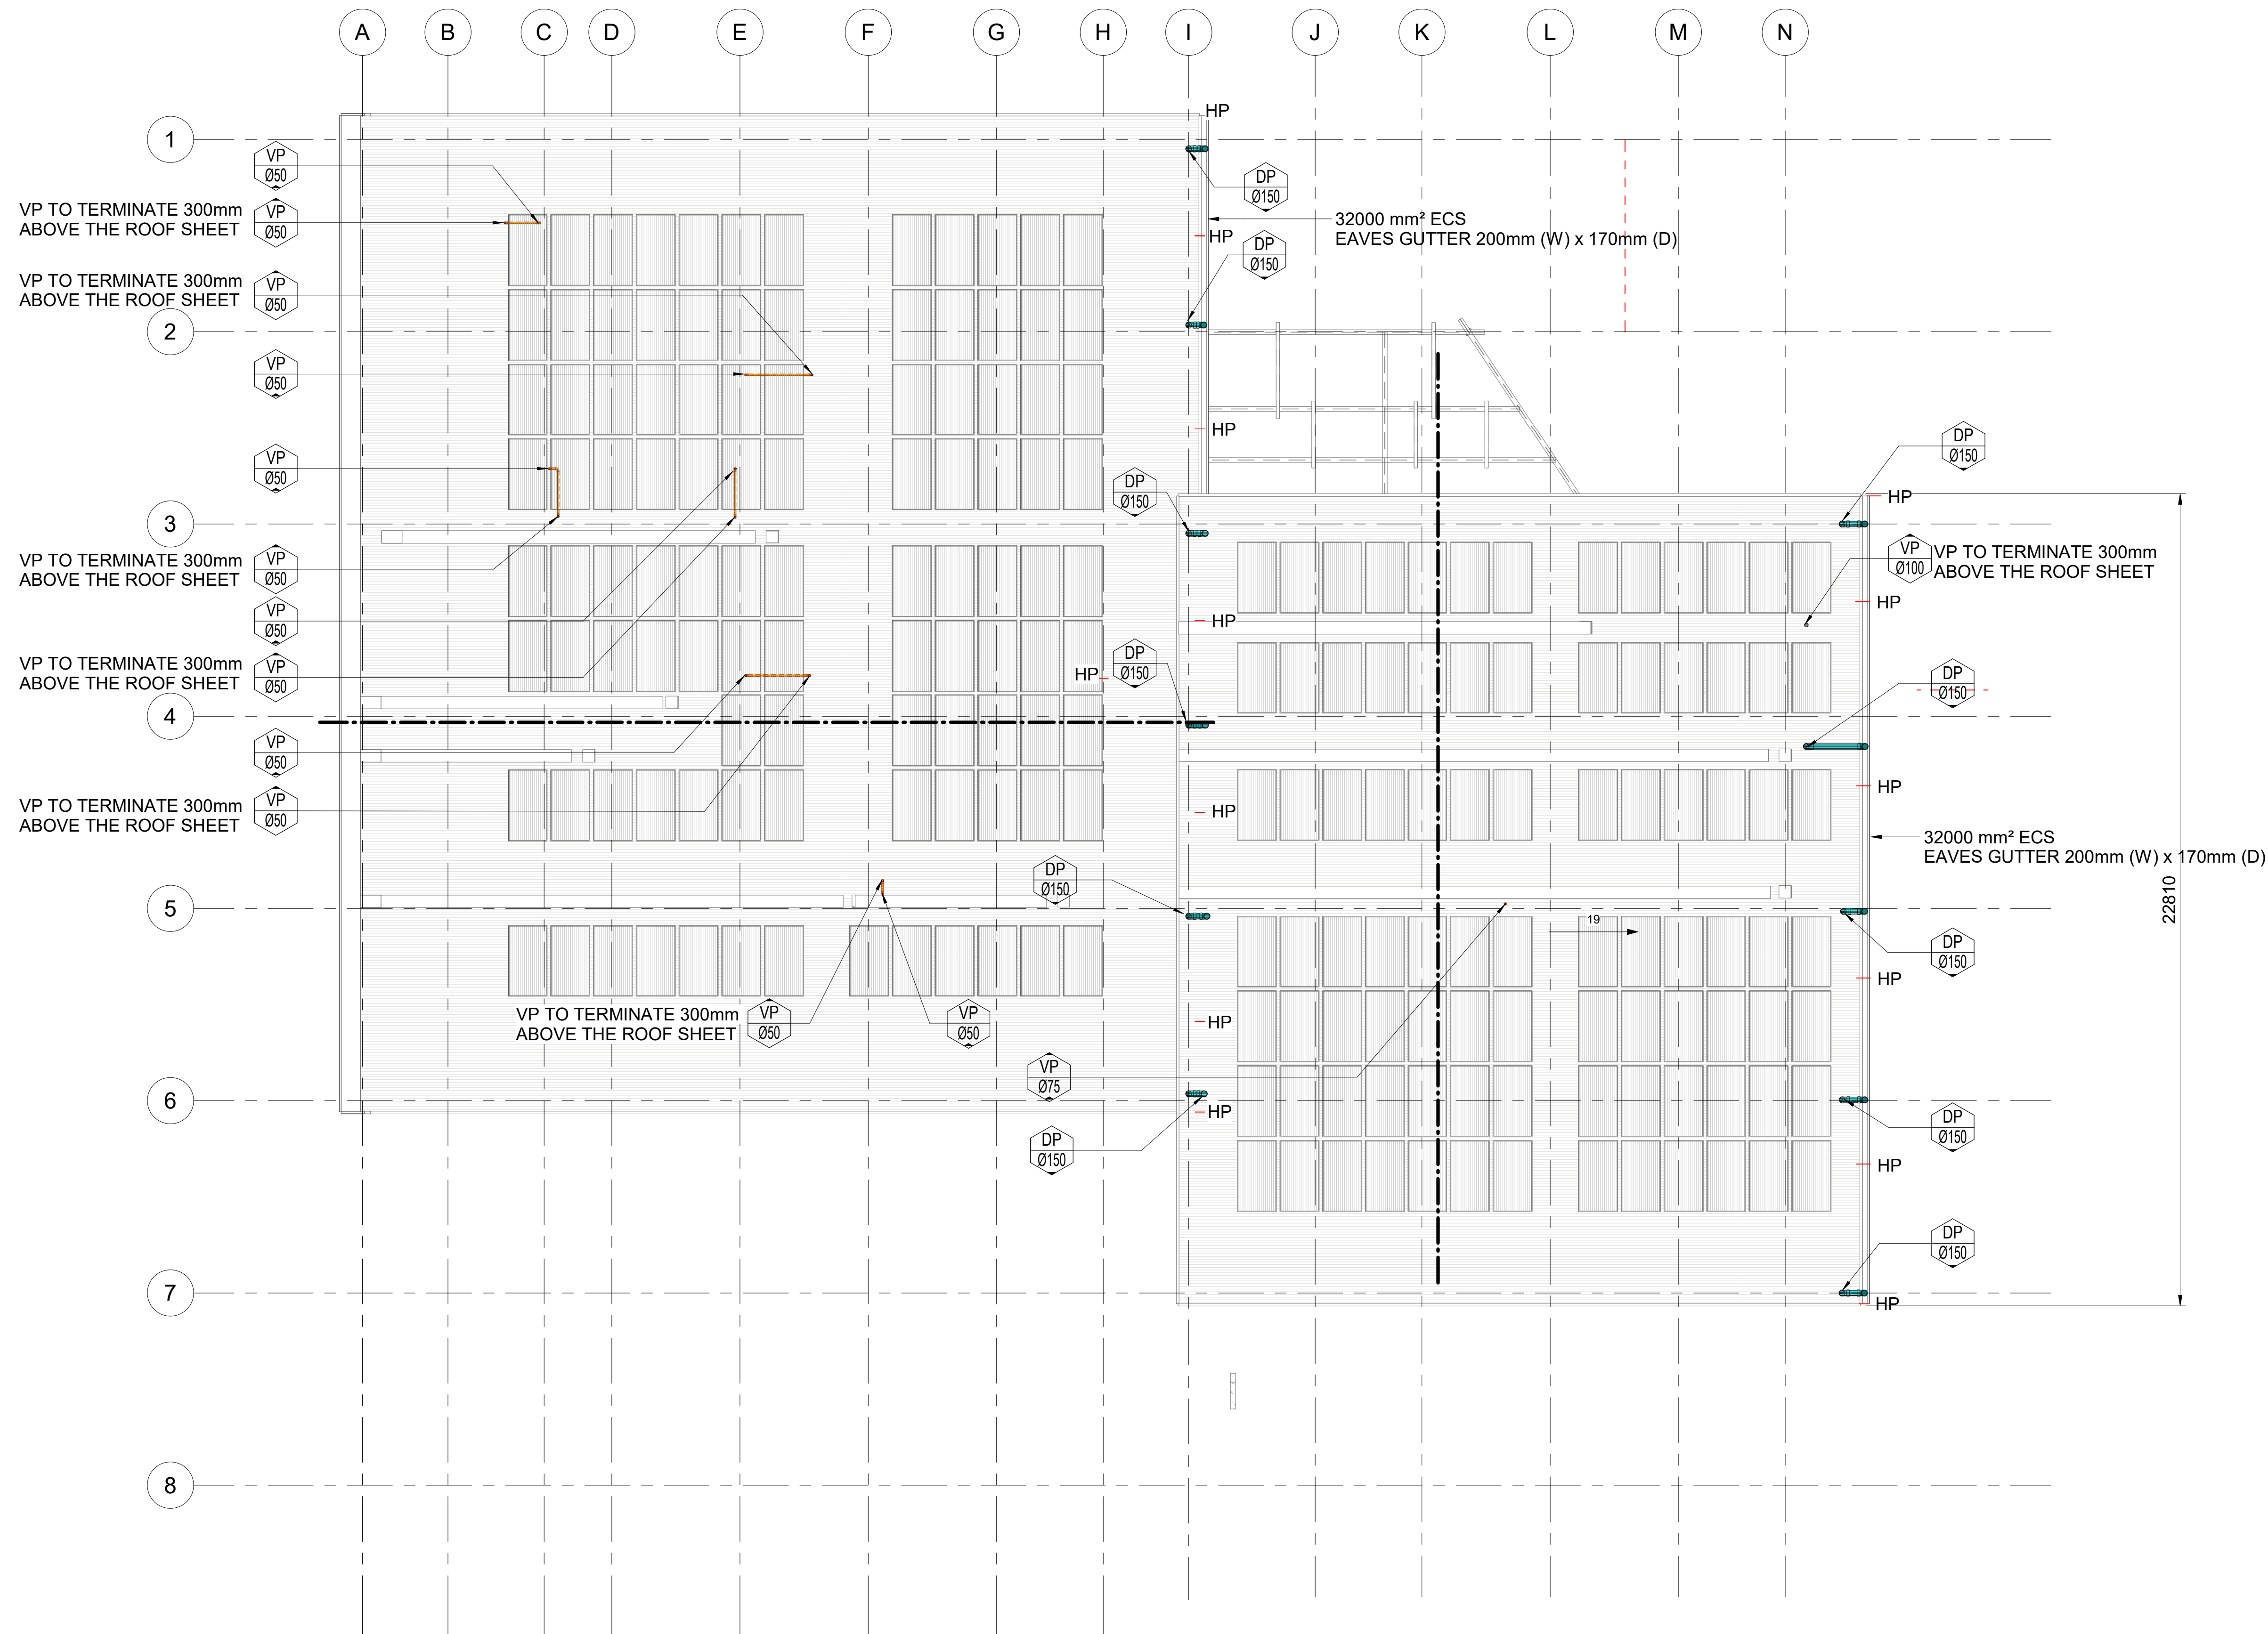


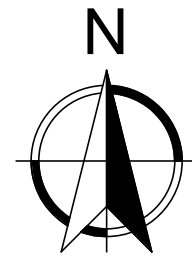

0 1 2 3 4 5 6 7 8 9 10m
SCALE 1:100 AT A1 SHEET | 1:200 AT A3 SHEET

ALL DIMENSIONS SHOWN IN MM. DO NOT SCALE FROM DRAWINGS.
DIMENSIONS TAKE PRECEDENCE. IF IN DOUBT REFER TO HK SOLUTIONS.

ROOF LEVEL STORM WATER LAYOUT
SCALE 1 : 100

FOR TENDER

						H K Solutions ENGINEERING PROJECT MANAGEMENT DARWIN, GEELONG, CAIRNS, TOWNSVILLE PERTH, BALLARAT admin@hksolutions.com.au www.hksolutions.com.au
T1	ISSUE FOR TENDER		17.06.2026	MC	HKS	Conditions of use. This document may only be used by Harris Kmon Solutions clients for the purpose for which it was prepared and must not be used by any other person or for any other purpose.
REV.	DESCRIPTION	DATE	INT.	COMPANY		
REVISIONS						

SPORTENG™

DRAWN	AL
CHECKED	MC
DESIGNED	MC
CHECKED	LM
APPROVED	

THIS DRAWING MUST
NOT BE USED FOR
CONSTRUCTION UNLESS
SIGNED AS APPROVED

STAGE 1
ROCKHAMPTON SPORTS PRECINCT - NETBALL CLUBHOUSE
554-700 YAAMBA ROAD, NORMAN GARDEN - 4701
ROOF LEVEL STORM WATER LAYOUT

PAGE No	PROJECT No - DRAWING No	DISCIPLINE	REV.	SHEET SIZE
07 of 10	25015-H-NBC-103	HYDRAULIC	T1	A1

DRAWINGS TO BE PRINTED IN COLOUR