



### DRAWING NOTES:

ALL HOSE TAPS EXCEPT FOR GIT TAP  
WILL HAVE A VETICAL BREAK OR SINGLE  
CHECK VALVE INSTALLED.

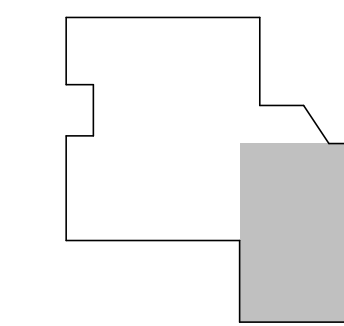

KEYPLAN

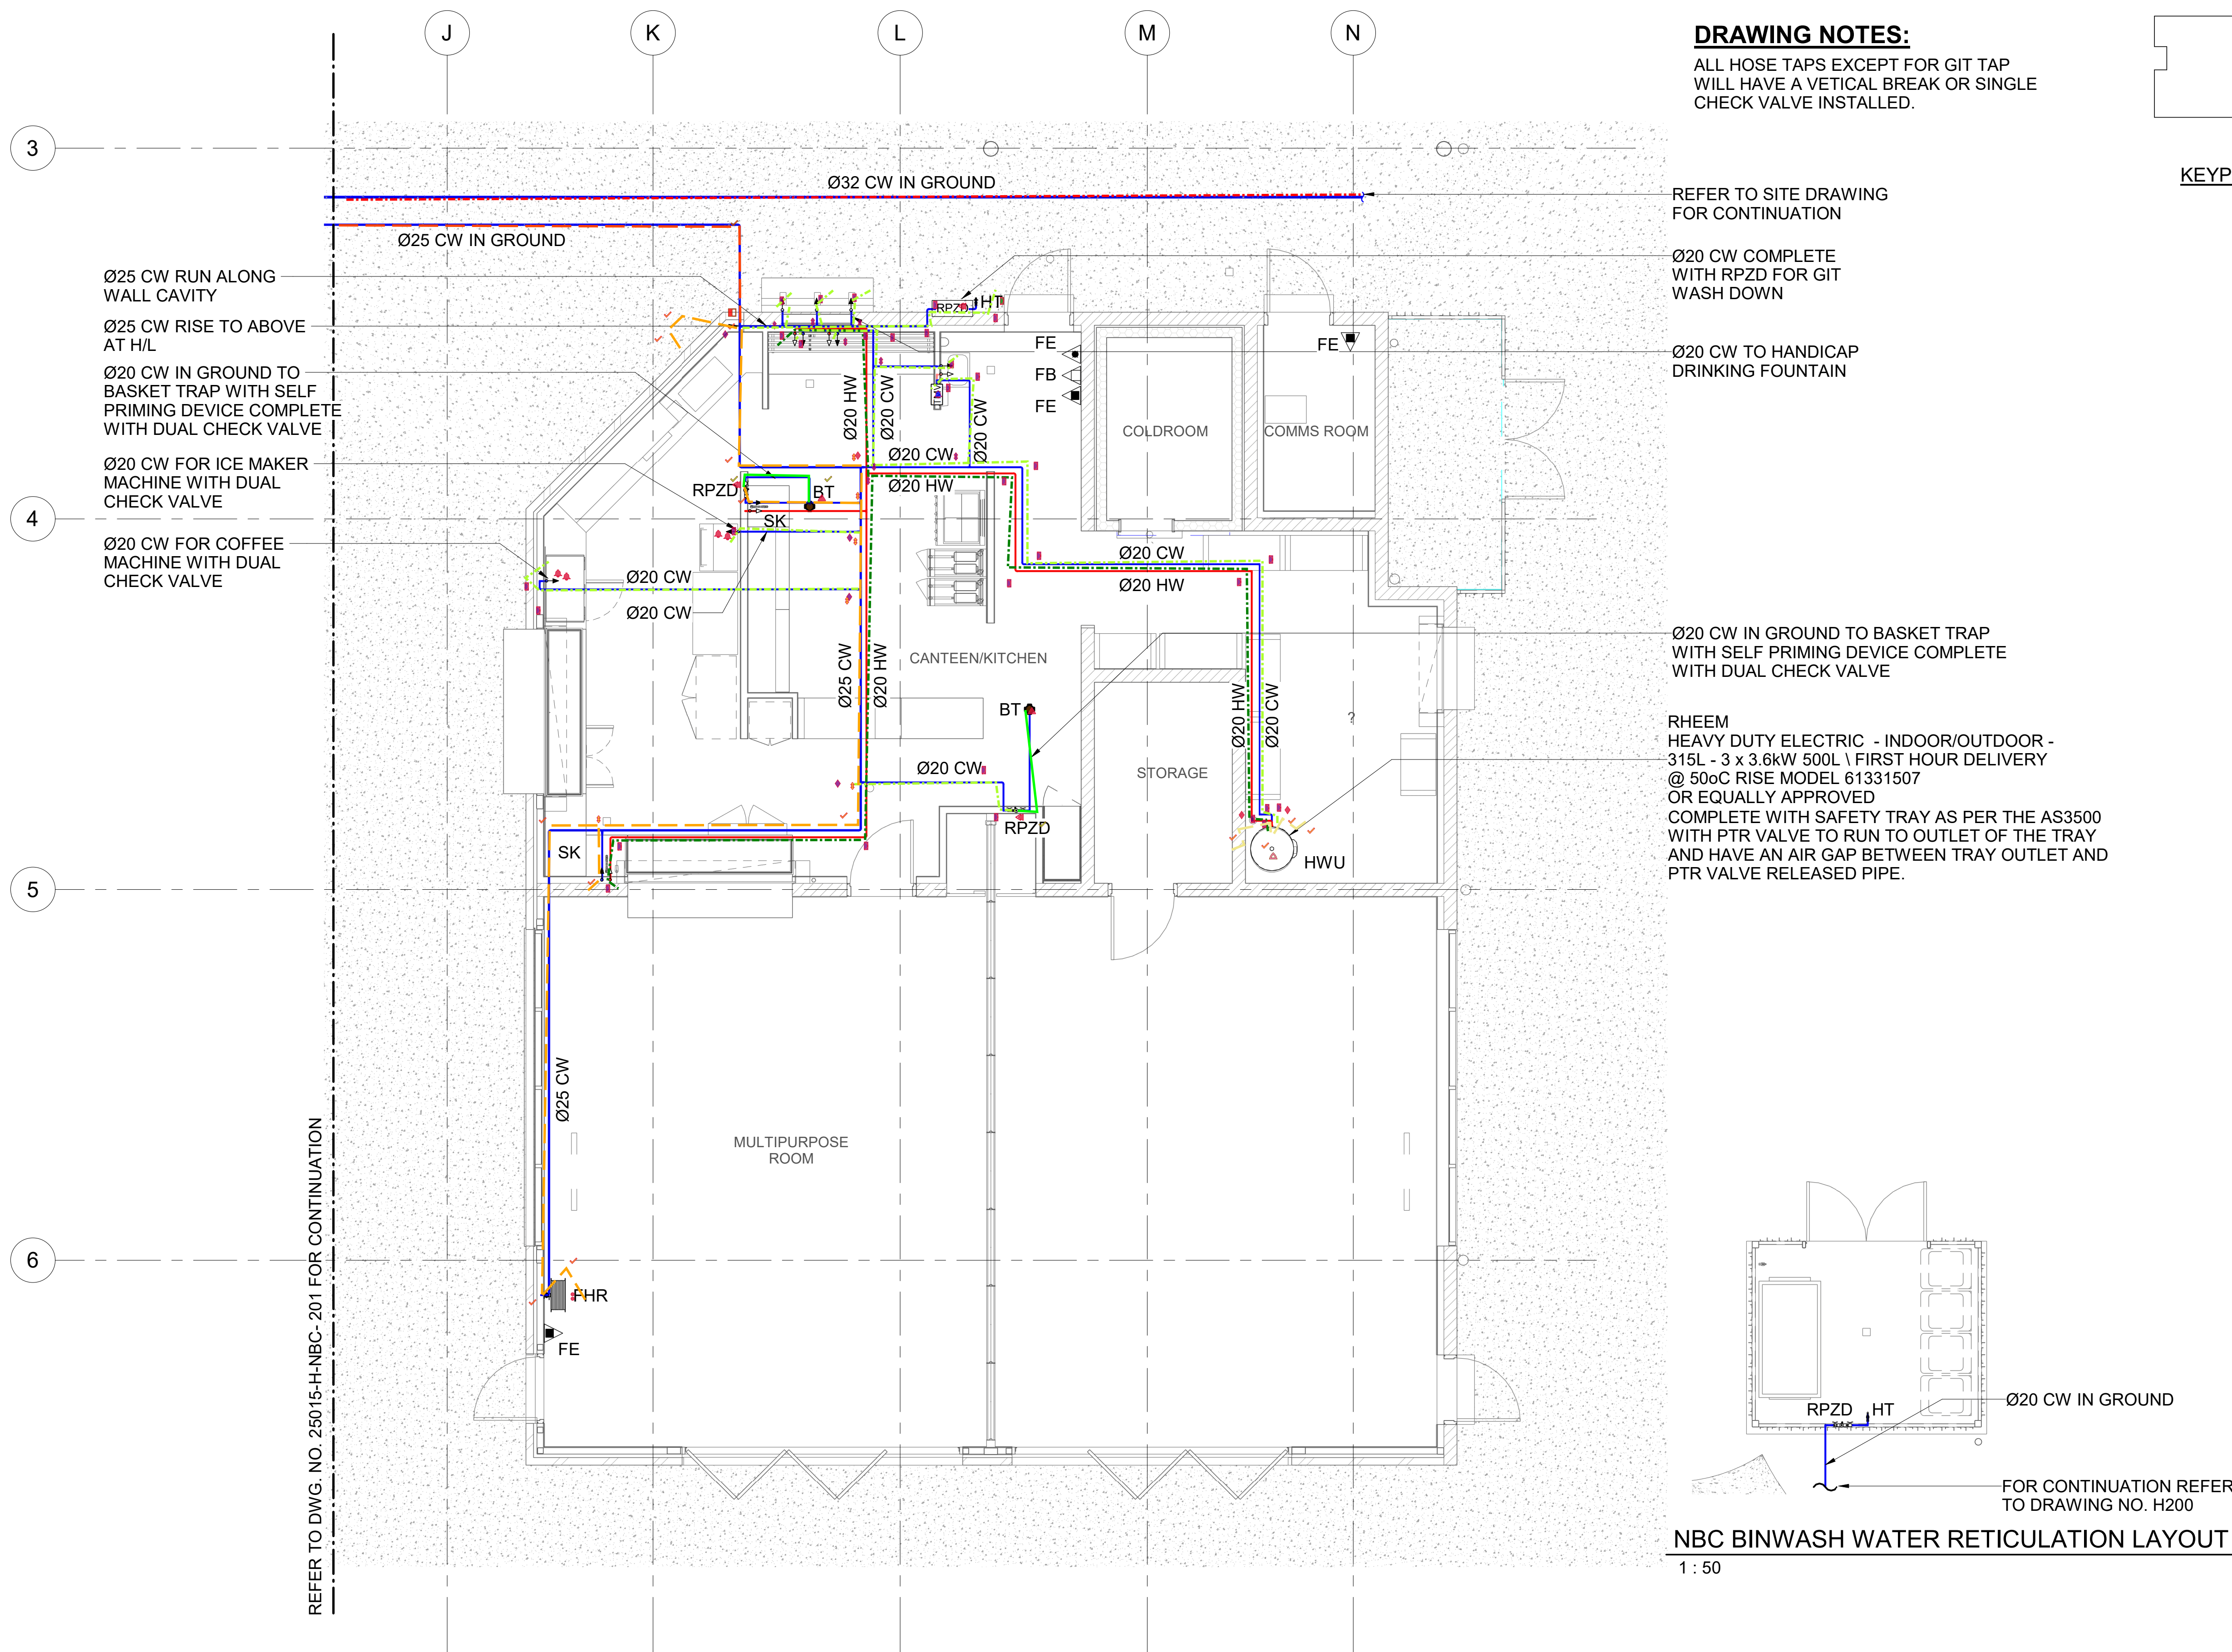


REFER TO SITE DRAWING  
FOR CONTINUATION

Ø20 CW COMPLETE  
WITH RPZD FOR GIT  
WASH DOWN

Ø20 CW TO HANDICAP  
DRINKING FOUNTAIN

Ø20 CW IN GROUND TO BASKET TRAP  
WITH SELF PRIMING DEVICE COMPLETE  
WITH DUAL CHECK VALVE

RHEEM  
HEAVY DUTY ELECTRIC - INDOOR/OUTDOOR -  
315L - 3 x 3.6kW 500L \ FIRST HOUR DELIVERY  
@ 50oC RISE MODEL 61331507  
OR EQUALLY APPROVED  
COMPLETE WITH SAFETY TRAY AS PER THE AS3500  
WITH PTR VALVE TO RUN TO OUTLET OF THE TRAY  
AND HAVE AN AIR GAP BETWEEN TRAY OUTLET AND  
PTR VALVE RELEASED PIPE.

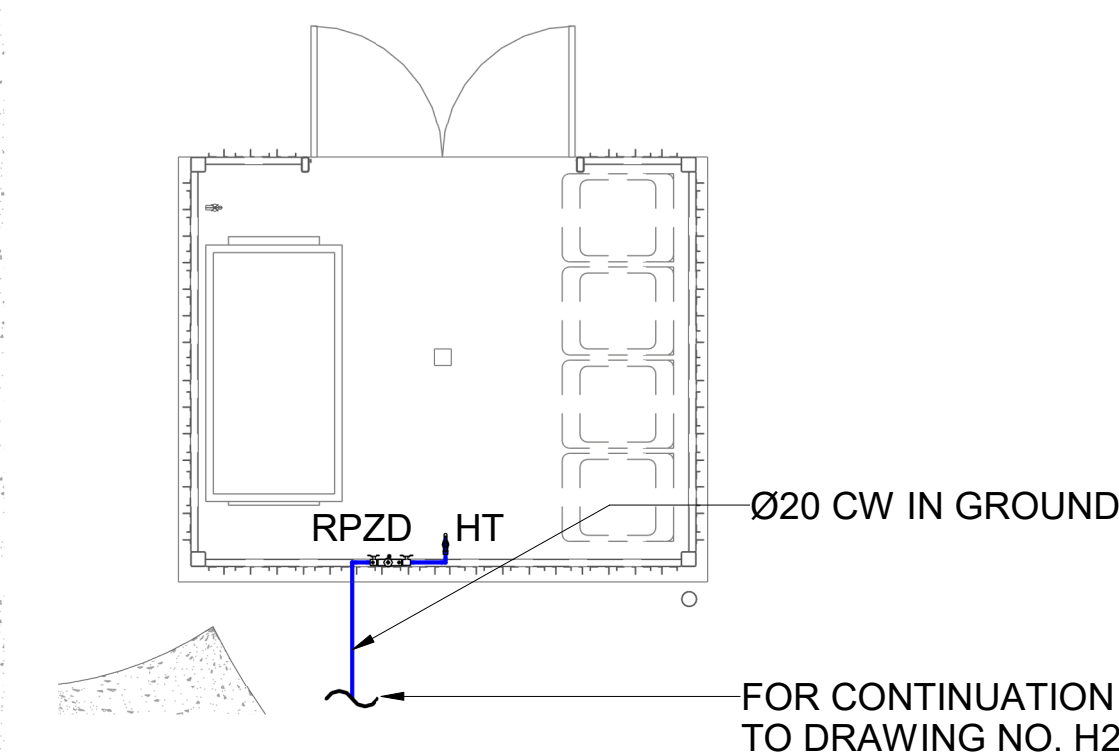

NBC BINWASH WATER RETICULATION LAYOUT

1 : 50

0 1 1 2 2 3 3 4 4 5 5m

SCALE 1:50 AT A1 SHEET | 1:100 AT A3 SHEET

ALL DIMENSIONS SHOWN IN MM. DO NOT SCALE FROM DRAWINGS.  
DIMENSIONS TAKE PRECEDENCE. IF IN DOUBT REFER TO HK SOLUTIONS.

GROUND FLOOR WATER RETICULATION LAYOUT - PART PLAN 3

1 : 50

FOR TENDER



ENGINEERING  
PROJECT MANAGEMENT  
DARWIN, GEELONG,  
CAIRNS, TOWNSVILLE,  
PERTH, BALLARAT  
admin@hksolutions.com.au  
www.hksolutions.com.au

Conditions of use. This document may only be used by  
Harris Kmon Solutions clients for the purpose for which  
it was prepared and must not be used by any other  
person or for any other purpose.

SPORTENG™

DRAWN AL  
CHECKED MC  
DESIGNED MC  
CHECKED LM  
APPROVED

THIS DRAWING MUST  
NOT BE USED FOR  
CONSTRUCTION UNLESS  
SIGNED AS APPROVED

### STAGE 1

ROCKHAMPTON SPORTS PRECINCT - NETBALL CLUBHOUSE  
554-700 YAAMBA ROAD, NORMAN GARDEN - 4701

### GROUND FLOOR WATER RETICULATION LAYOUT-PART 3

| REV. | DESCRIPTION      | DATE       | INT. | COMPANY |
|------|------------------|------------|------|---------|
| T1   | ISSUE FOR TENDER | 17.06.2026 | MC   | HKS     |

### REVISIONS

| PAGE No  | PROJECT No - DRAWING No | DISCIPLINE | REV. | SHEET SIZE |
|----------|-------------------------|------------|------|------------|
| 10 of 10 | 25015-H-NBC-202         | HYDRAULIC  | T1   | A1         |

DRAWINGS TO BE PRINTED IN COLOUR