

LEGEND:

ACCESS CHAMBER

ROAD GULLY INLET

FIELD INLET

HEADWALL INLET / OUTLET

STORMWATER PIPE / CULVERT

GRATED TRENCH DRAIN

GRASSED SWALE WITH CONCRETE-LINED INVERT

GRASSED SWALE

VEGETATED SWALE

EXISTING CREEK / SWALE


SUBSURFACE STRIP FILTER DRAIN WITH SUBSOIL CLEANOUT POINTS WHERE APPLICABLE.

LOT BOUNDARY (VISION SURVEY 10/12/2025)

NOTES:

1. REFER TO F1320 FOR GRATED TRENCH SCHEDULE AND DETAILS.

2. REFER TO IPWEA RSD-802 SUBSOIL DRAINS FOR SUBSOIL OUTLETS TO NATURAL SURFACES.

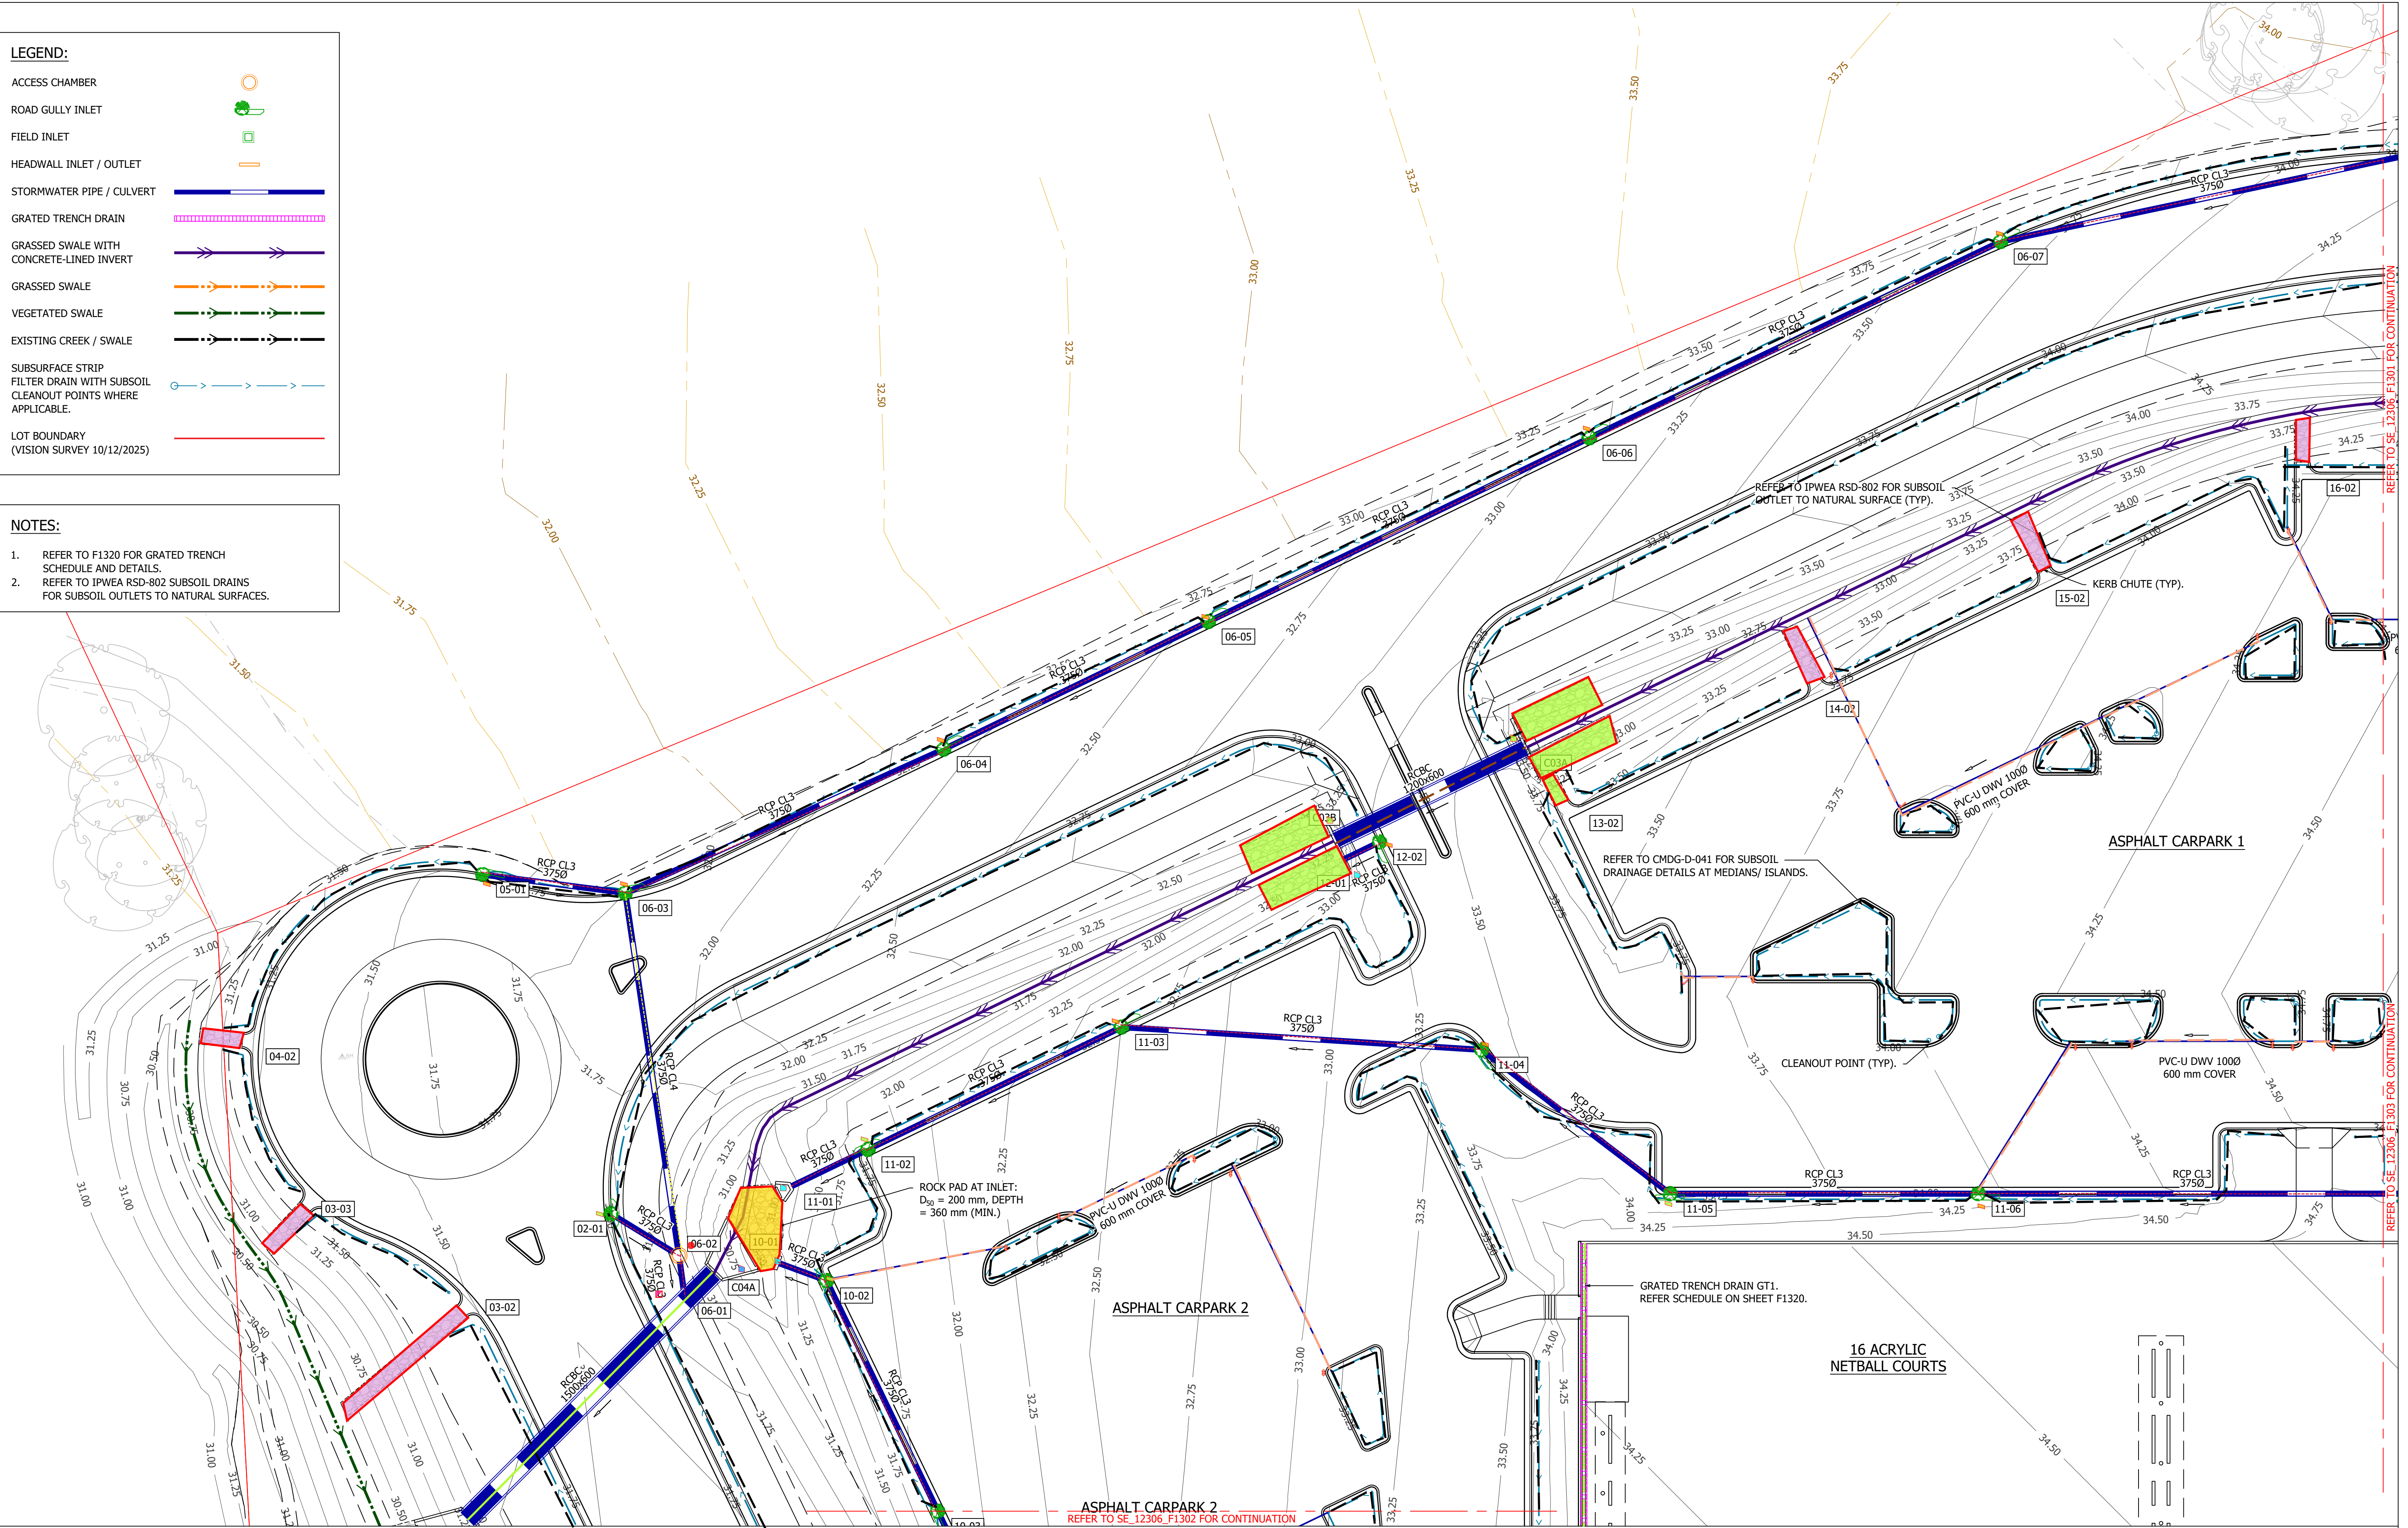

WARNING

BEWARE OF UNDERGROUND SERVICES

THE LOCATION OF UNDERGROUND SERVICES ARE APPROXIMATE ONLY. IT IS THE RESPONSIBILITY OF THE CONTRACTOR TO PROVE THEIR EXACT POSITION ON SITE. NO GUARANTEE IS GIVEN THAT ALL EXISTING SERVICES ARE SHOWN.

WARNING

OVERHEAD ELECTRICITY IN VICINITY OF WORKS

NOT FOR CONSTRUCTION



T1	17/06/26	TPC	JZV	JDH	ISSUE FOR TENDER
Issue	Date	By	Chkd	Appd	Description

Job Title
**ROCKHAMPTON
NETBALL CENTRE**

Drawing Title
**STORMWATER DRAINAGE
LAYOUT PLAN
SHEET 1**

0 1m 5m 10m 15m 20m

SCALE 1:250 @ A1

Discipline
CIVIL AND FIELD OF PLAY

Drawing Status
ISSUE FOR TENDER

Drawing Number
SE_12306_F1300

Issue
T1