



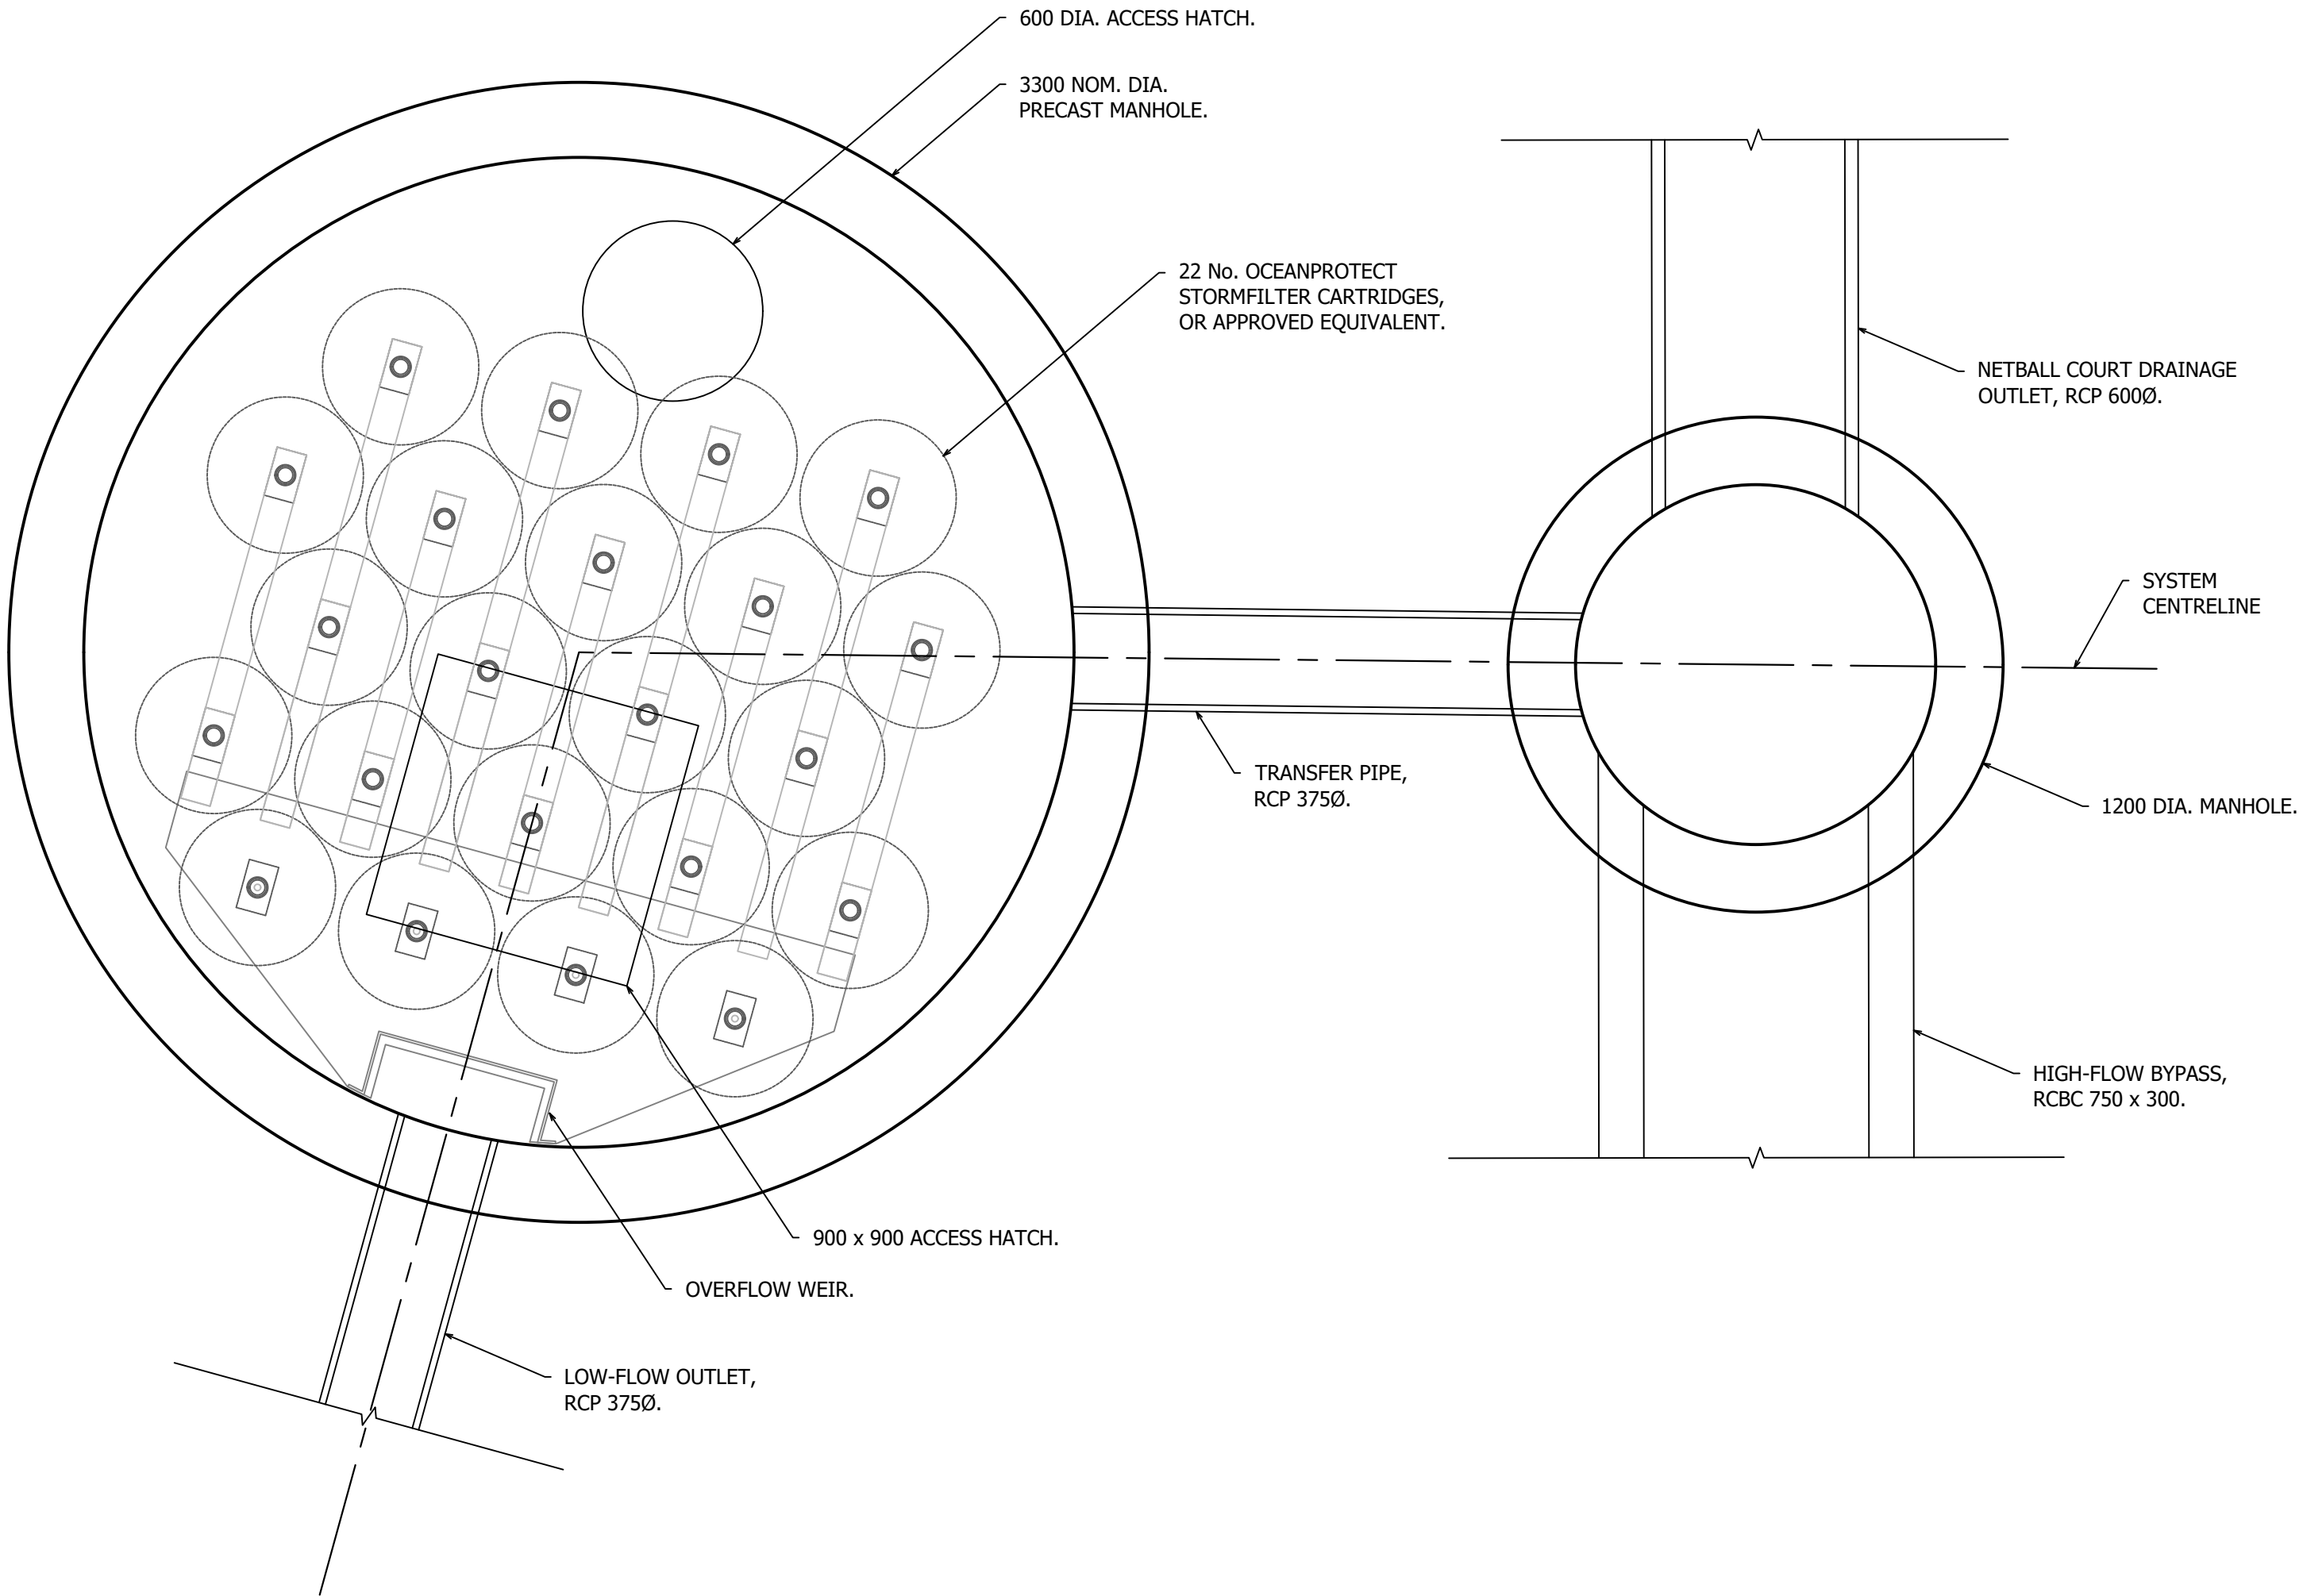

WSUD FILTRATION SYSTEM
PLAN DETAIL
SCALE 1:20

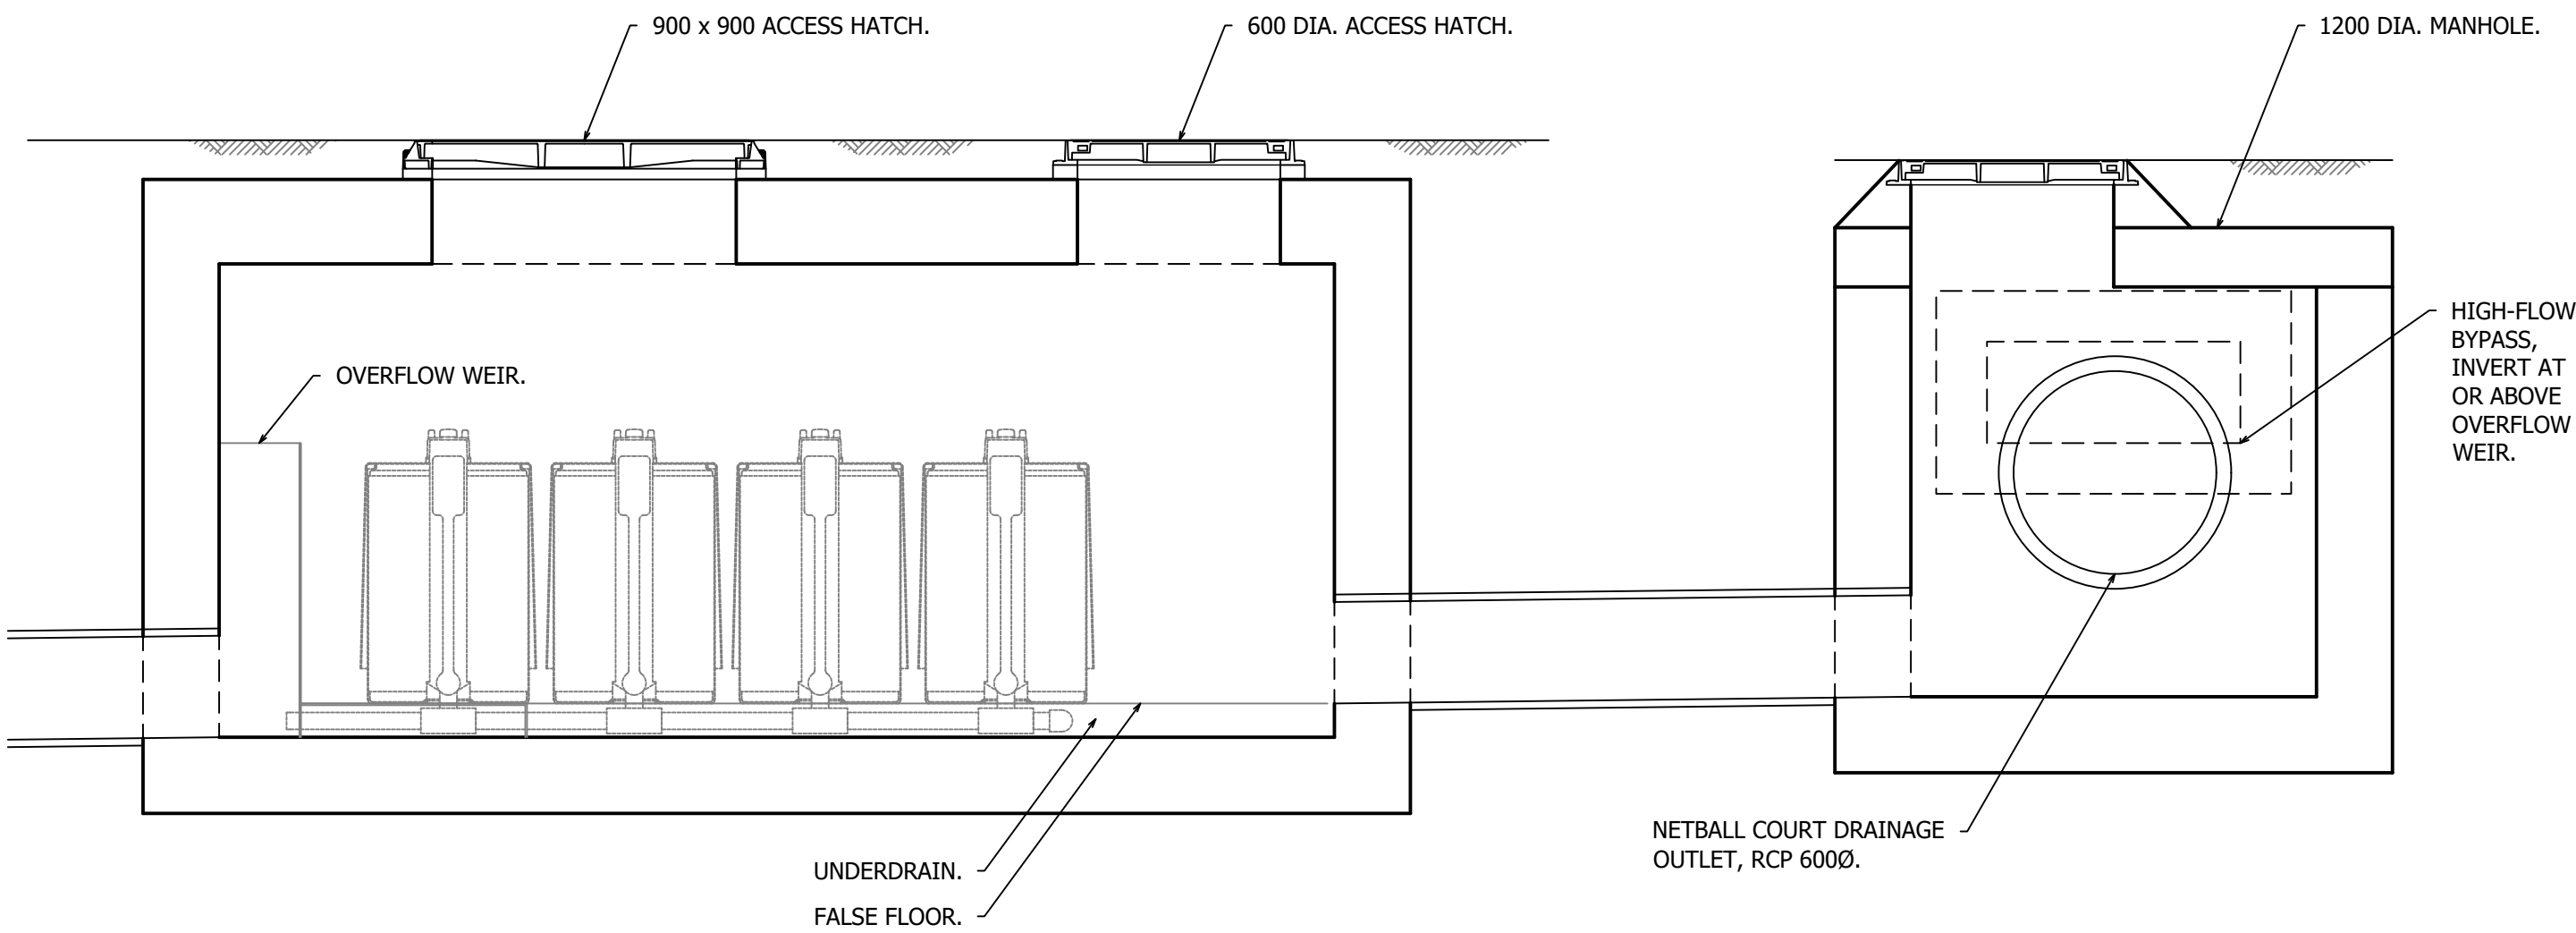

WSUD FILTRATION SYSTEM
SCHEMATIC SECTION
SCALE 1:20

NOT FOR CONSTRUCTION



T1	17/06/26	TPC	JZV	JDH	ISSUE FOR TENDER
Issue	Date	By	Chkd	Appd	Description

Job Title
ROCKHAMPTON
NETBALL CENTRE

Drawing Title
STORMWATER DRAINAGE
DETAILS
SHEET 5

Discipline	CIVIL AND FIELD OF PLAY
Drawing Status	ISSUE FOR TENDER
Drawing Number	SE_12306_F1324
Issue	T1