


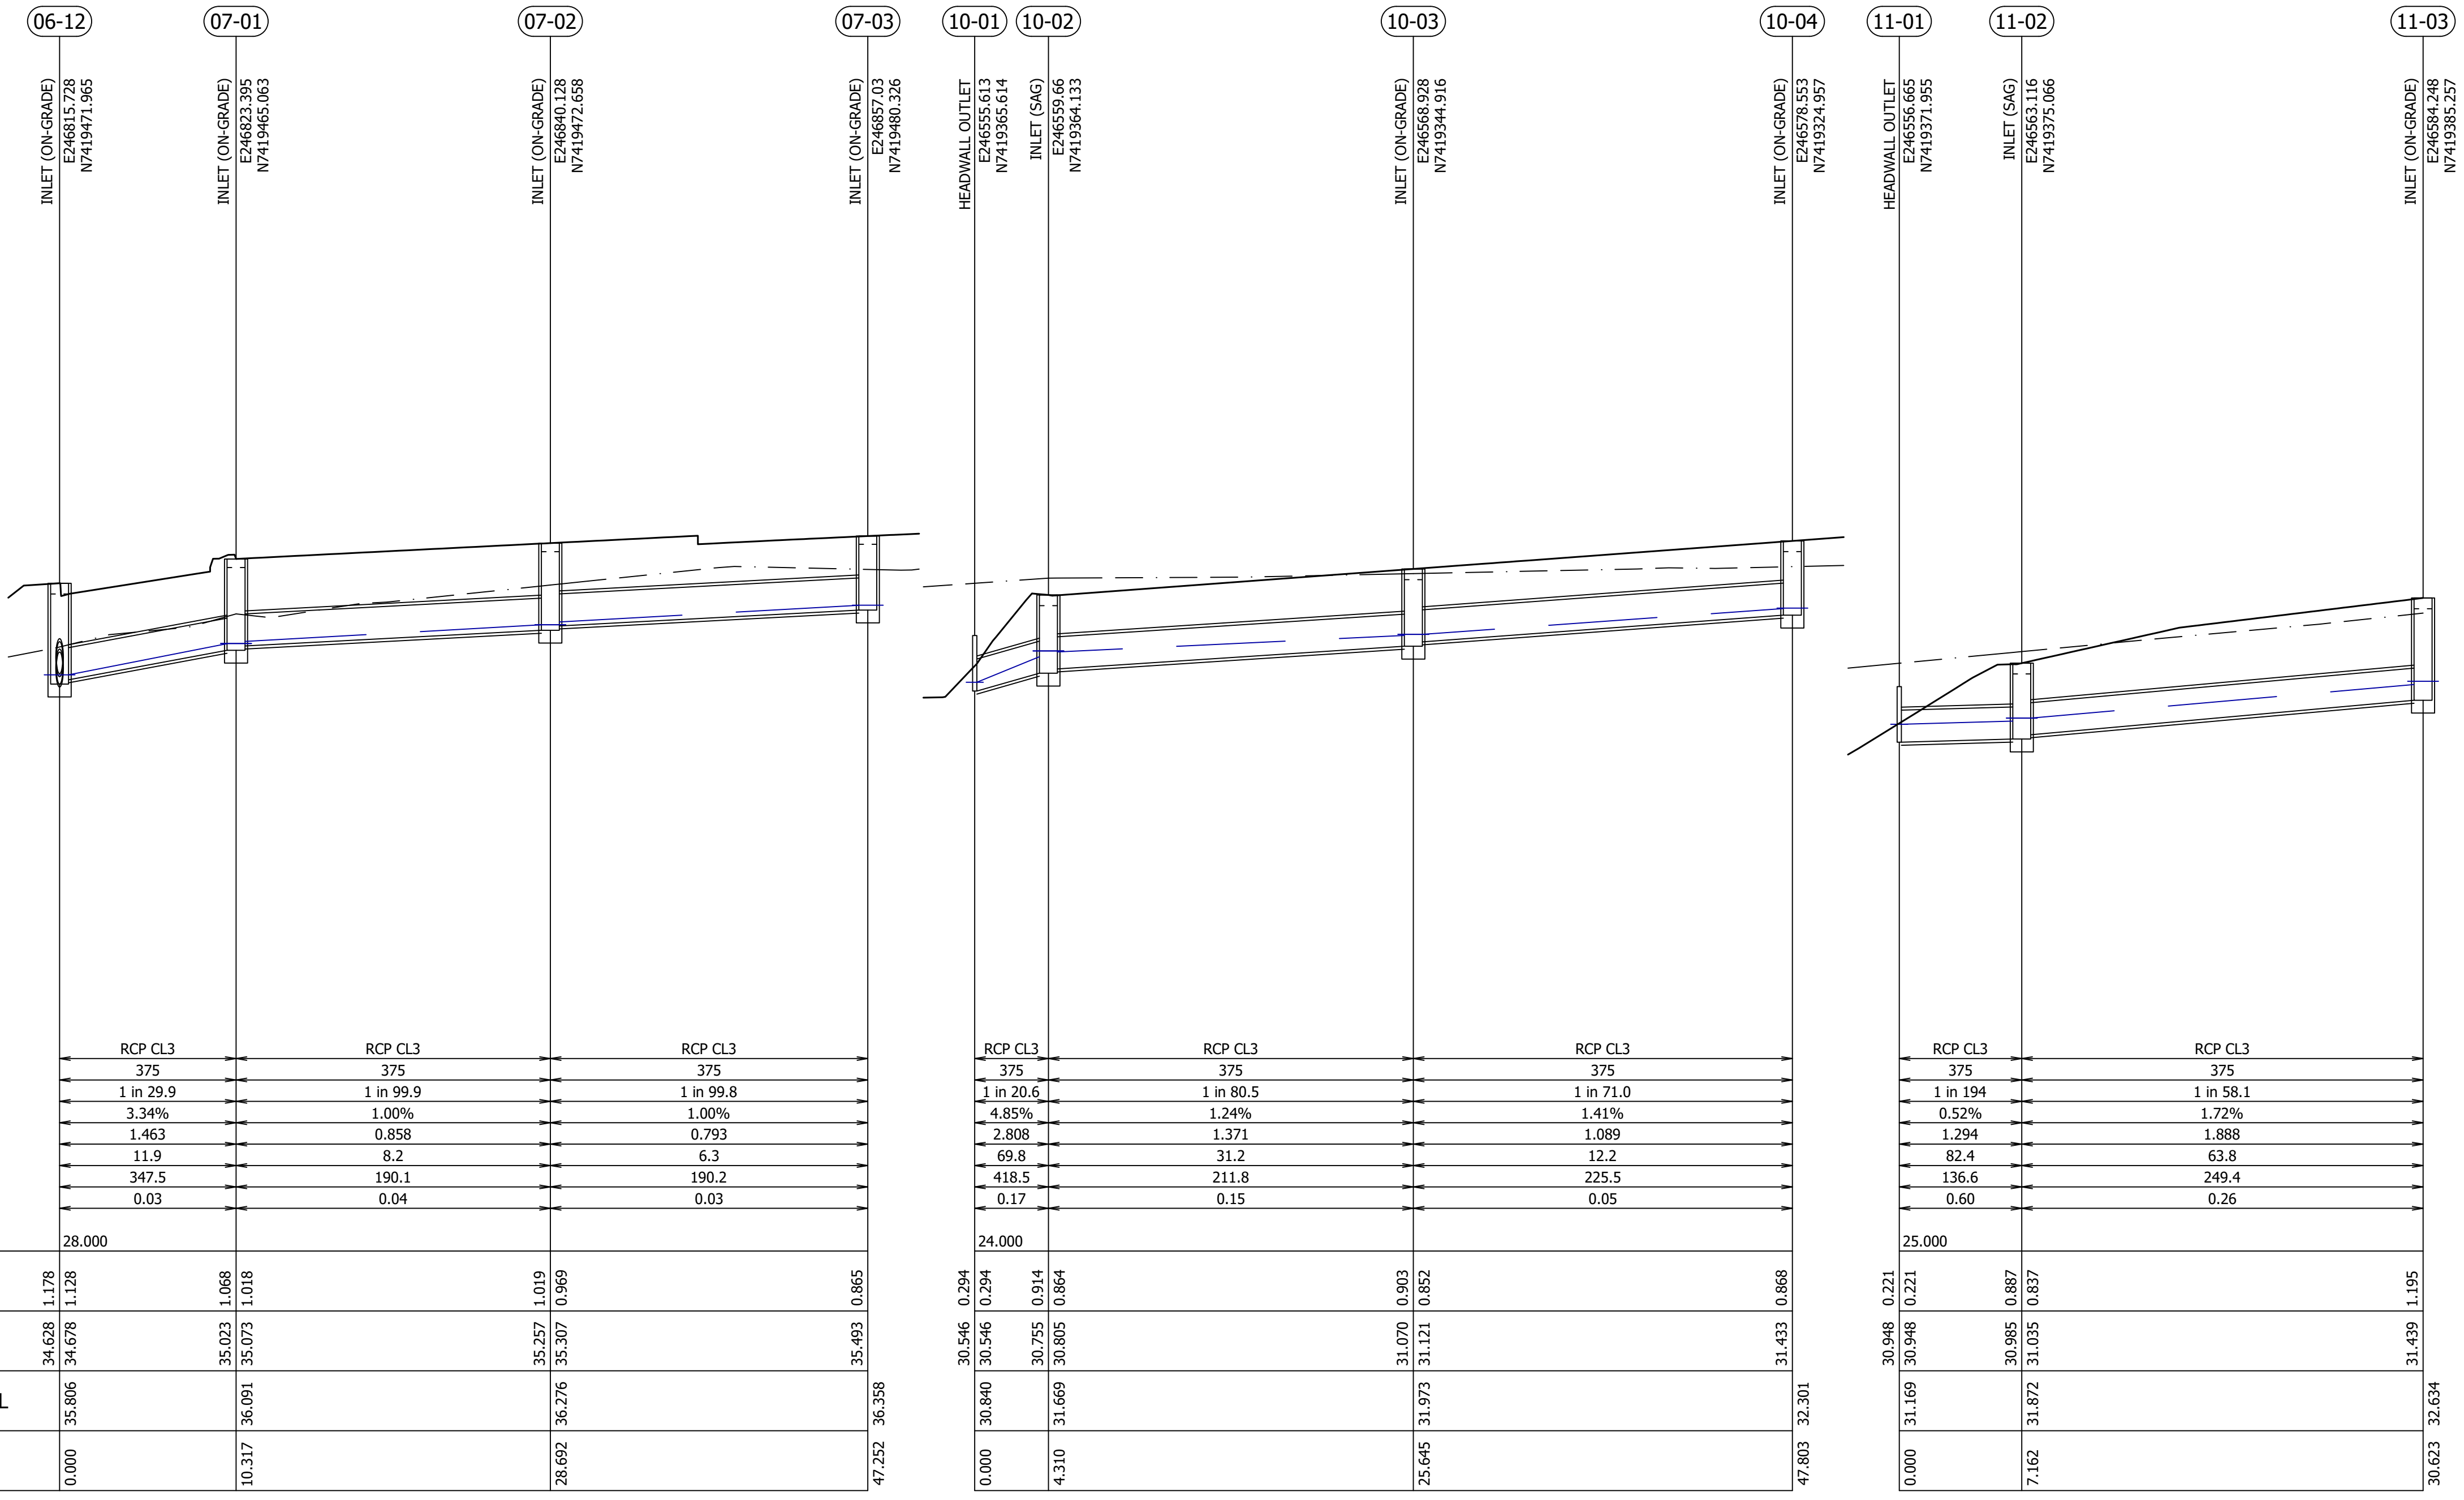

TYPE
SIZE (mm)
PIPE GRADE
GRADE (%)
VELOCITY (m/s)
DESIGN FLOW (L/s)
FLOW CAPACITY (L/s)
CAPACITY RATIO

DATUM RL	28.000		
DEPTH FSL TO INVERT	1.178 1.128	1.068 1.018	1.019 0.969
DESIGN INVERT LEVEL	34.628 34.678	35.023 35.073	35.257 35.307
FINISHED SURFACE LEVEL	35.806	36.091	36.276
LENGTH/CHAINAGE	0.000	10.317	28.692

HORIZONTAL SCALE 1:250
VERTICAL SCALE 1:50

07

DATUM RL	24.000		
DEPTH FSL TO INVERT	0.294 0.294	0.914 0.864	0.903 0.852
DESIGN INVERT LEVEL	30.546 30.546	30.755 30.805	31.070 31.121
FINISHED SURFACE LEVEL	30.840	31.669	31.973
LENGTH/CHAINAGE	0.000	4.310	25.645

10

DATUM RL	25.000	
DEPTH FSL TO INVERT	0.221 0.221	0.887 0.837
DESIGN INVERT LEVEL	30.948 30.948	30.985 31.035
FINISHED SURFACE LEVEL	31.169	31.872
LENGTH/CHAINAGE	0.000	7.162

11

NOT FOR CONSTRUCTION



T1	17/06/26	TPC	JZV	JDH	ISSUE FOR TENDER
Issue	Date	By	Chkd	Appd	Description

Job Title
ROCKHAMPTON
NETBALL CENTRE

Drawing Title
STORMWATER DRAINAGE
LONG SECTIONS
SHEET 4

Discipline	CIVIL AND FIELD OF PLAY
Drawing Status	ISSUE FOR TENDER
Drawing Number	SE_12306_F1353
Issue	T1