


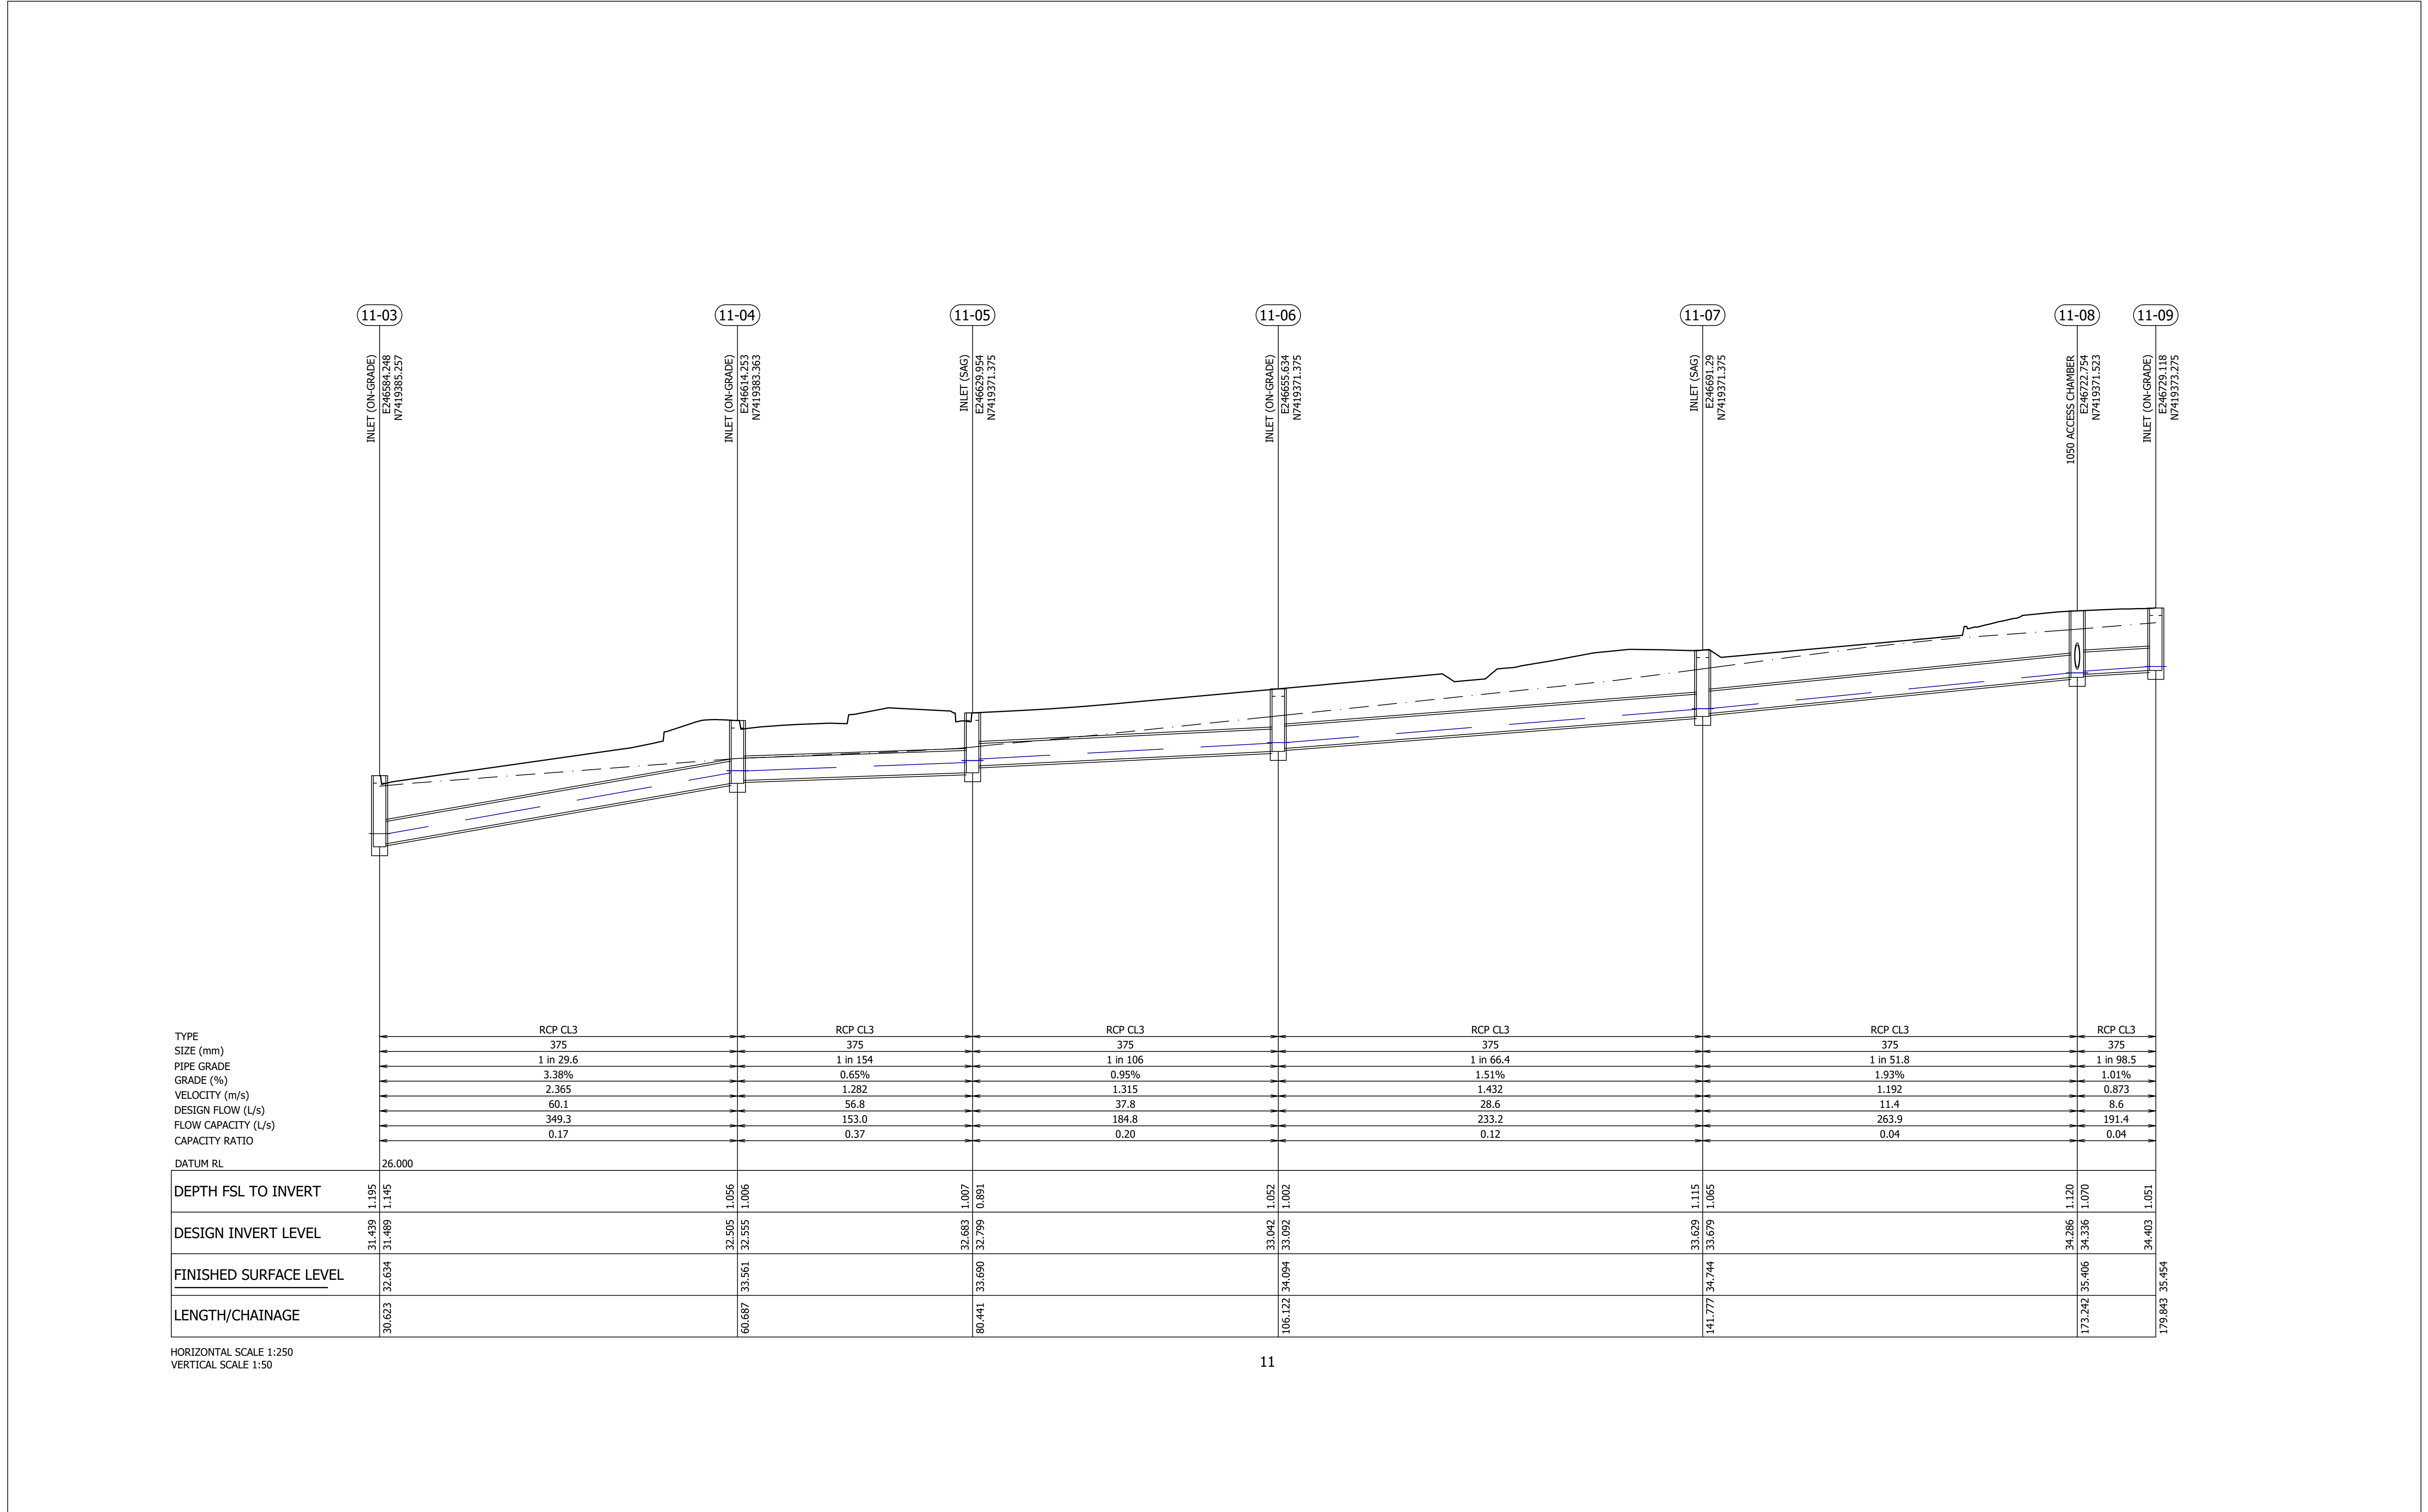

TYPE	RCP CL3		RCP CL3		RCP CL3		RCP CL3		RCP CL3	
SIZE (mm)	375		375		375		375		375	
PIPE GRADE	1 in 29.6		1 in 154		1 in 106		1 in 66.4		1 in 51.8	
GRADE (%)	3.38%		0.65%		0.95%		1.51%		1.93%	
VELOCITY (m/s)	2.365		1.282		1.315		1.432		1.192	
DESIGN FLOW (L/s)	60.1		56.8		37.8		28.6		11.4	
FLOW CAPACITY (L/s)	349.3		153.0		184.8		233.2		263.9	
CAPACITY RATIO	0.17		0.37		0.20		0.12		0.04	
DATUM RL	26.000									
DEPTH FSL TO INVERT	1.195	1.145	1.056	1.006	1.007	0.891	1.052	1.002	1.115	1.065
DESIGN INVERT LEVEL	31.439	31.409	32.505	32.555	32.683	32.799	33.042	33.092	33.629	33.679
FINISHED SURFACE LEVEL	32.634		33.561		33.690		34.094		34.744	
LENGTH/CHAINAGE	30.623		60.687		80.441		106.122	34.094	141.777	34.744
			</							

HORIZONTAL SCALE 1:250
VERTICAL SCALE 1:50

NOT FOR CONSTRUCTION



T1	17/06/26	TPC	JZV	JDH	ISSUE FOR TENDER
Issue	Date	By	Chkd	Appd	Description

Job Title
ROCKHAMPTON
NETBALL CENTRE

Drawing Title
STORMWATER DRAINAGE
LONG SECTIONS
SHEET 5

Discipline CIVIL AND FIELD OF PLAY
Drawing Status ISSUE FOR TENDER
Drawing Number SE_12306_F1354
Issue T1