

TYPE
SIZE (mm)
PIPE GRADE
GRADE (%)
VELOCITY (m/s)
DESIGN FLOW (L/s)
FLOW CAPACITY (L/s)
CAPACITY RATIO

DATUM RL	28.000
DEPTH FSL TO INVERT	34.403 1.051 34.453 1.001
DESIGN INVERT LEVEL	34.864 1.021
FINISHED SURFACE LEVEL	179.843 35.454 34.453 1.001
LENGTH/CHAINAGE	179.843 35.454 34.453 1.001

HORIZONTAL SCALE 1:250
VERTICAL SCALE 1:50

11


12

19

20

25

26

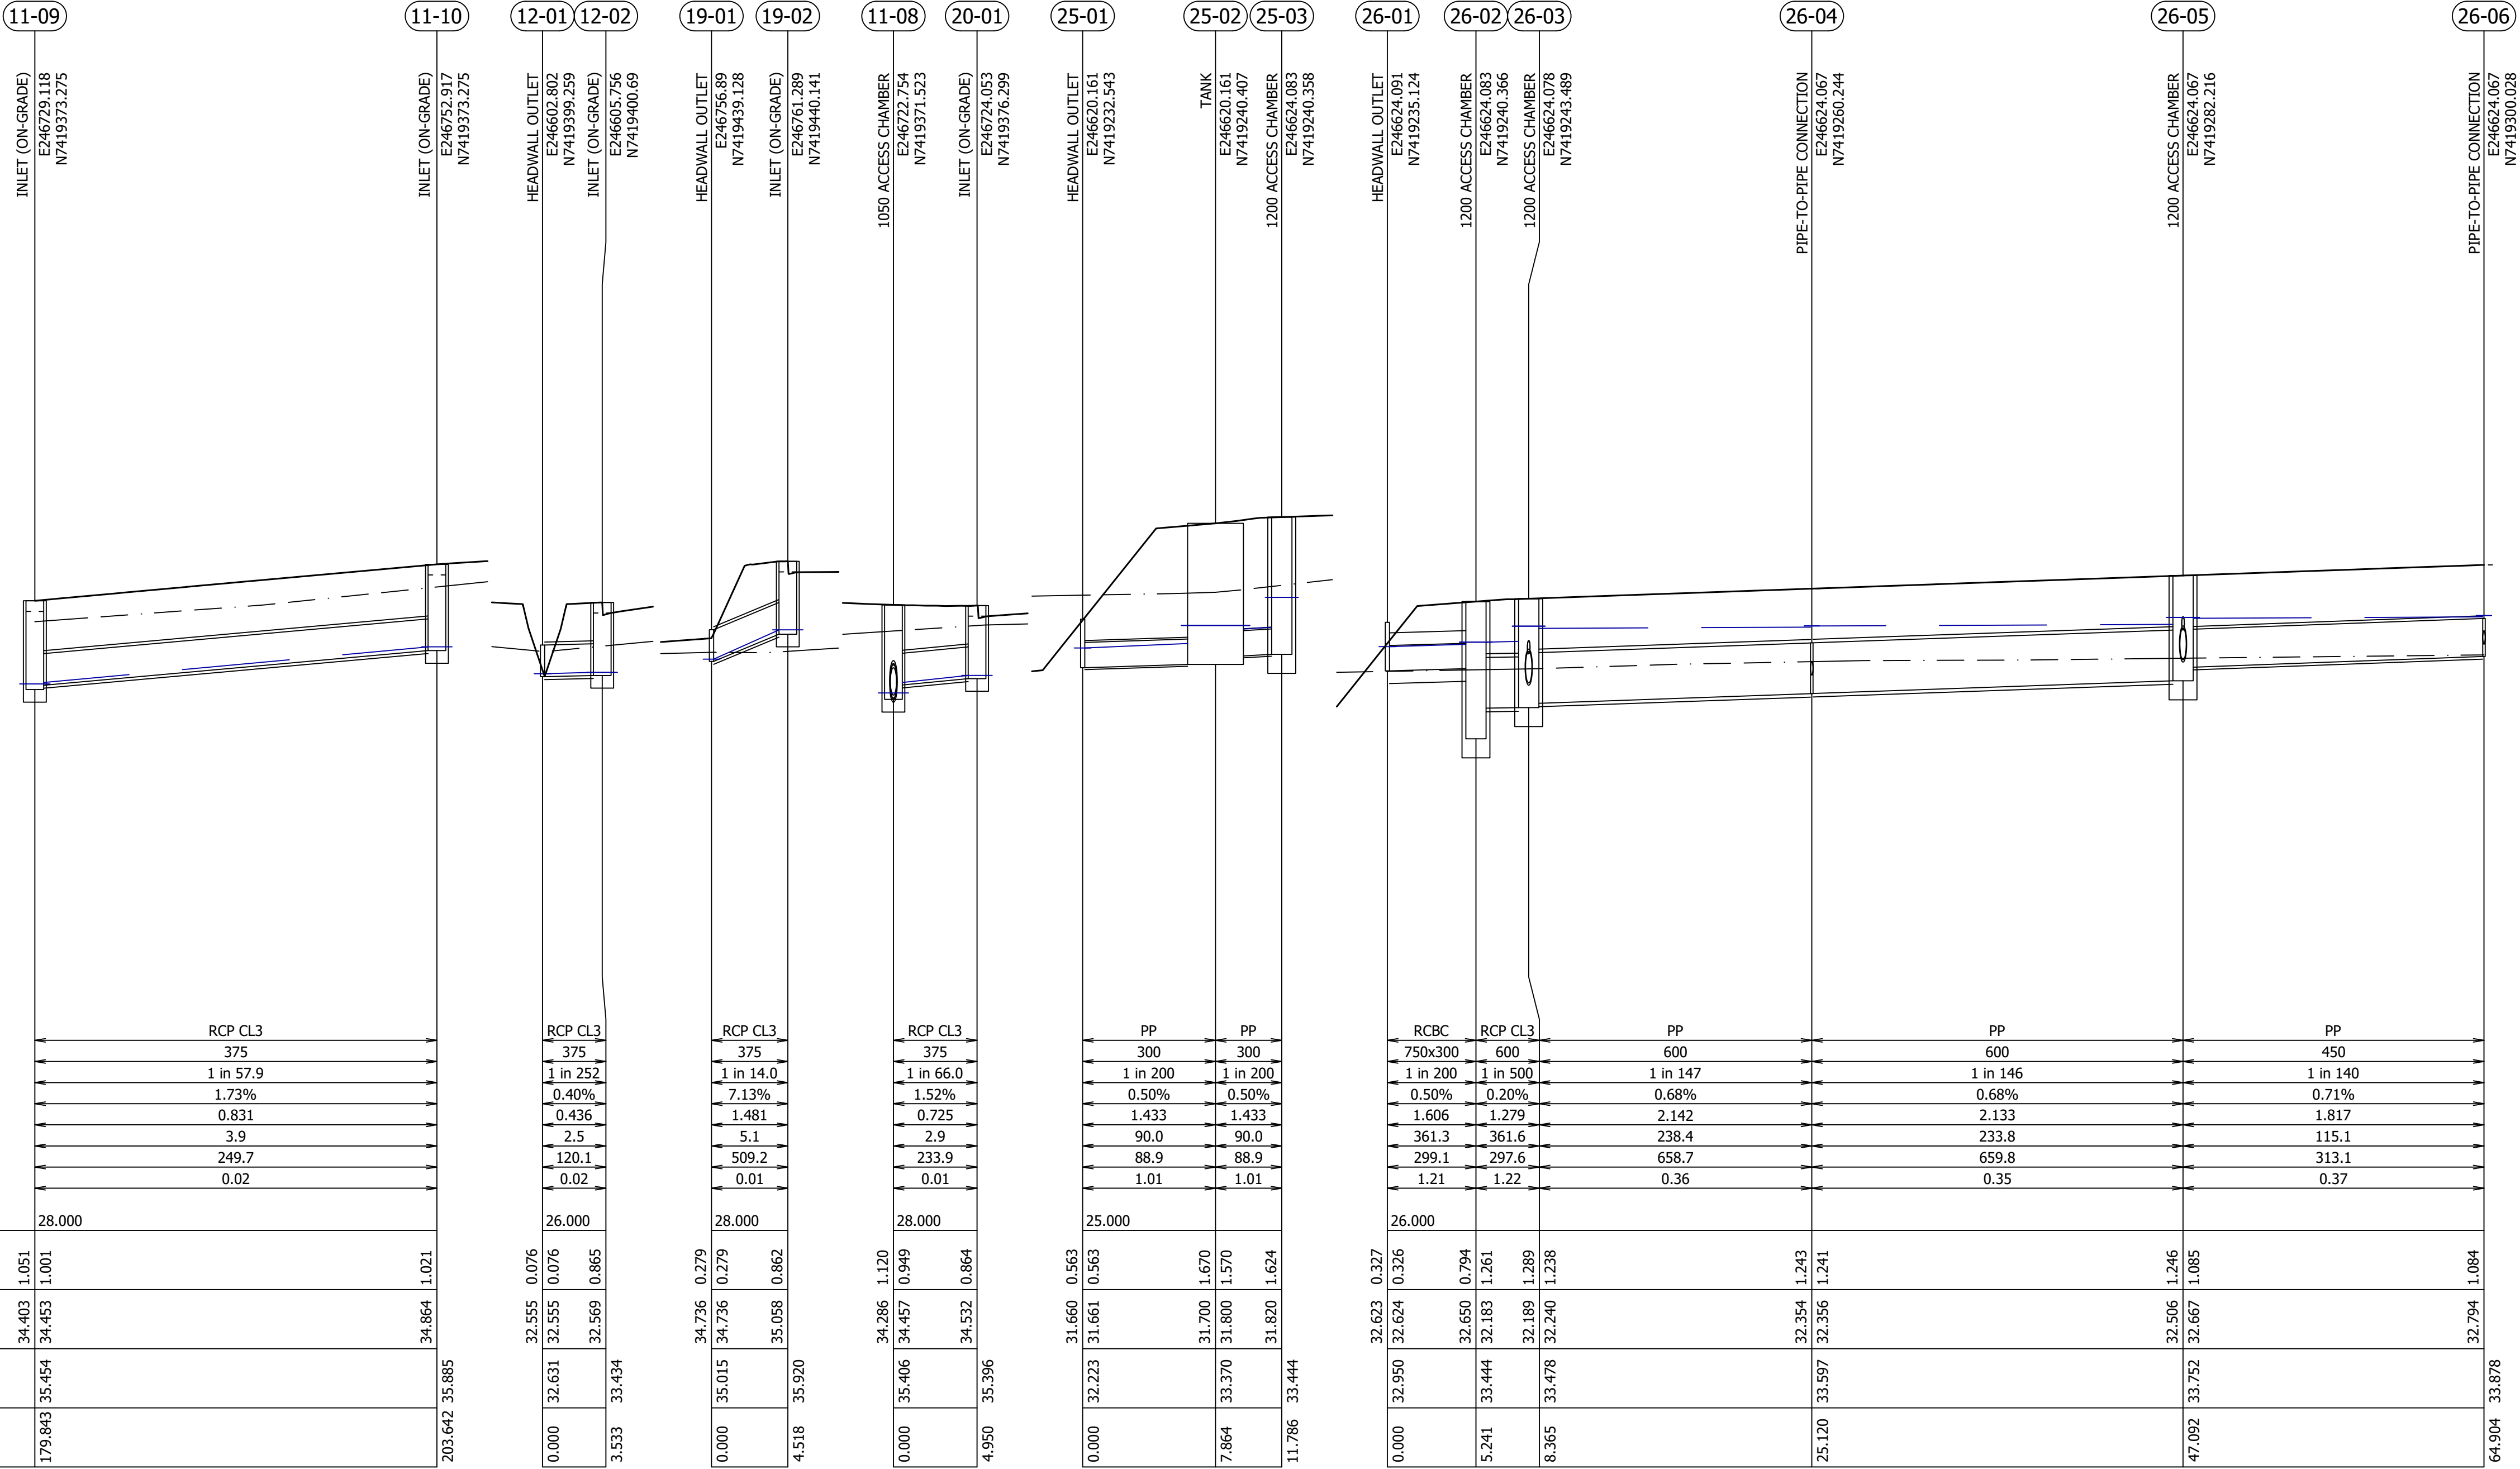

NOT FOR CONSTRUCTION



SPORTENG™

T1 17/06/26 TPC JZV JDH ISSUE FOR TENDER
Issue Date By Chkd Appd Description

Job Title
ROCKHAMPTON
NETBALL CENTRE

Drawing Title
STORMWATER DRAINAGE
LONG SECTIONS
SHEET 6

Discipline
CIVIL AND FIELD OF PLAY
Drawing Status
ISSUE FOR TENDER
Drawing Number
SE_12306_F1355
Issue
T1