


NOTES:
1. FOR LEGEND AND NOTES, REFER TO DRAWING SE_12306_F1300.

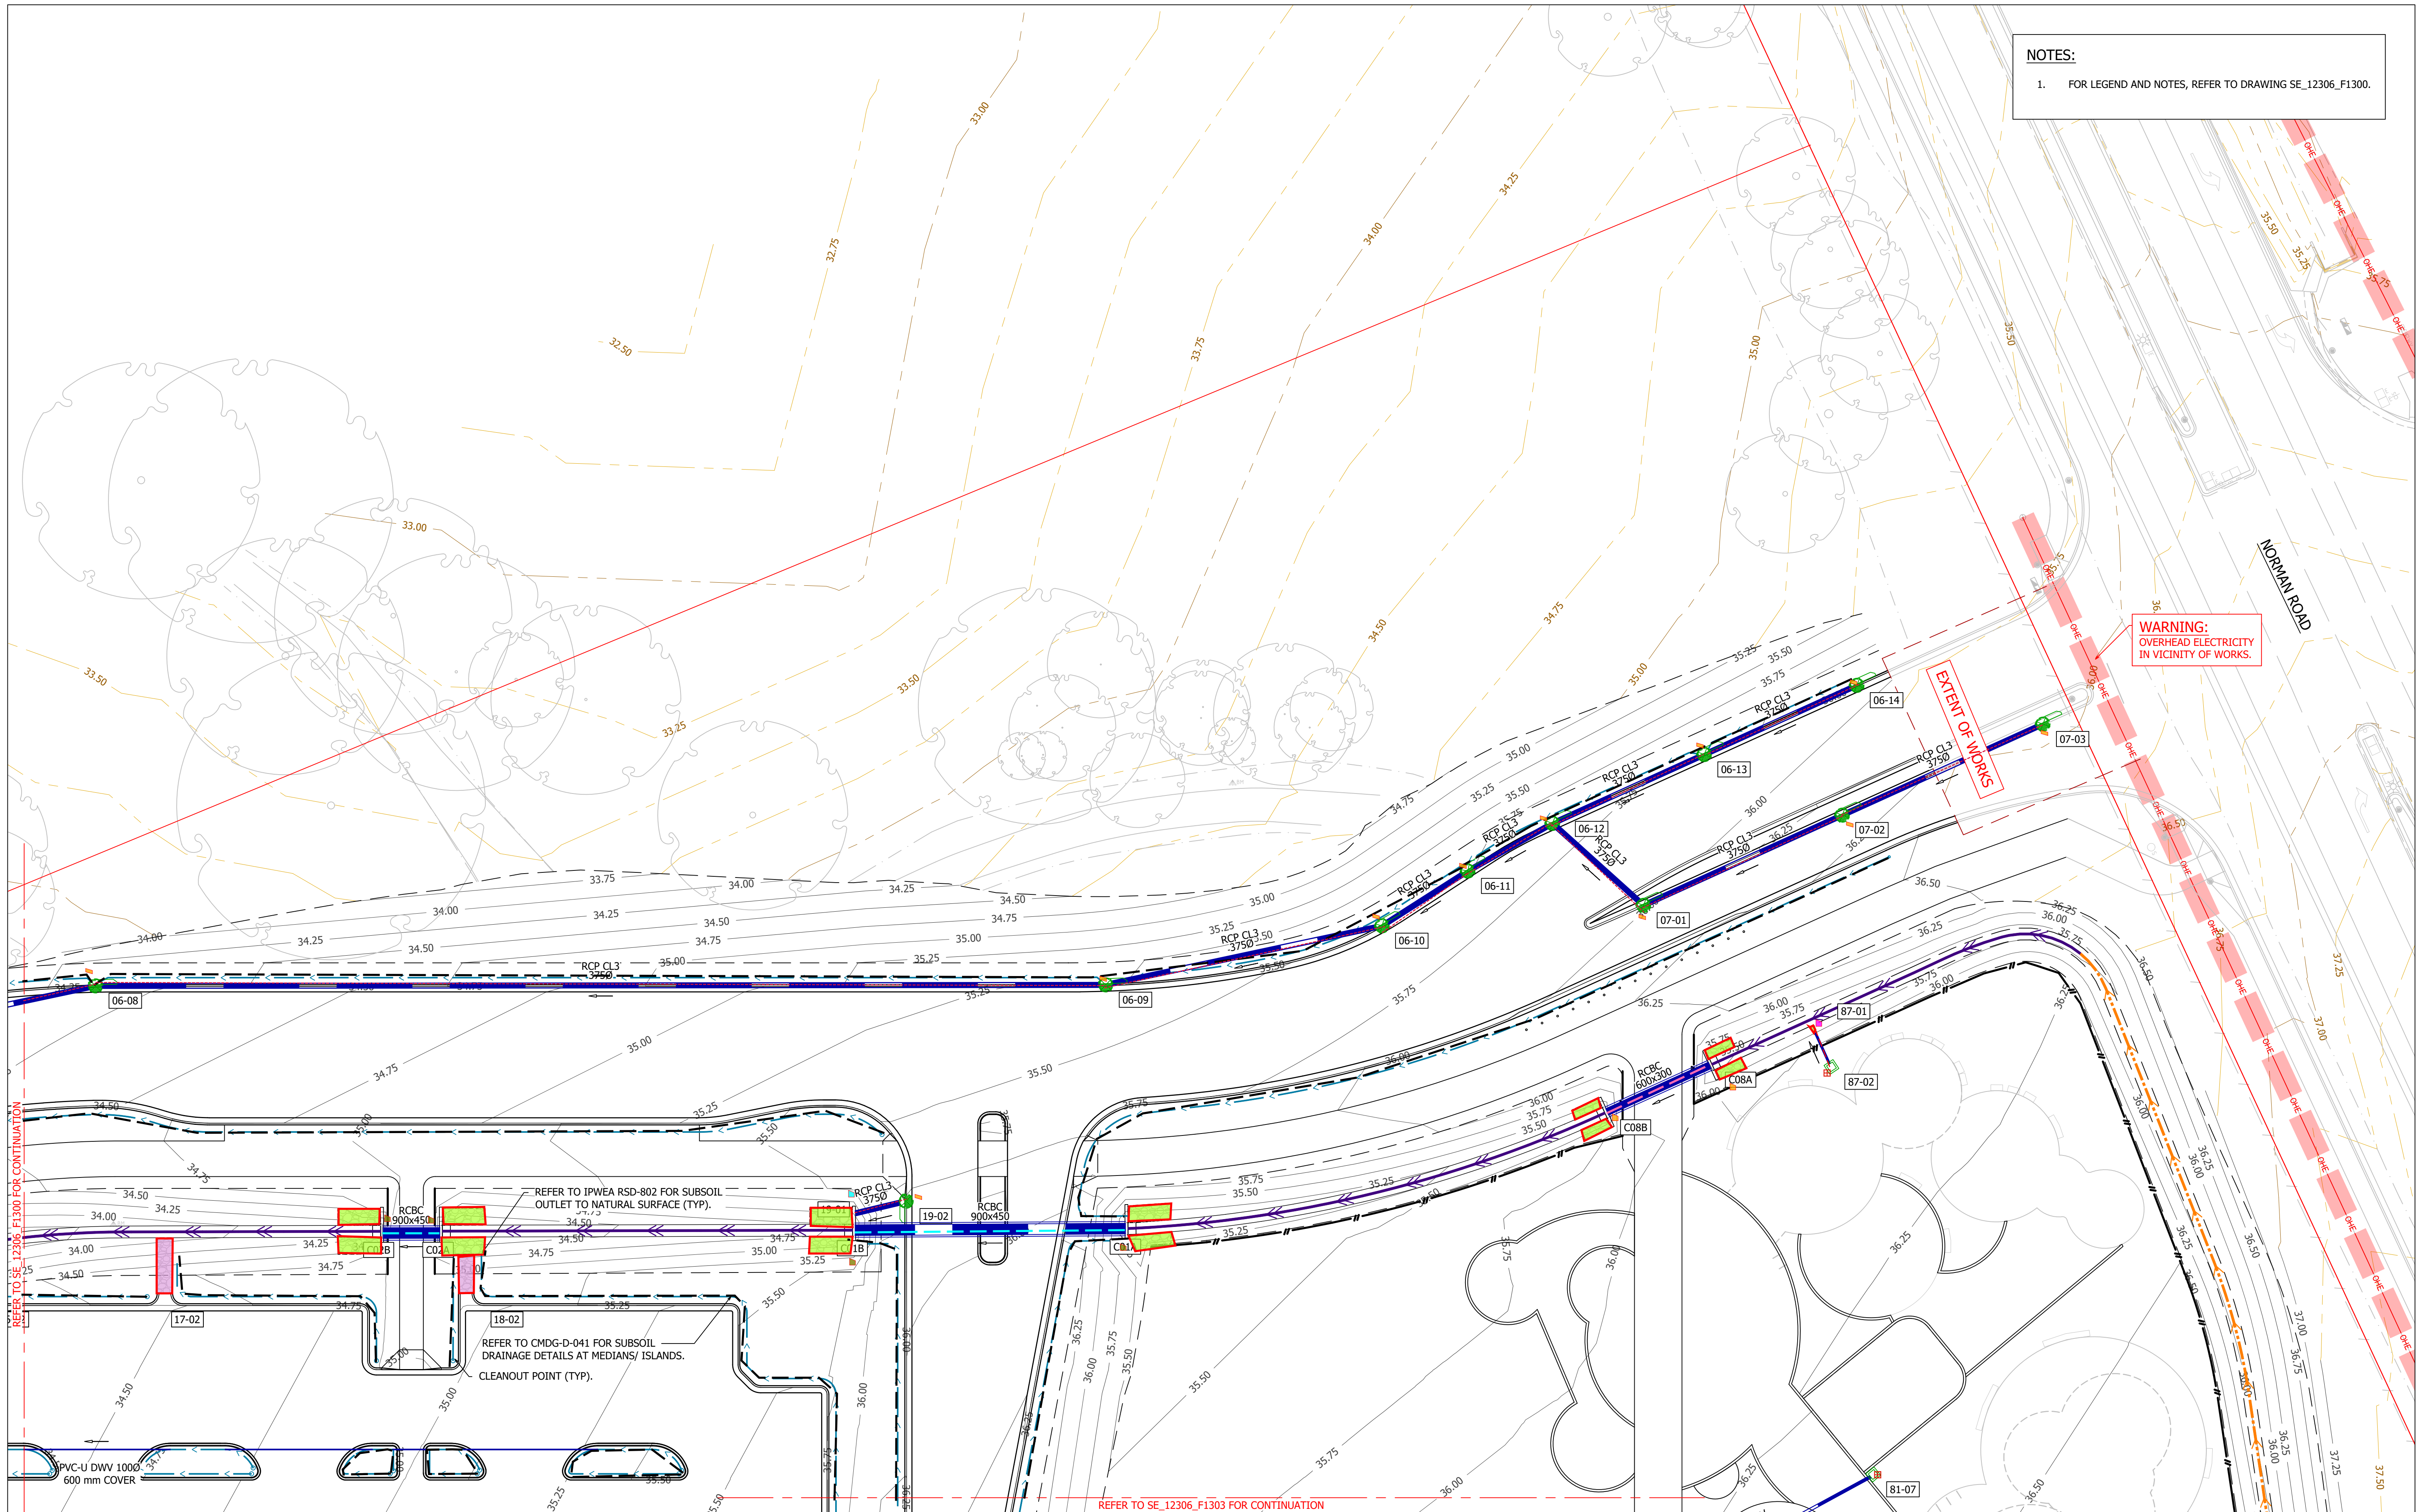

WARNING
BEWARE OF UNDERGROUND SERVICES
THE LOCATION OF UNDERGROUND SERVICES ARE APPROXIMATE ONLY. IT IS THE RESPONSIBILITY OF THE CONTRACTOR TO PROVE THEIR EXACT POSITION ON SITE. NO GUARANTEE IS GIVEN THAT ALL EXISTING SERVICES ARE SHOWN.

WARNING
OVERHEAD ELECTRICITY IN VICINITY OF WORKS
NOT FOR CONSTRUCTION



T1	17/06/26	TPC	JZV	JDH	ISSUE FOR TENDER
Issue	Date	By	Chkd	Appd	Description

Job Title
**ROCKHAMPTON
NETBALL CENTRE**

Drawing Title
**STORMWATER DRAINAGE
LAYOUT PLAN
SHEET 2**

01m	5m	10m	15m	20m
SCALE 1:250 @ A1				
Discipline				
CIVIL AND FIELD OF PLAY				
Drawing Status				
ISSUE FOR TENDER				
Drawing Number				
SE_12306_F1301				
Issue				
T1				