


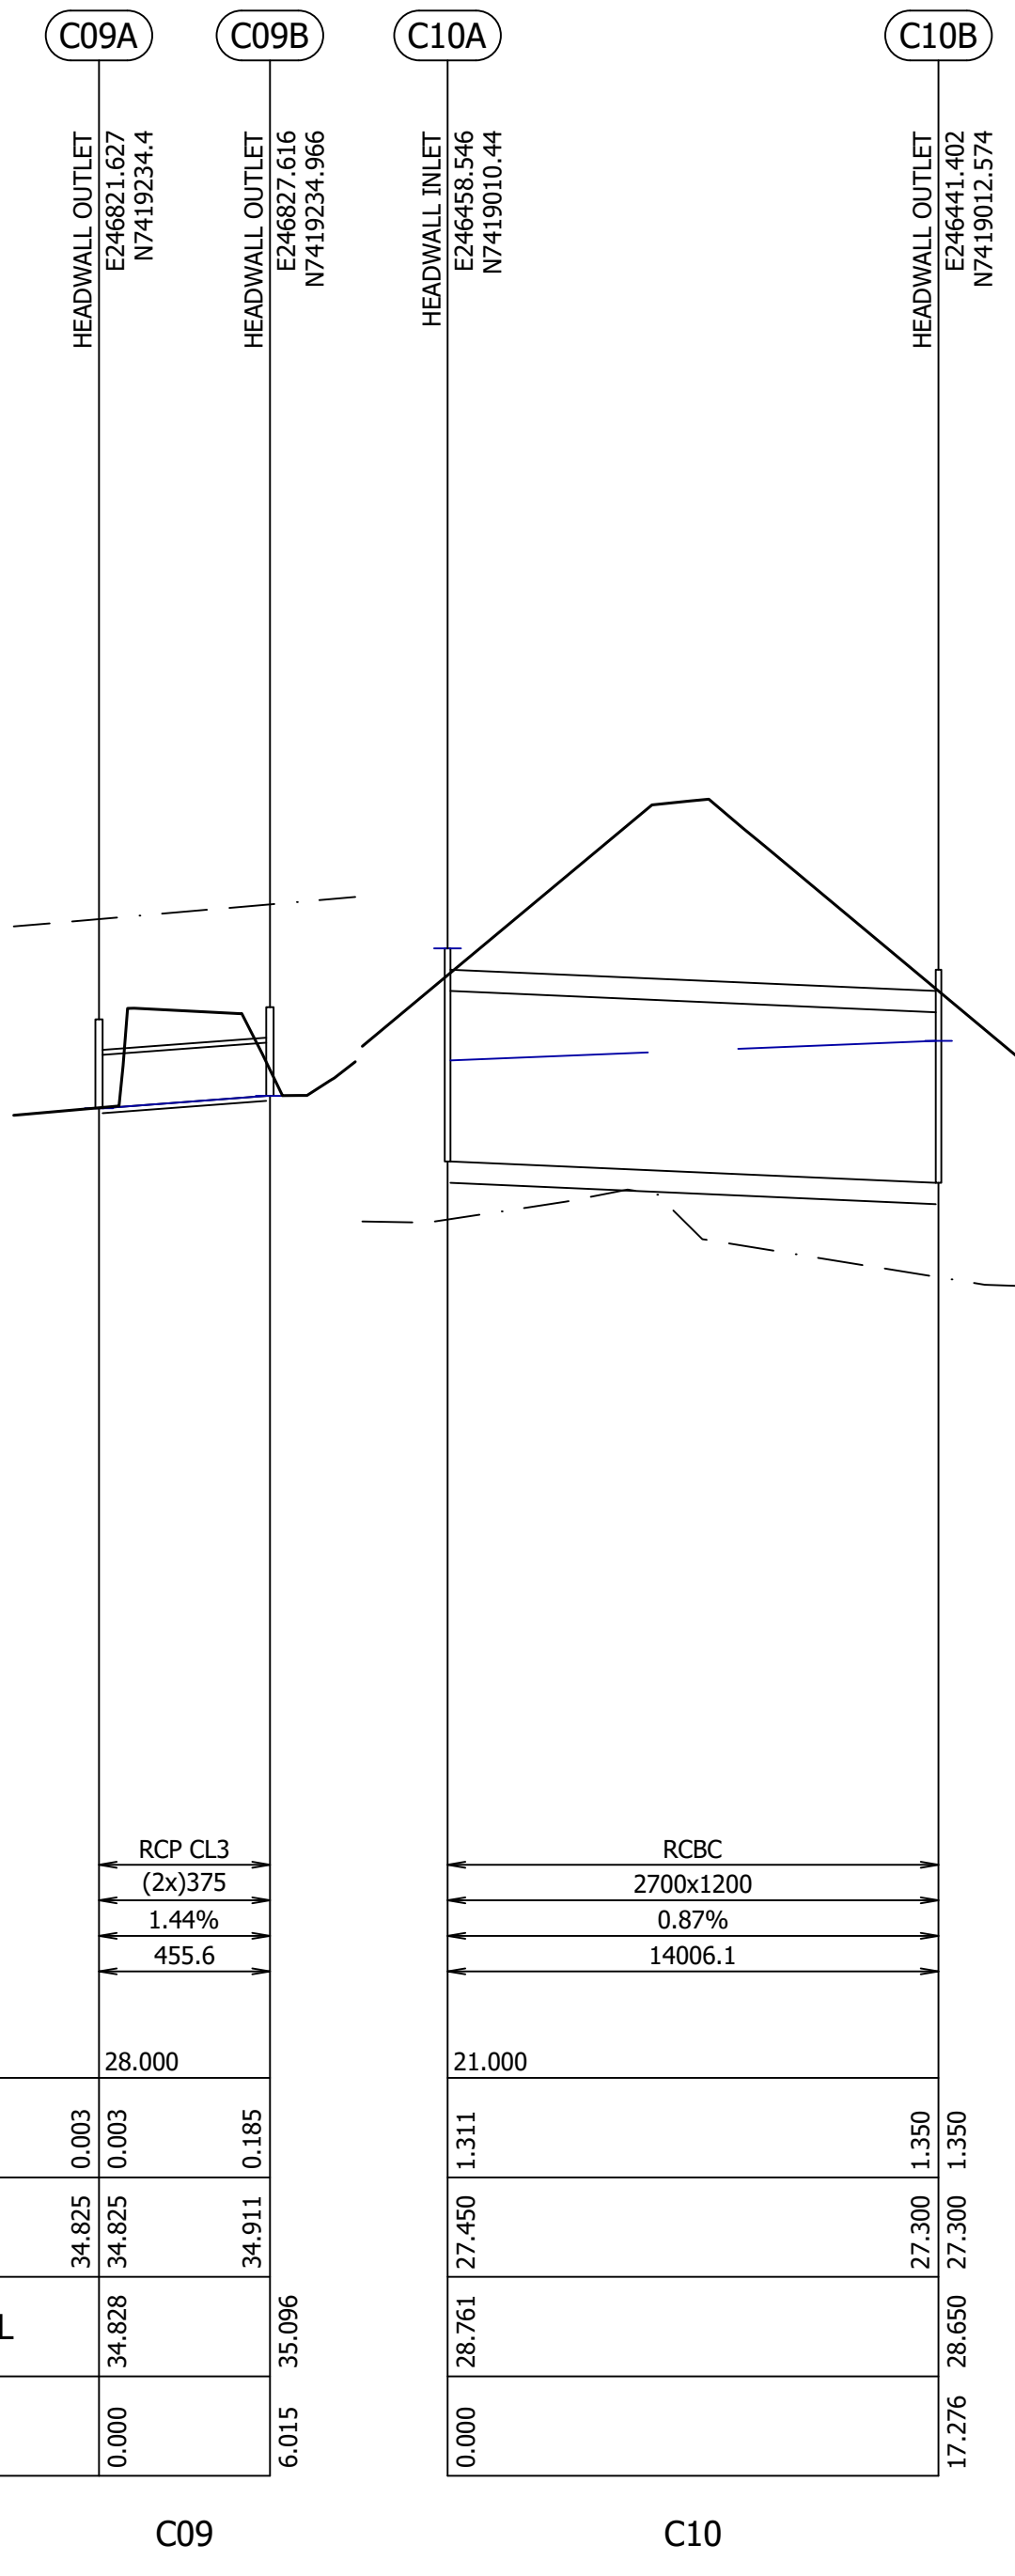

TYPE
SIZE (mm)
GRADE (%)
FLOW CAPACITY (L/s)

DATUM RL	28.000	
DEPTH FSL TO INVERT	0.003	0.003
DESIGN INVERT LEVEL	34.825	34.825
FINISHED SURFACE LEVEL	34.828	34.911
LENGTH/CHAINAGE	0.000	6.015

C09

RCBC	2700x1200	
GRADE (%)	0.87%	0.87%
FLOW CAPACITY (L/s)	14006.1	14006.1
DATUM RL	21.000	
DEPTH FSL TO INVERT	1.311	1.350
DESIGN INVERT LEVEL	27.450	27.300
FINISHED SURFACE LEVEL	28.761	28.650
LENGTH/CHAINAGE	0.000	17.276

C10

NOT FOR CONSTRUCTION



SPORTENG™

T1	17/06/26	TPC	JZV	JDH	ISSUE FOR TENDER
Issue	Date	By	Chkd	Appd	Description

Job Title
ROCKHAMPTON
NETBALL CENTRE

Drawing Title
STORMWATER DRAINAGE
LONG SECTIONS
SHEET 15

Discipline
CIVIL AND FIELD OF PLAY
Drawing Status
ISSUE FOR TENDER
Drawing Number
SE_12306_F1363

Issue
T1