


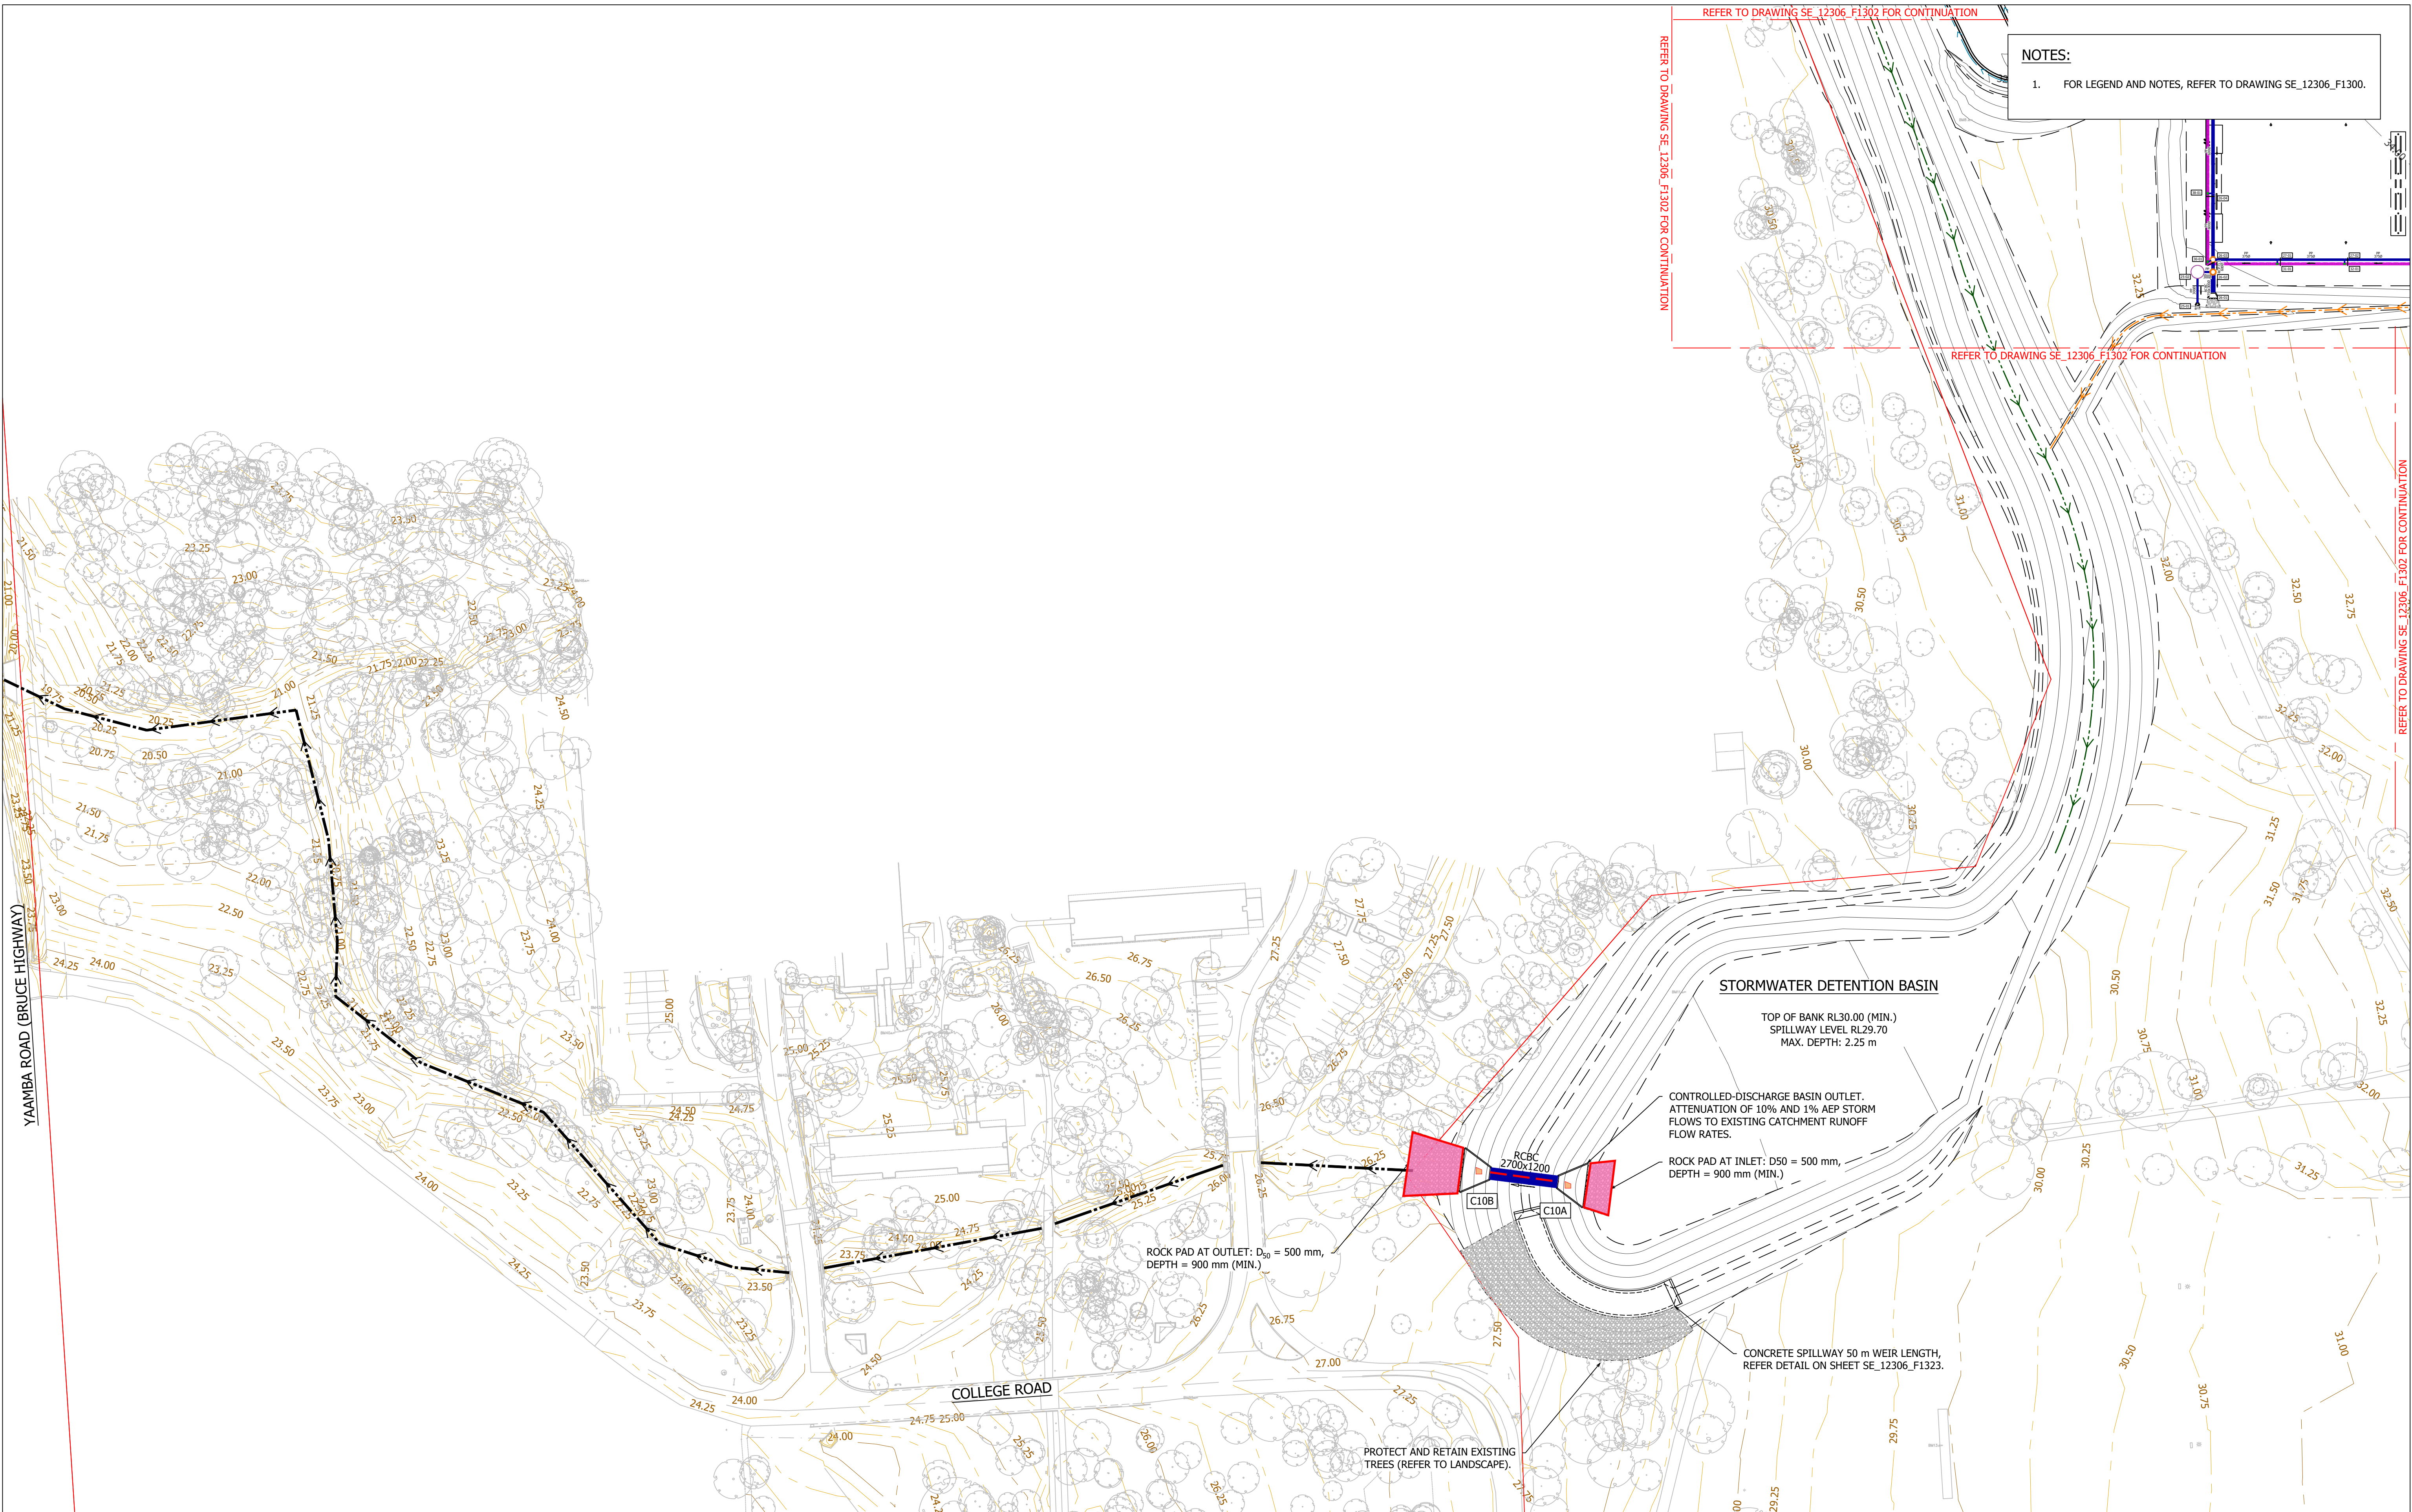

NOTES:  
1. FOR LEGEND AND NOTES, REFER TO DRAWING SE\_12306\_F1300.

**WARNING**  
**BEWARE OF UNDERGROUND SERVICES**  
THE LOCATION OF UNDERGROUND SERVICES ARE APPROXIMATE ONLY. IT IS THE RESPONSIBILITY OF THE CONTRACTOR TO PROVE THEIR EXACT POSITION ON SITE. NO GUARANTEE IS GIVEN THAT ALL EXISTING SERVICES ARE SHOWN.

**WARNING**  
**OVERHEAD ELECTRICITY IN VICINITY OF WORKS**  
**NOT FOR CONSTRUCTION**



**SPORTENG™**

|       |          |     |      |      |                  |
|-------|----------|-----|------|------|------------------|
| T1    | 17/06/26 | TPC | JZV  | JDH  | ISSUE FOR TENDER |
| Issue | Date     | By  | Chkd | Appd | Description      |

Job Title  
**ROCKHAMPTON  
NETBALL CENTRE**  
  
Drawing Title  
**STORMWATER DRAINAGE  
LAYOUT PLAN  
SHEET 6**

0 10m 50m  
SCALE 1:750 @ A1  
Discipline  
**CIVIL AND FIELD OF PLAY**  
Drawing Status  
**ISSUE FOR TENDER**  
Drawing Number  
**SE\_12306\_F1305**  
Issue  
**T1**