




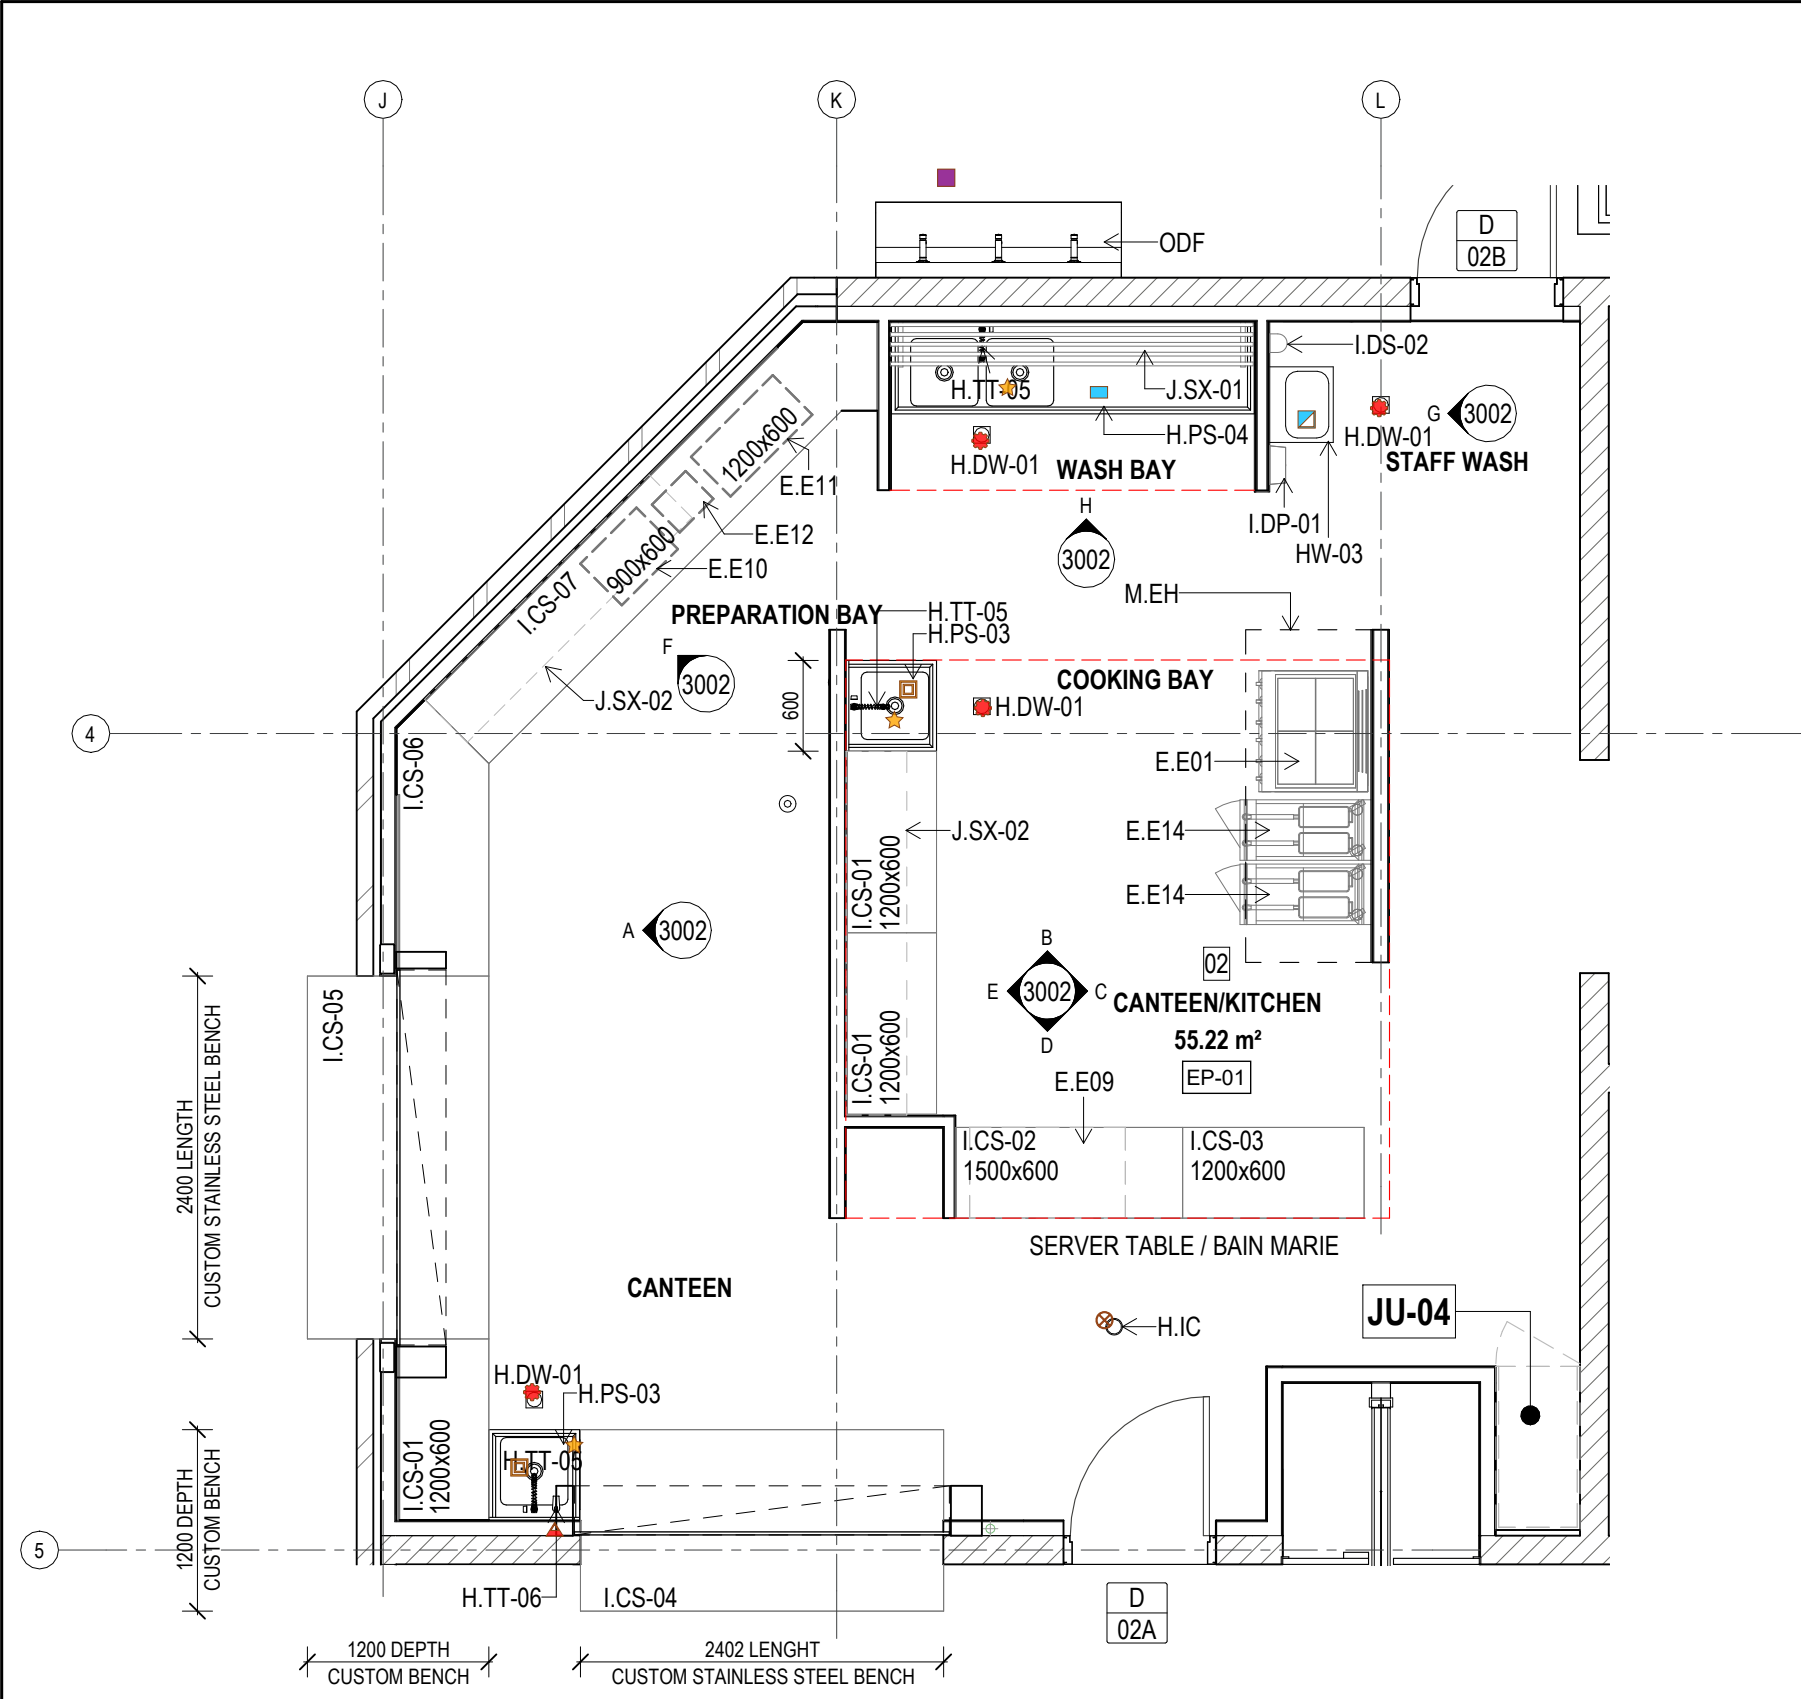


1 PLAN CANTEEN / KITCHEN
Scale: 1: 50

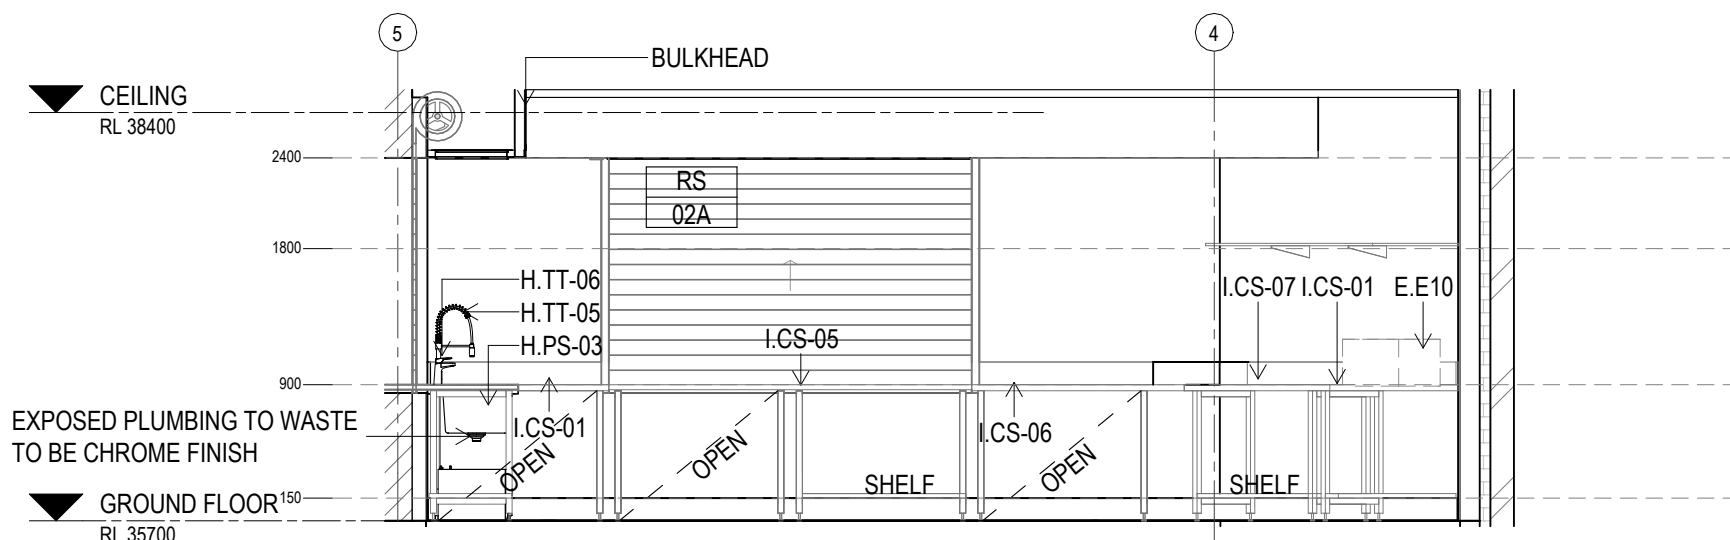


A ELEVATION CANTEEN/KITCHEN
Scale: 1: 50

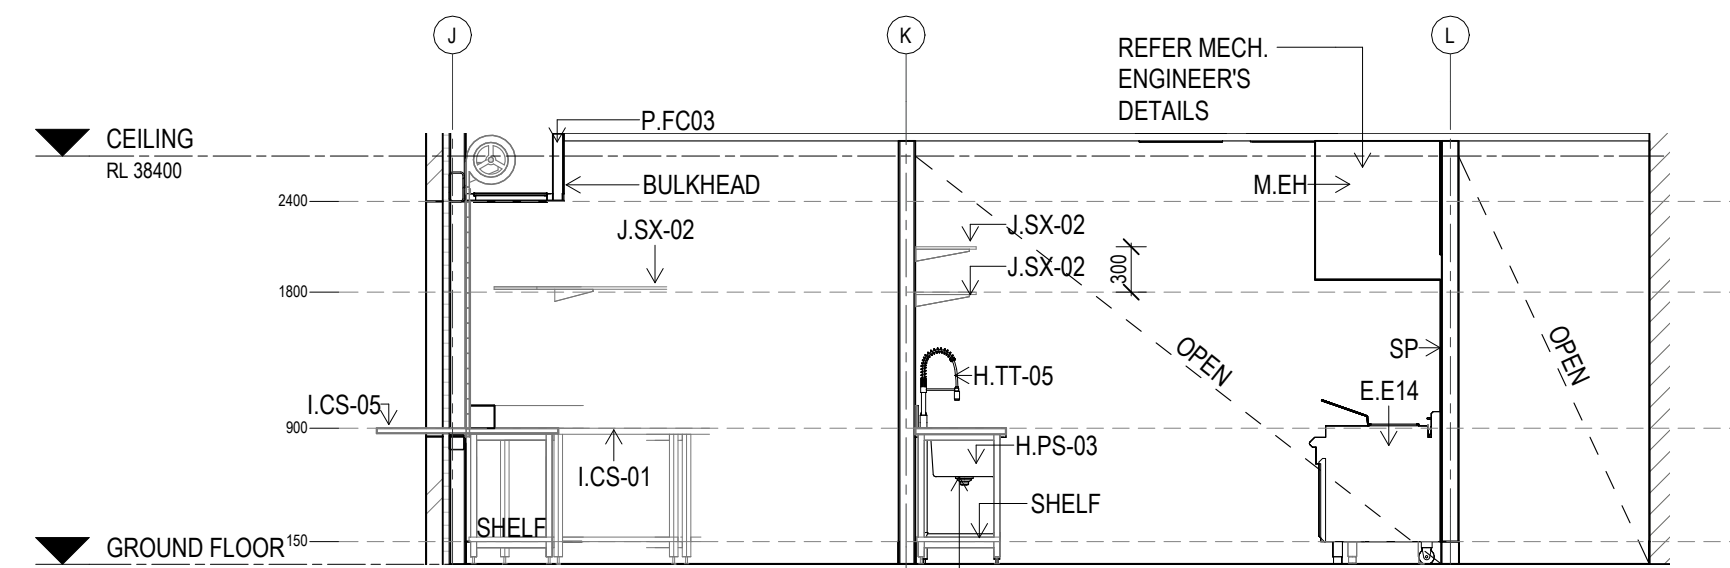


B ELEVATION CANTEEN/KITCHEN
Scale: 1: 50

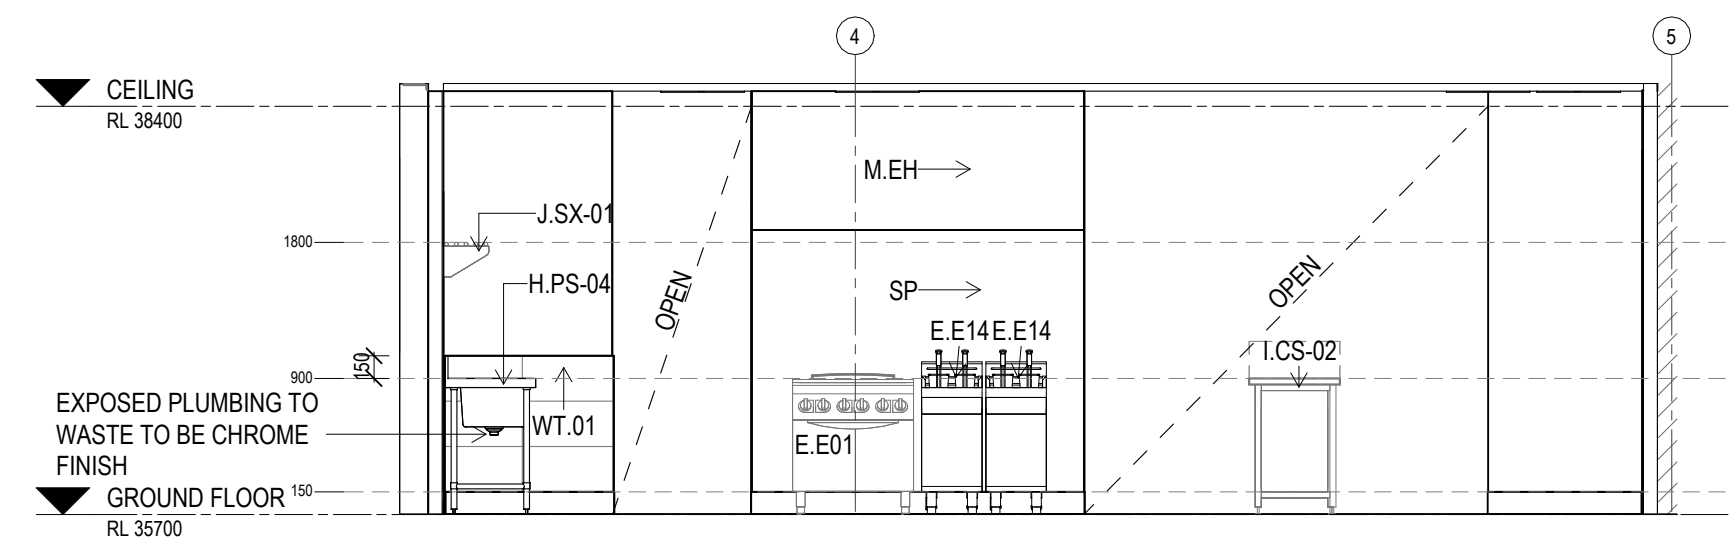


C ELEVATION CANTEEN/KITCHEN
Scale: 1: 50

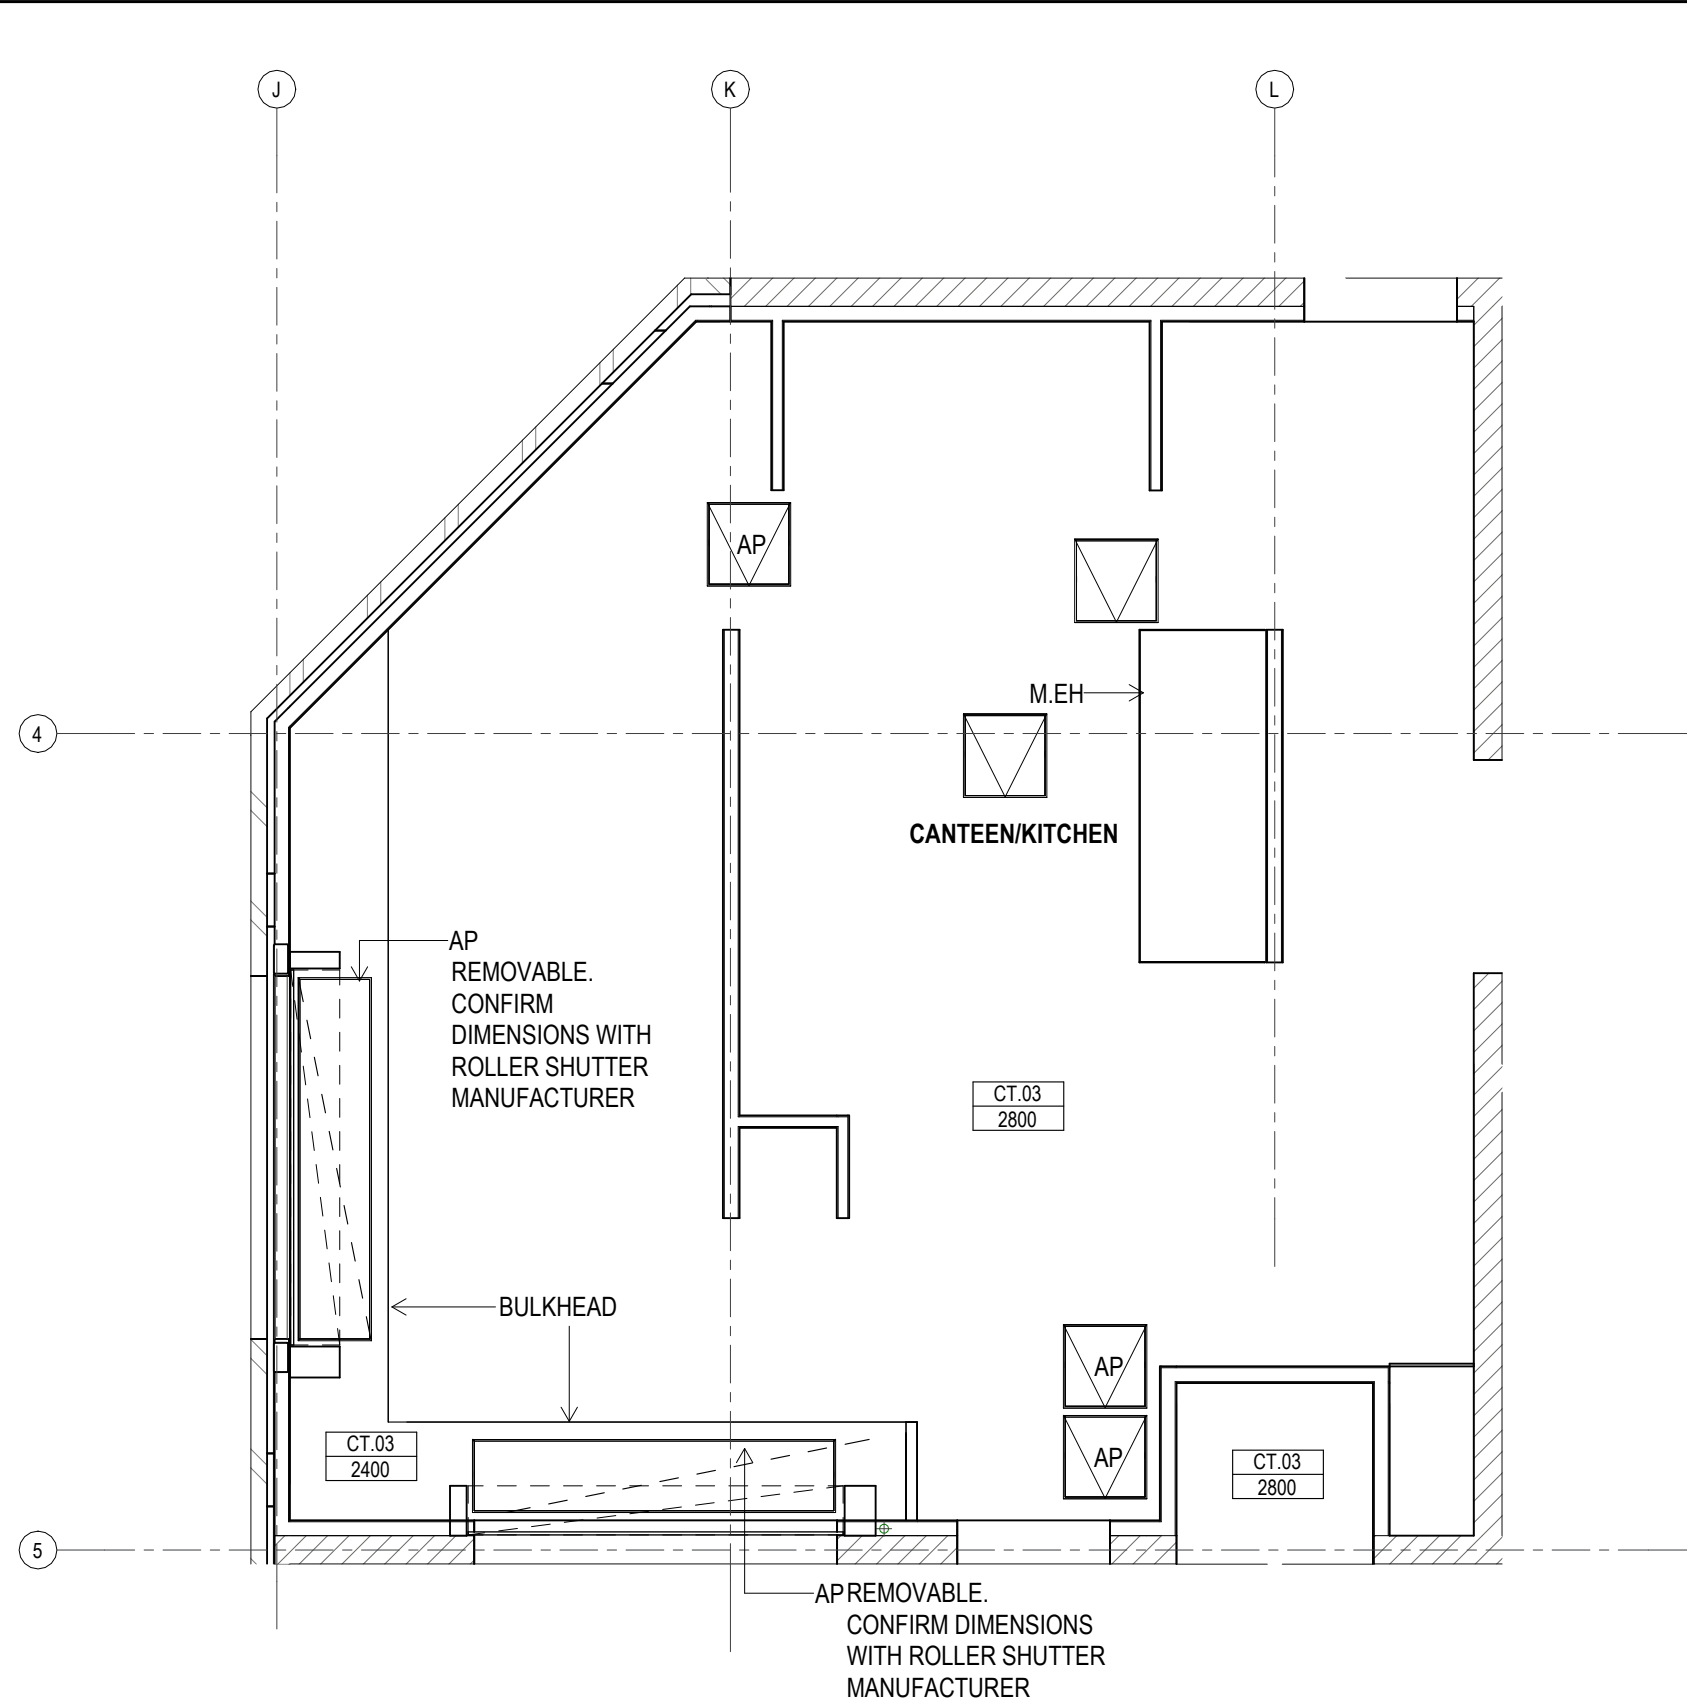


2 REFLECTED CEILING PLAN CANTEEN / KITCHEN
Scale: 1: 50

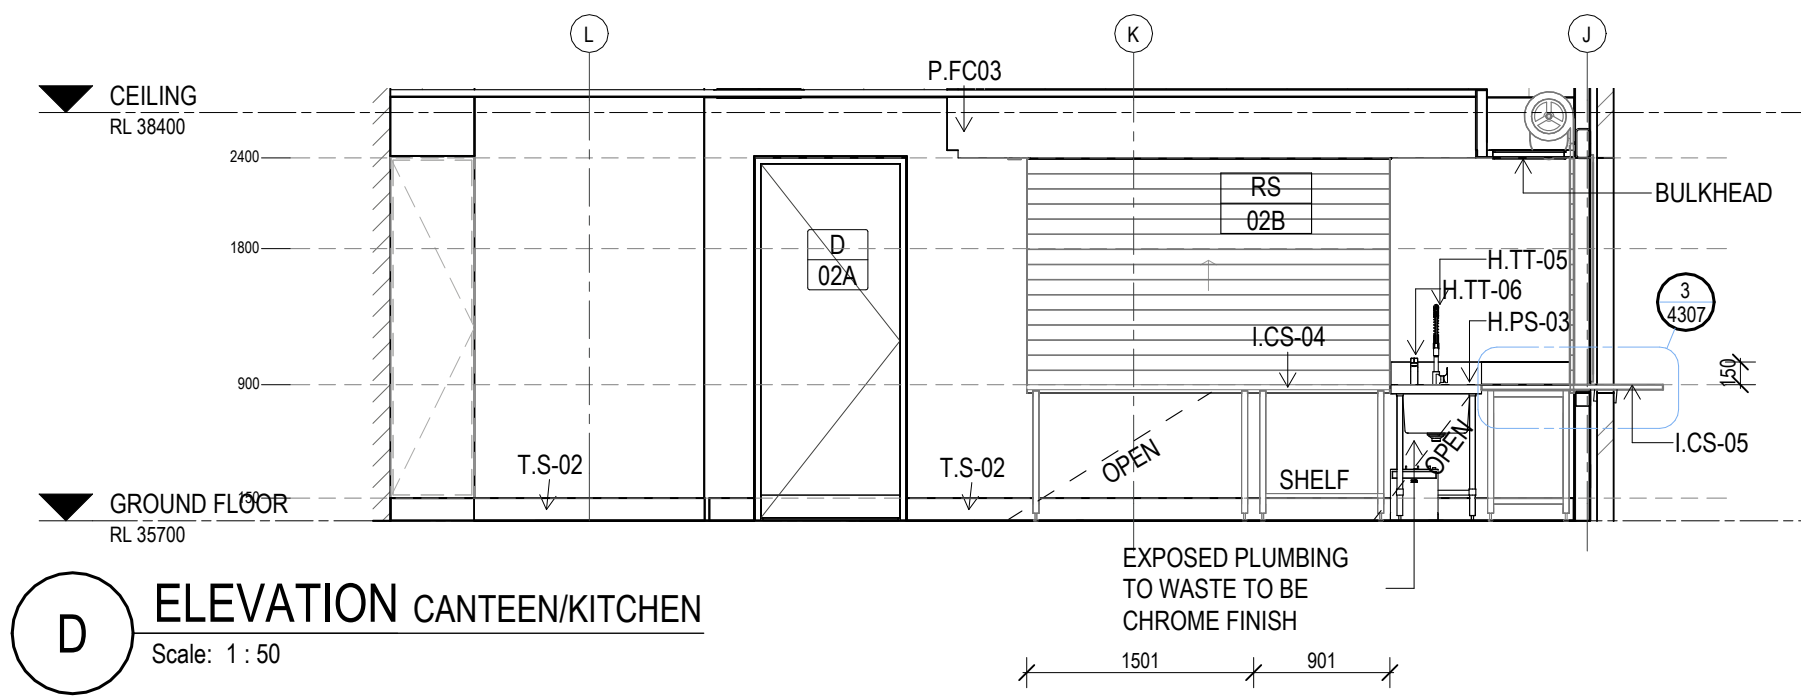


D ELEVATION CANTEEN/KITCHEN
Scale: 1: 50

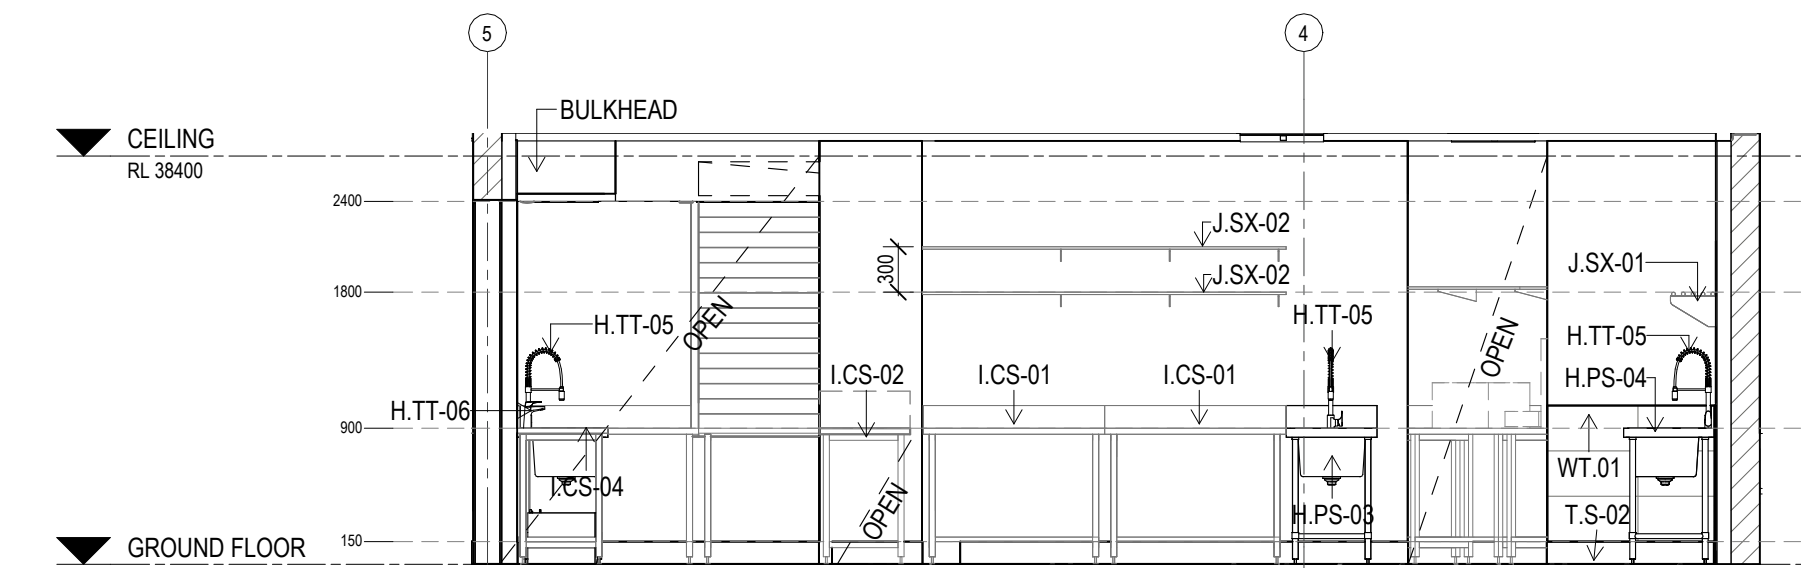


E ELEVATION CANTEEN/KITCHEN
Scale: 1: 50

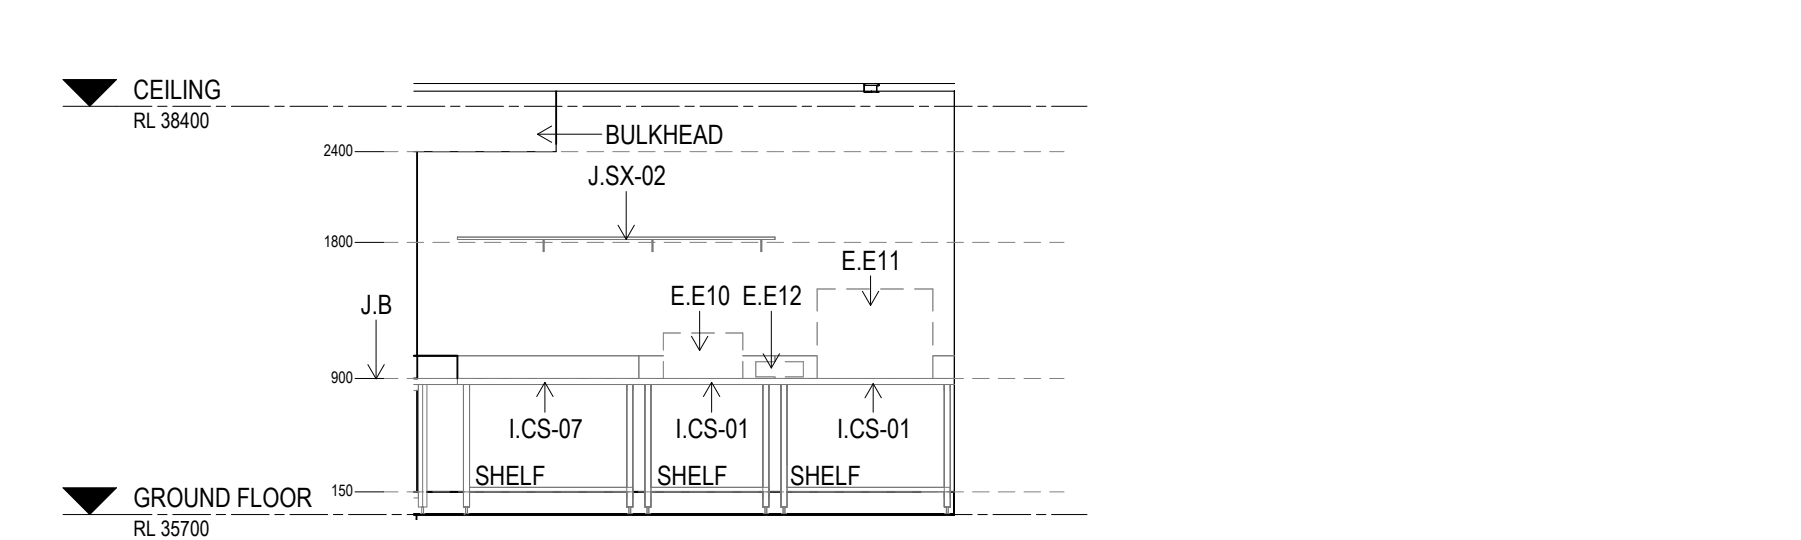


F ELEVATION CANTEEN/KITCHEN
Scale: 1: 50

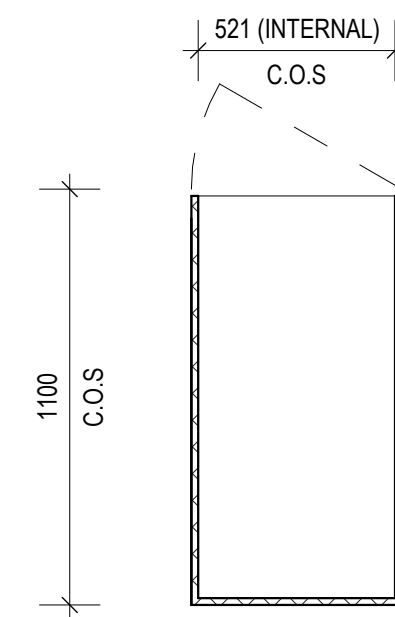


5 DETAIL PLAN JU-04
Scale: 1: 20

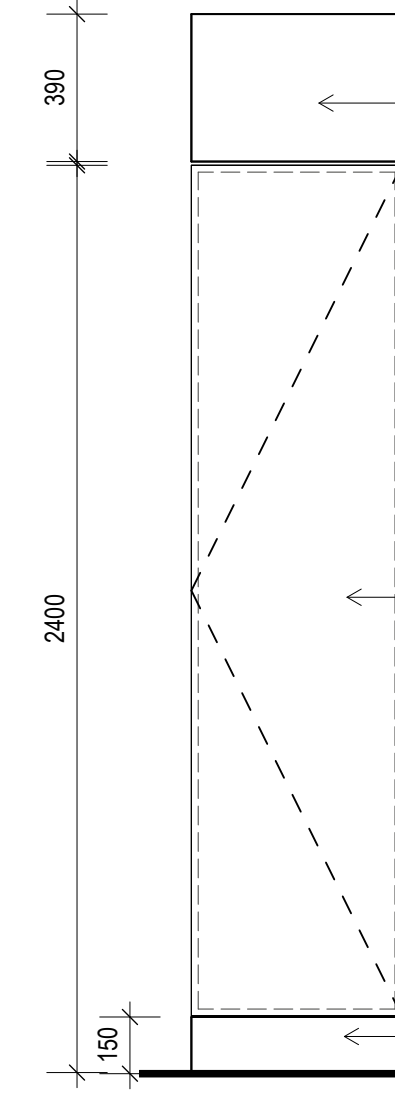


4 ELEVATION JU-04
Scale: 1: 20

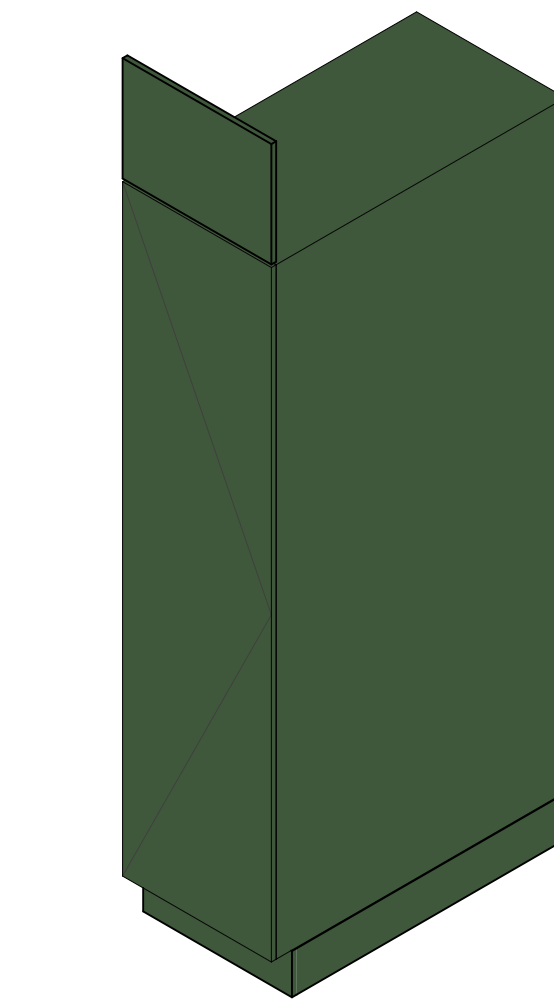


6 3D VIEW JU-04
Scale: NTS

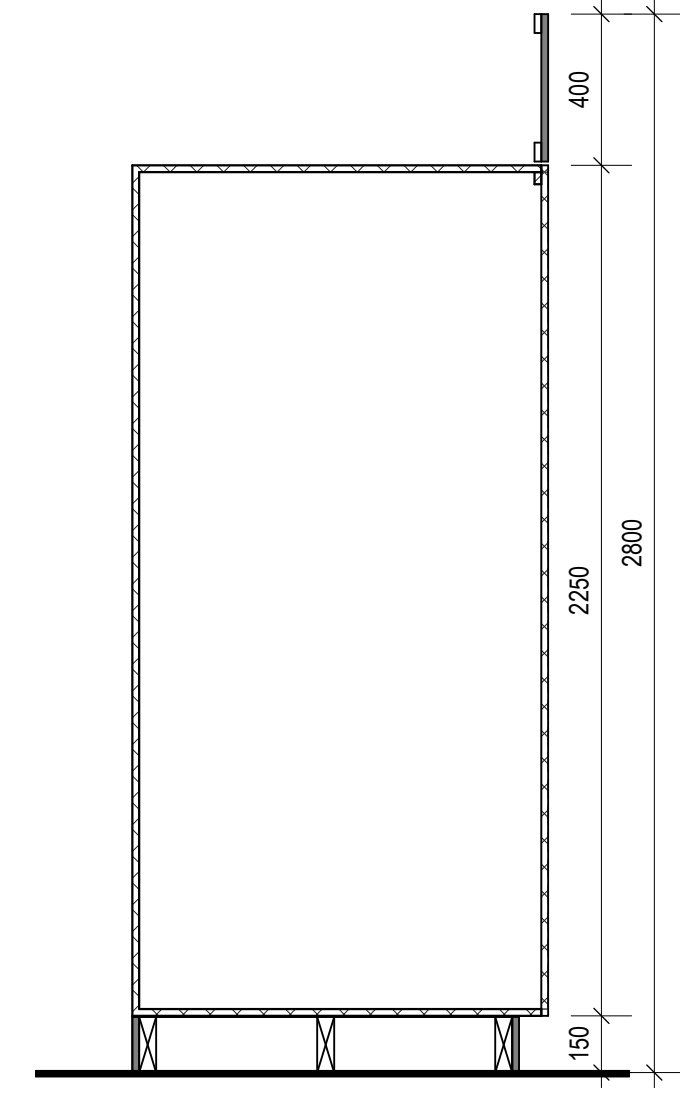

3 DETAIL SECTION JU-04
Scale: 1: 20

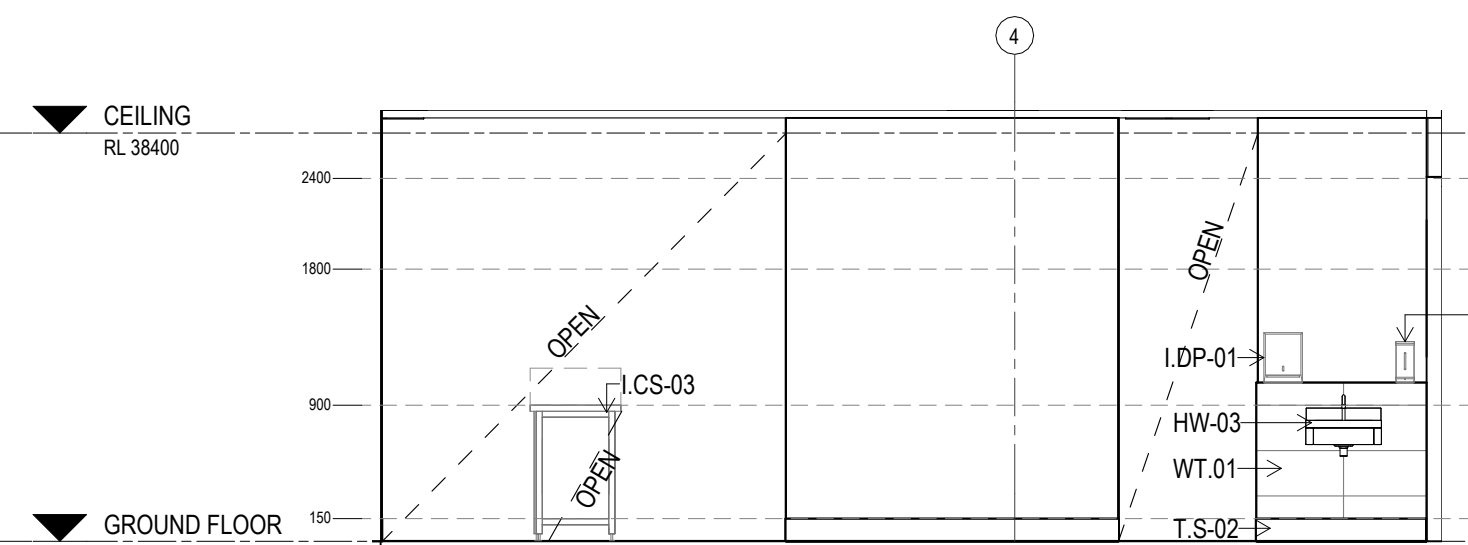


G ELEVATION CANTEEN/KITCHEN
Scale: 1: 50

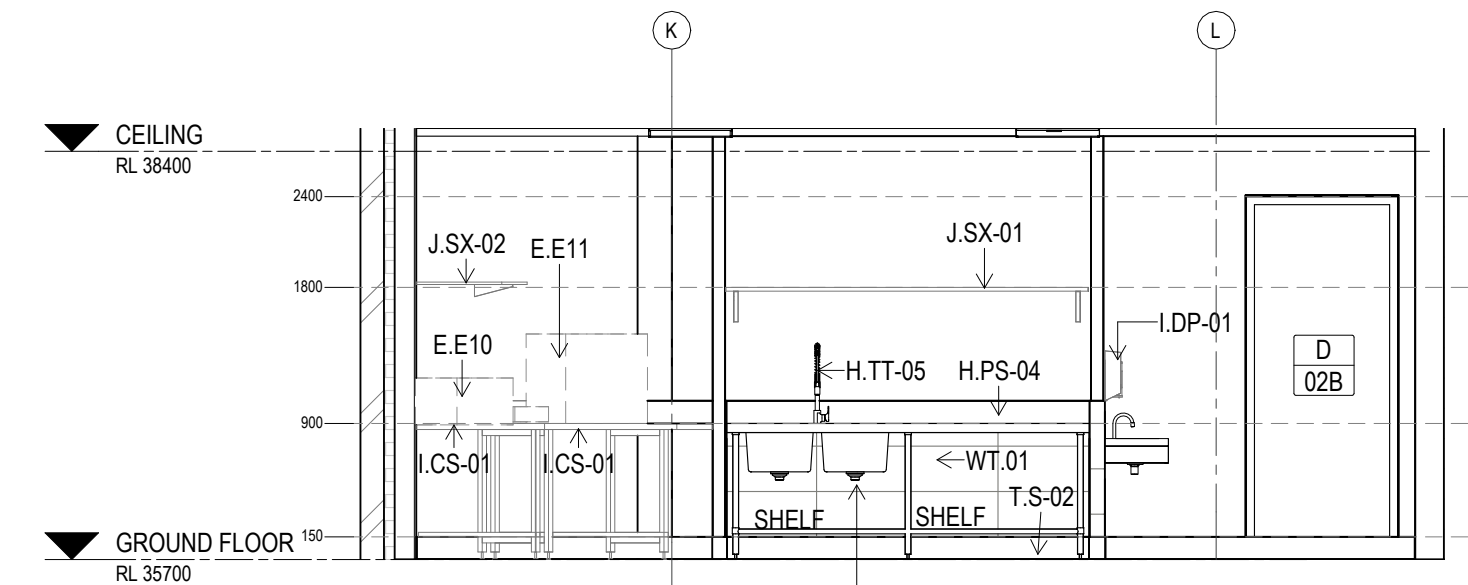

H ELEVATION CANTEEN/KITCHEN
Scale: 1: 50

- These designs and plans are the copyright of MODE DESIGN Corp. Pty Ltd and cannot be reproduced without written permission.
- Verify all dimensions on site prior to commencement of work.
- DO NOT scale off these drawings.
- Report any discrepancies to the architect before carrying out any work.

AMENDMENTS				
REV	DESCRIPTION	AUTH	CHK	DATE
T1	ISSUE FOR TENDER	DW	GB	18/06/26

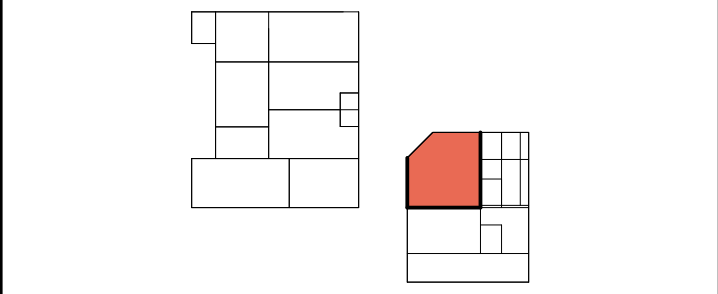

NOTE:
- REFER TO AR-NBC-0010 FOR CODE LIST.

ROOM LAYOUT NOTES

- SUBMIT SHOP DRAWINGS OF ALL JOINERY ITEMS FOR REVIEW PRIOR FABRICATION
- REFER TO TYPICAL FIXTURE HEIGHT SETOUT FOR FIXTURE MOUNTING HEIGHTS - ALL FIXTURE SETOUTS ARE NOMINAL - INSTALL TO MANUFACTURER'S DETAILS
- REFER TO INTERNAL FINISHES SCHEDULE FOR ALL FINISHES INTERNAL
- REFER TO FF&E SCHEDULE FOR ALL FIXTURES, FITTINGS AND EQUIPMENT SPECIFICATIONS
- ALLOW FOR NOGGINS AND FRAMING TO SUPPORT ALL WALL-MOUNTED INSTALLATIONS
- ALL CUBICLE DOORS TO INCLUDE PRIVACY INDICATOR LOCKSETS
- REFER FF&E SCHEDULE FOR TYPE SPECIFICATION

FURNITURE & EQUIPMENT

- ALL JOINERY, EQUIPMENT AND LOOSE FURNITURE SHOWN DASHED GREY ARE INDICATIVE ONLY AND TO BE PROVIDED BY OTHERS
- ITEMS PROVIDED BY BCC:
 - COLD ROOM/RY SHET (AR-4310) FOR DETAILS ON JU-01 & JU-02
 - IN-BENCH APPLIANCES: DEEP FRYER, STOVE, COOK TOP
 - RANGEHOOD
 - PANTRY/KITCHEN STORAGE
 - BILLI BOILER UNIT

- NOTE:
 - TYPICAL SHOWER FALL TO BE 1:80 - 1:80
 - TYPICAL KITCHEN FALL TO BE 1:80 - 1:100
 - TYPICAL PWD SHOWER FALL TO BE 1:80 - 1:80
 - TYPICAL PWD SHOWER FALL TO BE 1:80 - 1:100

NOM. REG. Architect: Rhonan O'Brien QLD 2350 NSW 7176 VIC 16162
TAS 1216 NZ 4712, Peter Bertram QLD 2333 WA 2143 NT AR1213

STATUS
ISSUED FOR TENDER

BRISBANE
mode
Plaza Level, Mosaic
826 Ann St
Fortitude Valley QLD 4006
T +61 7 3253 9900
bne@modedesign.com.au
ABN: 65 112 807 931



CLIENT
SPORTENG™

PROJECT
ROCKHAMPTON NETBALL
CENTRE (STAGE 1) -
NETBALL CLUBHOUSE
554-700 YAAMBA ROAD, NORMAN GARDEN - 4701
DRAWING TITLE
ROOM LAYOUT - CANTEEN
/ KITCHEN

DRAWN DW	CHECKED SM
ISSUE 17/06/2026 2:42:14 PM	SCALE @ A1 As indicated
PROJECT No 24523	STAGE IFT
DRAWING No AR-NBC-3002	REVISION T1