




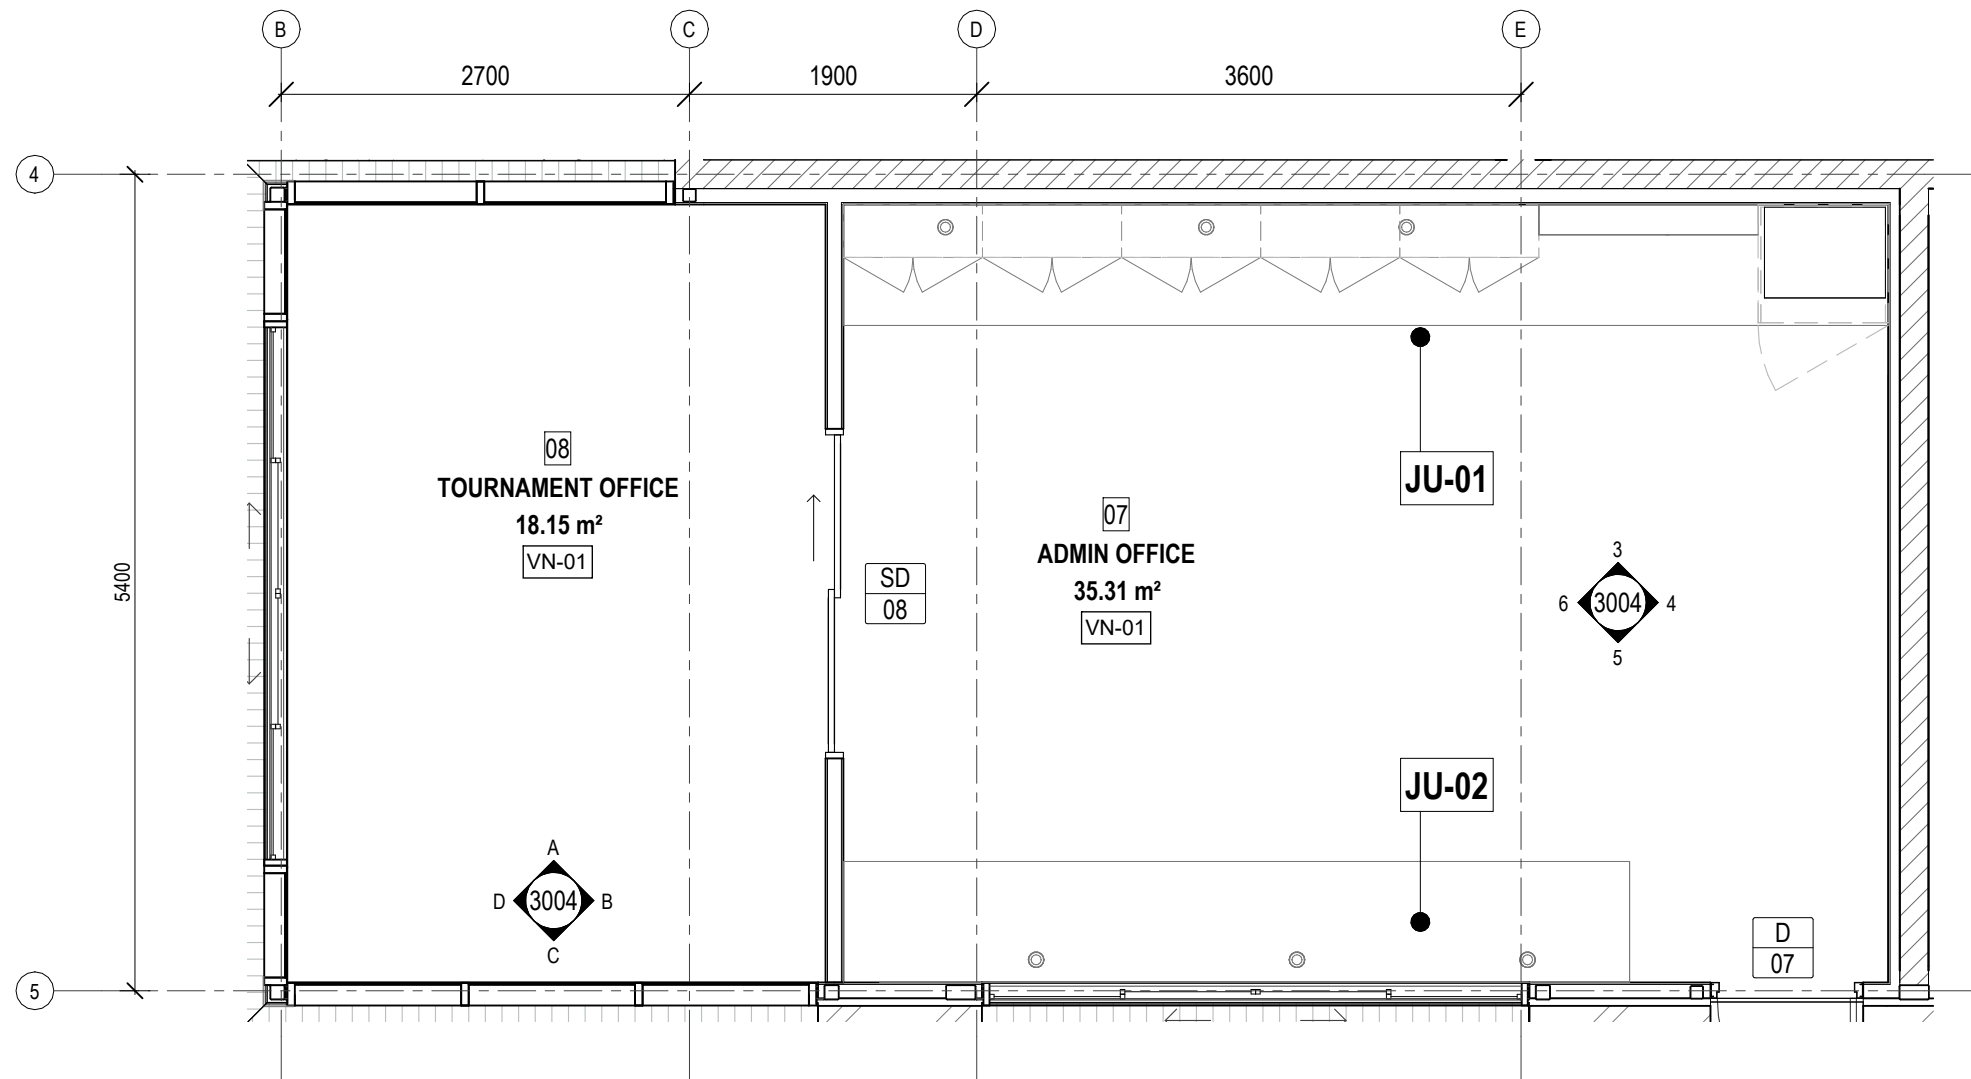


1 PLAN ROOM LAYOUT - ADMIN / TOURNAMENT OFFICE
Scale: 1 : 50

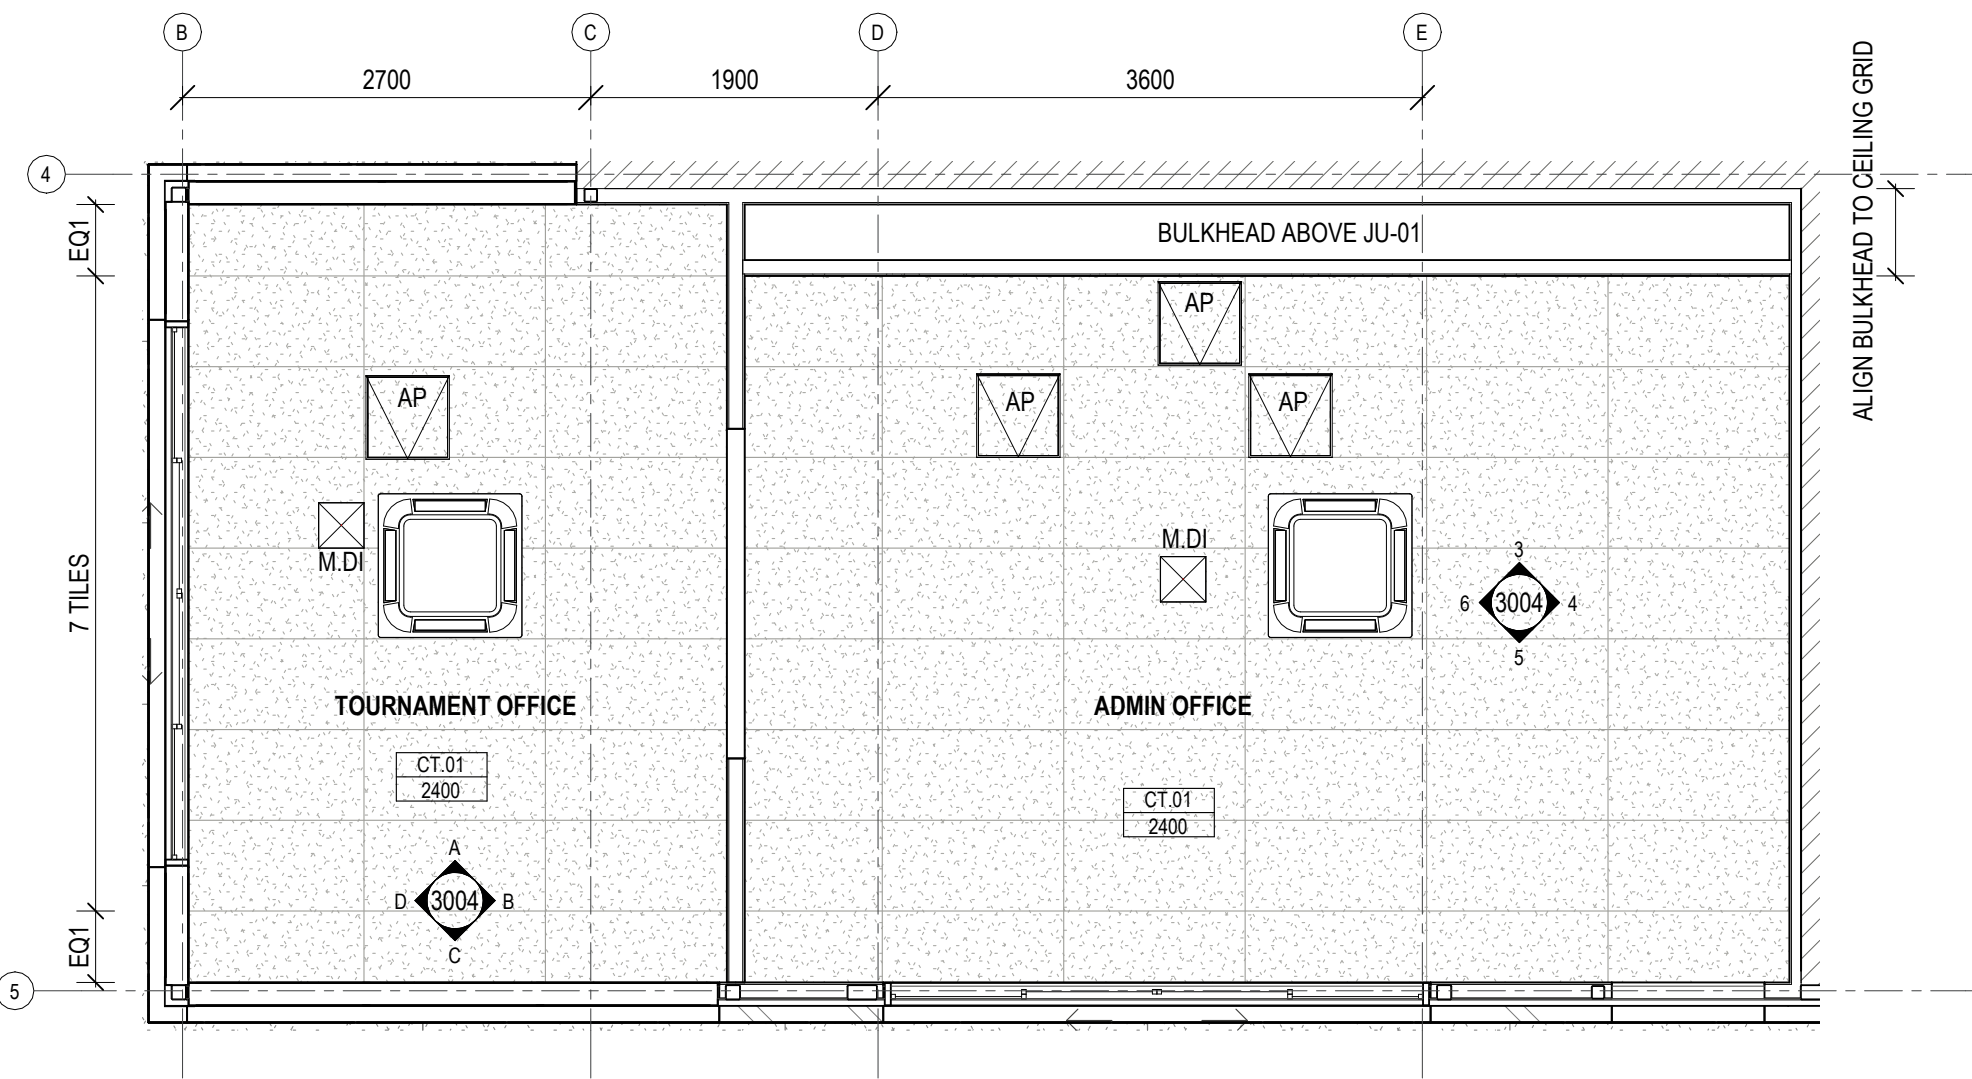


2 REFLECTED CEILING PLAN ROOM LAYOUT - ADMIN / TOURNAMENT OFFICE
Scale: 1 : 50

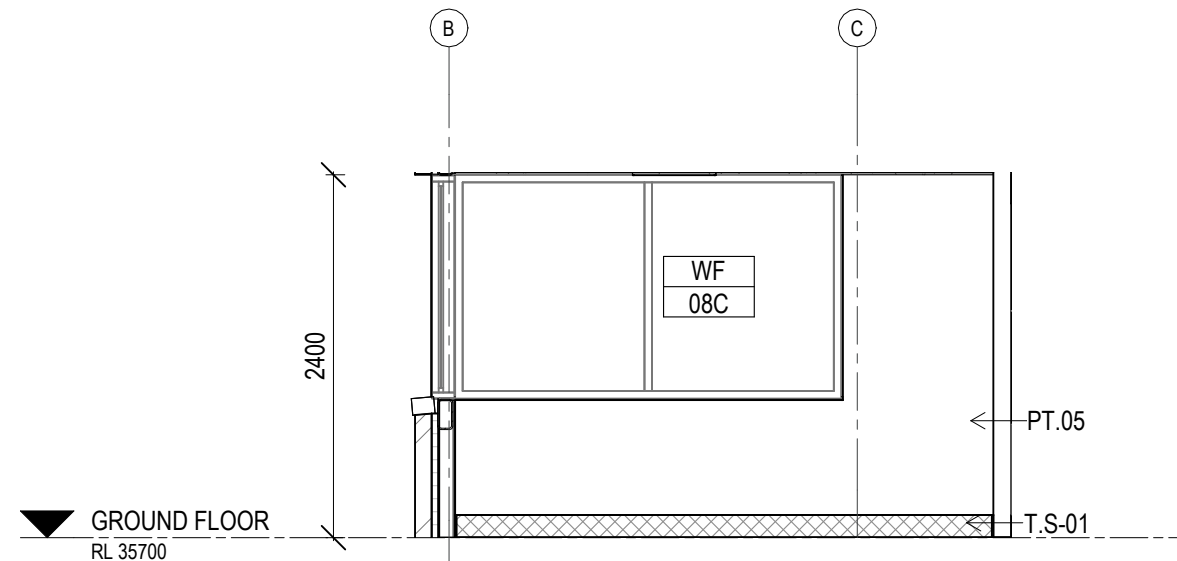


A ELEVATION TOURNAMENT OFFICE
Scale: 1 : 50

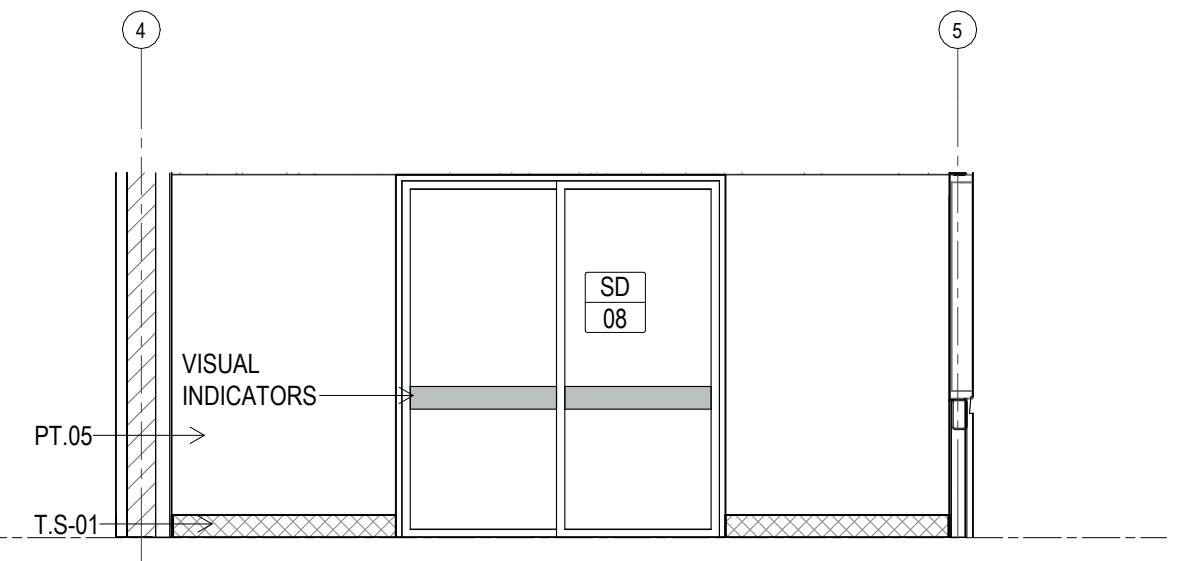


B ELEVATION TOURNAMENT OFFICE
Scale: 1 : 50

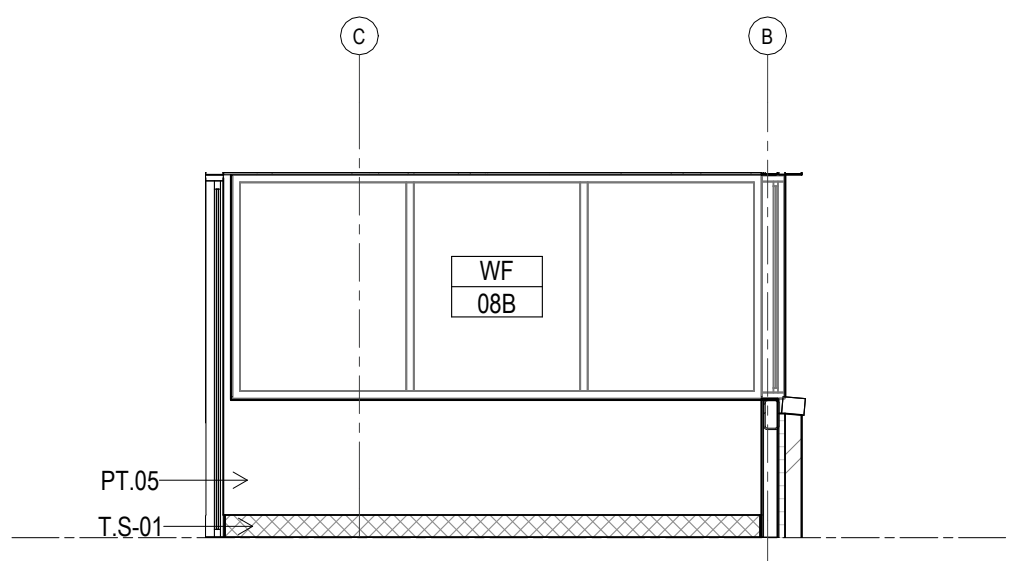


C ELEVATION TOURNAMENT OFFICE
Scale: 1 : 50

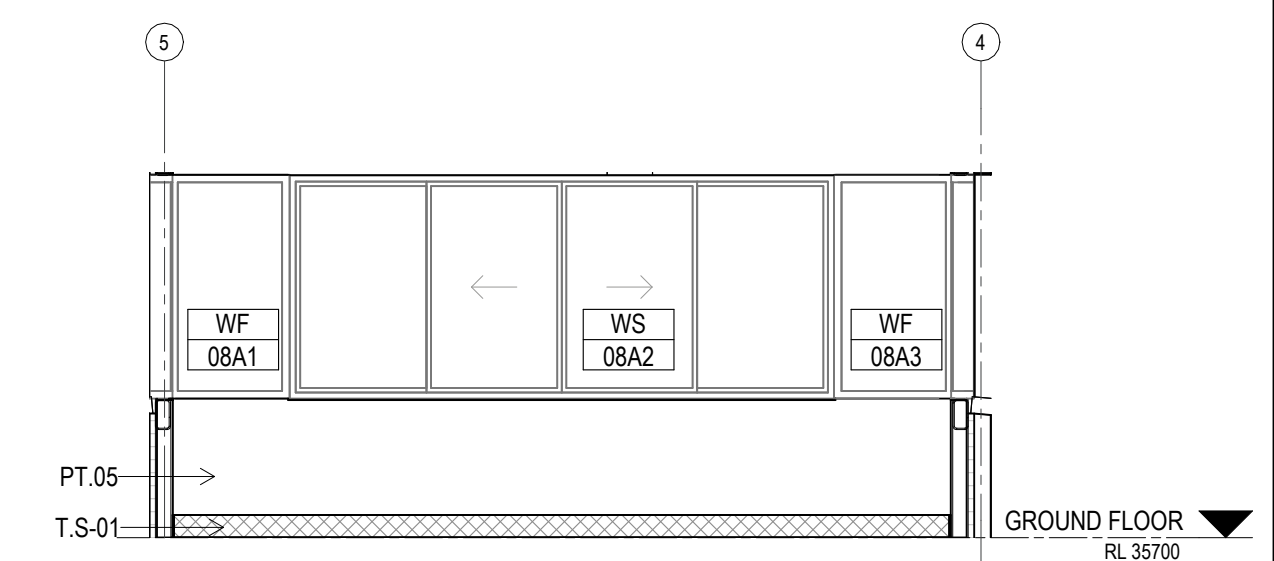


D ELEVATION TOURNAMENT OFFICE
Scale: 1 : 50

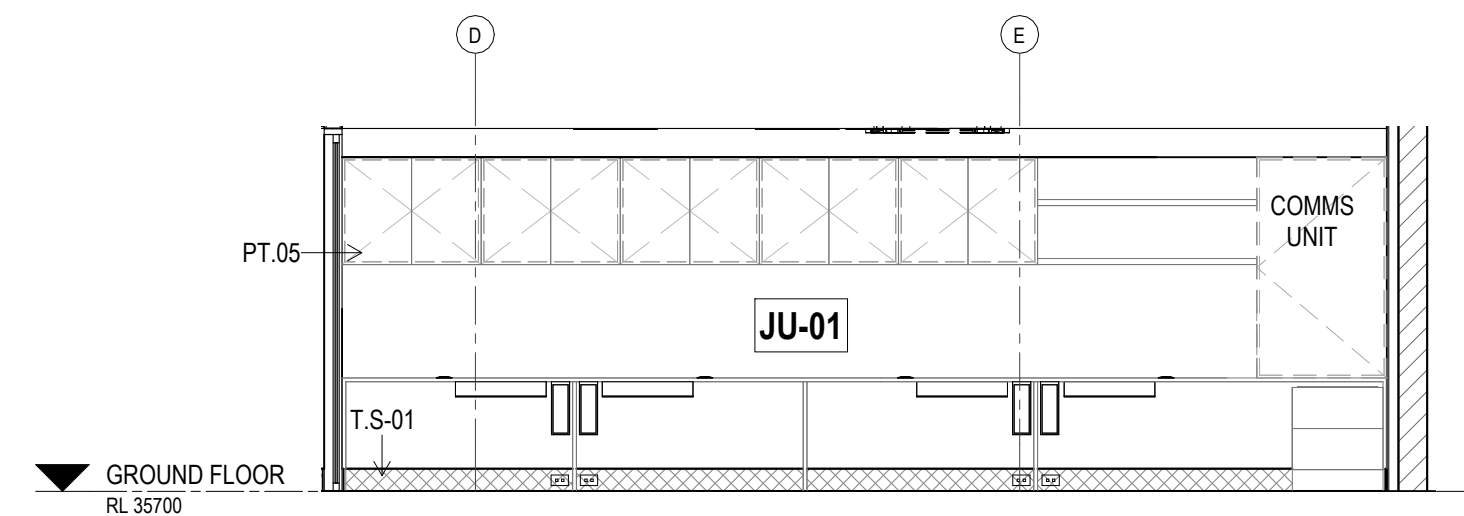


3 ELEVATION ADMIN OFFICE
Scale: 1 : 50

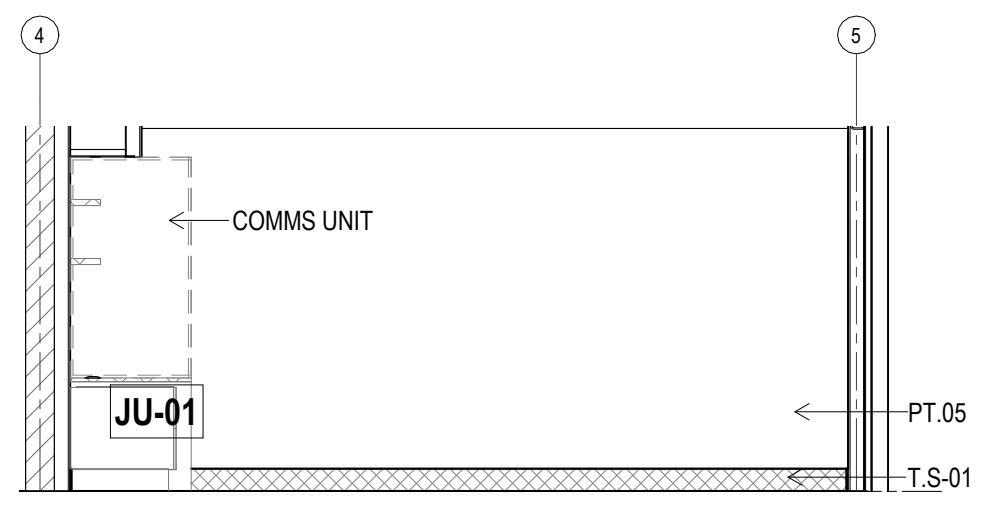

4 ELEVATION ADMIN OFFICE
Scale: 1 : 50

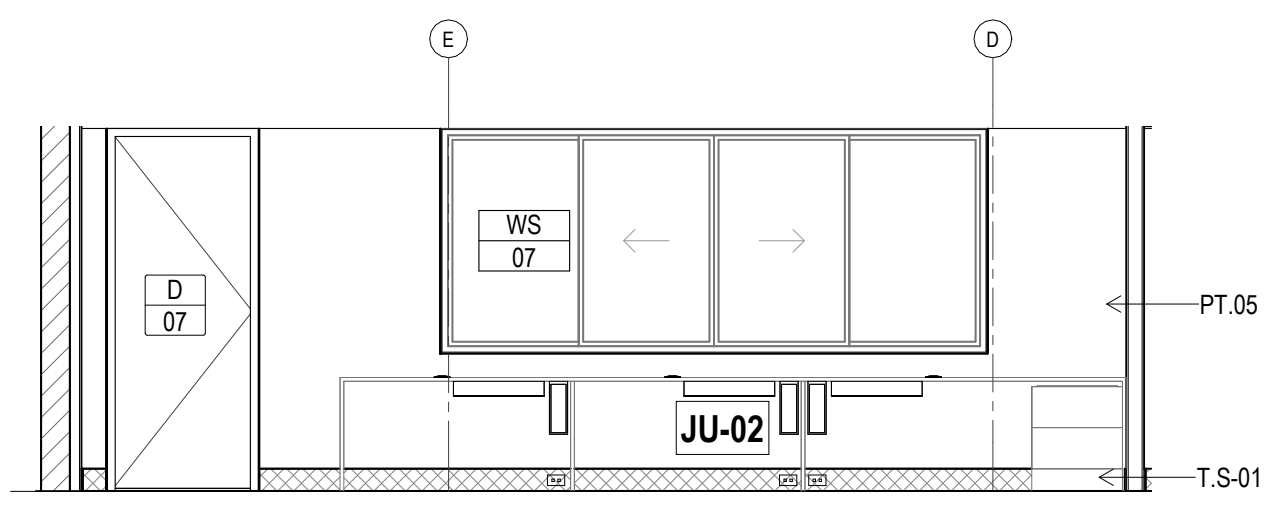

5 ELEVATION ADMIN OFFICE
Scale: 1 : 50

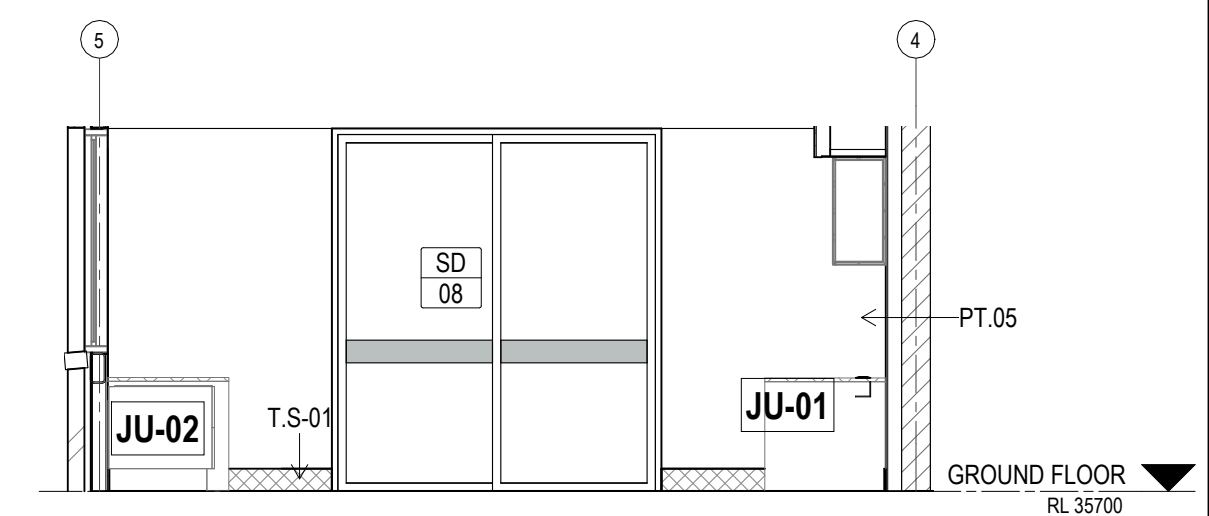

6 ELEVATION ADMIN OFFICE
Scale: 1 : 50

• These designs and plans are the copyright of MODE DESIGN Corp. Pty Ltd and cannot be reproduced without written permission.

• Verify all dimensions on site prior to commencement of work.

• DO NOT scale off these drawings.

• Report any discrepancies to the architect before carrying out any work.

AMENDMENTS				
REV	DESCRIPTION	AUTH	CHK	DATE
T1	ISSUE FOR TENDER	DW	GB	18/06/26

NOTE:

- REFER TO AR-NBC-0010 FOR CODE LIST.

ROOM LAYOUT NOTES

SUBMIT SHOP DRAWINGS OF ALL JOINERY ITEMS FOR REVIEW PRIOR FABRICATION

REFER TO TYPICAL FIXTURE HEIGHT SETOUT FOR FIXTURE MOUNTING

HEIGHTS - ALL FIXTURE SETOUTS ARE NOMINAL - INSTALL TO MANUFACTURER'S DETAILS

REFER TO INTERNAL FINISHES SCHEDULE FOR ALL FINISHES INTERNAL

REFER TO FF&E SCHEDULE FOR ALL FIXTURES, FITTINGS AND EQUIPMENT SPECIFICATIONS

ALLOW FOR NOGGINS AND FRAMING TO SUPPORT ALL WALL-MOUNTED INSTALLATIONS

ALL CUBICLE DOORS TO INCLUDE PRIVACY INDICATOR LOCKSETS

REFER FF&E SCHEDULE FOR TYPE SPECIFICATION

FURNITURE & EQUIPMENT

ALL JOINERY, EQUIPMENT AND LOOSE FURNITURE SHOWN DASHED GREY ARE INDICATIVE ONLY AND TO BE PROVIDED BY OTHERS

REFER TO JOINERY SHEET (AR-4310) FOR DETAILS ON JU-01 & JU-02

FALL TO FLOOR WASTE

NOTE:

- TYPICAL SHOWER FALL TO BE 1:80 - 1:80
- TYPICAL KITCHEN FALL TO BE 1:80 - 1:100
- TYPICAL PWD SHOWER FALL TO BE 1:80 - 1:80
- TYPICAL PWD SHOWER FALL TO BE 1:80 - 1:100

NOM. REG. Architect: Rhonan O'Brien QLD 2350 NSW 7176 VIC 16162
TAS 1216 NZ 4712, Peter Bertram QLD 2333 WA 2143 NT AR1213

STATUS
ISSUED FOR TENDER

0m 0.5 1 1.5 2 2.5

BRISBANE

mode Plaza Level, Mosaic
826 Ann St
Fortitude Valley QLD 4006
T +61 7 3253 9900
bne@modedesign.com.au
ABN: 65 112 807 931

Rockhampton Regional Council

CLIENT
SPORTENG™

PROJECT
ROCKHAMPTON NETBALL CENTRE (STAGE 1) - NETBALL CLUBHOUSE
554-700 YAAMBA ROAD, NORMAN GARDEN - 4701

DRAWING TITLE
ROOM LAYOUT - ADMIN / TOURNAMENT OFFICE

DRAWN DW	CHECKED SM
ISSUE 17/06/2026 2:42:18 PM As indicated	SCALE @ A1 As indicated
PROJECT No 24523	STAGE IFT
DRAWING No AR-NBC-3004	REVISION T1