

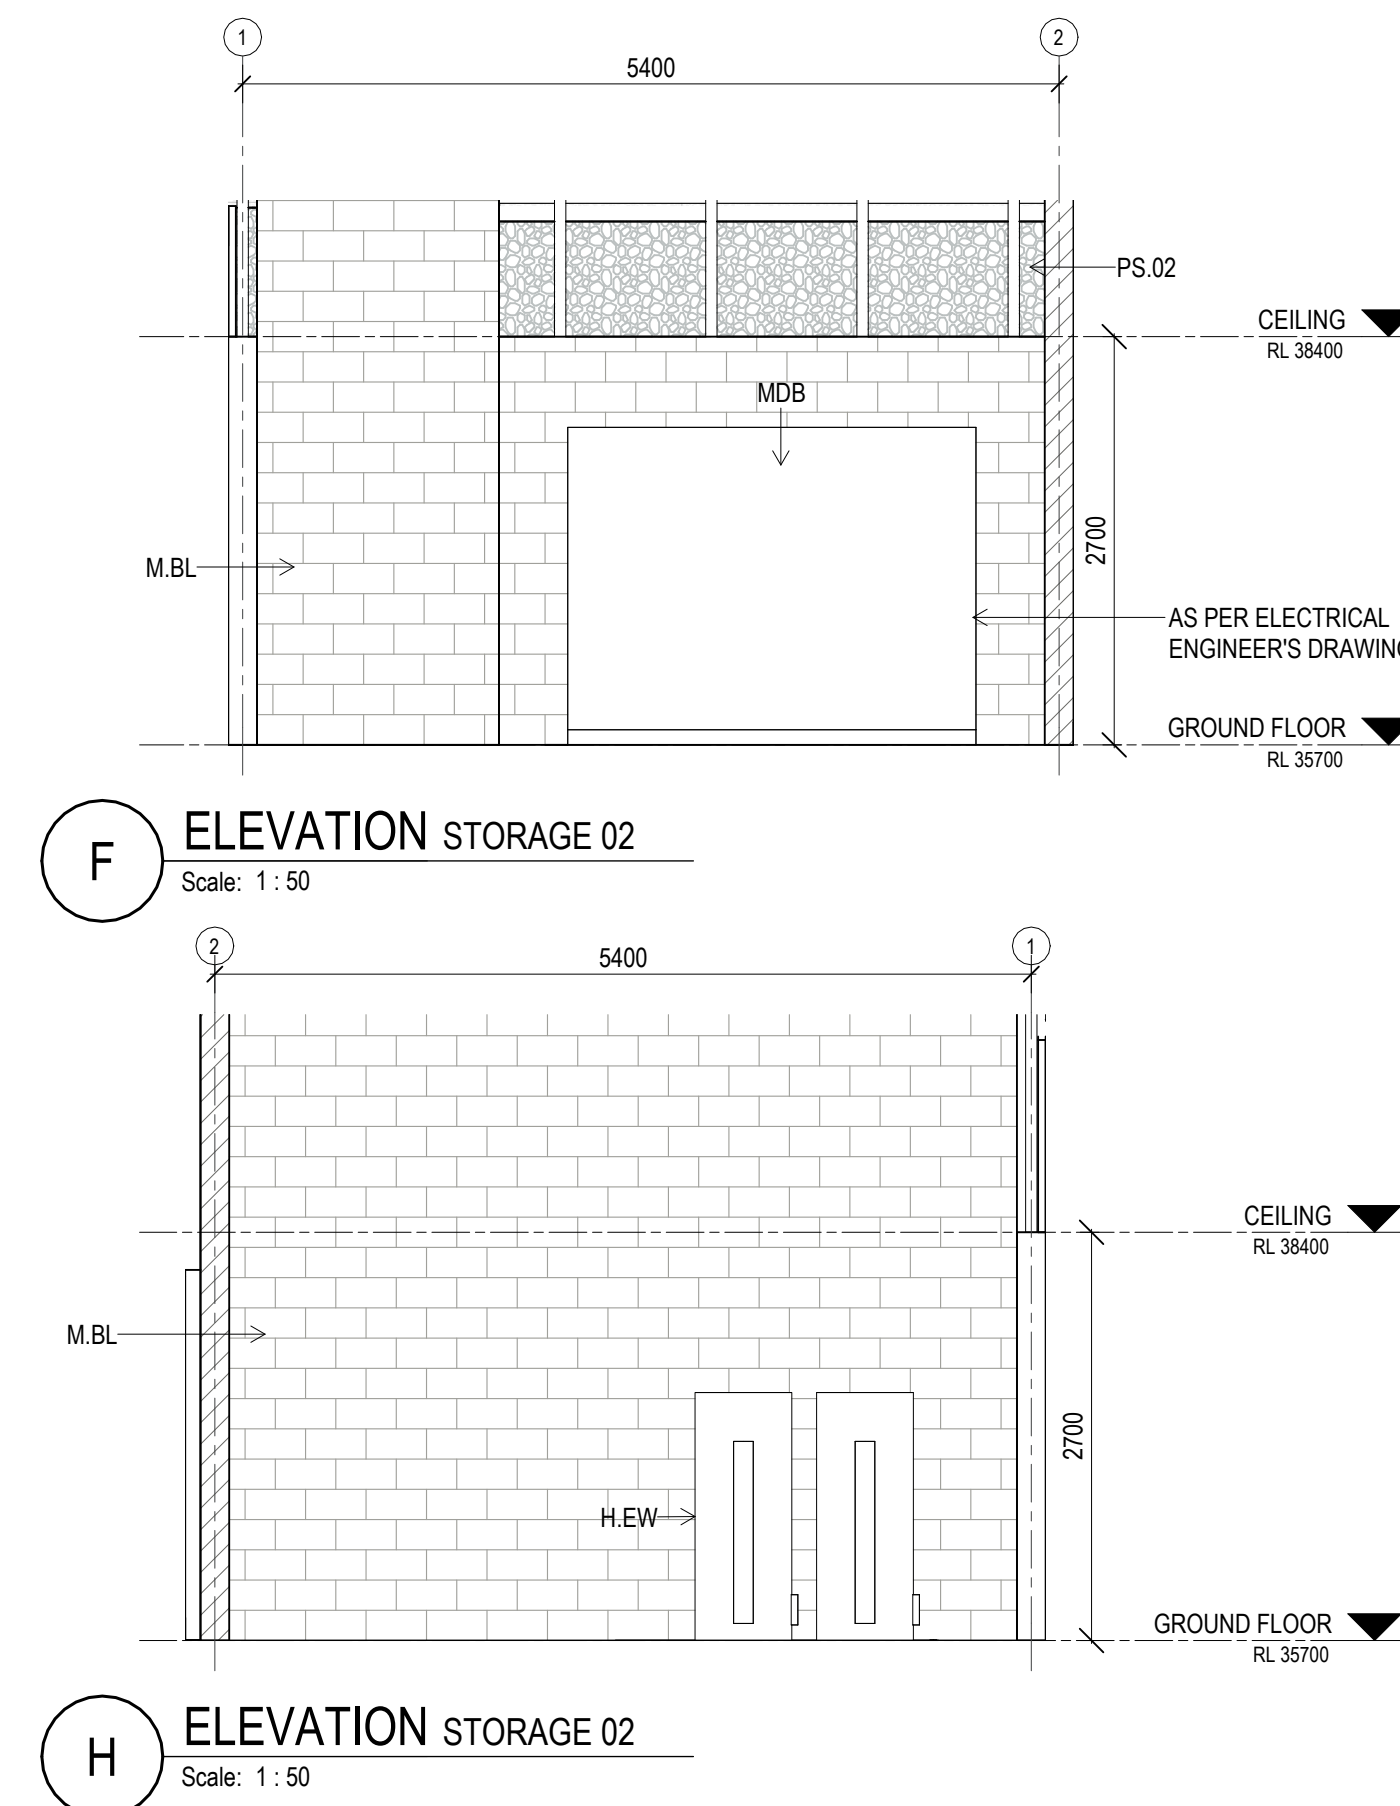
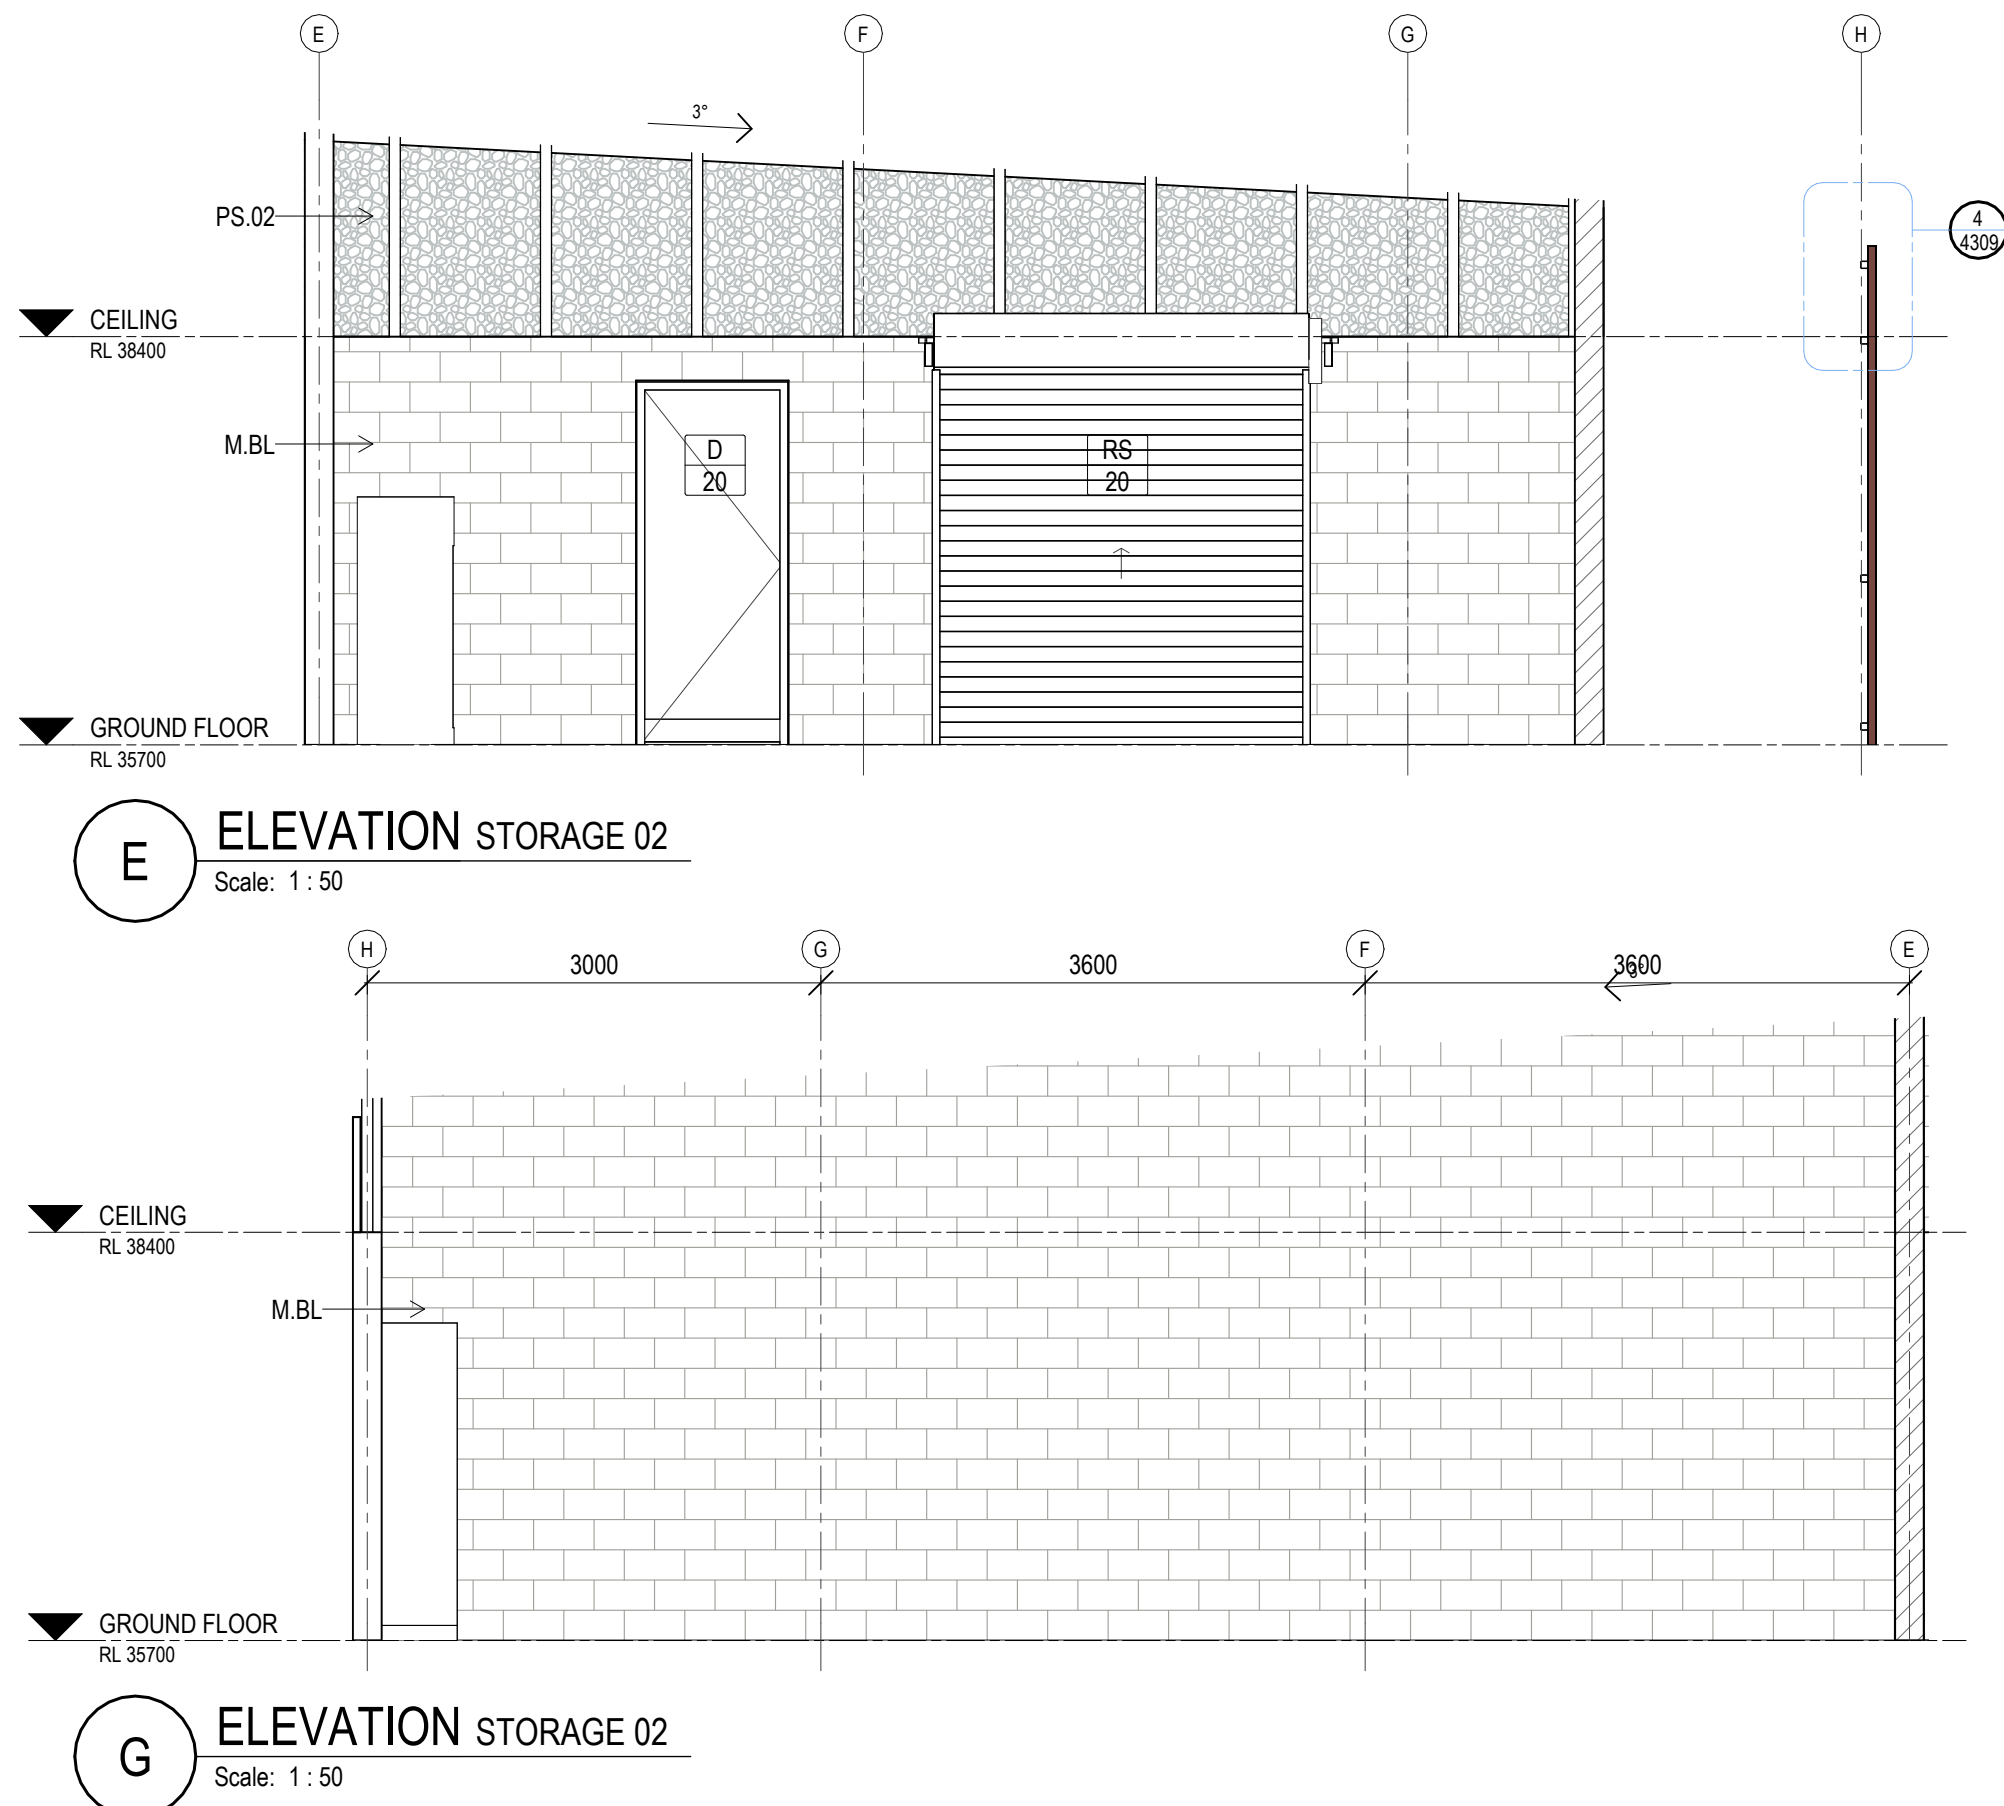
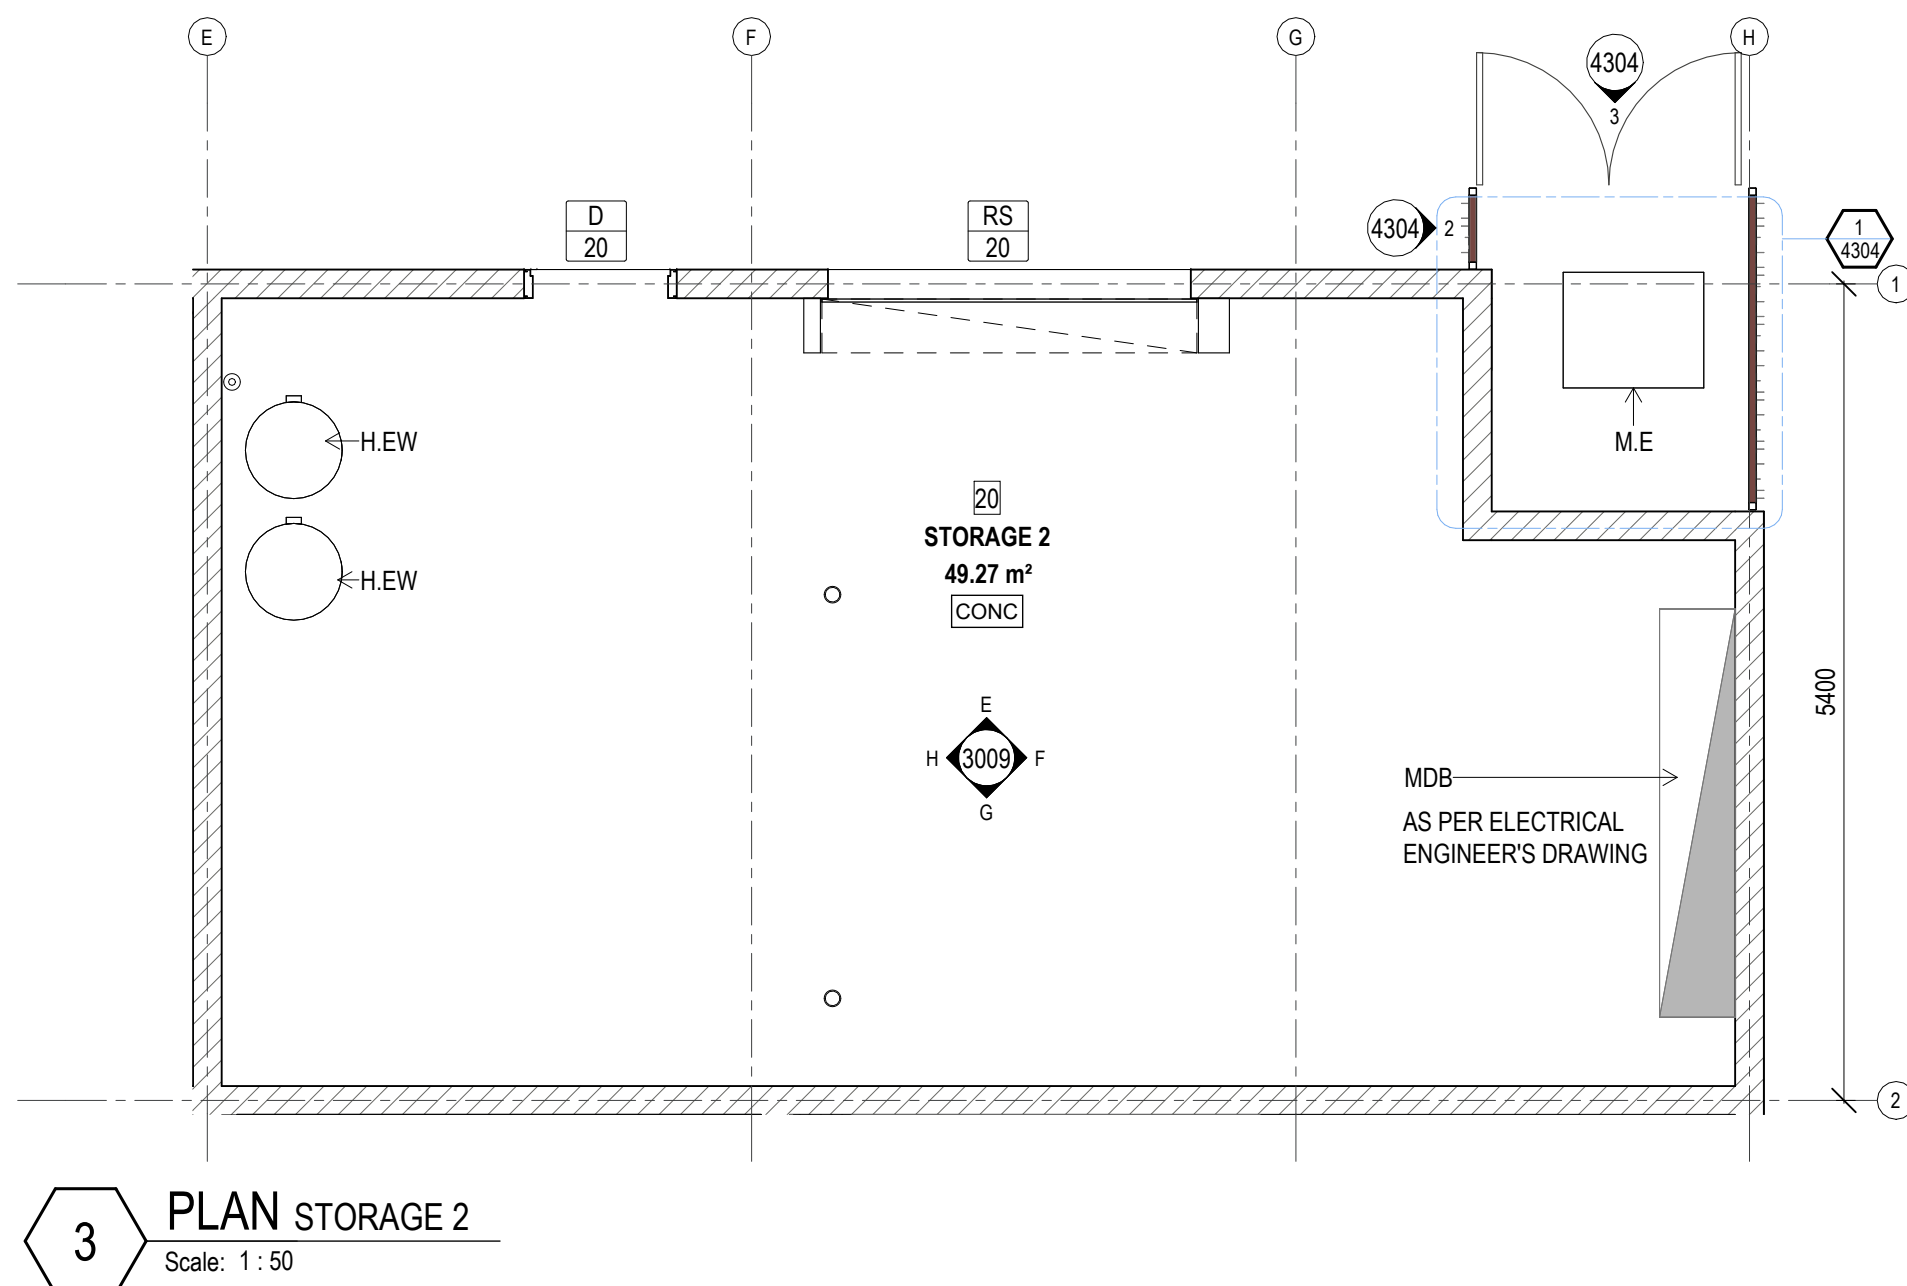


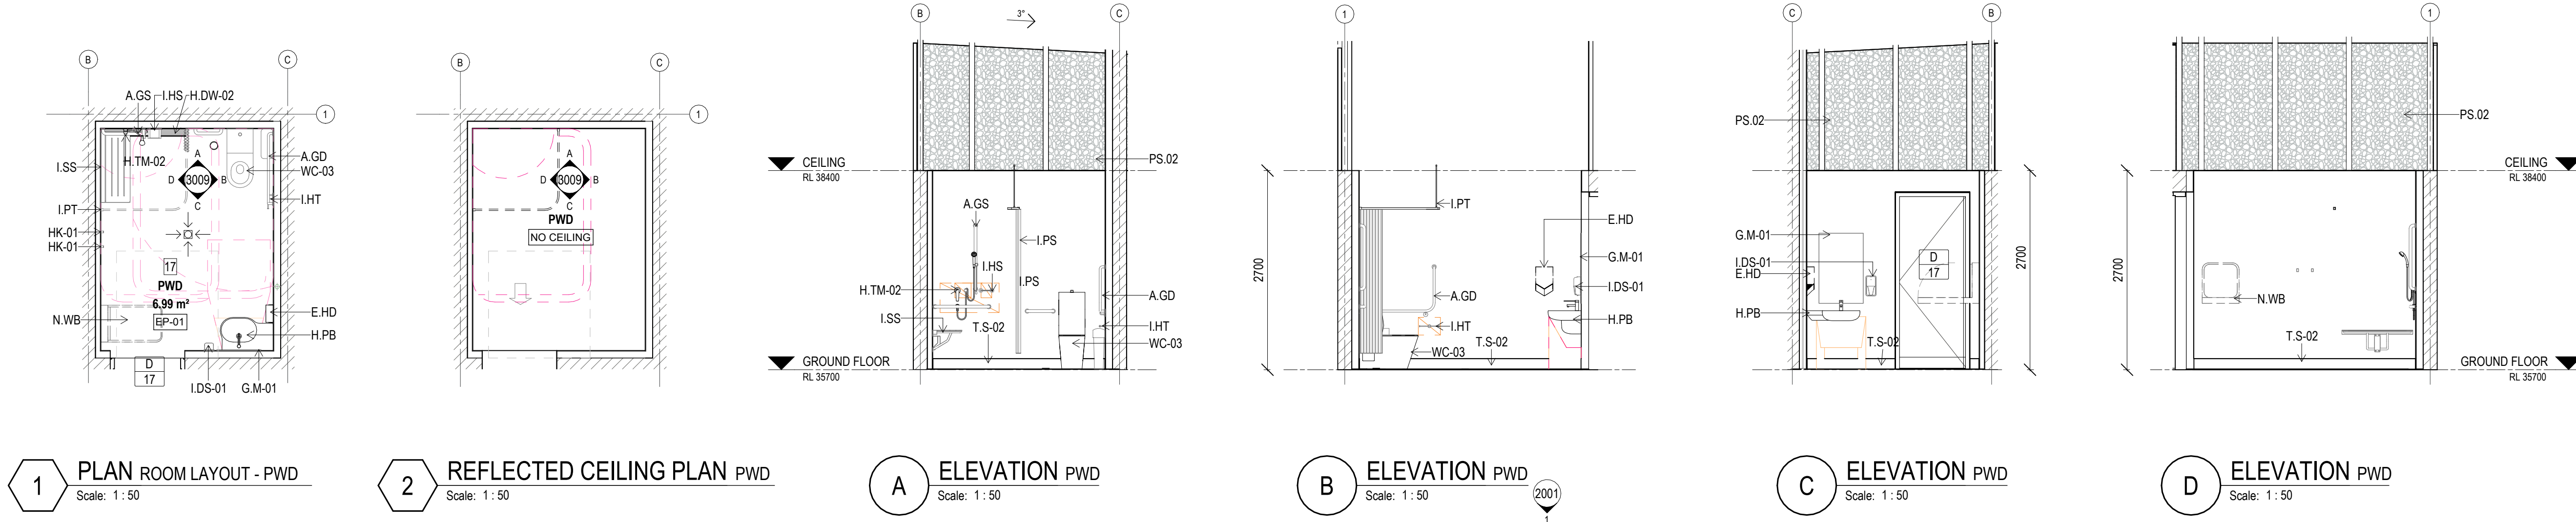

- These designs and plans are the copyright of MODE DESIGN Corp. Pty Ltd and cannot be reproduced without written permission.
- Verify all dimensions on site prior to commencement of work.
- DO NOT scale off these drawings.
- Report any discrepancies to the architect before carrying out any work.

AMENDMENTS				
REV	DESCRIPTION	AUTH	CHK	DATE
T1	ISSUE FOR TENDER	DW	GB	18/06/26

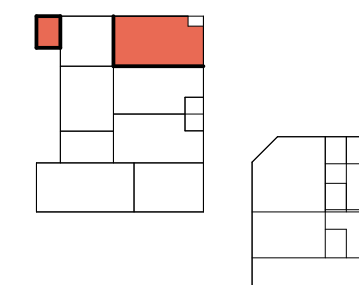

NOTE:
- REFER TO AR-NBC-0010 FOR CODE LIST.

ROOM LAYOUT NOTES	
SUBMIT SHOP DRAWINGS OF ALL JOINERY ITEMS FOR REVIEW PRIOR FABRICATION	
REFER TO TYPICAL FIXTURE HEIGHT SETOUT FOR FIXTURE MOUNTING HEIGHTS - ALL FIXTURE SETOUTS ARE NOMINAL - INSTALL TO MANUFACTURER'S DETAILS	
REFER TO INTERNAL FINISHES SCHEDULE FOR ALL FINISHES INTERNAL	
REFER TO FF&E SCHEDULE FOR ALL FIXTURES, FITTINGS AND EQUIPMENT SPECIFICATIONS	
ALLOW FOR NOGGINs AND FRAMING TO SUPPORT ALL WALL-MOUNTED INSTALLATIONS	
ALL CUBICLE DOORS TO INCLUDE PRIVACY INDICATOR LOCKSETS	
REFER FF&E SCHEDULE FOR TYPE SPECIFICATION	
FURNITURE & EQUIPMENT	
ALL JOINERY, EQUIPMENT AND LOOSE FURNITURE SHOWN DASHED GREY ARE INDICATIVE ONLY AND TO BE PROVIDED BY OTHERS	
REFER TO JOINERY SHEET (AR-4310) FOR DETAILS ON JU-01 & JU-02	

- FALL TO FLOOR WASTE
- NOTE:
- TYPICAL SHOWER FALL TO BE 1:80 - 1:80
 - TYPICAL KITCHEN FALL TO BE 1:80 - 1:100
 - TYPICAL PWD SHOWER FALL TO BE 1:80 - 1:80
 - TYPICAL PWD SHOWER FALL TO BE 1:80 - 1:100

NOM. REG. Architect: Rhonan O'Brien QLD 2350 NSW 7176 VIC 16182
TAS 1216 NZ 4712, Peter Bertram QLD 2333 WA 2143 NT AR1213

STATUS
ISSUED FOR TENDER

0m 0.5 1 1.5 2 2.5

NORTH

BRISBANE

mode

Plaza Level, Mosaic
826 Ann St
Fortitude Valley QLD 4006
T +61 7 3253 9900
bne@modedesign.com.au
ABN: 65 112 807 931

Rockhampton
Regional Council

CLIENT

SPORTENG™

PROJECT
ROCKHAMPTON NETBALL CENTRE (STAGE 1) - NETBALL CLUBHOUSE
554-700 YAAMBA ROAD, NORMAN GARDEN - 4701

DRAWING TITLE
ROOM LAYOUT - PWD / STORAGE

DRAWN DW	CHECKED SM
ISSUE 17/06/2026 2:42:32 PM	SCALE @ A1 As indicated
PROJECT No 24523	STAGE IFT
DRAWING No AR-NBC-3009	REVISION T1