


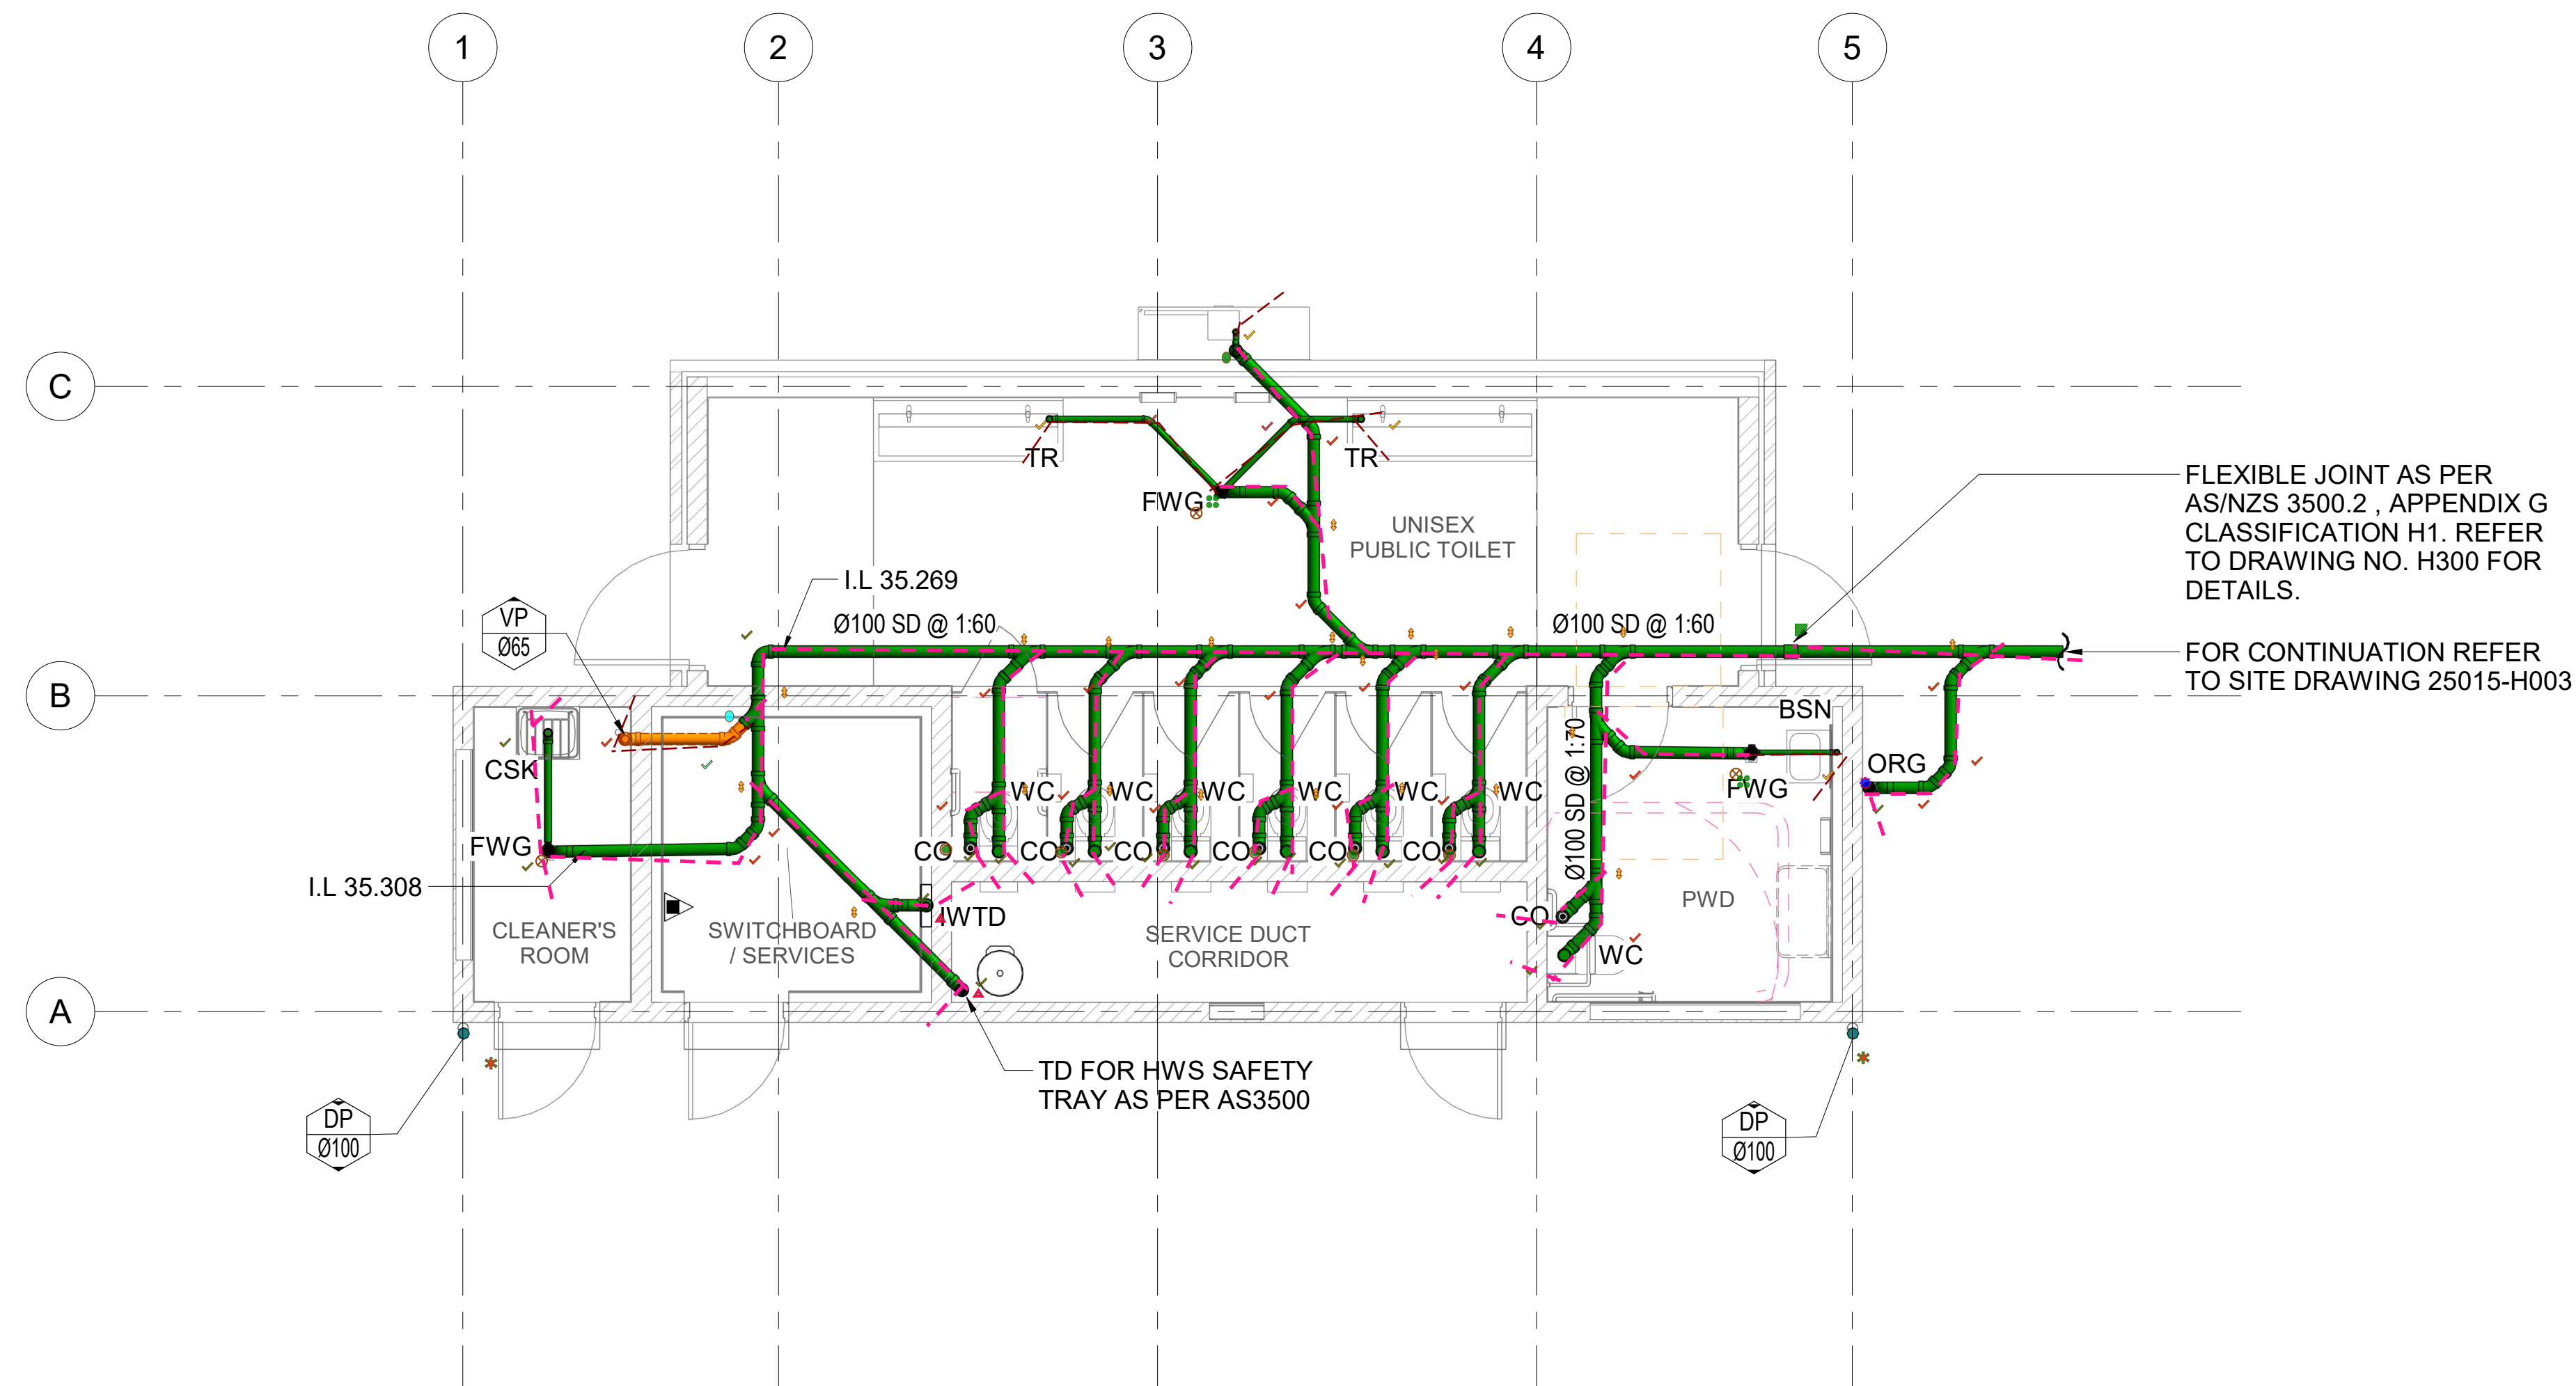

PAM - SANITARY PLUMBING LAYOUT
1 : 50

ALL DIMENSIONS SHOWN IN MM. DO NOT SCALE FROM DRAWINGS.
DIMENSIONS TAKE PRECEDENCE. IF IN DOUBT REFER TO HK SOLUTIONS.

T1	ISSUE FOR TENDER	17.06.2026	MC	HKS
REV.	DESCRIPTION	DATE	INT.	COMPANY
REVISIONS				



ENGINEERING
PROJECT MANAGEMENT
DARWIN, GEELONG,
CAIRNS, TOWNSVILLE,
PERTH, BALLARAT
admin@hksolutions.com.au
www.hksolutions.com.au

Conditions of use. This document may only be used by
Harris Kmon Solutions clients for the purpose for which
it was prepared and must not be used by any other
person or for any other purpose.



DRAWN	MC
CHECKED	WK
DESIGNED	MC
CHECKED	Approver
APPROVED	

THIS DRAWING MUST
NOT BE USED FOR
CONSTRUCTION UNLESS
SIGNED AS APPROVED

FOR TENDER

STAGE 1
ROCKHAMPTON SPORTS PRECINCT - PUBLIC AMENITIES BLOCK
554-700 YAAMBA ROAD, NORMAN GARDEN - 4701
GROUND FLOOR SANITARY PLUMBING LAYOUT

PAGE No	PROJECT No - DRAWING No	DISCIPLINE	REV.	SHEET SIZE
04 of 06	25015-H-PAM-100	HYDRAULIC	T1	A1

DRAWINGS TO BE PRINTED IN COLOUR