




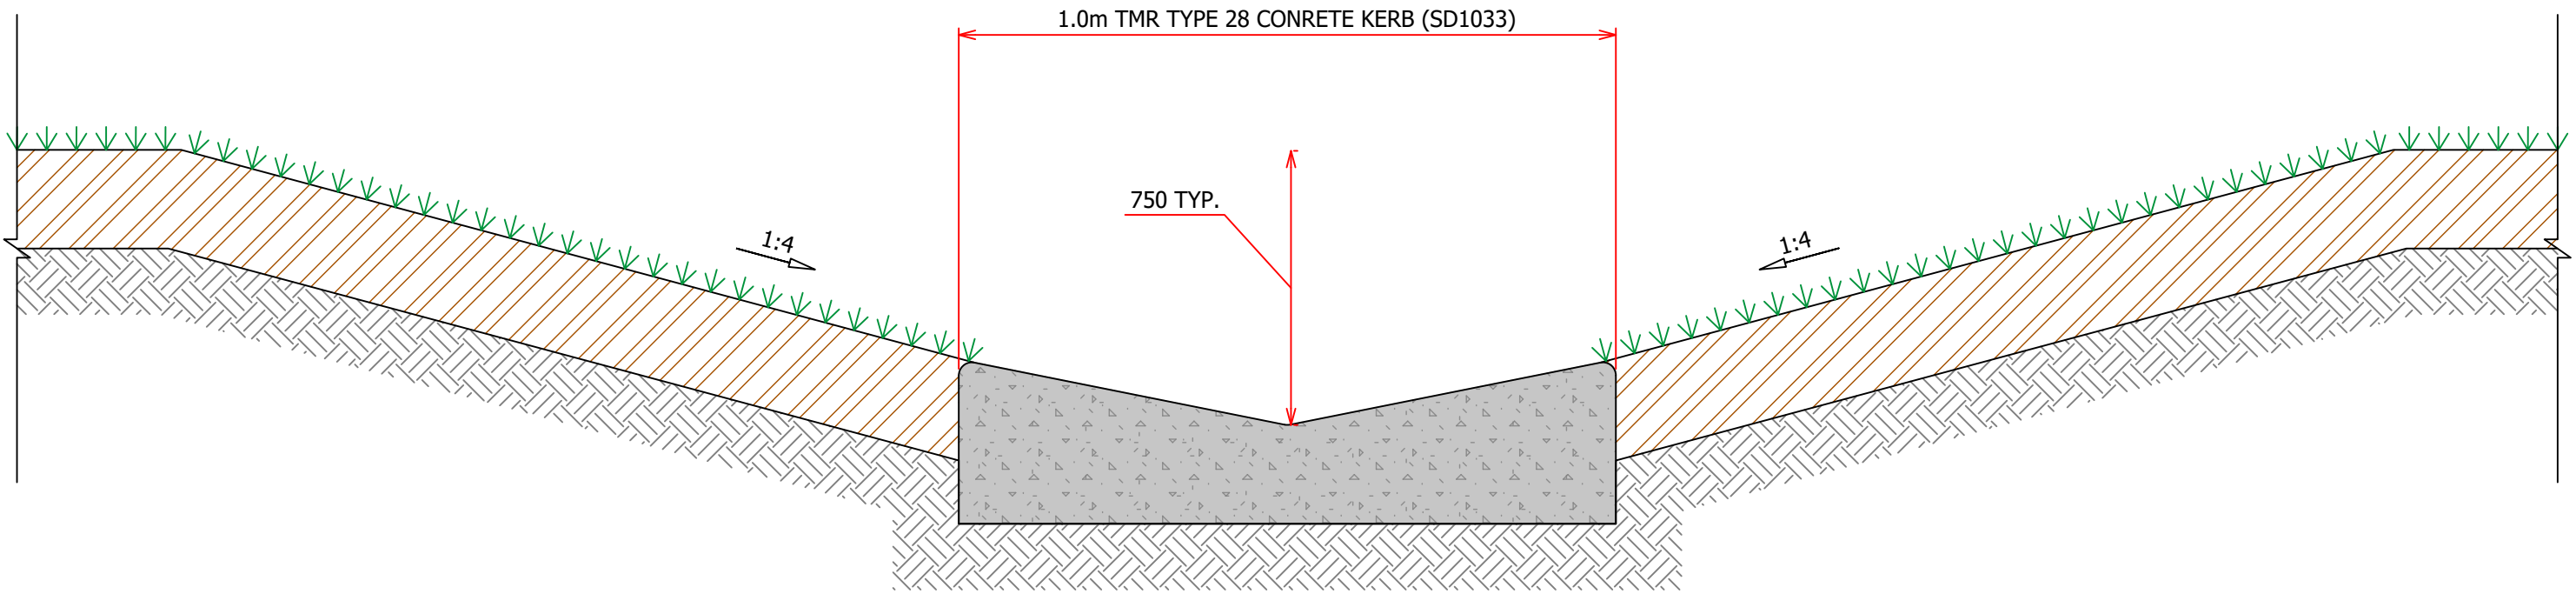

GRASSED SWALE WITH SPOON DRAIN
TYPICAL DETAIL
N.T.S

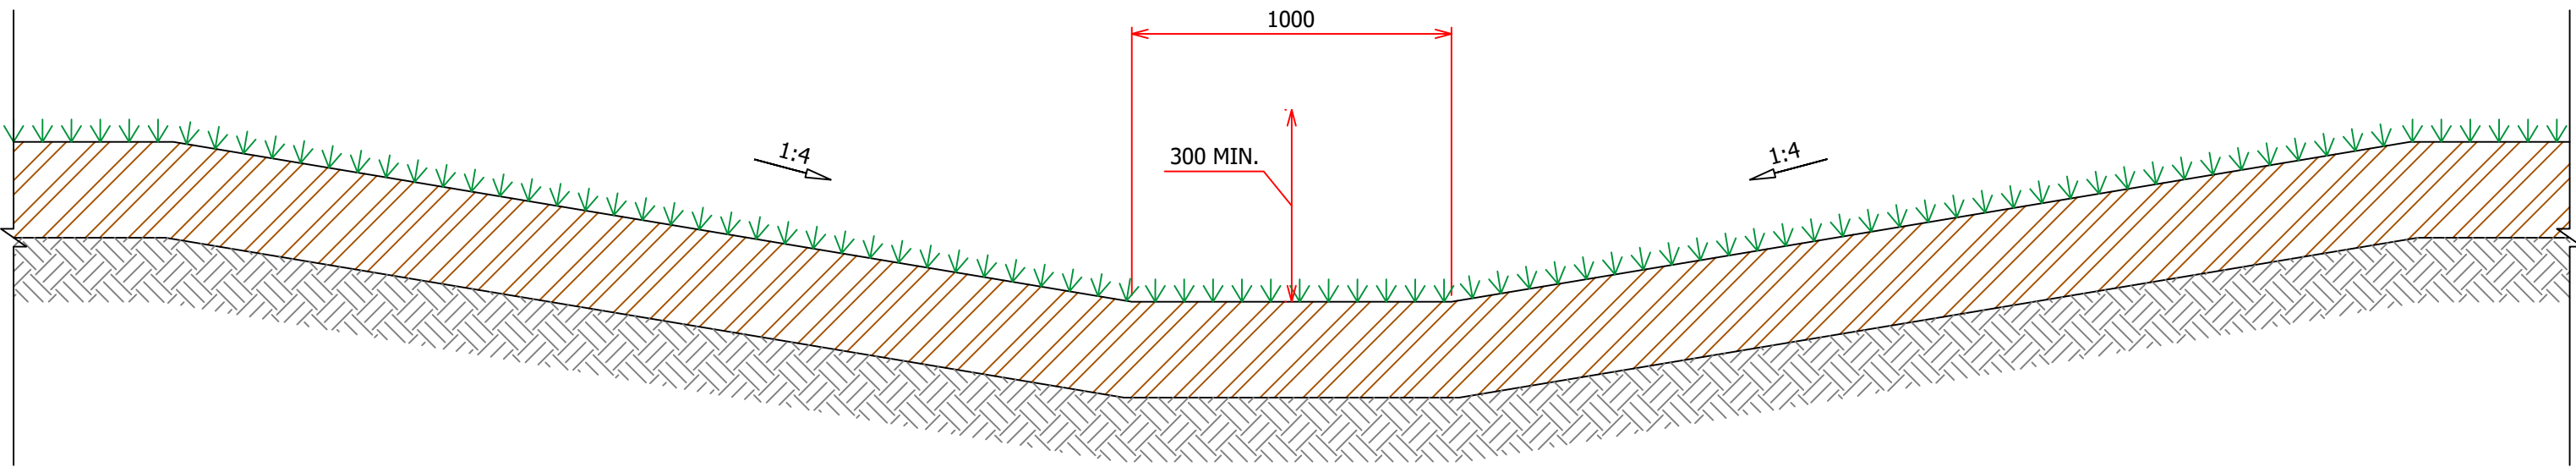

GRASSED SWALE TYPICAL DETAIL
N.T.S

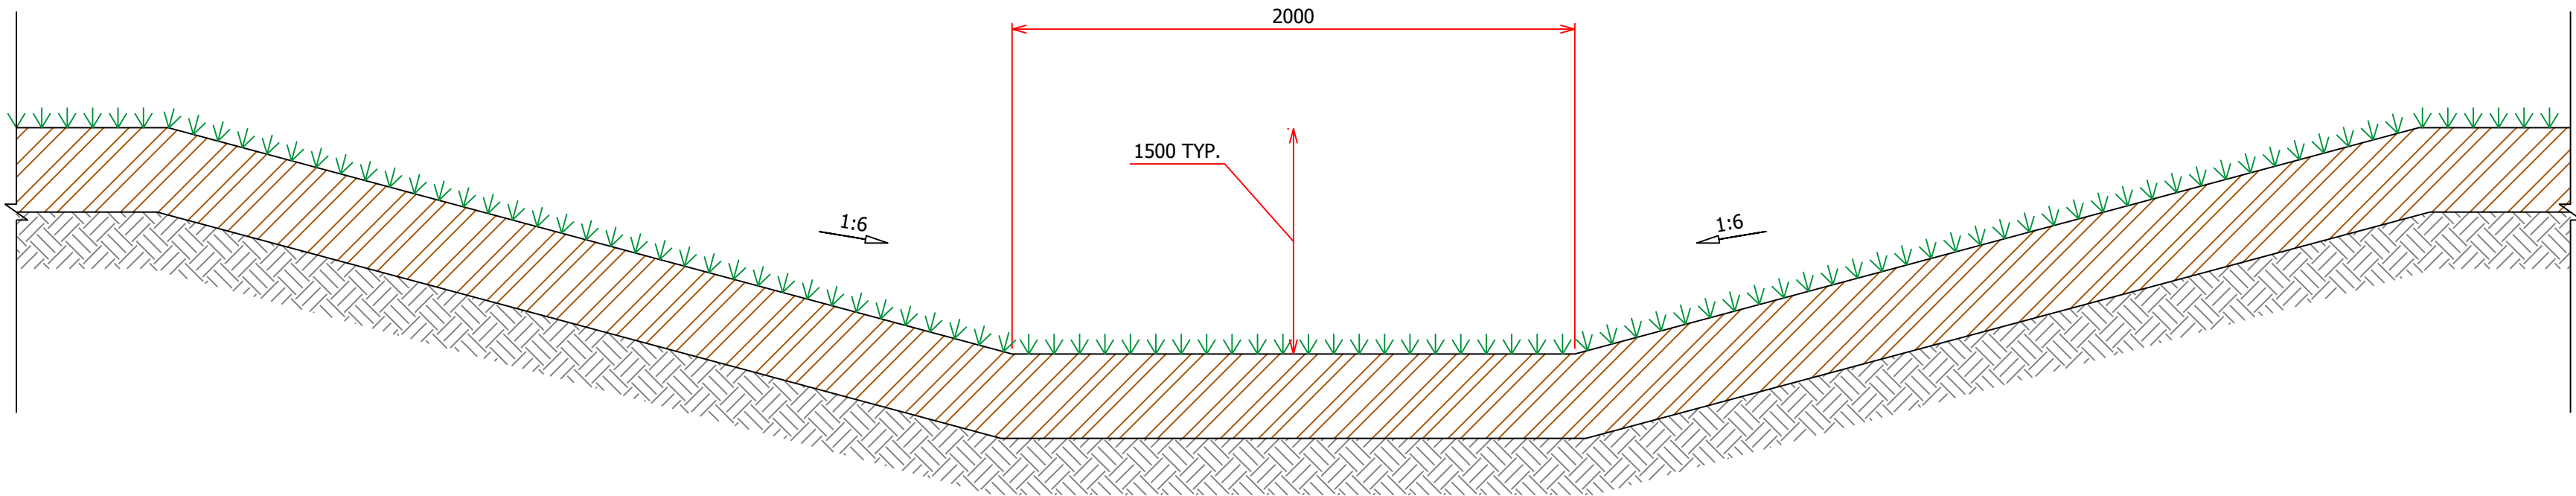

VEGETATED SWALE TYPICAL DETAIL
N.T.S

NOT FOR CONSTRUCTION



SPORTENG™

T1	17/06/26	TPC	JZV	JDH	ISSUE FOR TENDER
Issue	Date	By	Chkd	Appd	Description

Job Title
ROCKHAMPTON
NETBALL CENTRE

Drawing Title
STORMWATER DRAINAGE
DETAILS
SHEET 3

Discipline
CIVIL AND FIELD OF PLAY
Drawing Status
ISSUE FOR TENDER
Drawing Number
SE_12306_F1322

Issue
T1