



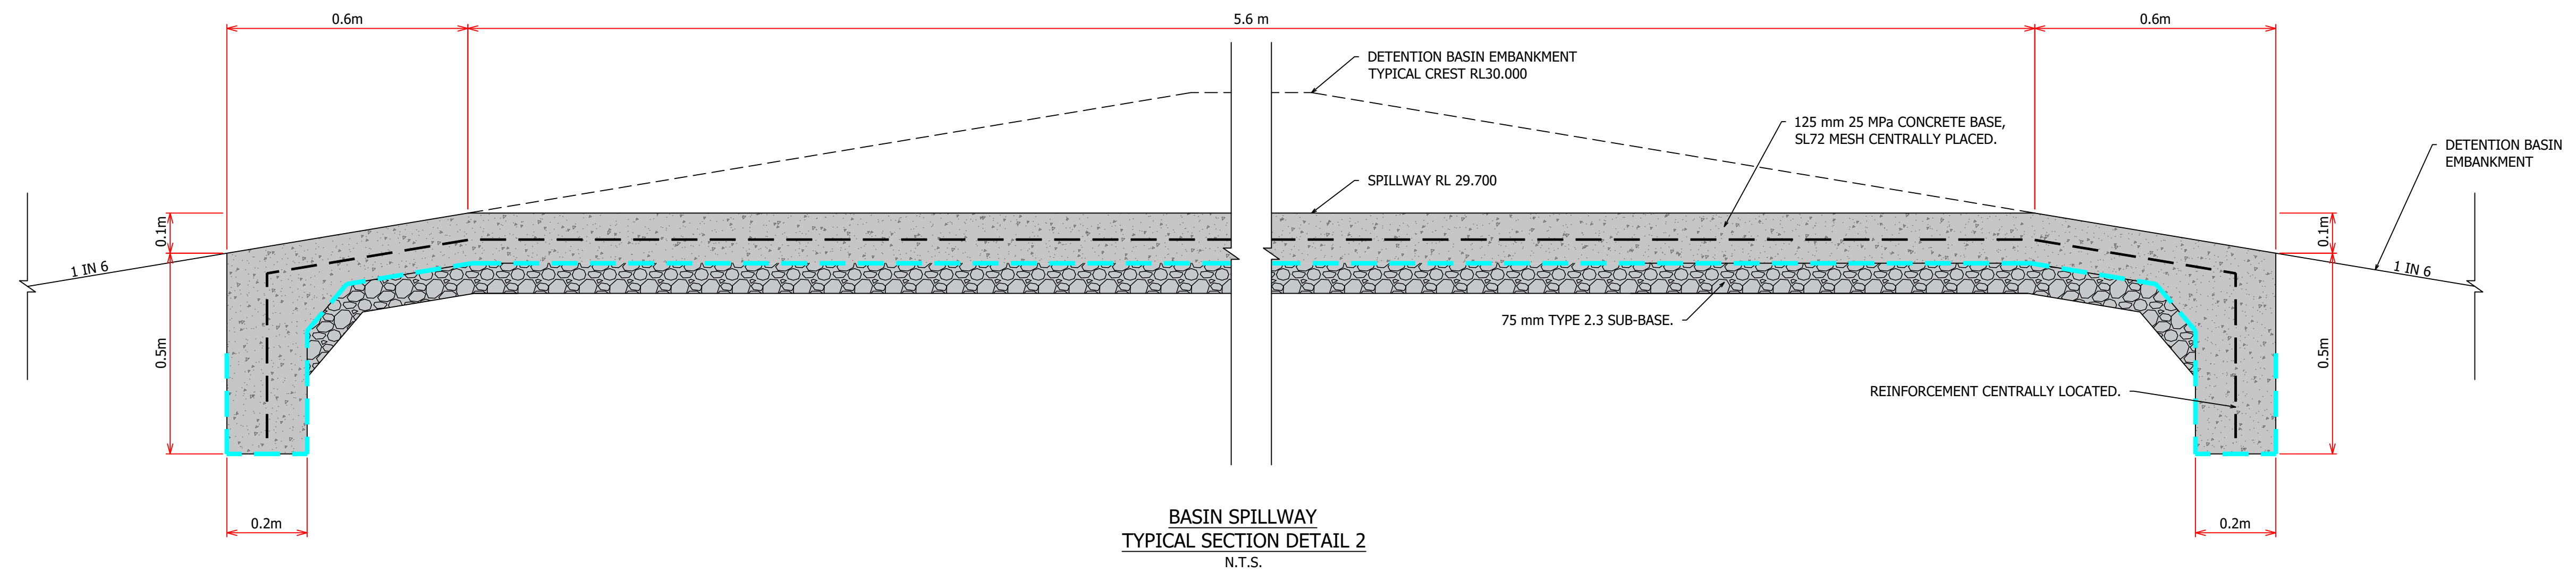

NOT FOR CONSTRUCTION

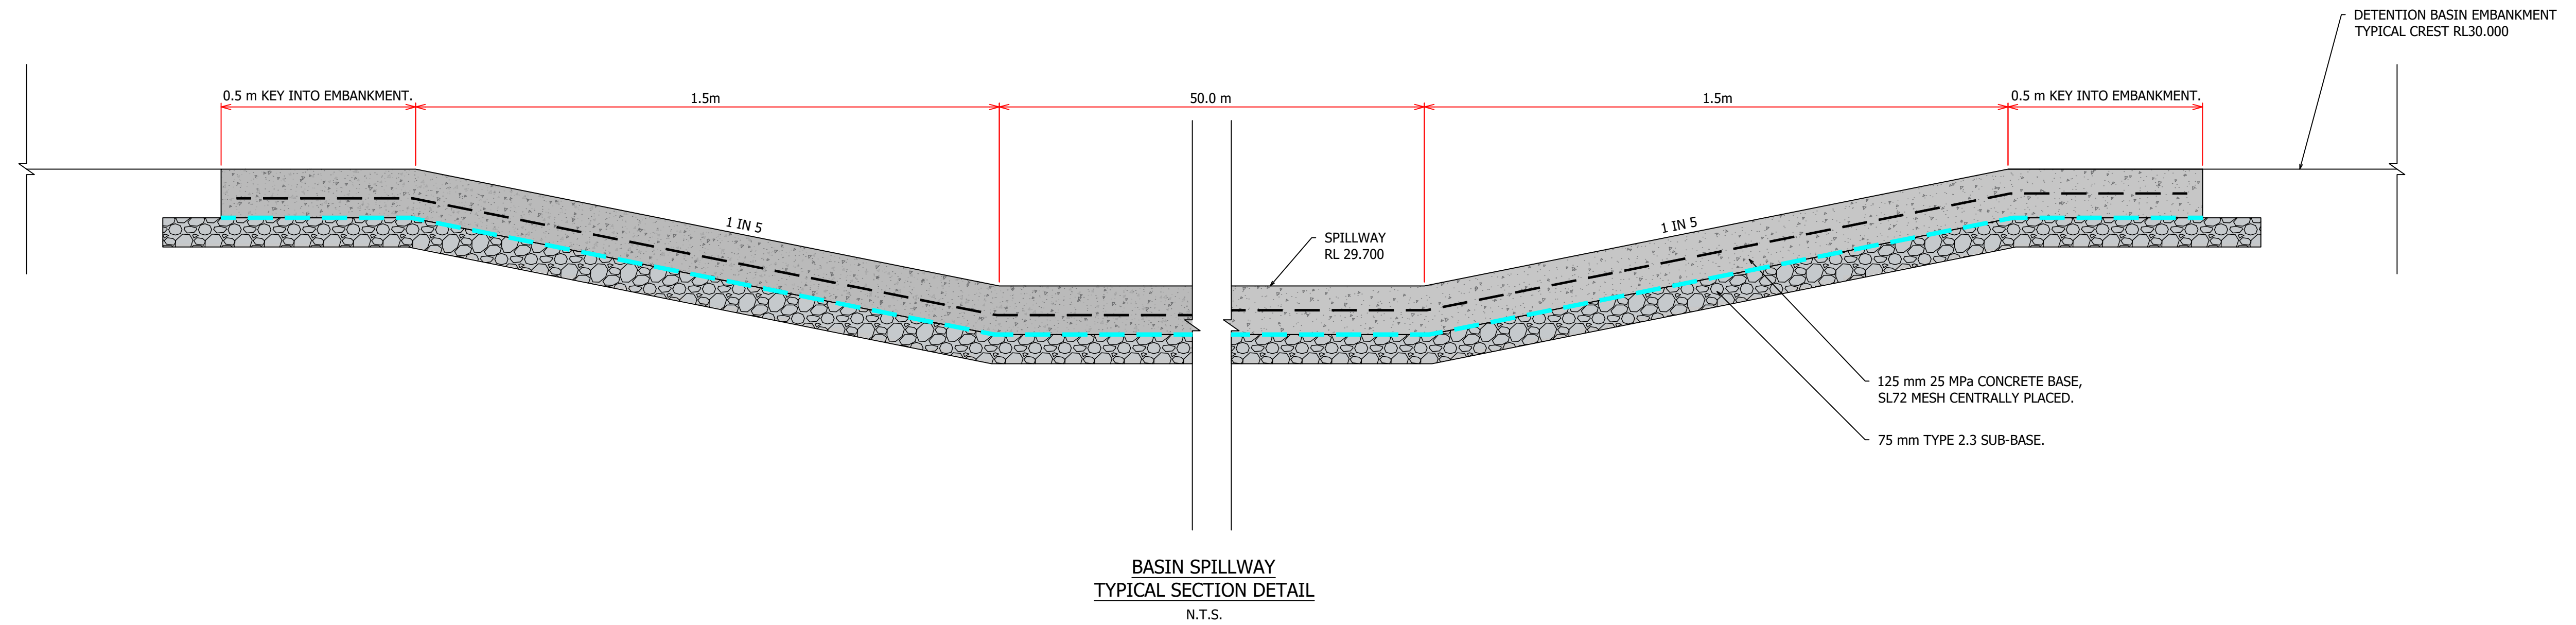

SPORTENG™

T1	17/06/26	TPC	JZV	JDH	ISSUE FOR TENDER
Issue	Date	By	Chkd	Appd	Description

Job Title
ROCKHAMPTON
NETBALL CENTRE

Drawing Title
STORMWATER DRAINAGE
DETAILS
SHEET 4

Discipline
CIVIL AND FIELD OF PLAY

Drawing Status
ISSUE FOR TENDER

Drawing Number
SE_12306_F1323

Issue
T1