


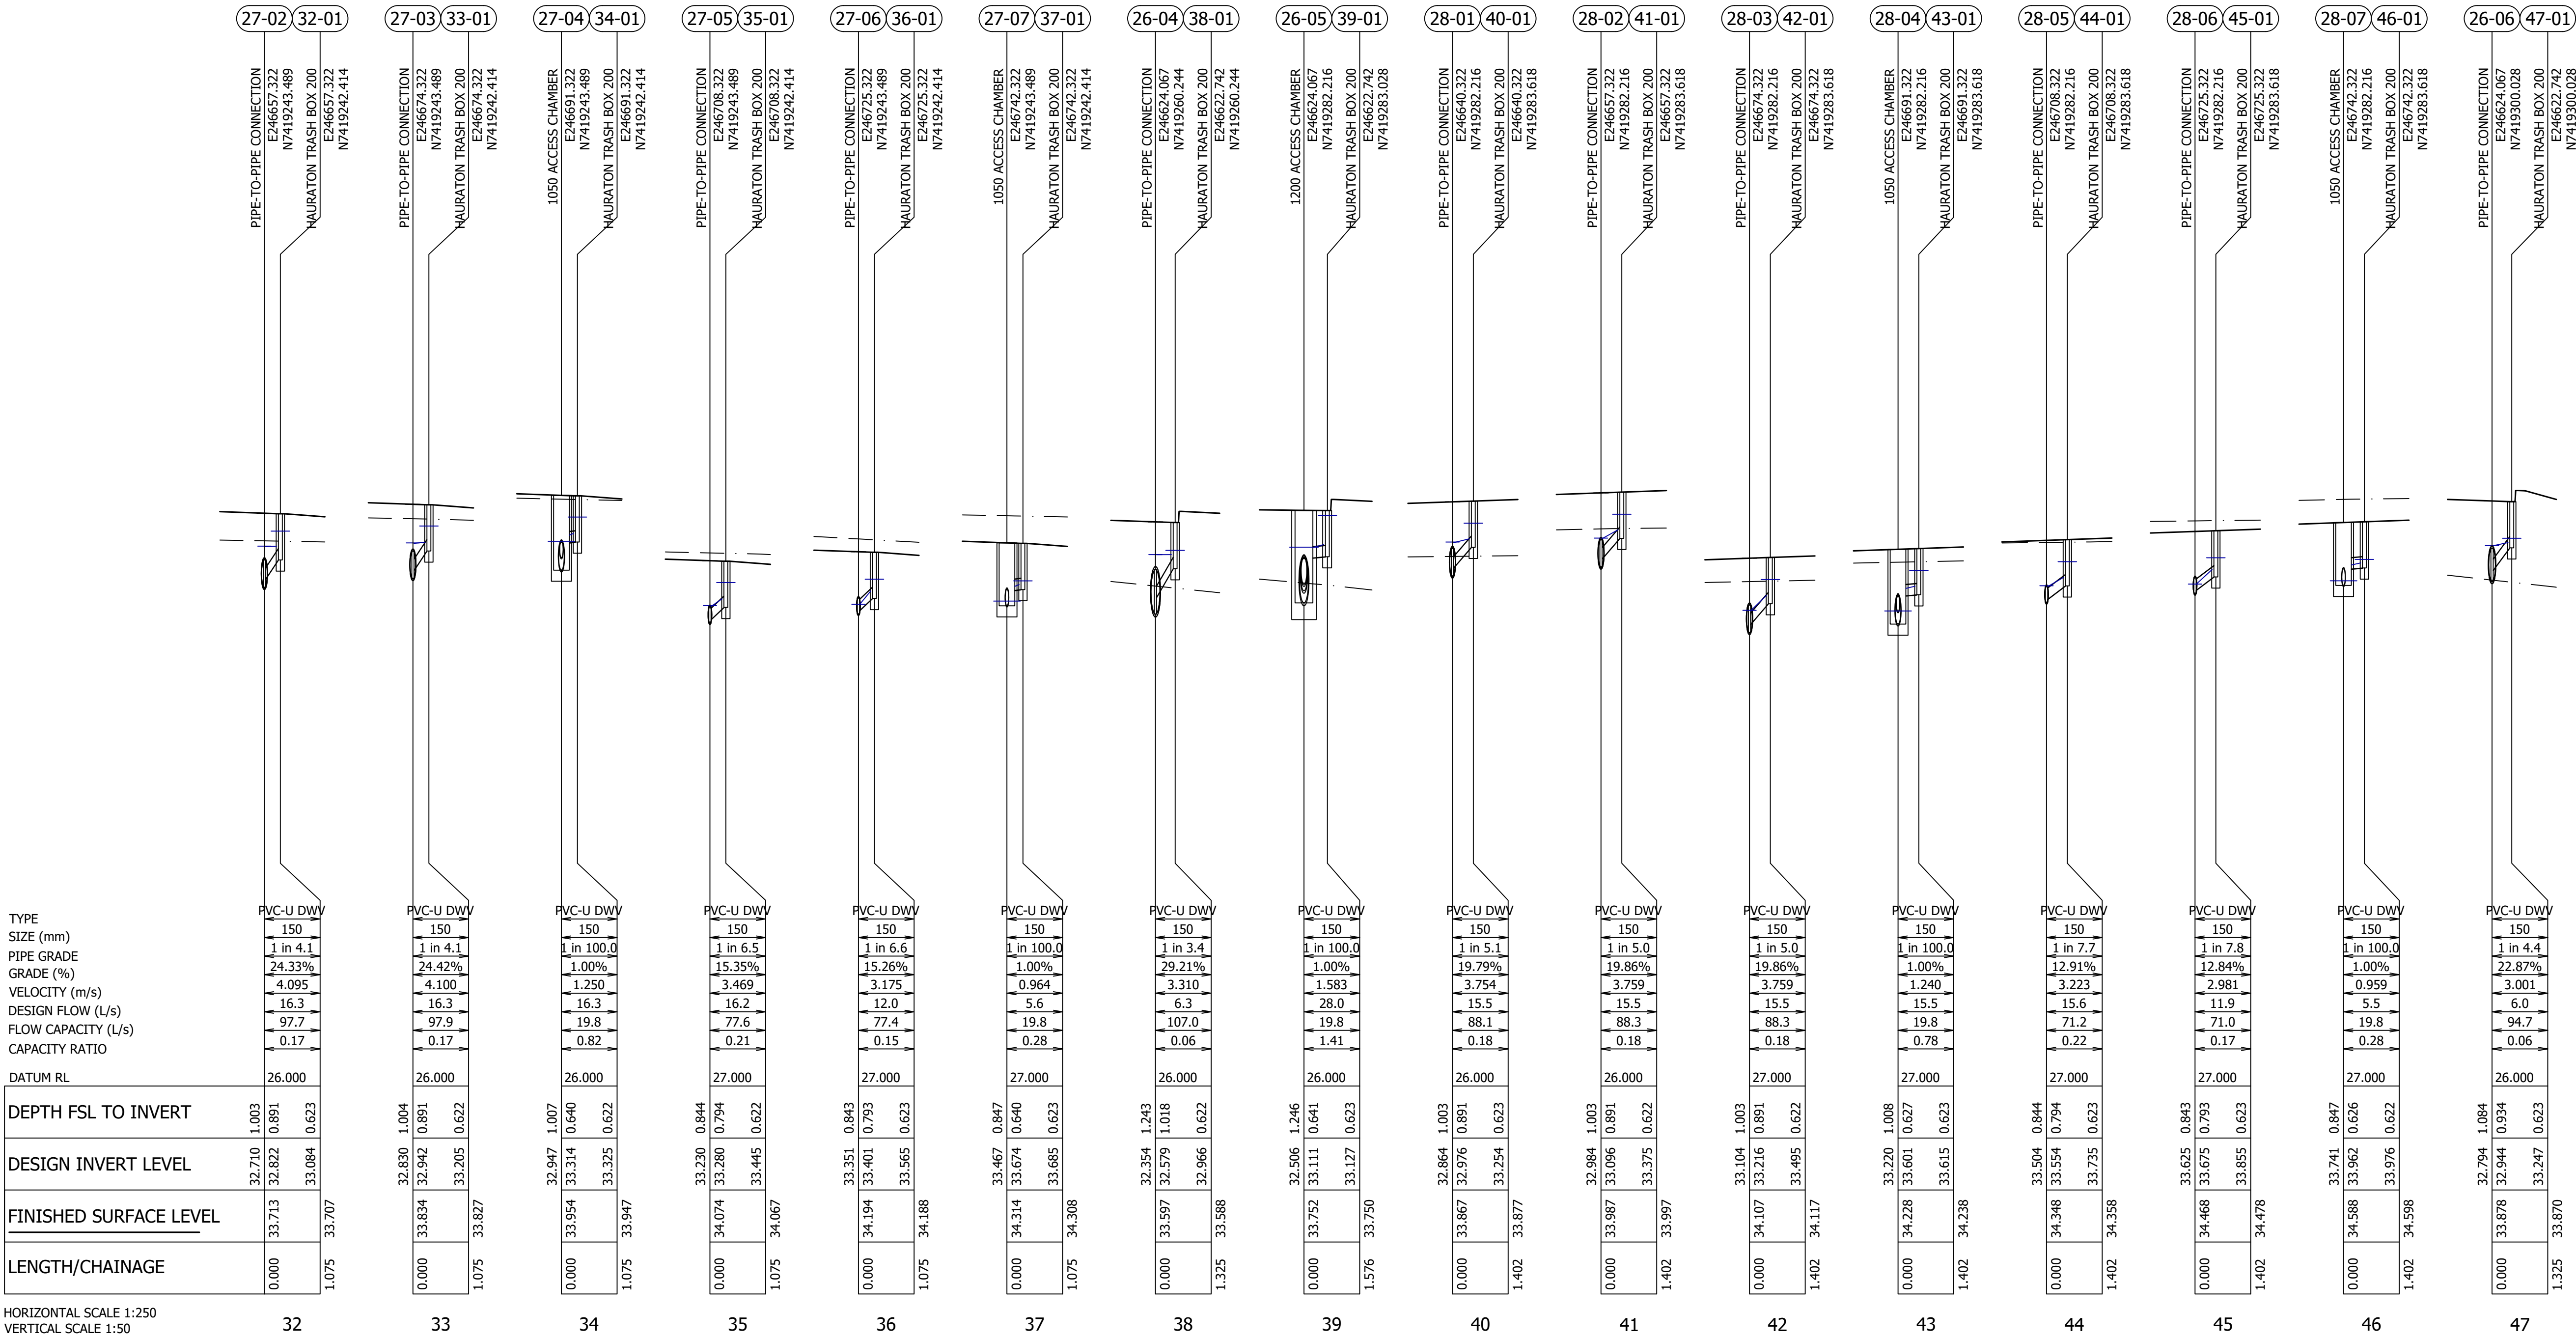

NOT FOR CONSTRUCTION



SPORTENG™

T1 17/06/26 TPC JZV JDH ISSUE FOR TENDER
Issue Date By Chkd Appd Description

Job Title
ROCKHAMPTON
NETBALL CENTRE

Drawing Title
STORMWATER DRAINAGE
LONG SECTIONS
SHEET 10

Discipline
CIVIL AND FIELD OF PLAY
Drawing Status
ISSUE FOR TENDER
Drawing Number
SE_12306_F1359

Issue
T1