


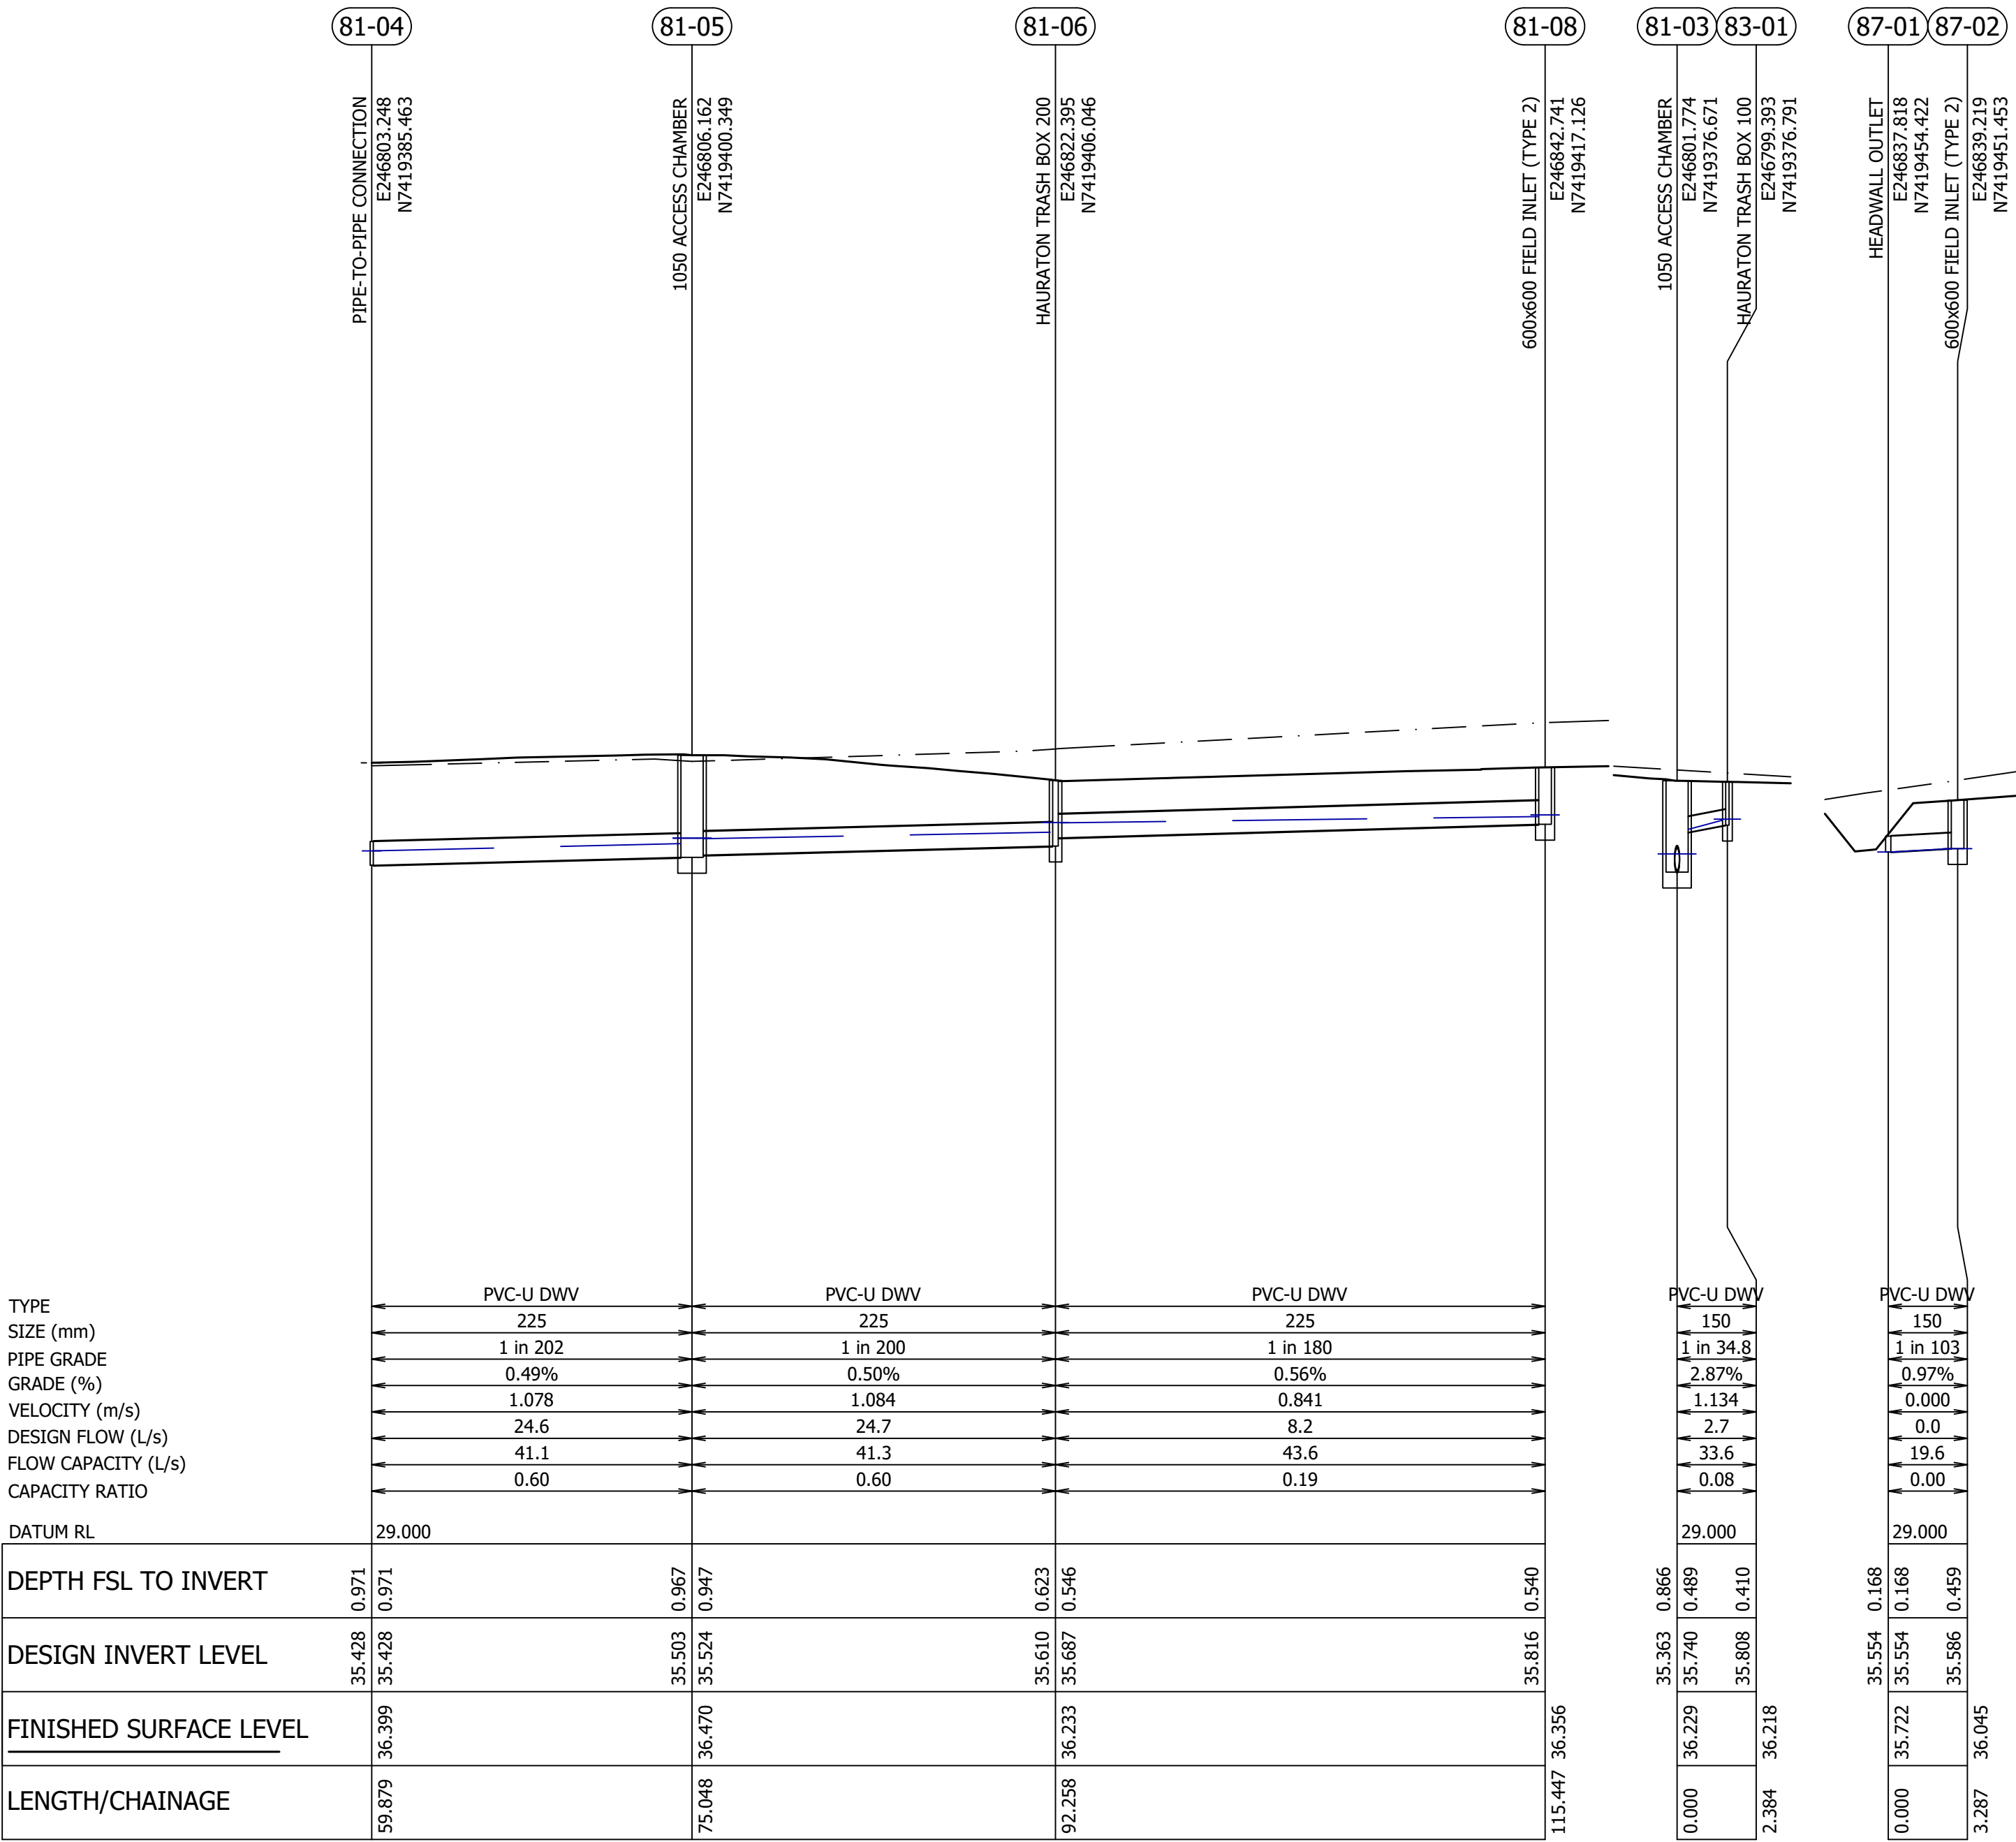

HORIZONTAL SCALE 1:250
VERTICAL SCALE 1:50

81

83

87

NOT FOR CONSTRUCTION



T1	17/06/26	TPC	JZV	JDH	ISSUE FOR TENDER
Issue	Date	By	Chkd	Appd	Description

Job Title
ROCKHAMPTON
NETBALL CENTRE

Drawing Title
STORMWATER DRAINAGE
LONG SECTIONS
SHEET 12

Discipline
CIVIL AND FIELD OF PLAY
Drawing Status
ISSUE FOR TENDER
Drawing Number
SE_12306_F1361

Issue
T1