


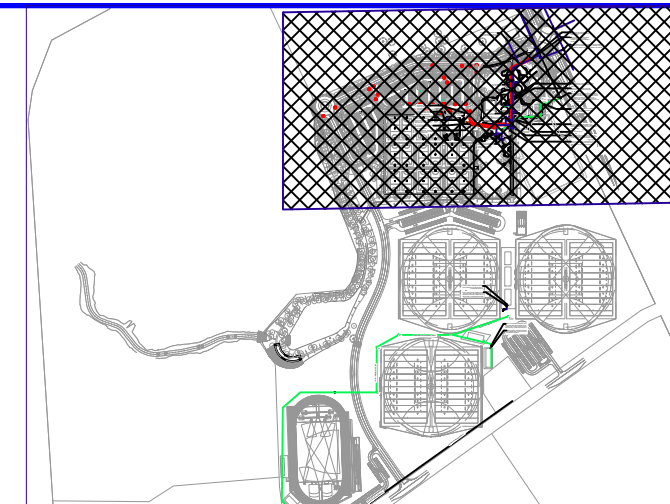

N

WATER TO CONNECT UP TO NEW HOUSES ESTATE TO THE NORTH OF THE SITE AT A FUTURE POINT

Ø200 COLD WATER COMPLETE WITH ISOLATING VALVE CAPPED FOR FUTURE CONNECTION TO MAINTENANCE BUILDING.

EXISTING AUTHORITY Ø80 MPVC COLD WATER

EXISTING AUTHORITY Ø250 MPVC COLD WATER

4m x 2m SLAB FOR WATER METERS COMPLETE WITH BOLLARDS TO PROTECT METER ASSEMBLY

PROPOSED Ø100mm FIRE WATER METER ASSEMBLY AND Ø100 COLD WATER ASSEMBLY AUTHORITY'S REQUIREMENTS AND APPROVAL

PROPOSED Ø200mm COLD WATER TAPPING FOR FIRE AND GENERAL TO AUTHORITY'S WATER MAIN LOCATED EAST OF NORMAN ROAD TO ROCKHAMPTON REGIONAL COUNCIL REQUIREMENTS AND APPROVAL

SL. 36.490
IL. 34.805

Ø100 FS INGROUND
Ø100 CW INGROUND

Ø100 S @ 1:60
REFER TO DRAWING H300 FOR THE TRENCH DETAIL

Ø100 SEWER RAISING MAIN

MH-1
RL. 37.800
IL. 35.716

NEW Ø150 UPVC SEWER @ 1:100 FALL

IL. 35.433

PROPOSED SEWER RAISING MAIN TO BE CONNECTED TO SITE SEWER RETICULATION LOCATION TO BE CONFIRMED AND COORDINATED

PROPOSED SEWER PUMP AND CHAMBER (PIT) IN GROUND. QMAX FORTIS 3200 PUMPPWELL OR EQUALLY APPROVED. REFER TO DETAILS QCPS32V/A01 & A02 FOR FURTHER DETAILS.

R.L. TO BE SET AS THE F.S.L.

Ø100mm COLD WATER COMPLETE WITH ISOLATING AND CHECK METER VALVE CAPPED FOR FUTURE CONNECTION TO HIGH PERFORMANCE CENTER BUILDING AMENITIES

Ø100mm COLD WATER POINT FOR IRRIGATION TO TAKE OFF FROM. ISOLATION VALVE AND CHECK VALVE COMPLETE WITH E TYPE FLANGE CAPPED ABOVE GROUND.

FOR CONTINUATIONLN REFER TO DRAWING H004

ALL DIMENSIONS SHOWN IN MM! DO NOT SCALE FROM DRAWINGS. DIMENSIONS TAKE PRECEDENCE. IF IN DOUBT, REFER TO HK SOLUTIONS.

SCALE 1:500 @A1

TENDER ISSUE

FOR CONTINUATION LN REFER TO DRAWING H004

TENDER ISSUE

T1		ISSUE FOR TENDER		17.06.2026	MC	HKS	H K Solutions ENGINEERING PROJECT MANAGEMENT DARWIN. GEELONG. CAIRNS. TOWNSVILLE. PERTH. BALLARAT admin@hksolutions.com.au www.hksolutions.com.au															
REV.	DESCRIPTION			DATE	INIT.	COMPANY	Conditions of use. This document may only be used by Harris Kmon Solutions clients for the purpose for which it was prepared and must not be used by any other person or for any other purpose.															
REVISIONS																						

DRAWN		MC	CITY OF ROCKHAMPTON					
CHECKED		AB	ROCKHAMPTON SPORTS PRECINCT					
DESIGNED		MC	554-700 YAAMBA ROAD NORMAN GARDENS					
CHECKED		AB						
APPROVED			HYDRAULIC SERVICE					
Date Approved			STAGE 1 SITE RETICULATION					
THIS DRAWING MUST NOT BE USED FOR CONSTRUCTION UNLESS SIGNED AS APPROVED			PAGE No	PROJECT No	DRAWING No	DISCIPLINE	REV.	SHEET SIZE
			3 OF 4	25015 - H003		HYDRAULIC	T1	A1