

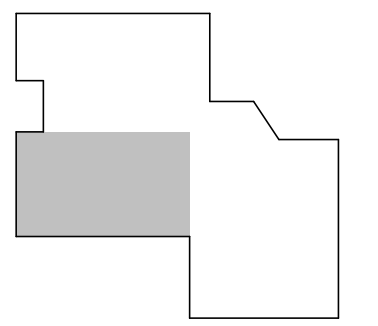


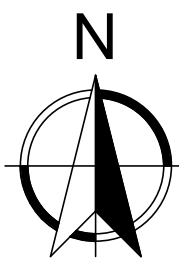

KEYPLAN

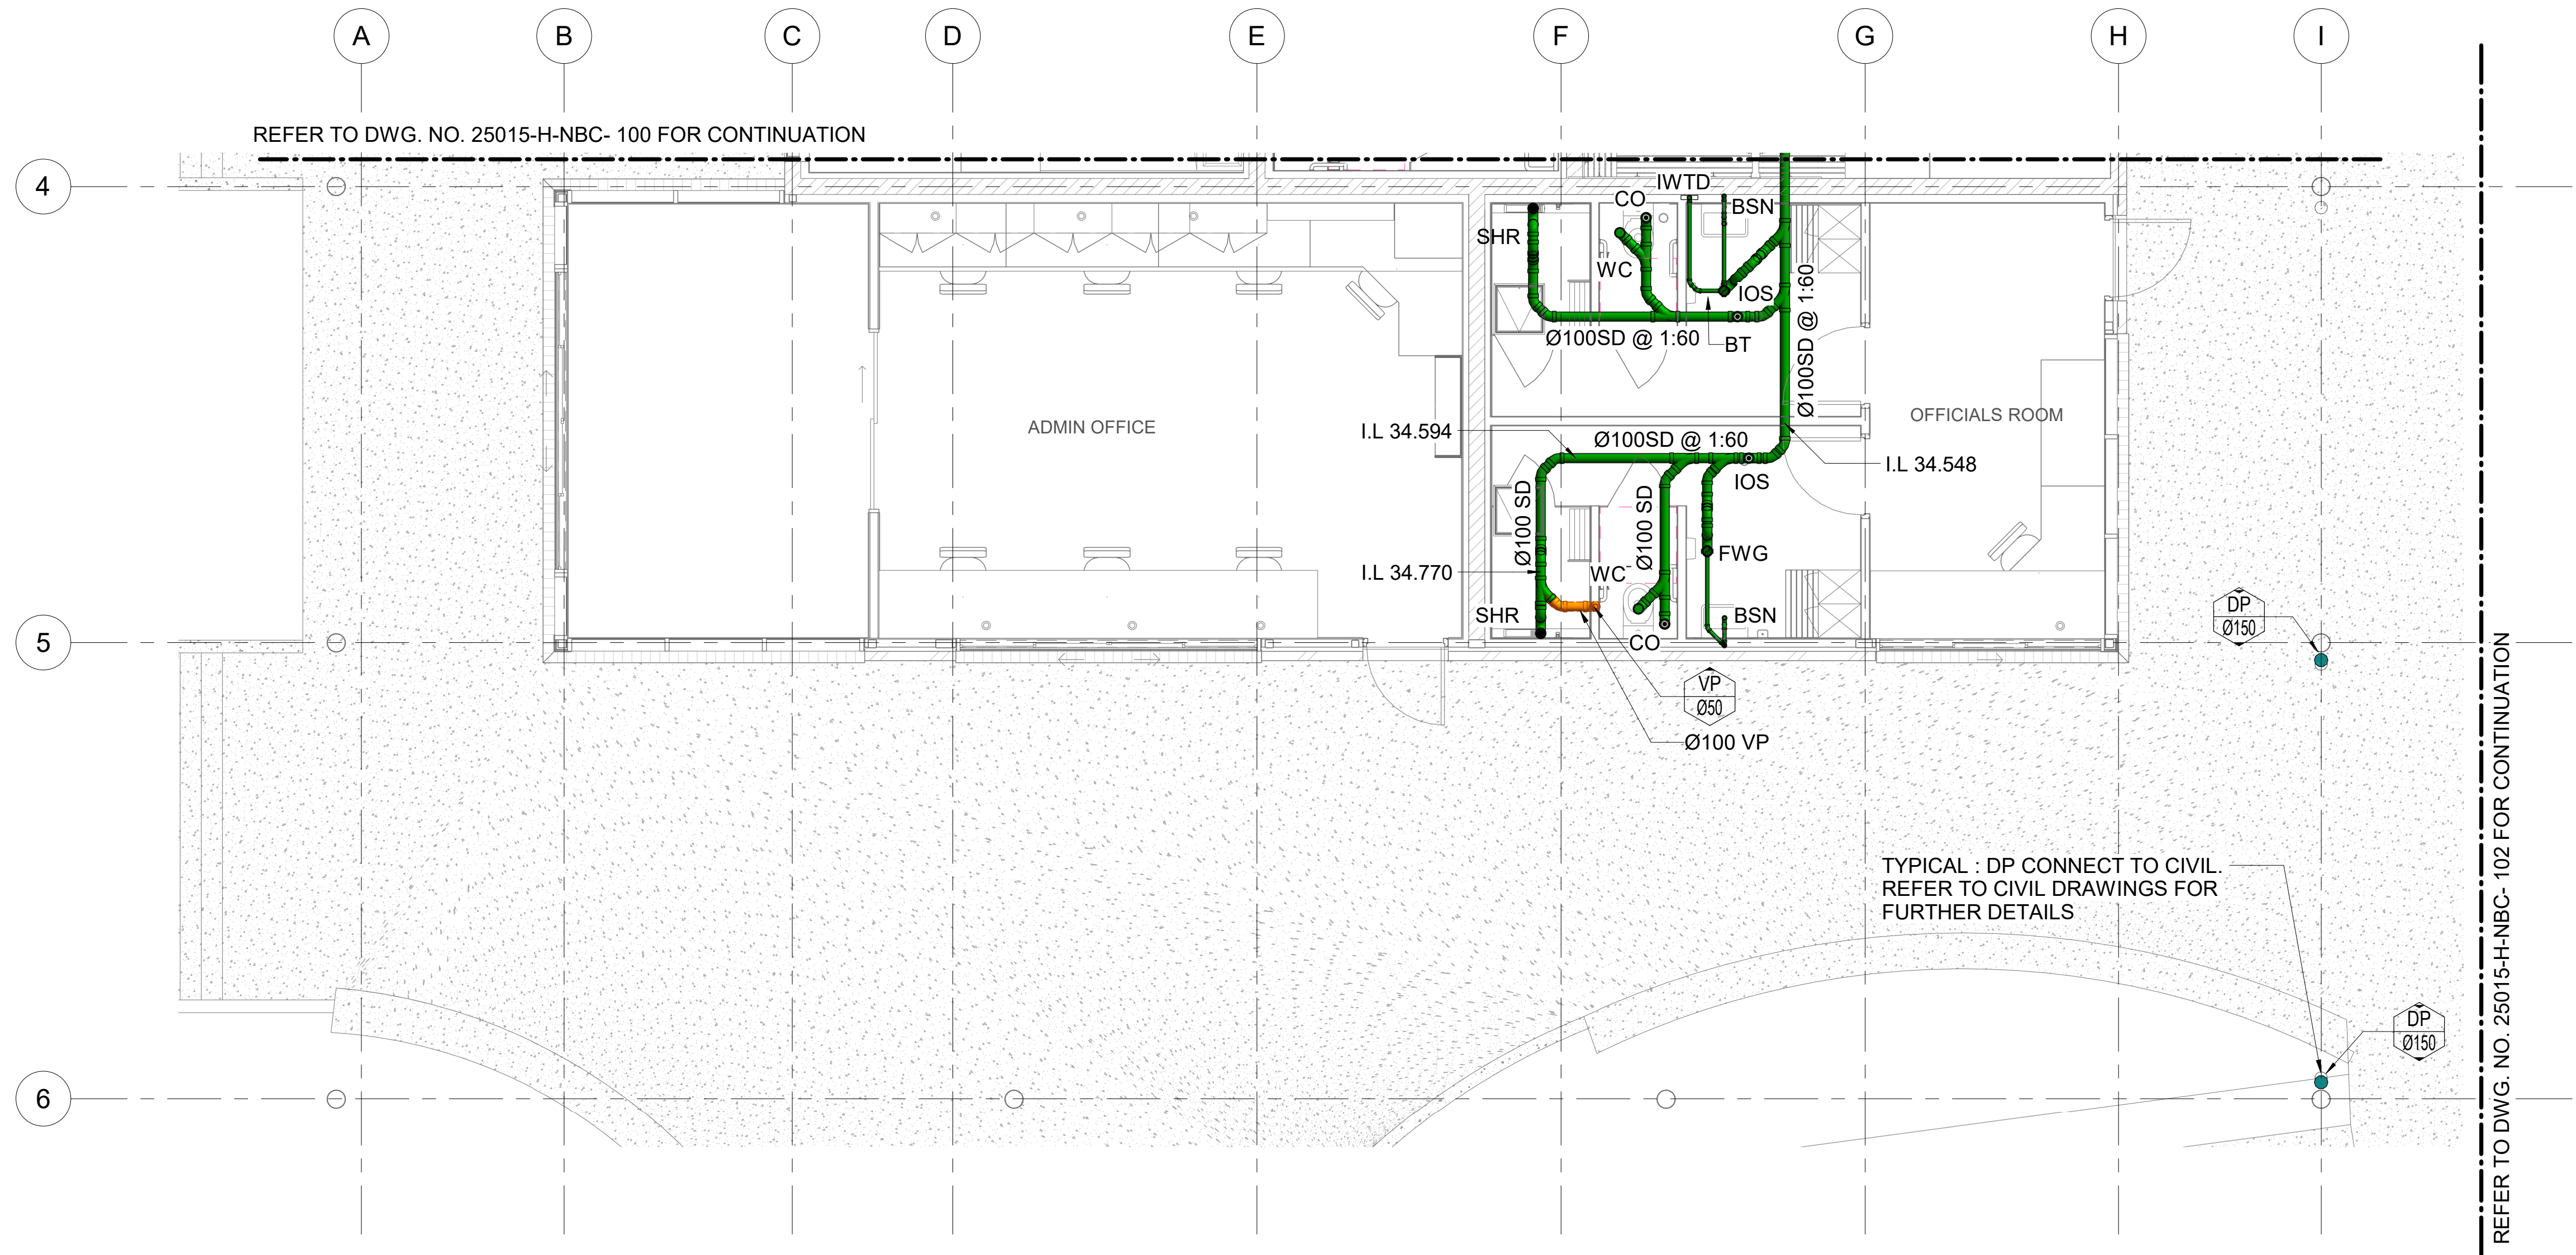

GROUND FLOOR SANITARY PLUMBING LAYOUT - PART 2
1 : 50

0 1 1 2 2 3 3 4 4 5 5m
SCALE 1:50 AT A1 SHEET | 1:100 AT A3 SHEET

ALL DIMENSIONS SHOWN IN MM. DO NOT SCALE FROM DRAWINGS.
DIMENSIONS TAKE PRECEDENCE. IF IN DOUBT REFER TO HK SOLUTIONS.

FOR TENDER

						 ENGINEERING PROJECT MANAGEMENT DARWIN, GEELONG, CAIRNS, TOWNSVILLE PERTH, BALLARAT admin@hksolutions.com.au www.hksolutions.com.au
T1	ISSUE FOR TENDER		17.06.2026	MC	HKS	Conditions of use. This document may only be used by Harris Kmon Solutions clients for the purpose for which it was prepared and must not be used by any other person or for any other purpose.
REV.	DESCRIPTION		DATE	INT.	COMPANY	
REVISIONS						

SPORTENG™

DRAWN	AL
CHECKED	MC
DESIGNED	MC
CHECKED	LM
APPROVED	

THIS DRAWING MUST
NOT BE USED FOR
CONSTRUCTION UNLESS
SIGNED AS APPROVED

STAGE 1 ROCKHAMPTON SPORTS PRECINCT - NETBALL CLUBHOUSE 554-700 YAAMBA ROAD, NORMAN GARDEN - 4701 GROUND FLOOR SANITARY PLUMBING LAYOUT - PART 2		PAGE No 05 of 10		PROJECT No - DRAWING No 25015-H-NBC-101		DISCIPLINE HYDRAULIC		REV. T1	SHEET SIZE A1
---	--	----------------------------	--	---	--	--------------------------------	--	-------------------	-------------------------

DRAWINGS TO BE PRINTED IN COLOUR