

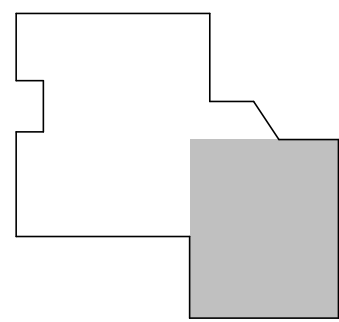


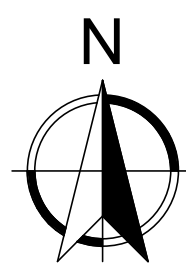


KEYPLAN

DRAWING NOTES:

1. ALL HOSE TAPS EXCEPT FOR GIT TAP WILL HAVE A VERTICAL BREAK OR SINGLE CHECK VALVE INSTALLED.
2. DRAIN GRADE SHOULD BE 1:40 FOR THE FIRST 800mm EXTERNAL TO THE SLAB.
3. SWIVEL EXPANSION JOINTS INSTALLED ON GRADE SHOULD BE USED TO CORRECT PIPE MISALIGNMENT.
4. SWIVEL EXPANSION JOINTS AND EXPANSION JOINTS SHOULD BE INSTALLED AT 50% OF THEIR TELESCOPIC MOVEMENT.
5. EXPANSION JOINTS INSTALLED ON VERTICAL RISERS SHOULD HAVE A MINIMUM OF 40mm TELESCOPIC MOVEMENT.

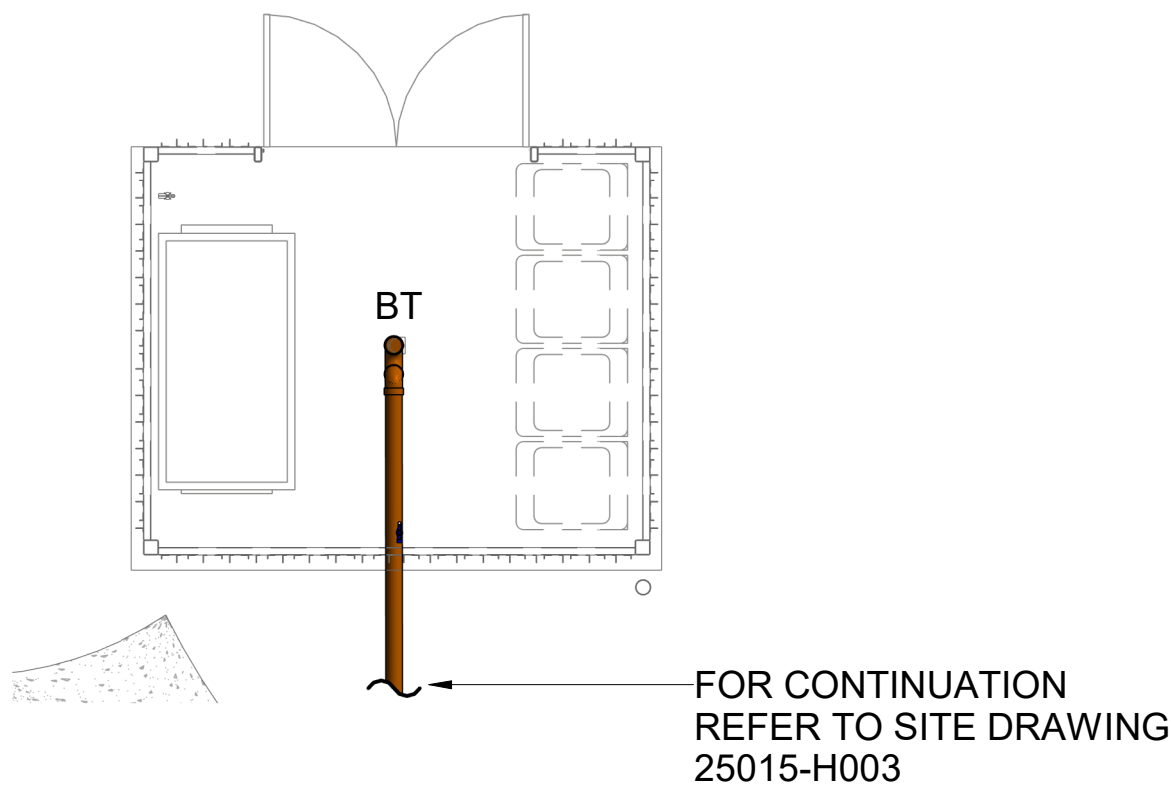

NBC BINWASH SANITARY LAYOUT
1 : 50

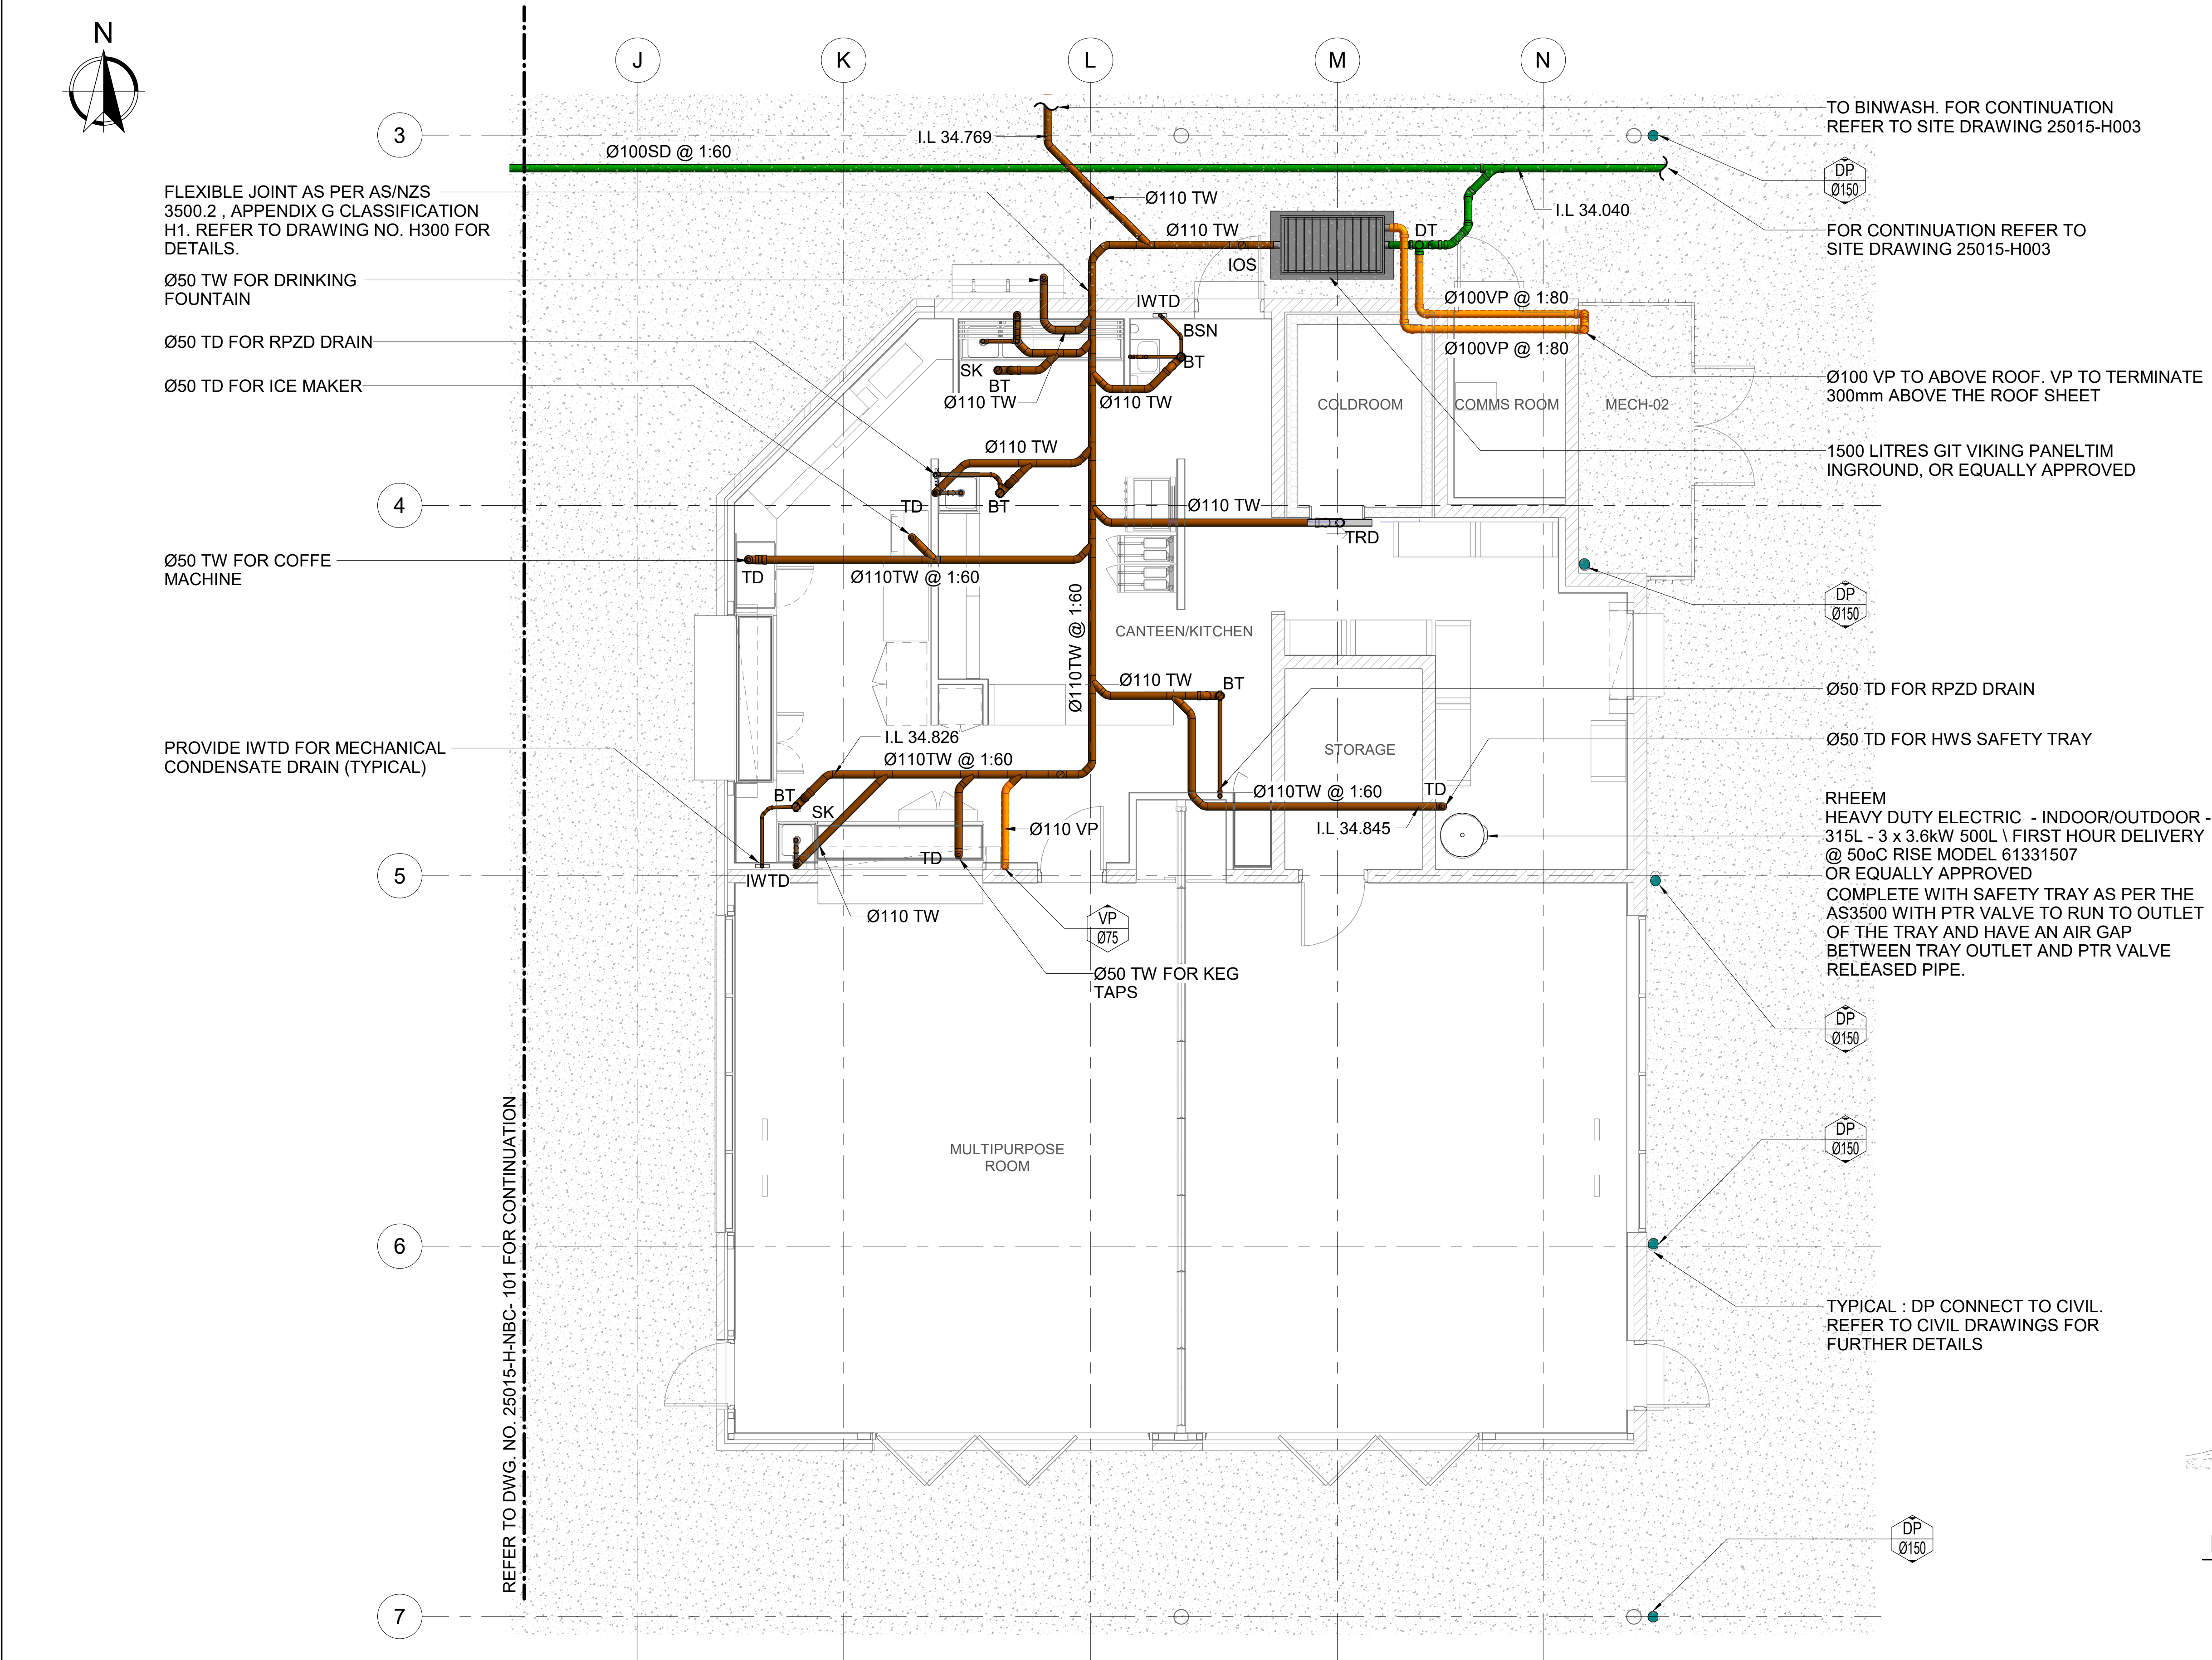

GROUND FLOOR SANITARY PLUMBING LAYOUT - PART PLAN 3
1 : 50

0 1 1 2 2 3 3 4 4 5 5m
SCALE 1:50 AT A1 SHEET | 1:100 AT A3 SHEET

ALL DIMENSIONS SHOWN IN MM. DO NOT SCALE FROM DRAWINGS.
DIMENSIONS TAKE PRECEDENCE. IF IN DOUBT REFER TO HK SOLUTIONS.

						 ENGINEERING PROJECT MANAGEMENT DARWIN.GEELONG. CAIRNS.TOWNSVILLE PERTH.BALLARAT admin@hksolutions.com.au www.hksolutions.com.au
T1	ISSUE FOR TENDER		17.06.2026	MC	HKS	Conditions of use. This document may only be used by Harris Kmon Solutions clients for the purpose for which it was prepared and must not be used by any other person or for any other purpose.
REV.	DESCRIPTION		DATE	INT.	COMPANY	
REVISIONS						

HK
Solutions
ENGINEERING
PROJECT MANAGEMENT
DARWIN, GEELONG,
CAIRNS, TOWNSVILLE,
PERTH, BALLARAT
admin@hksolutions.com.au
www.hksolutions.com.au

SPORTENG™

DRAWN	AL
CHECKED	MC
DESIGNED	MC
CHECKED	LM
APPROVED	

THIS DRAWING MUST
NOT BE USED FOR
CONSTRUCTION UNLESS
SIGNED AS APPROVED

STAGE 1
ROCKHAMPTON SPORTS PRECINCT - NETBALL CLUBHOUSE
554-700 YAAMBA ROAD, NORMAN GARDEN - 4701
GROUND FLOOR SANITARY PLUMBING LAYOUT - PART 3

PAGE No	PROJECT No - DRAWING No	DISCIPLINE	REV.	SHEET SIZE
06 of 10	25015-H-NBC-102	HYDRAULIC	T1	A1

FOR TENDER

DRAWINGS TO BE PRINTED IN COLOUR