
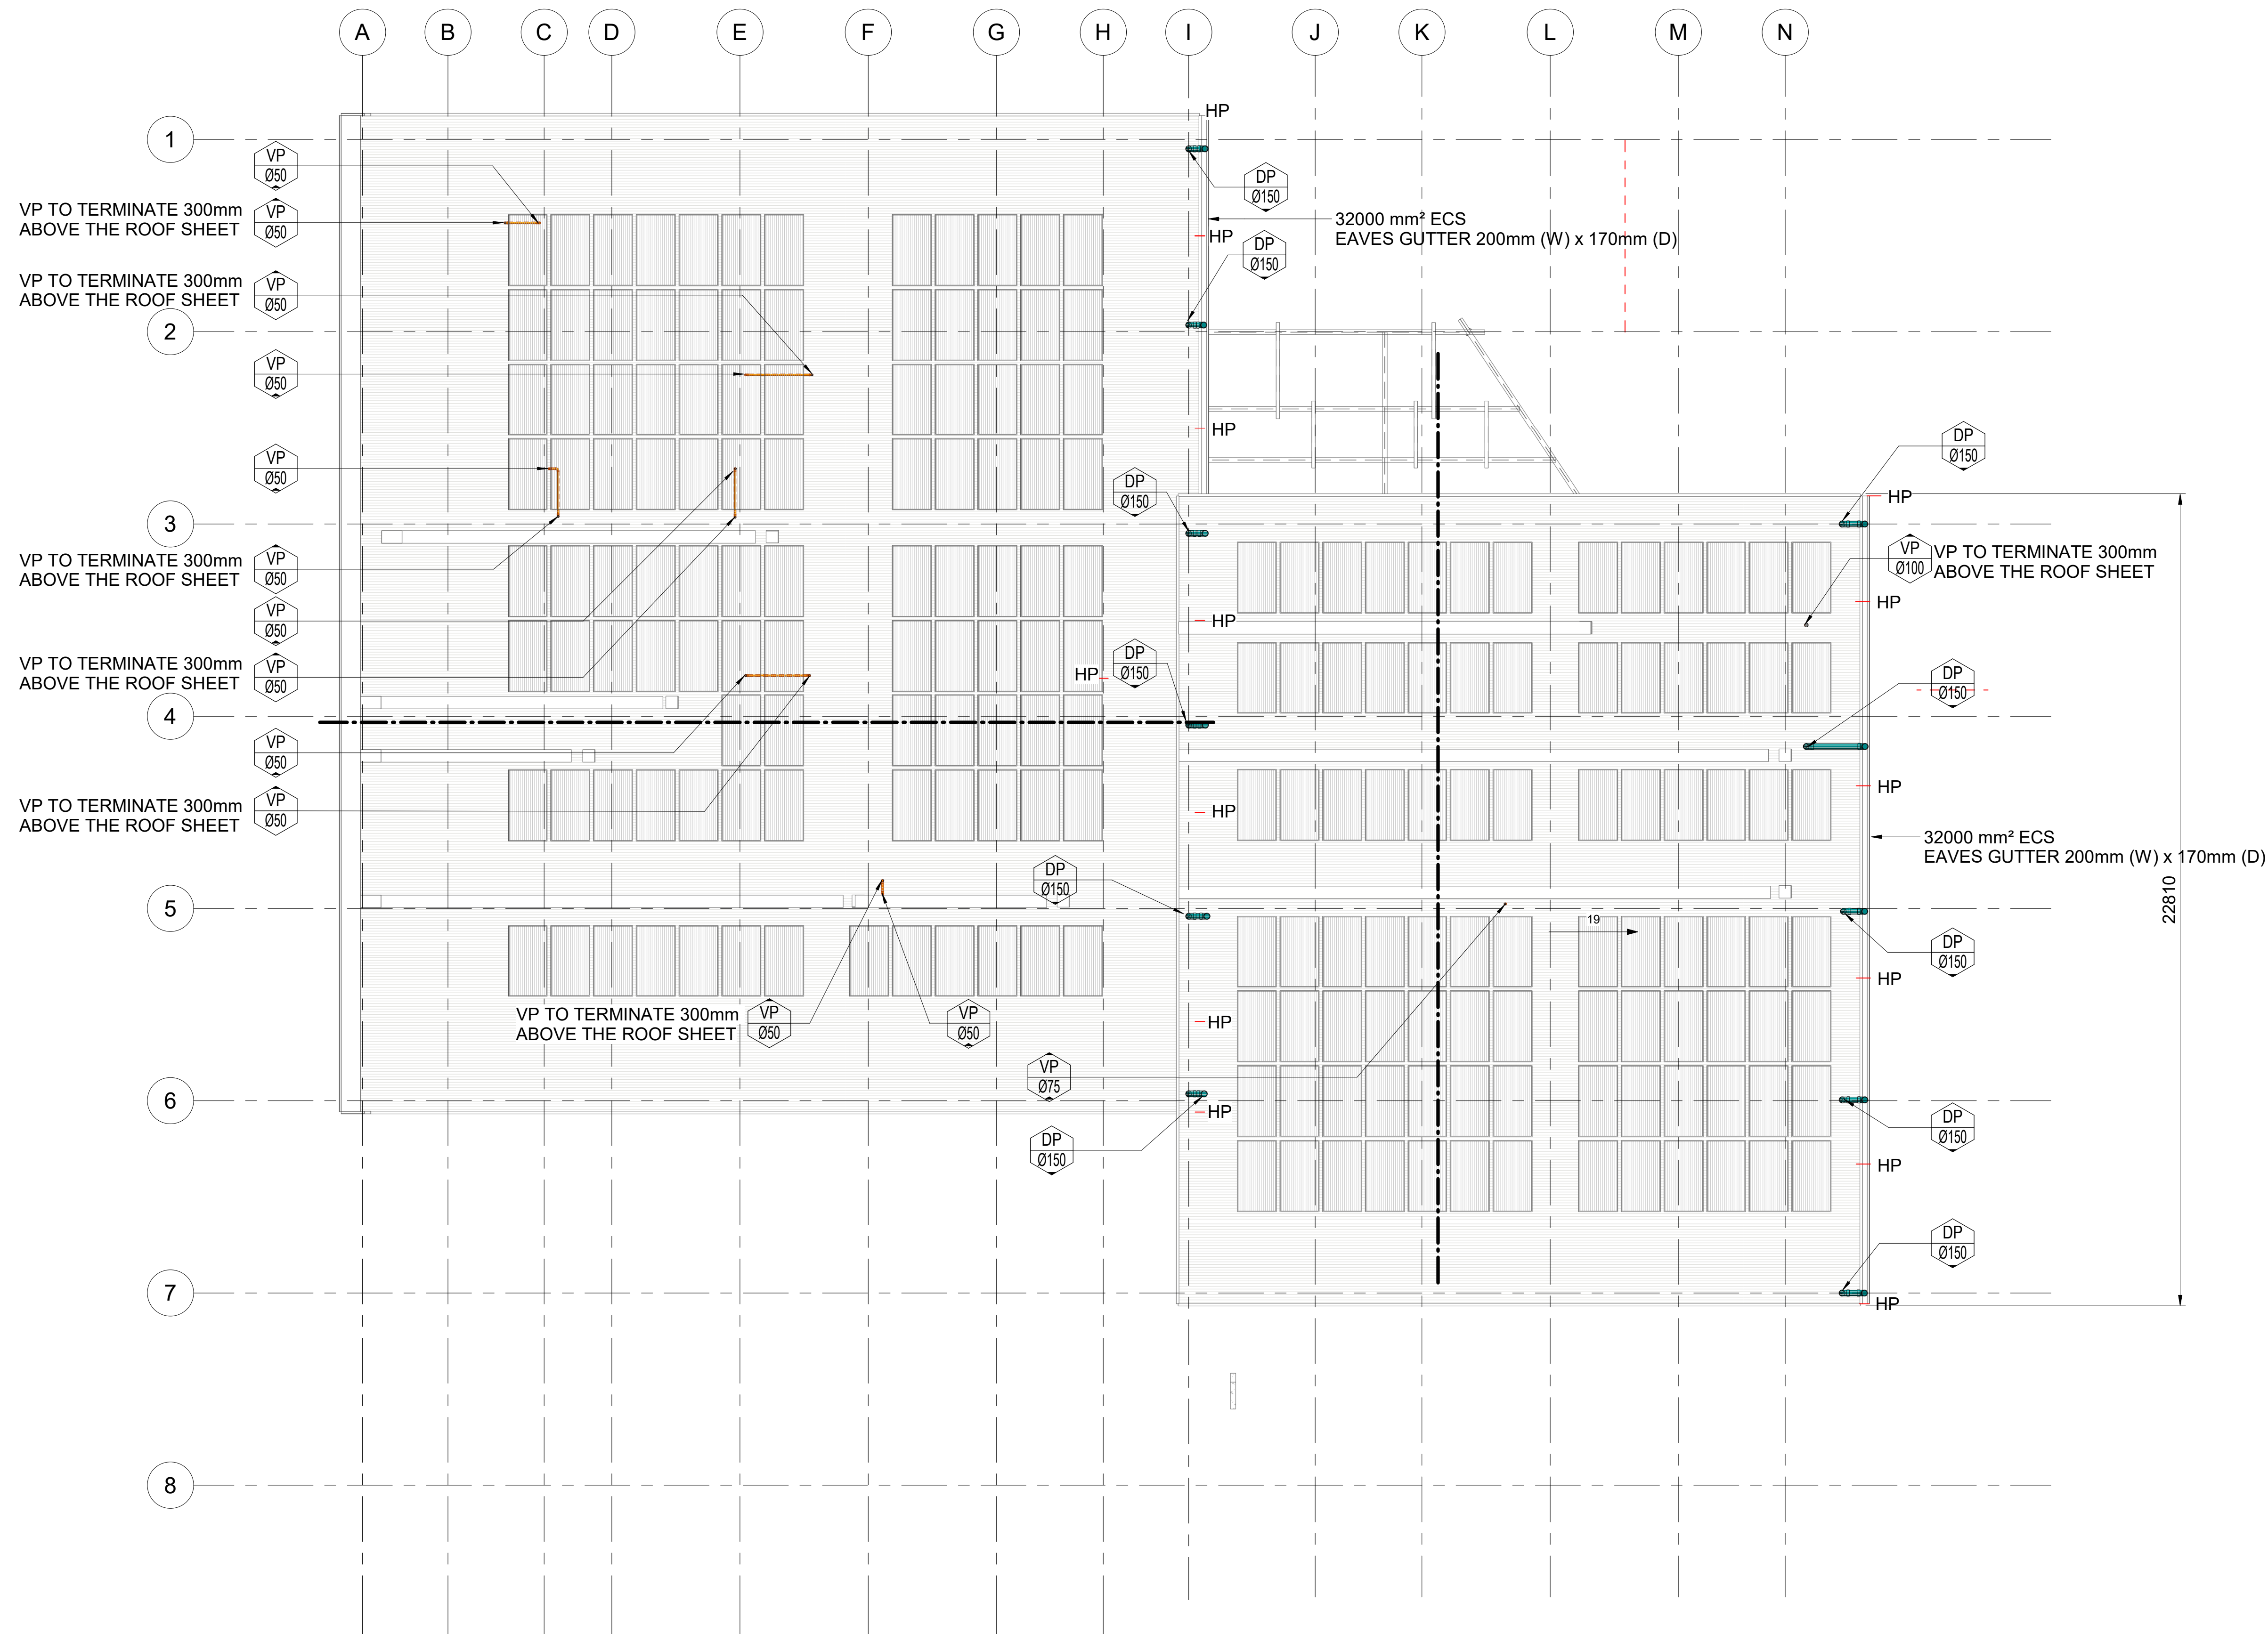


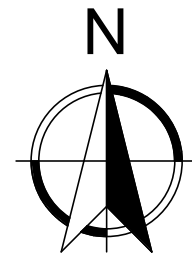

0 1 2 3 4 5 6 7 8 9 10m
SCALE 1:100 AT A1 SHEET | 1:200 AT A3 SHEET

ALL DIMENSIONS SHOWN IN MM. DO NOT SCALE FROM DRAWINGS.
DIMENSIONS TAKE PRECEDENCE. IF IN DOUBT REFER TO HK SOLUTIONS.

ROOF LEVEL STORM WATER LAYOUT
SCALE 1 : 100

FOR TENDER

T1	ISSUE FOR TENDER	17.06.2026	MC	HKS	 ENGINEERING PROJECT MANAGEMENT DARWIN, GEELONG, CAIRNS, TOWNSVILLE, PERTH, BALLARAT admin@hksolutions.com.au www.hksolutions.com.au
	REVISIONS				



DRAWN	AL
CHECKED	MC
DESIGNED	MC
CHECKED	LM
APPROVED	
THIS DRAWING MUST NOT BE USED FOR CONSTRUCTION UNLESS SIGNED AS APPROVED	

STAGE 1
ROCKHAMPTON SPORTS PRECINCT - NETBALL CLUBHOUSE
554-700 YAAMBA ROAD, NORMAN GARDEN - 4701
ROOF LEVEL STORM WATER LAYOUT

PAGE No	PROJECT No - DRAWING No	DISCIPLINE	REV.	SHEET SIZE
07 of 10	25015-H-NBC-103	HYDRAULIC	T1	A1

DRAWINGS TO BE PRINTED IN COLOUR