



DRAWING NOTES:

ALL HOSE TAPS EXCEPT FOR GIT TAP
WILL HAVE A VETICAL BREAK OR SINGLE
CHECK VALVE INSTALLED.

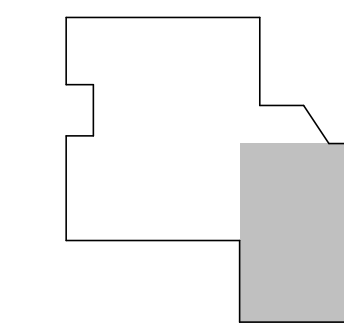

KEYPLAN

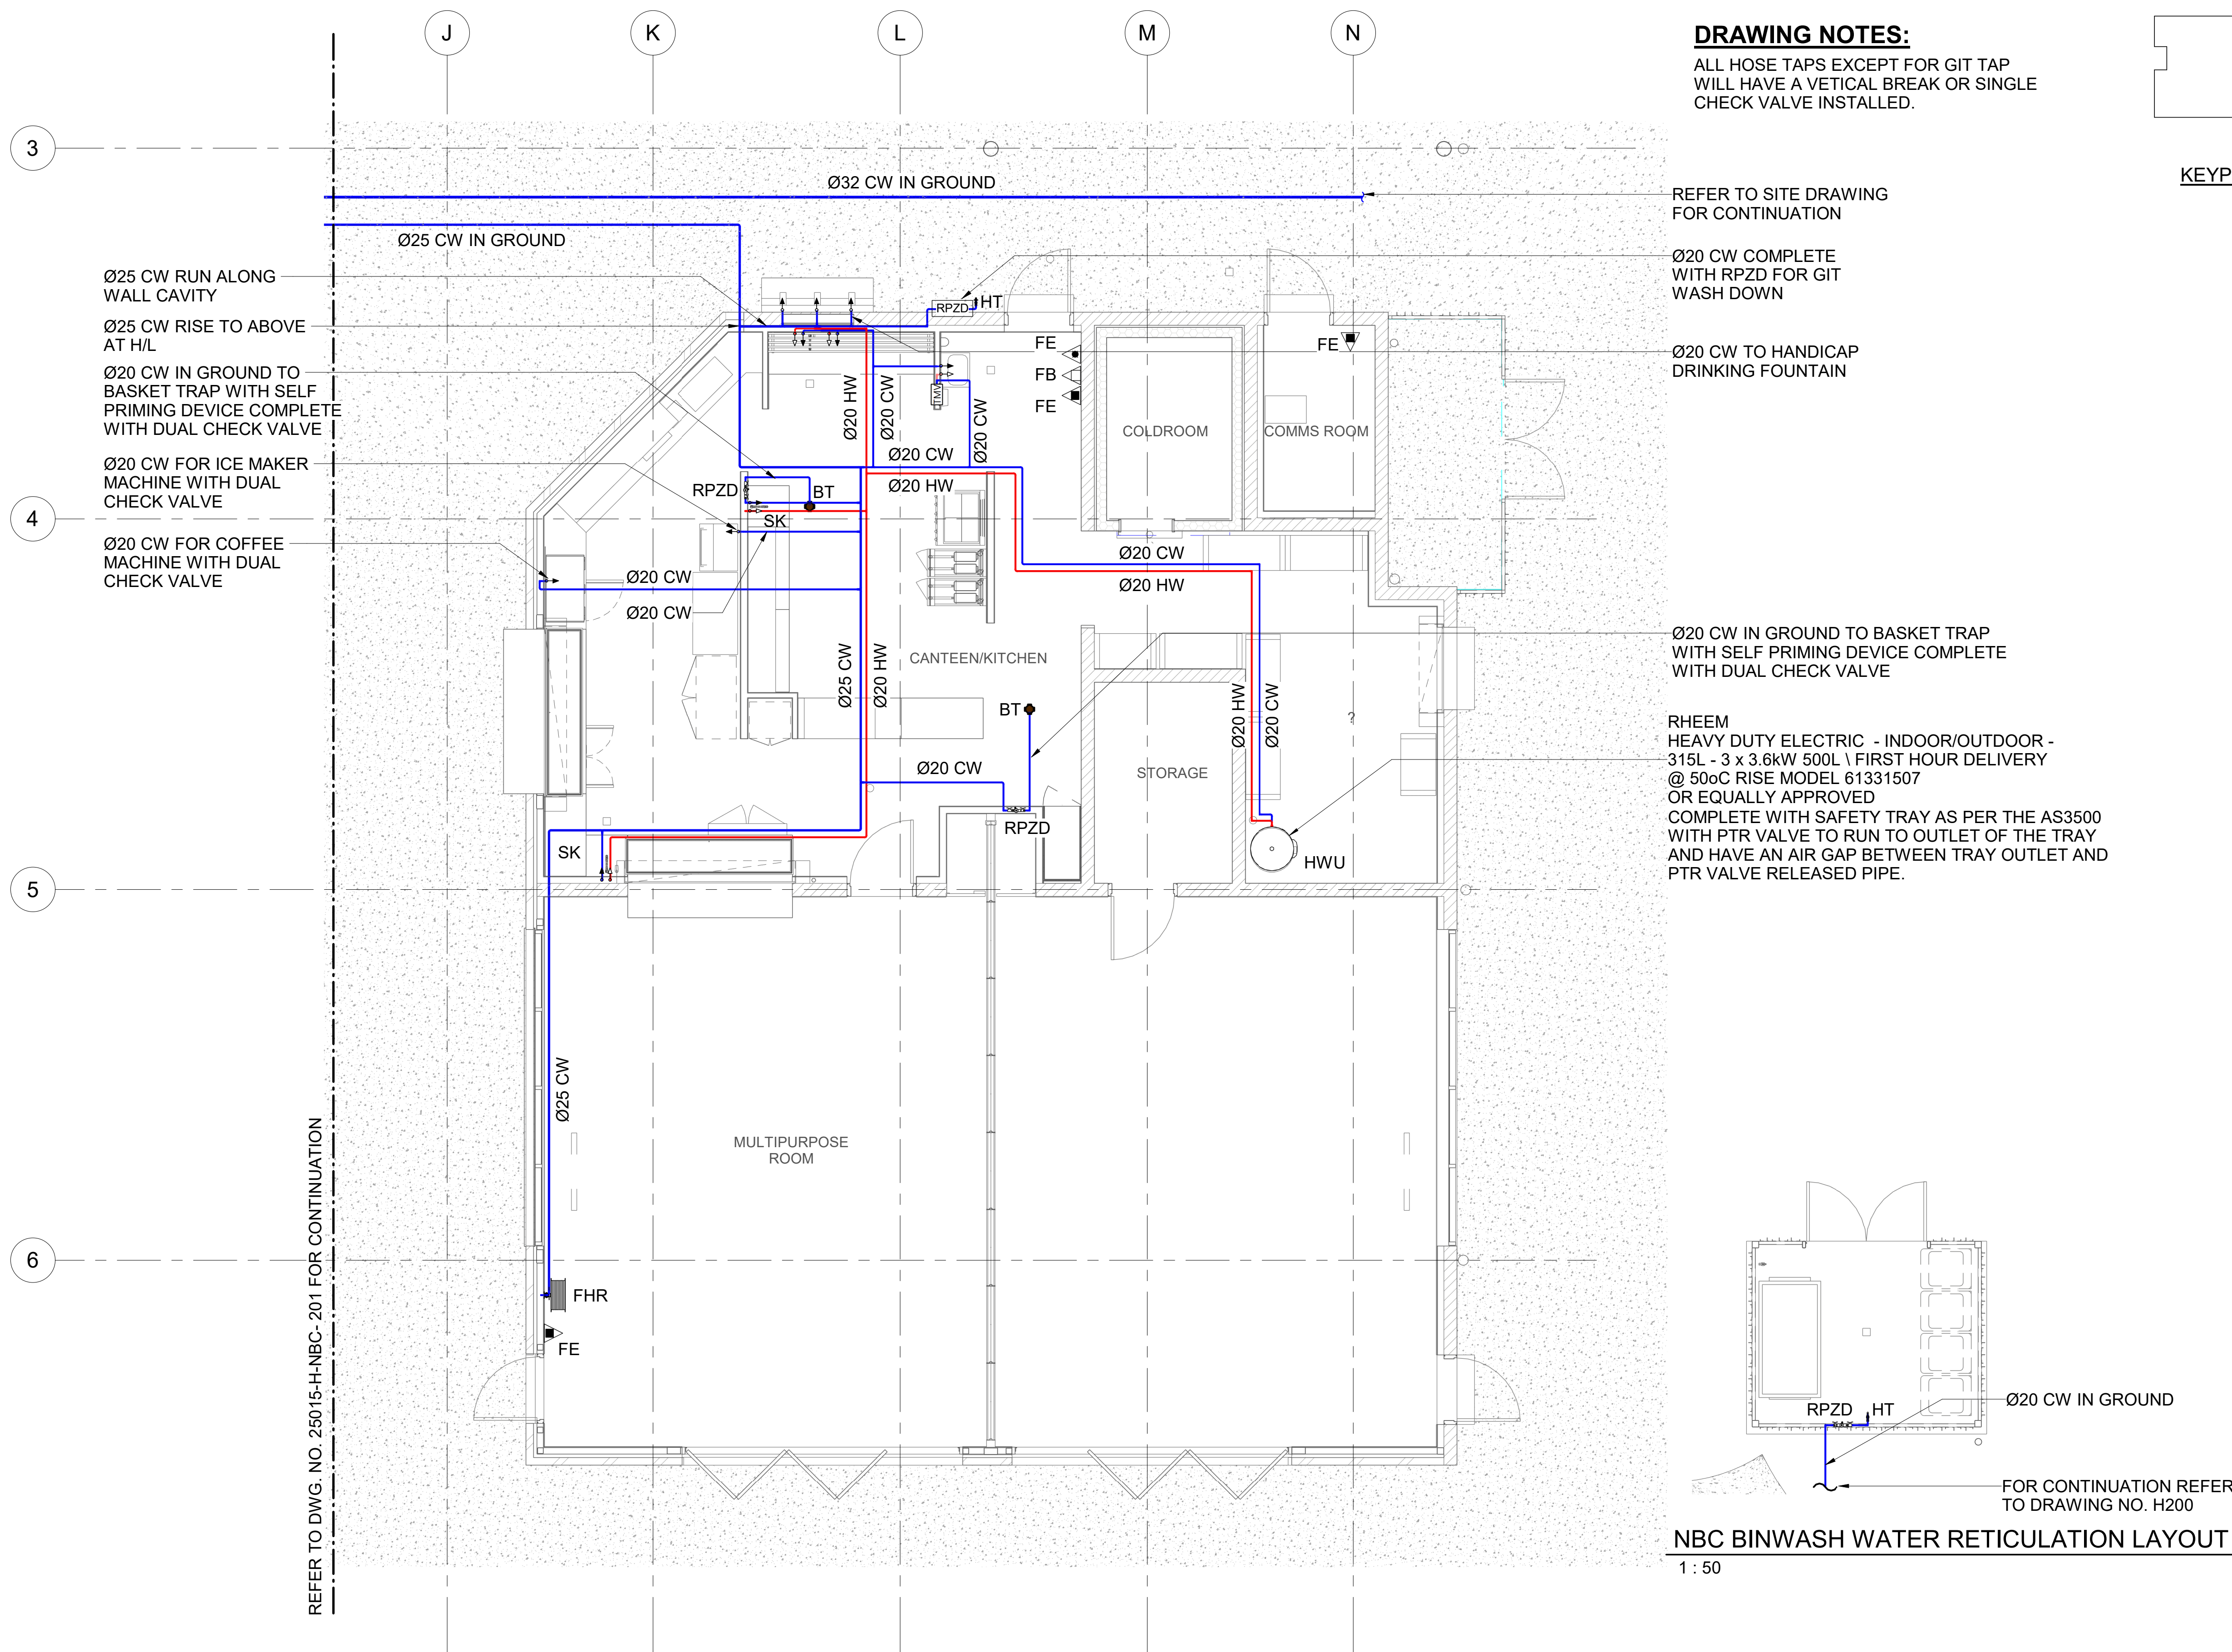

NBC BINWASH WATER RETICULATION LAYOUT

1 : 50

FOR CONTINUATION REFER
TO DRAWING NO. H200

0 1 1 2 2 3 3 4 4 5 5m

SCALE 1:50 AT A1 SHEET | 1:100 AT A3 SHEET

ALL DIMENSIONS SHOWN IN MM. DO NOT SCALE FROM DRAWINGS.
DIMENSIONS TAKE PRECEDENCE. IF IN DOUBT REFER TO HK SOLUTIONS.

GROUND FLOOR WATER RETICULATION LAYOUT - PART PLAN 3

1 : 50

FOR TENDER

						 ENGINEERING PROJECT MANAGEMENT DARWIN, GEELONG, CAIRNS, TOWNSVILLE, PERTH, BALLARAT admin@hksolutions.com.au www.hksolutions.com.au
T1	ISSUE FOR TENDER		17.06.2026	MC	HKS	Conditions of use. This document may only be used by Harris Kiron Solutions clients for the purpose for which it was prepared and must not be used by any other person or for any other purpose.
REV.	DESCRIPTION		DATE	INT.	COMPANY	
REVISIONS						

SPORTENG™

DRAWN	AL
CHECKED	MC
DESIGNED	MC
CHECKED	LM
APPROVED	

THIS DRAWING MUST
NOT BE USED FOR
CONSTRUCTION UNLESS
SIGNED AS APPROVED

STAGE 1
ROCKHAMPTON SPORTS PRECINCT - NETBALL CLUBHOUSE
554-700 YAAMBA ROAD, NORMAN GARDEN - 4701
GROUND FLOOR WATER RETICULATION LAYOUT-PART 3

PAGE No	PROJECT No - DRAWING No	DISCIPLINE	REV.	SHEET SIZE
10 of 10	25015-H-NBC-202	HYDRAULIC	T1	A1

DRAWINGS TO BE PRINTED IN COLOUR