




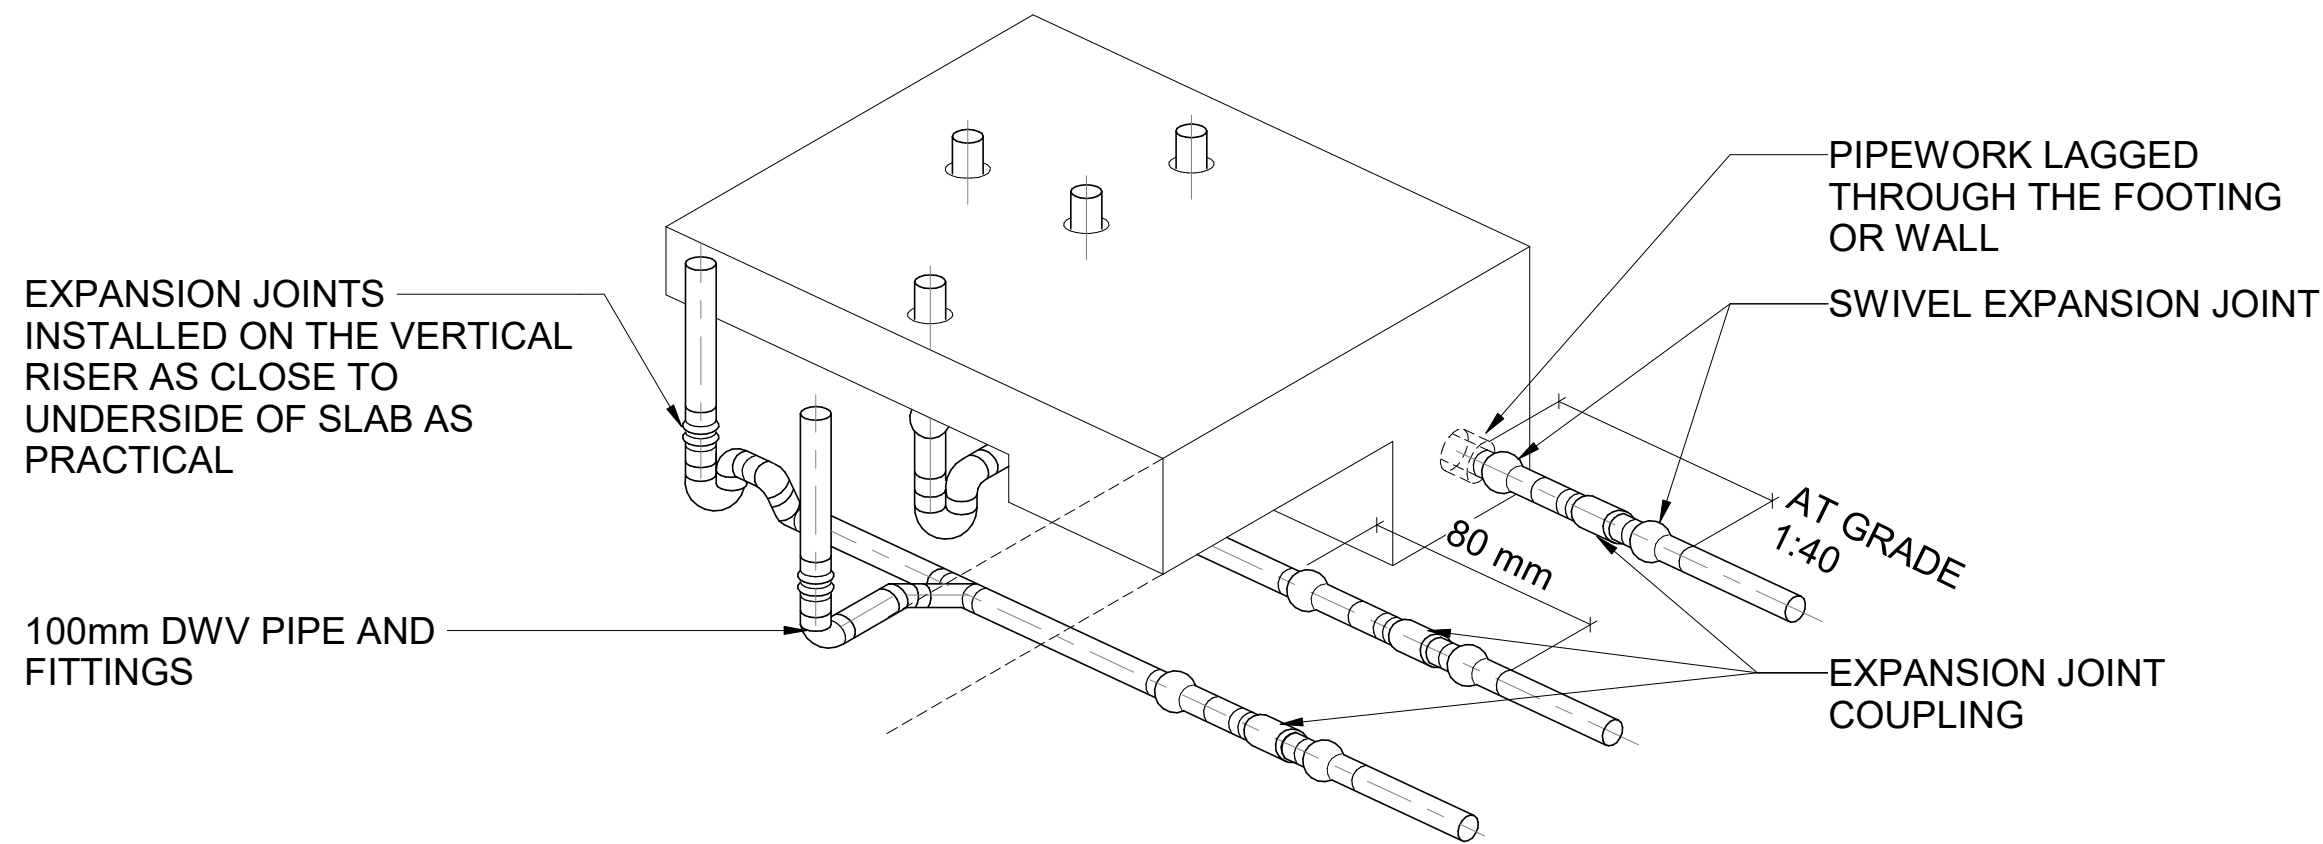


EXPANSION JOINT DETAIL
NTS

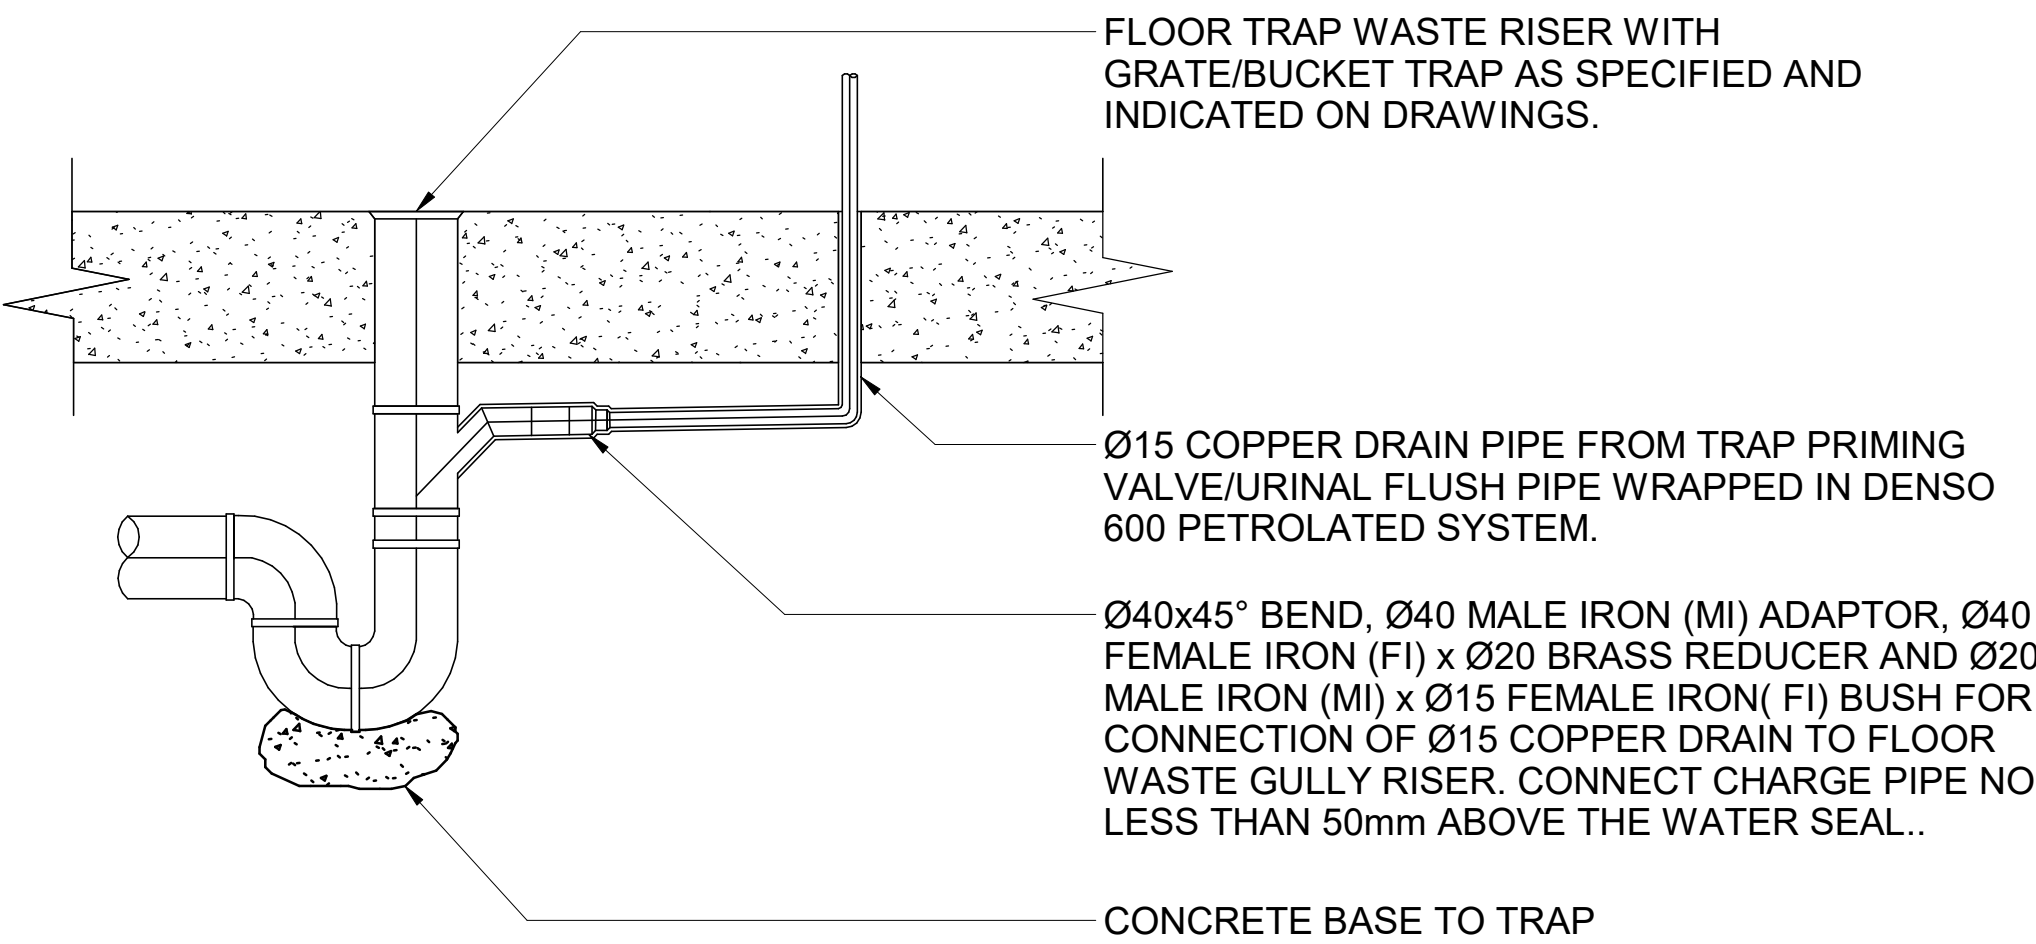


CHARGE LINE TO FLOOR WASTE
NTS

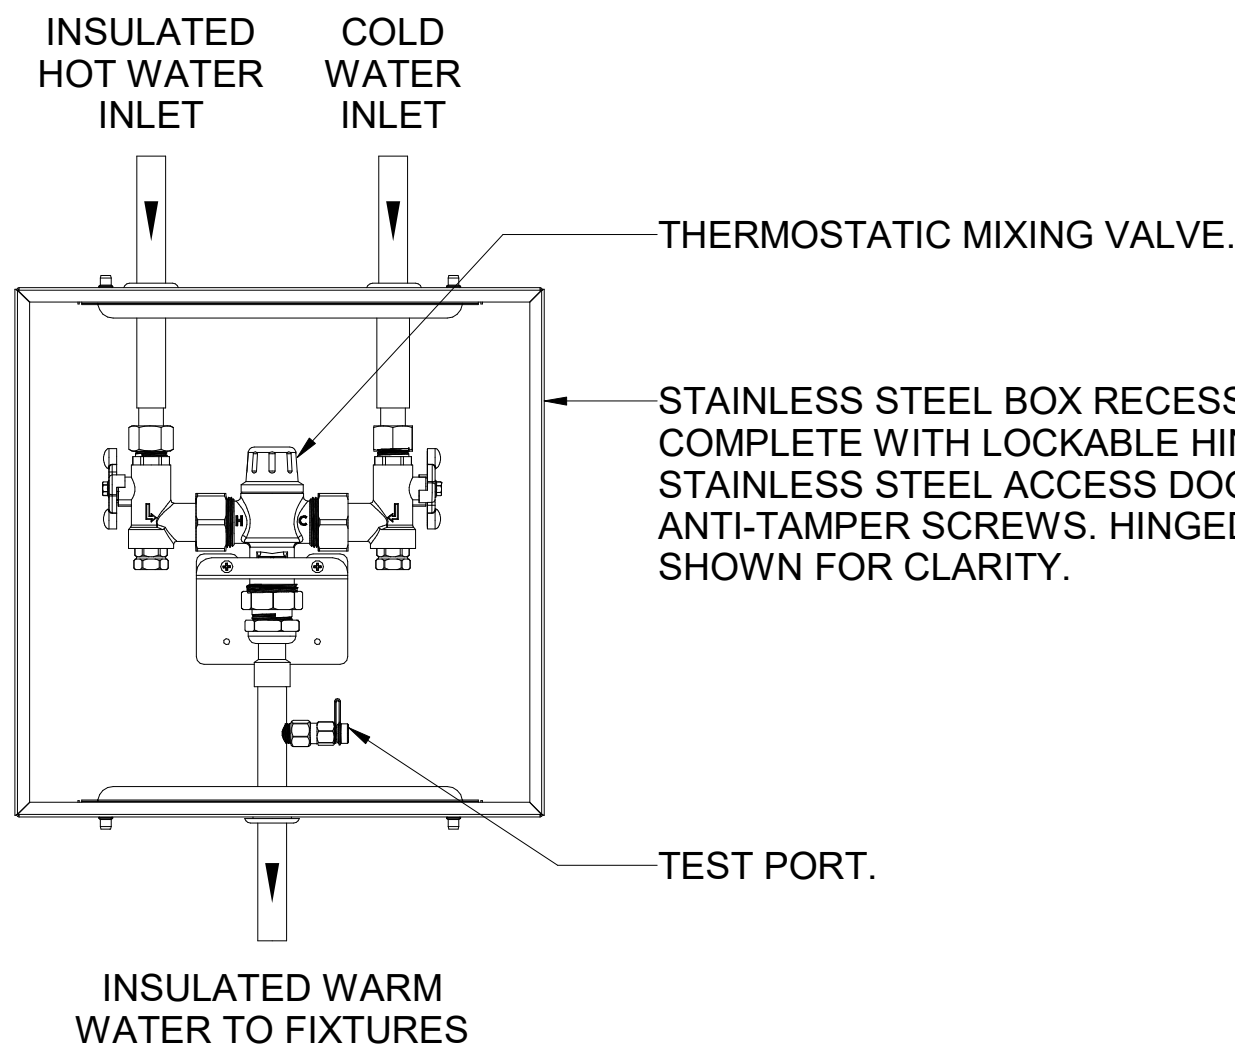


TMV IN WALL BOX
NTS

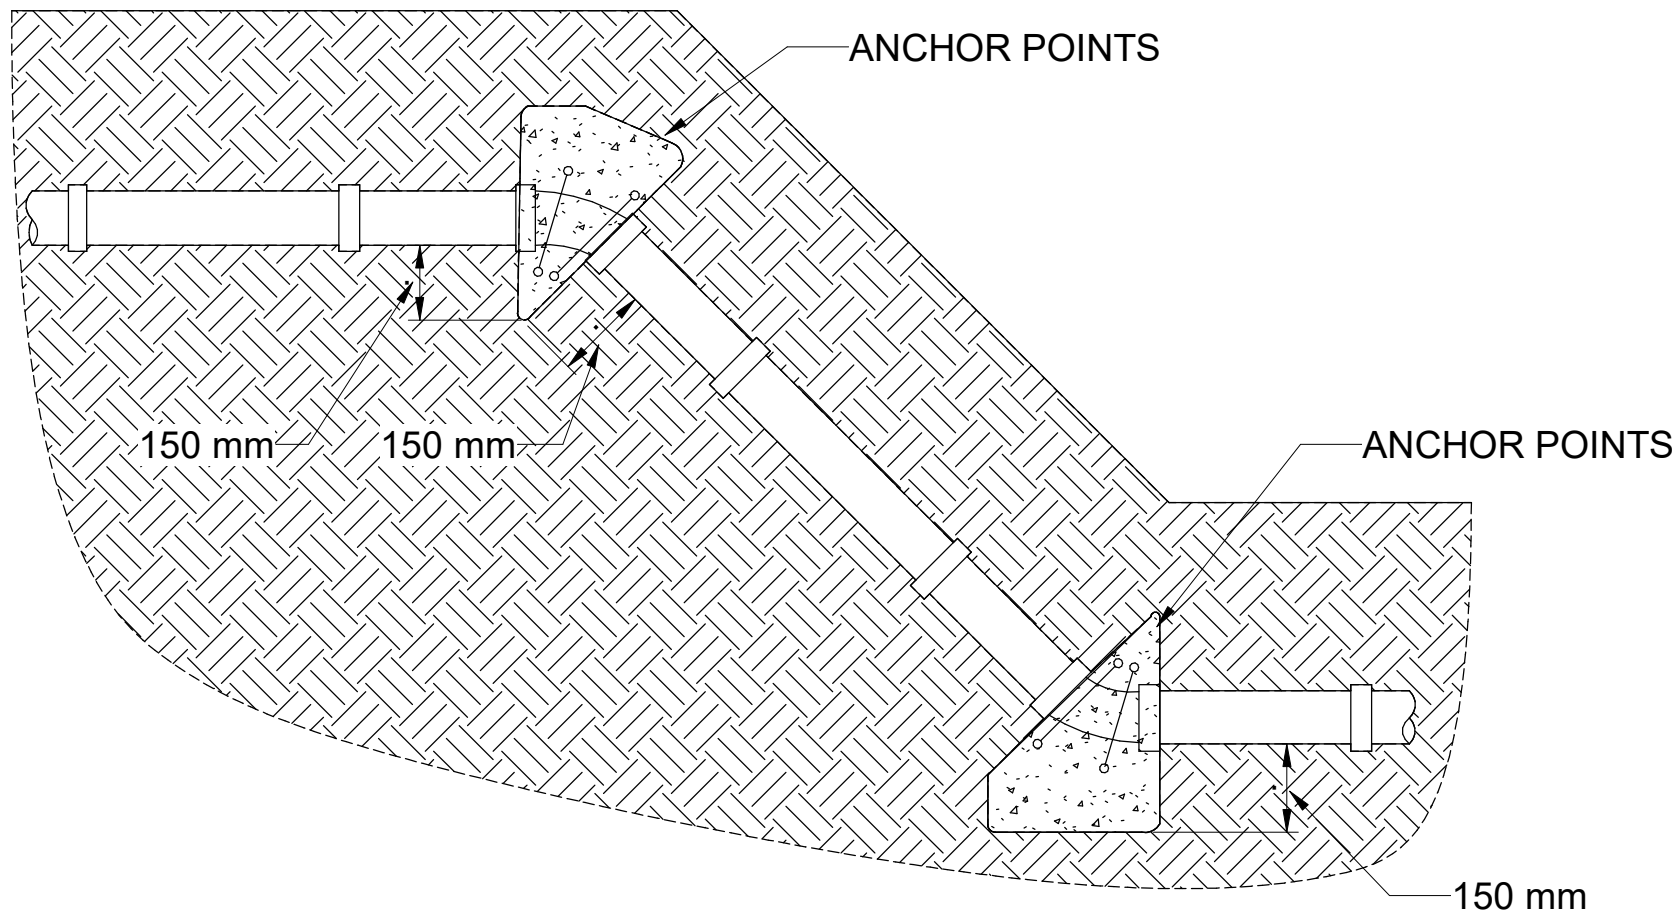


45° JUMP UP DETAIL
NTS

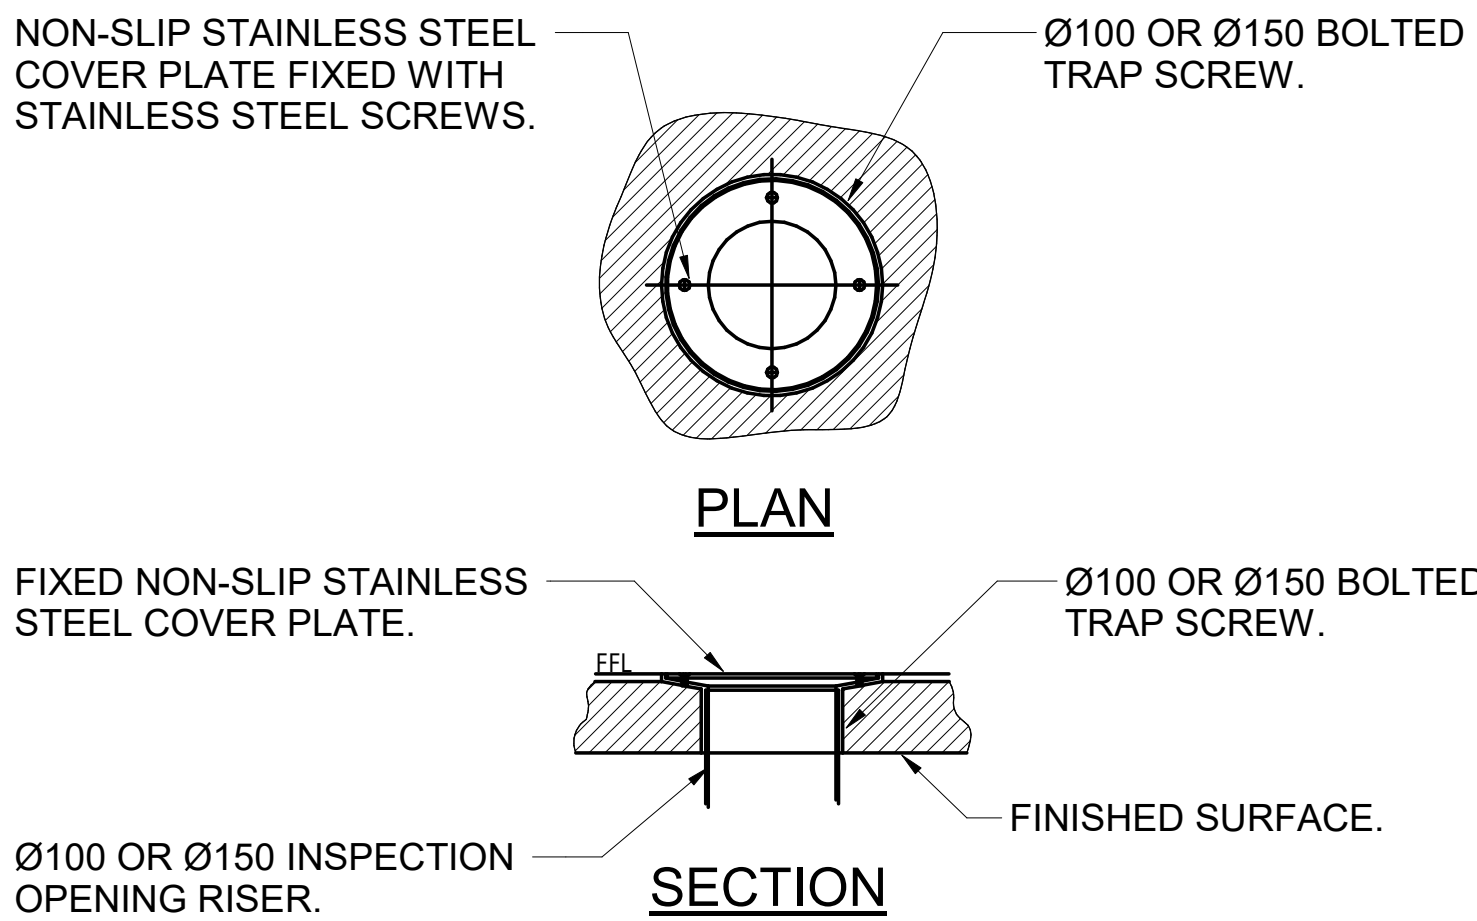


INSPECTION OPENING - NON-SLIP INTERNAL
NTS

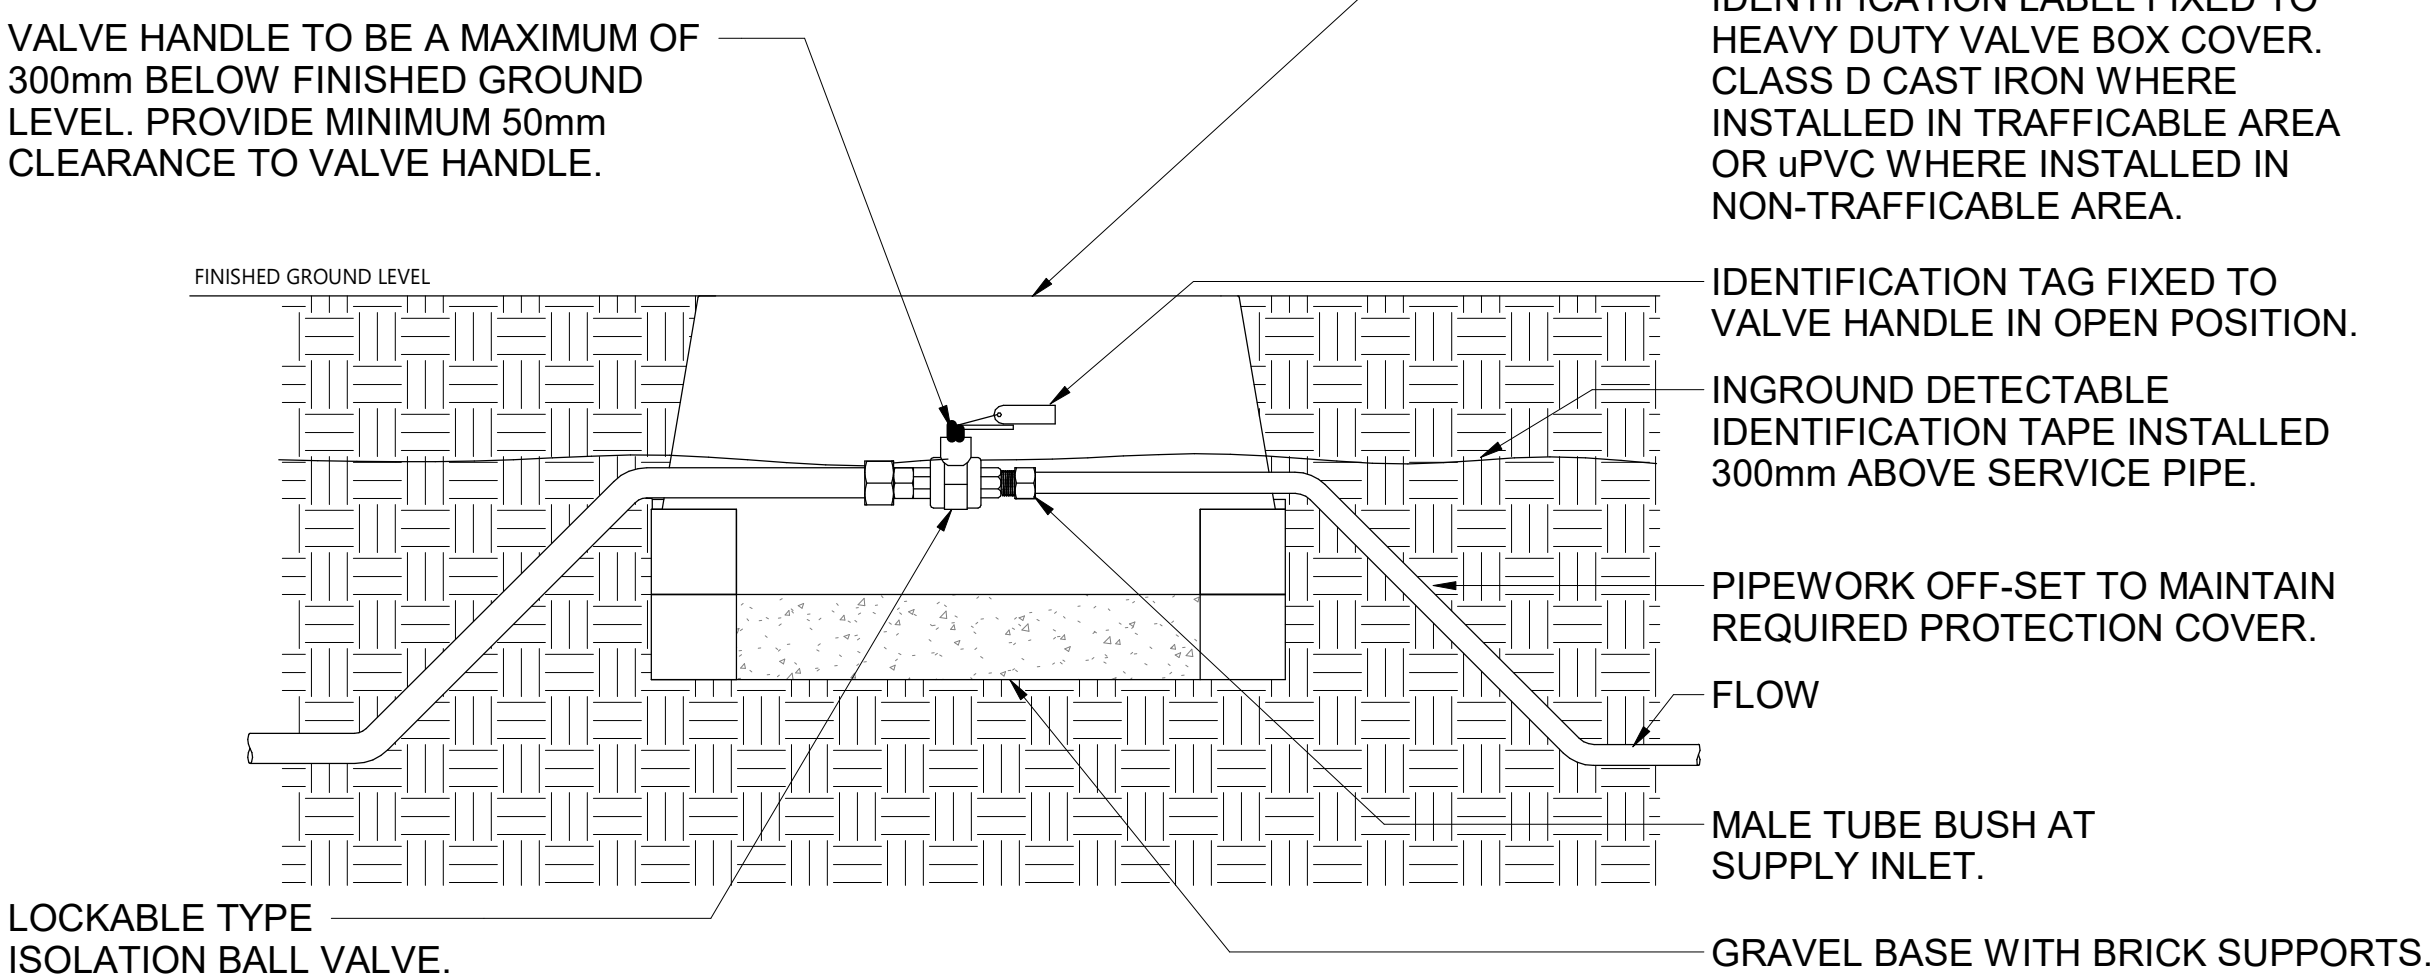


INGROUND ISOLATION VALVE BOX
NTS

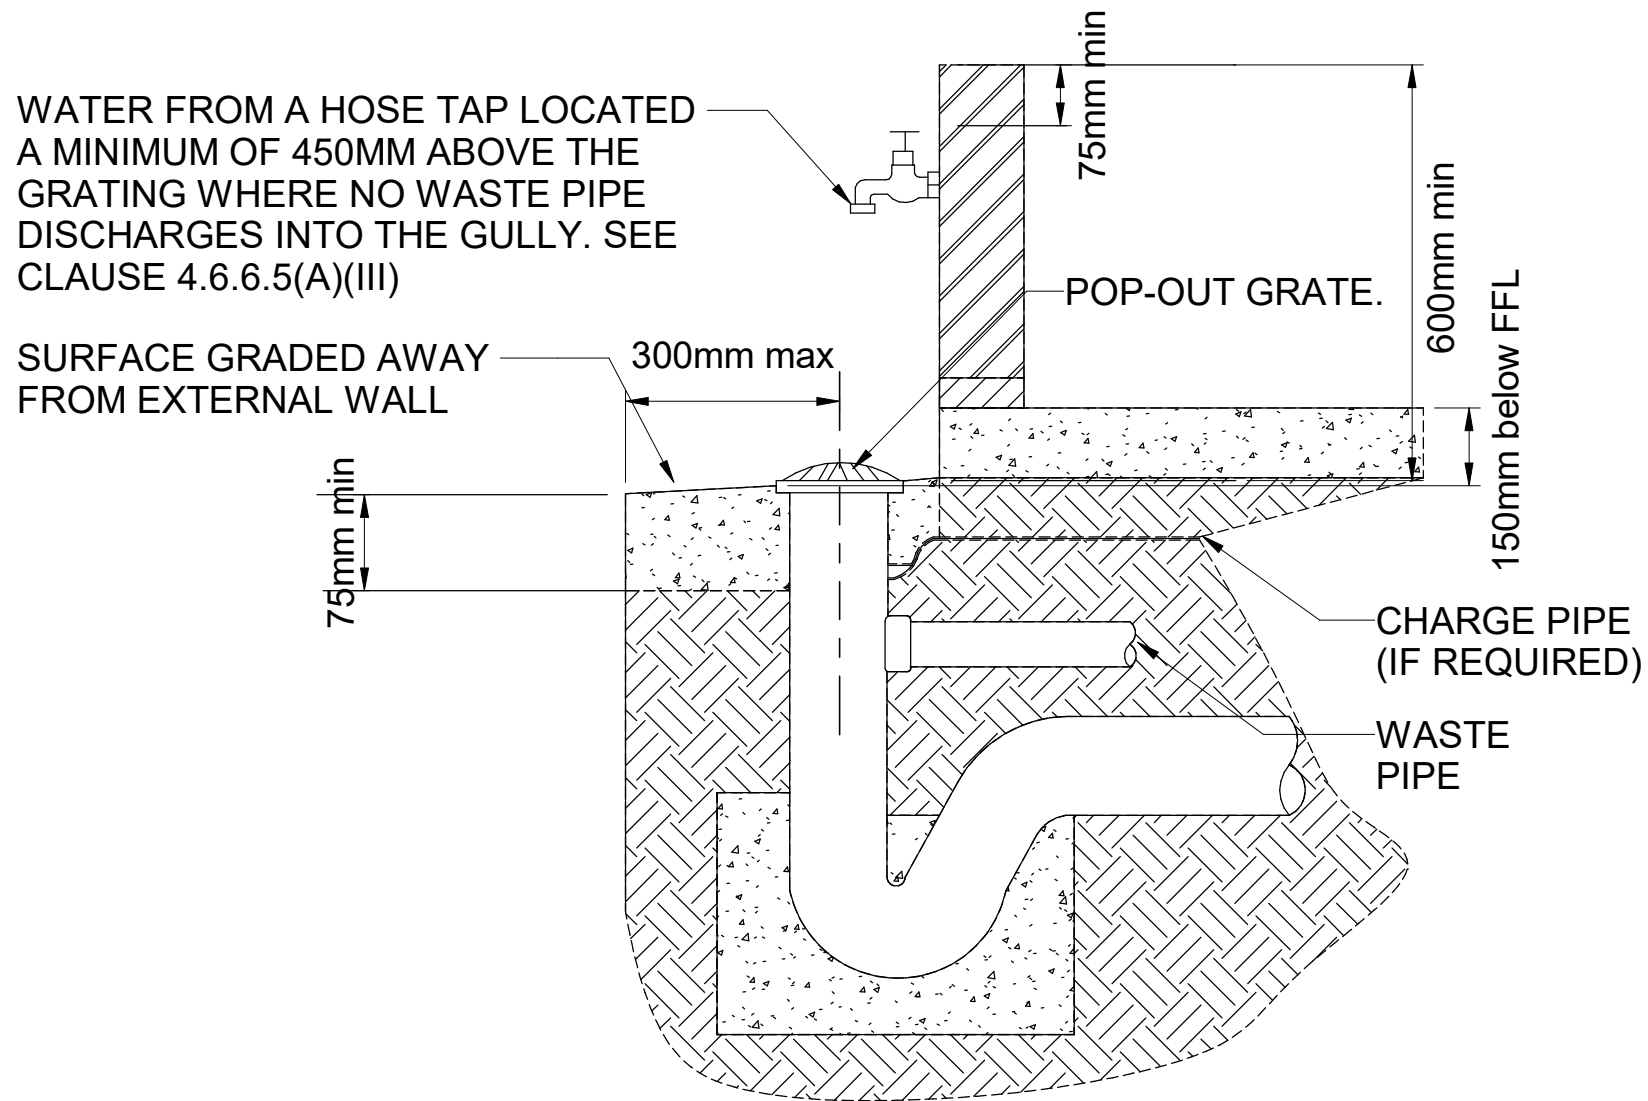

OVERFLOW RELIEF GULLY
NTS

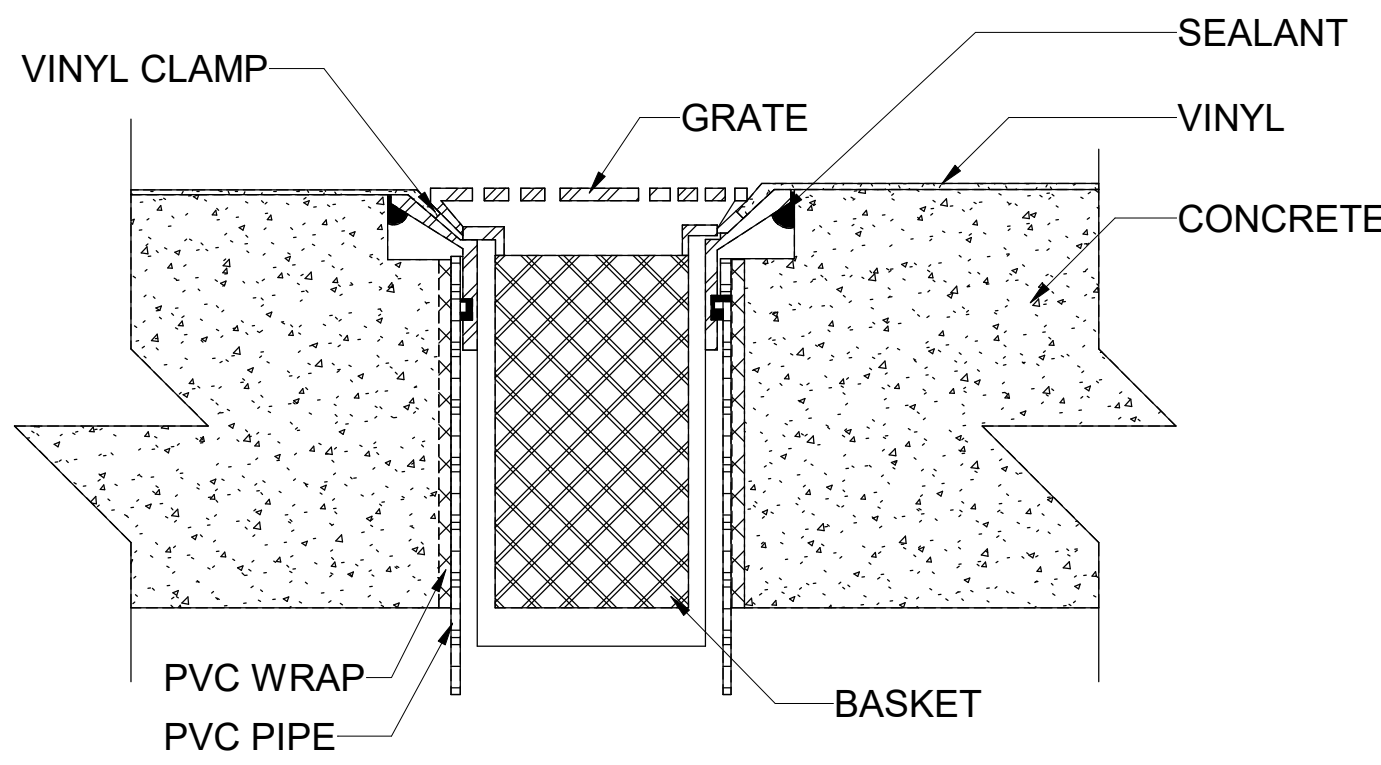

FLOOR/ BASKET WASTE DETAIL
NTS

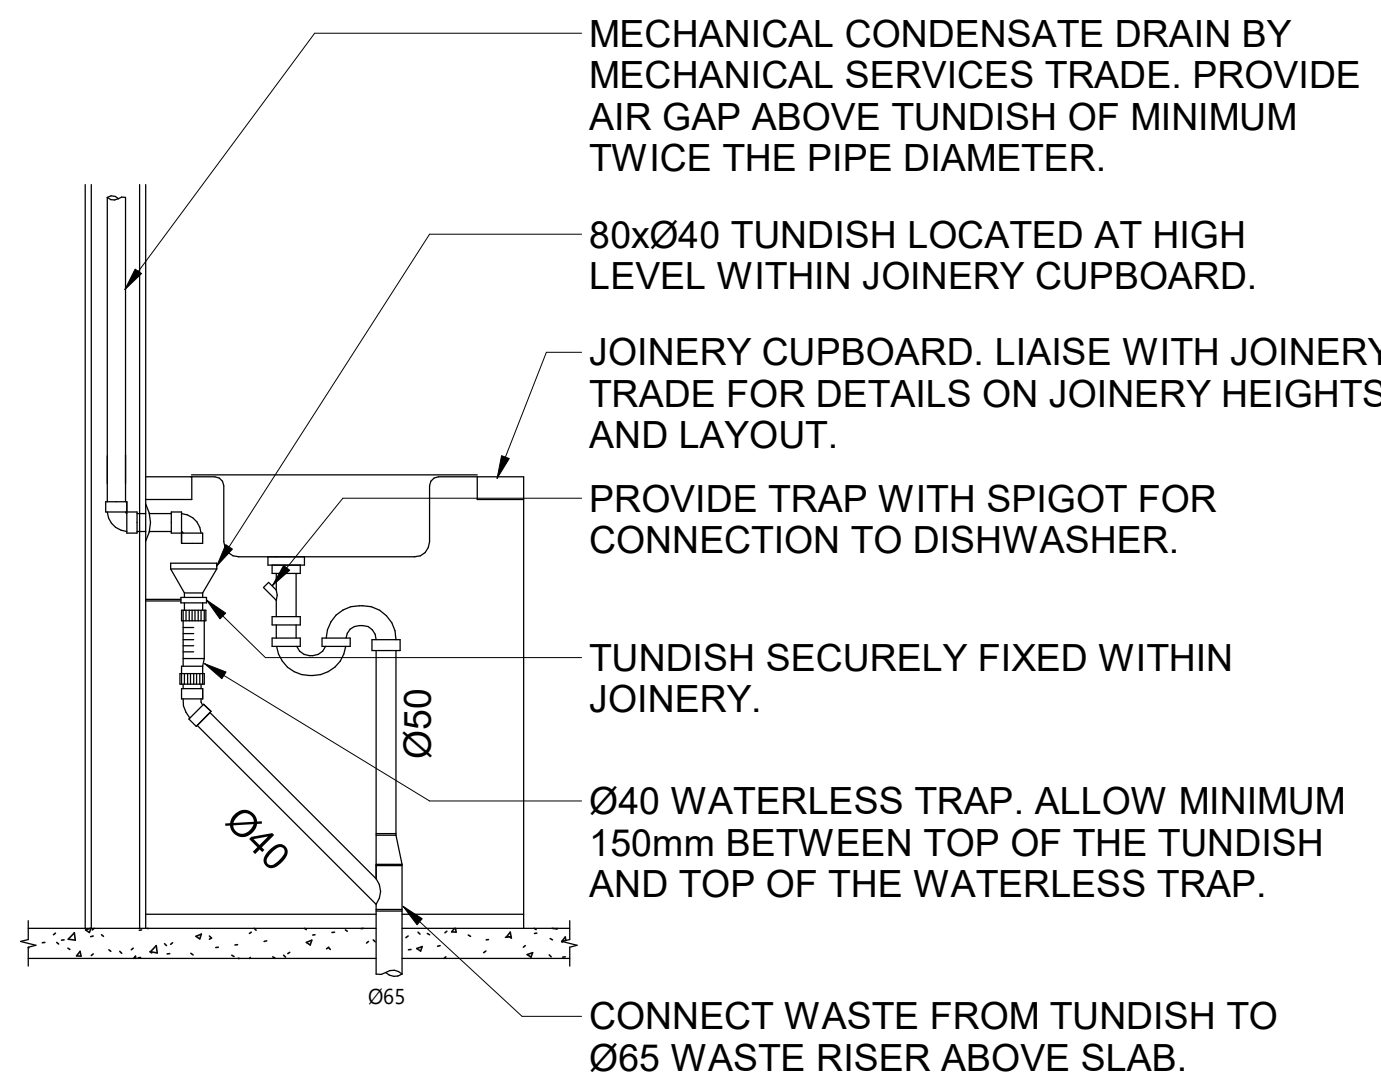

UNDERBENCH TUNDISH FOR A/C DISCHARGE
NTS

FOR TENDER

ALL DIMENSIONS SHOWN IN MM. DO NOT SCALE FROM DRAWINGS.
DIMENSIONS TAKE PRECEDENCE. IF IN DOUBT REFER TO HK SOLUTIONS.

T1	ISSUE FOR TENDER	17.06.2026	MC	HKS
REV.	DESCRIPTION	DATE	INT.	COMPANY
	REVISIONS			

HK Solutions

ENGINEERING PROJECT MANAGEMENT
DARWIN, GEELONG, CAIRNS, TOWNSVILLE, PERTH, BALLARAT
admin@hksolutions.com.au
www.hksolutions.com.au

Conditions of use. This document may only be used by Harris Kmon Solutions clients for the purpose for which it was prepared and must not be used by any other person or for any other purpose.

SPORTENG™

DRAWN	AL
CHECKED	MC
DESIGNED	MC
CHECKED	LM
APPROVED	

THIS DRAWING MUST NOT BE USED FOR CONSTRUCTION UNLESS SIGNED AS APPROVED

STAGE 1
ROCKHAMPTON SPORTS PRECINCT - NETBALL CLUBHOUSE
554-700 YAAMBA ROAD, NORMAN GARDEN - 4701
DETAILS

PAGE No	PROJECT No - DRAWING No	DISCIPLINE	REV.	SHEET SIZE
10 of 10	25015-H-NBC-300	HYDRAULIC	T1	A1

DRAWINGS TO BE PRINTED IN COLOUR