


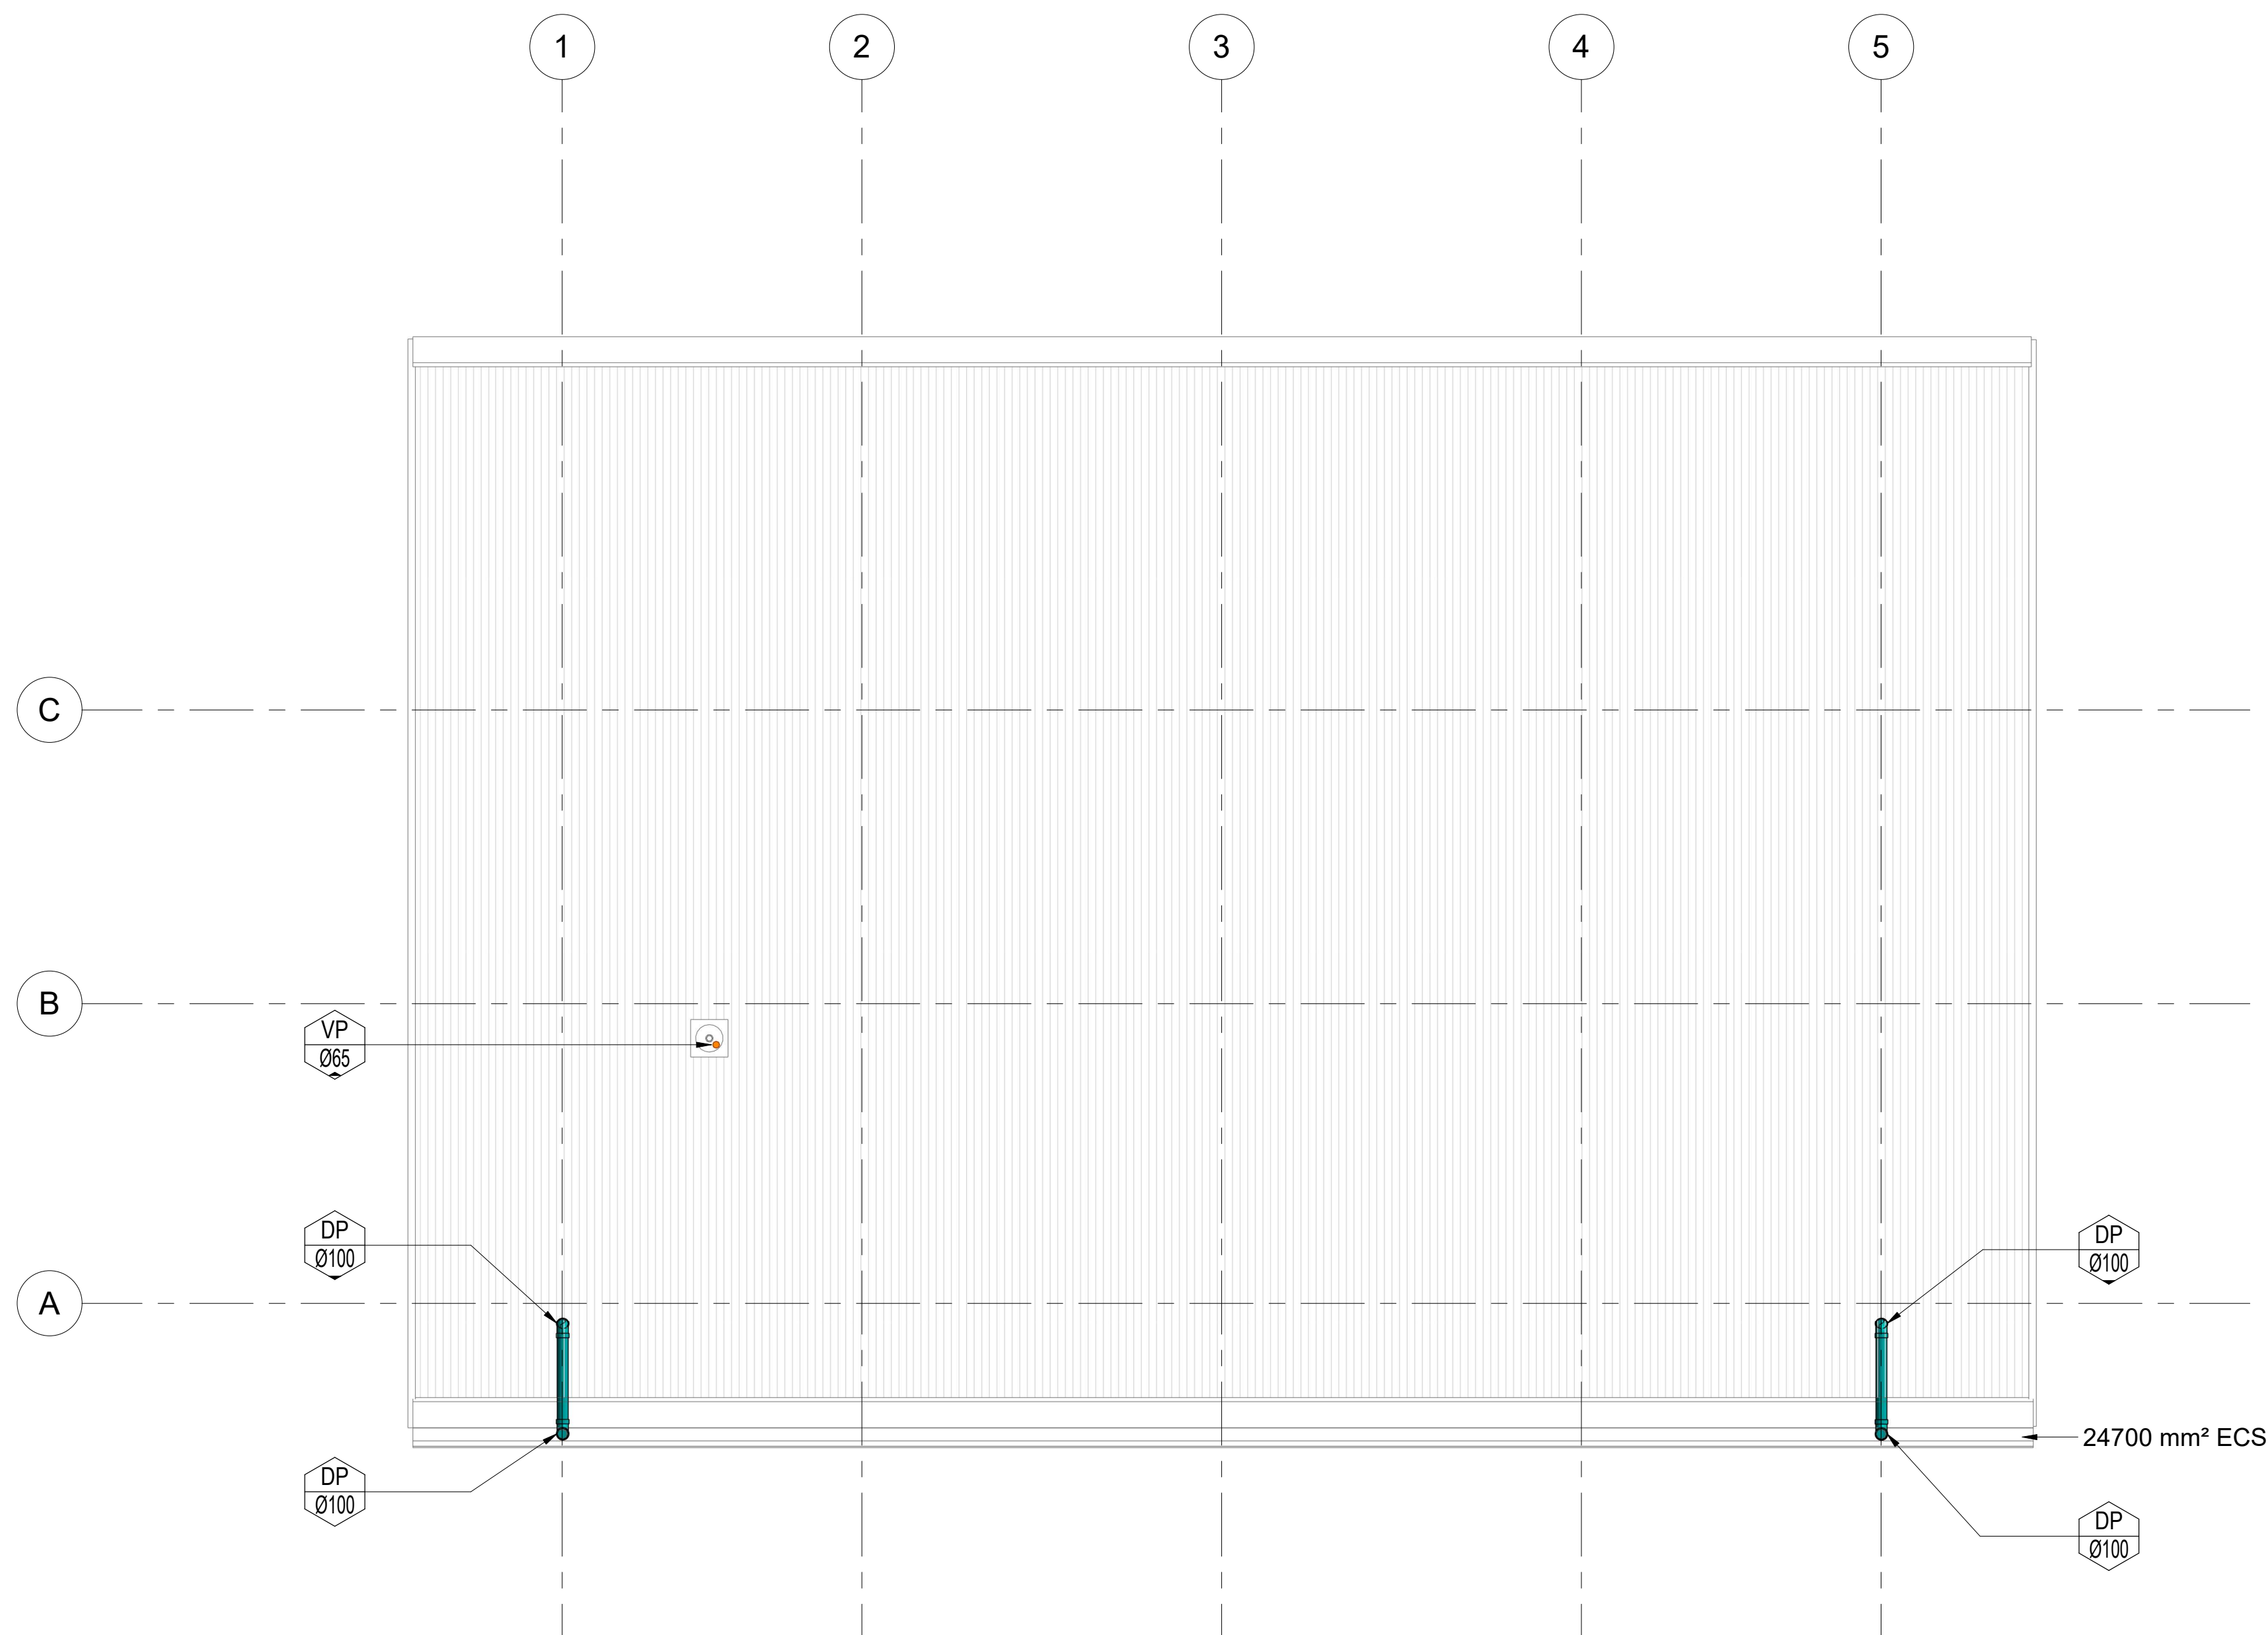

ROOF LEVEL STORM WATER LAYOUT
1 : 50

ALL DIMENSIONS SHOWN IN MM. DO NOT SCALE FROM DRAWINGS.
DIMENSIONS TAKE PRECEDENCE. IF IN DOUBT REFER TO HK SOLUTIONS.

FOR TENDER

						 ENGINEERING PROJECT MANAGEMENT DARWIN, GEELONG, CAIRNS, TOWNSVILLE PERTH, BALLARAT admin@hksolutions.com.au www.hksolutions.com.au
T1	ISSUE FOR TENDER		17.06.2026	MC	HKS	
REV.	DESCRIPTION		DATE	INT.	COMPANY	
REVISIONS						

Conditions of use. This document may only be used by Harris Kmon Solutions clients for the purpose for which it was prepared and must not be used by any other person or for any other purpose.

SPORTIVE

DRAWN	Author
CHECKED	Checker
DESIGNED	Designer
CHECKED	Approver
APPROVED	
THIS DRAWING MUST NOT BE USED FOR CONSTRUCTION UNLESS SIGNED AS APPROVED	

STAGE 1
ROCKHAMPTON SPORTS PRECINCT - PUBLIC AMENITIES BLOCK
554-700 YAAMBA ROAD, NORMAN GARDEN - 4701
ROOF LEVEL STORM WATER LAYOUT

PAGE No	PROJECT No - DRAWING No	DISCIPLINE	REV.	SHEET SIZE
05 of 06	25015-H-PAM-101	HYDRAULIC	T1	A1

DRAWINGS TO BE PRINTED IN COLOUR