




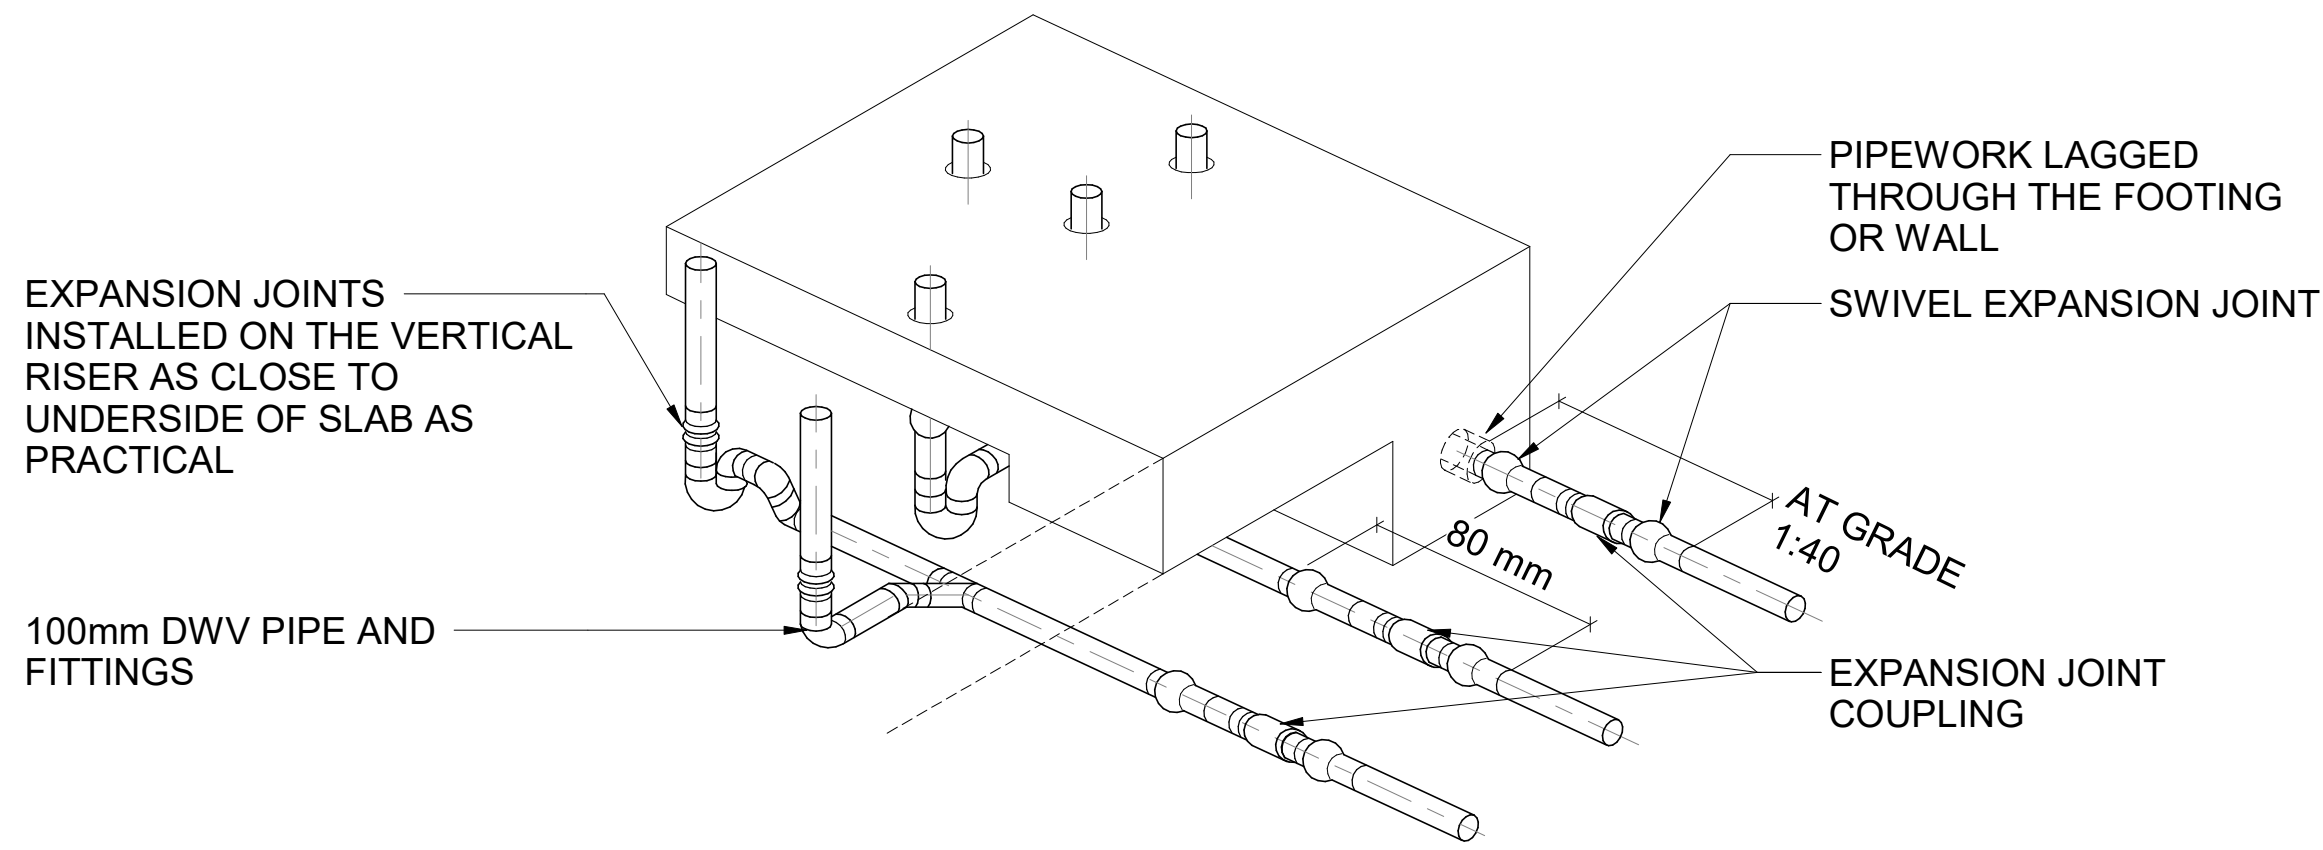


EXPANSION JOINT DETAIL
NTS

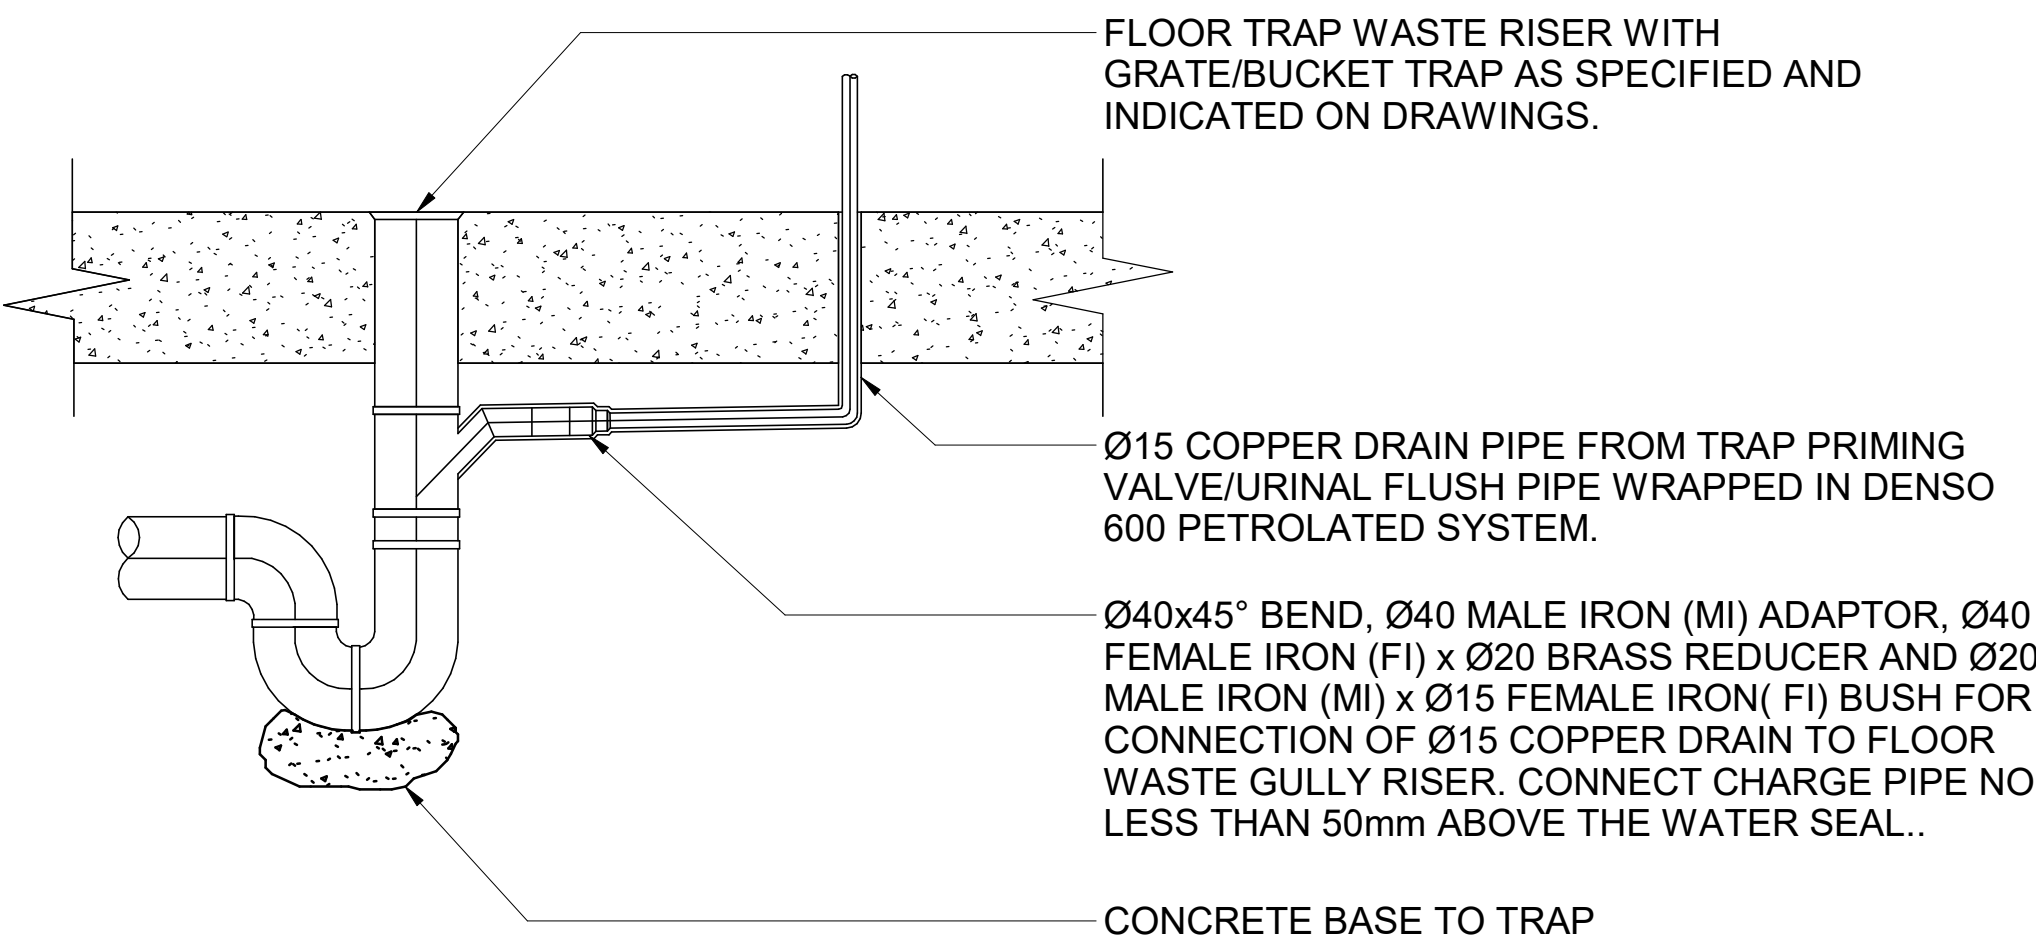


CHARGE LINE TO FLOOR WASTE
NTS

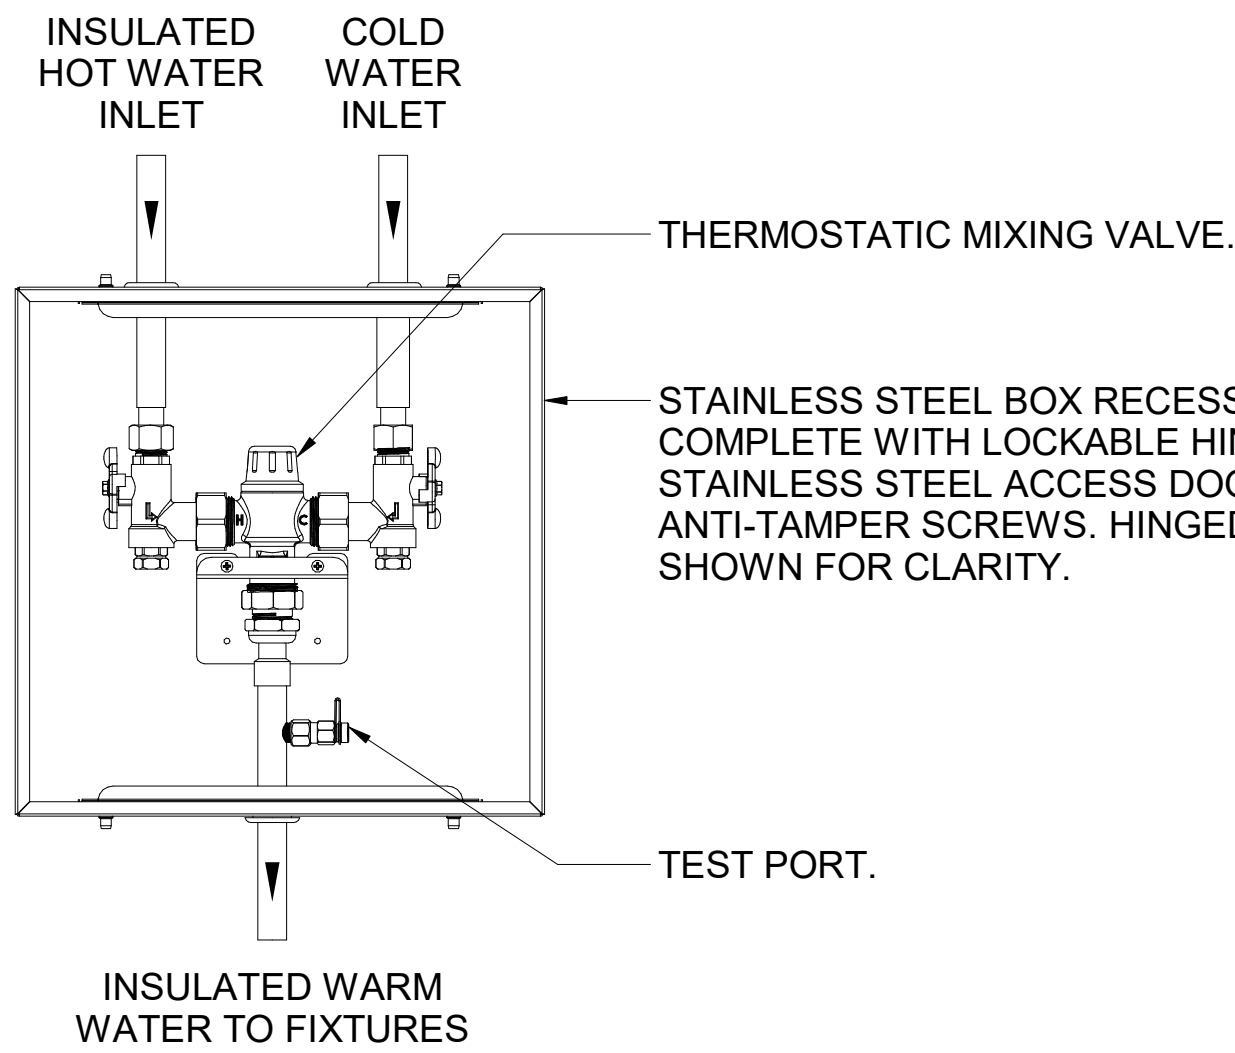


TMV IN WALL BOX
NTS

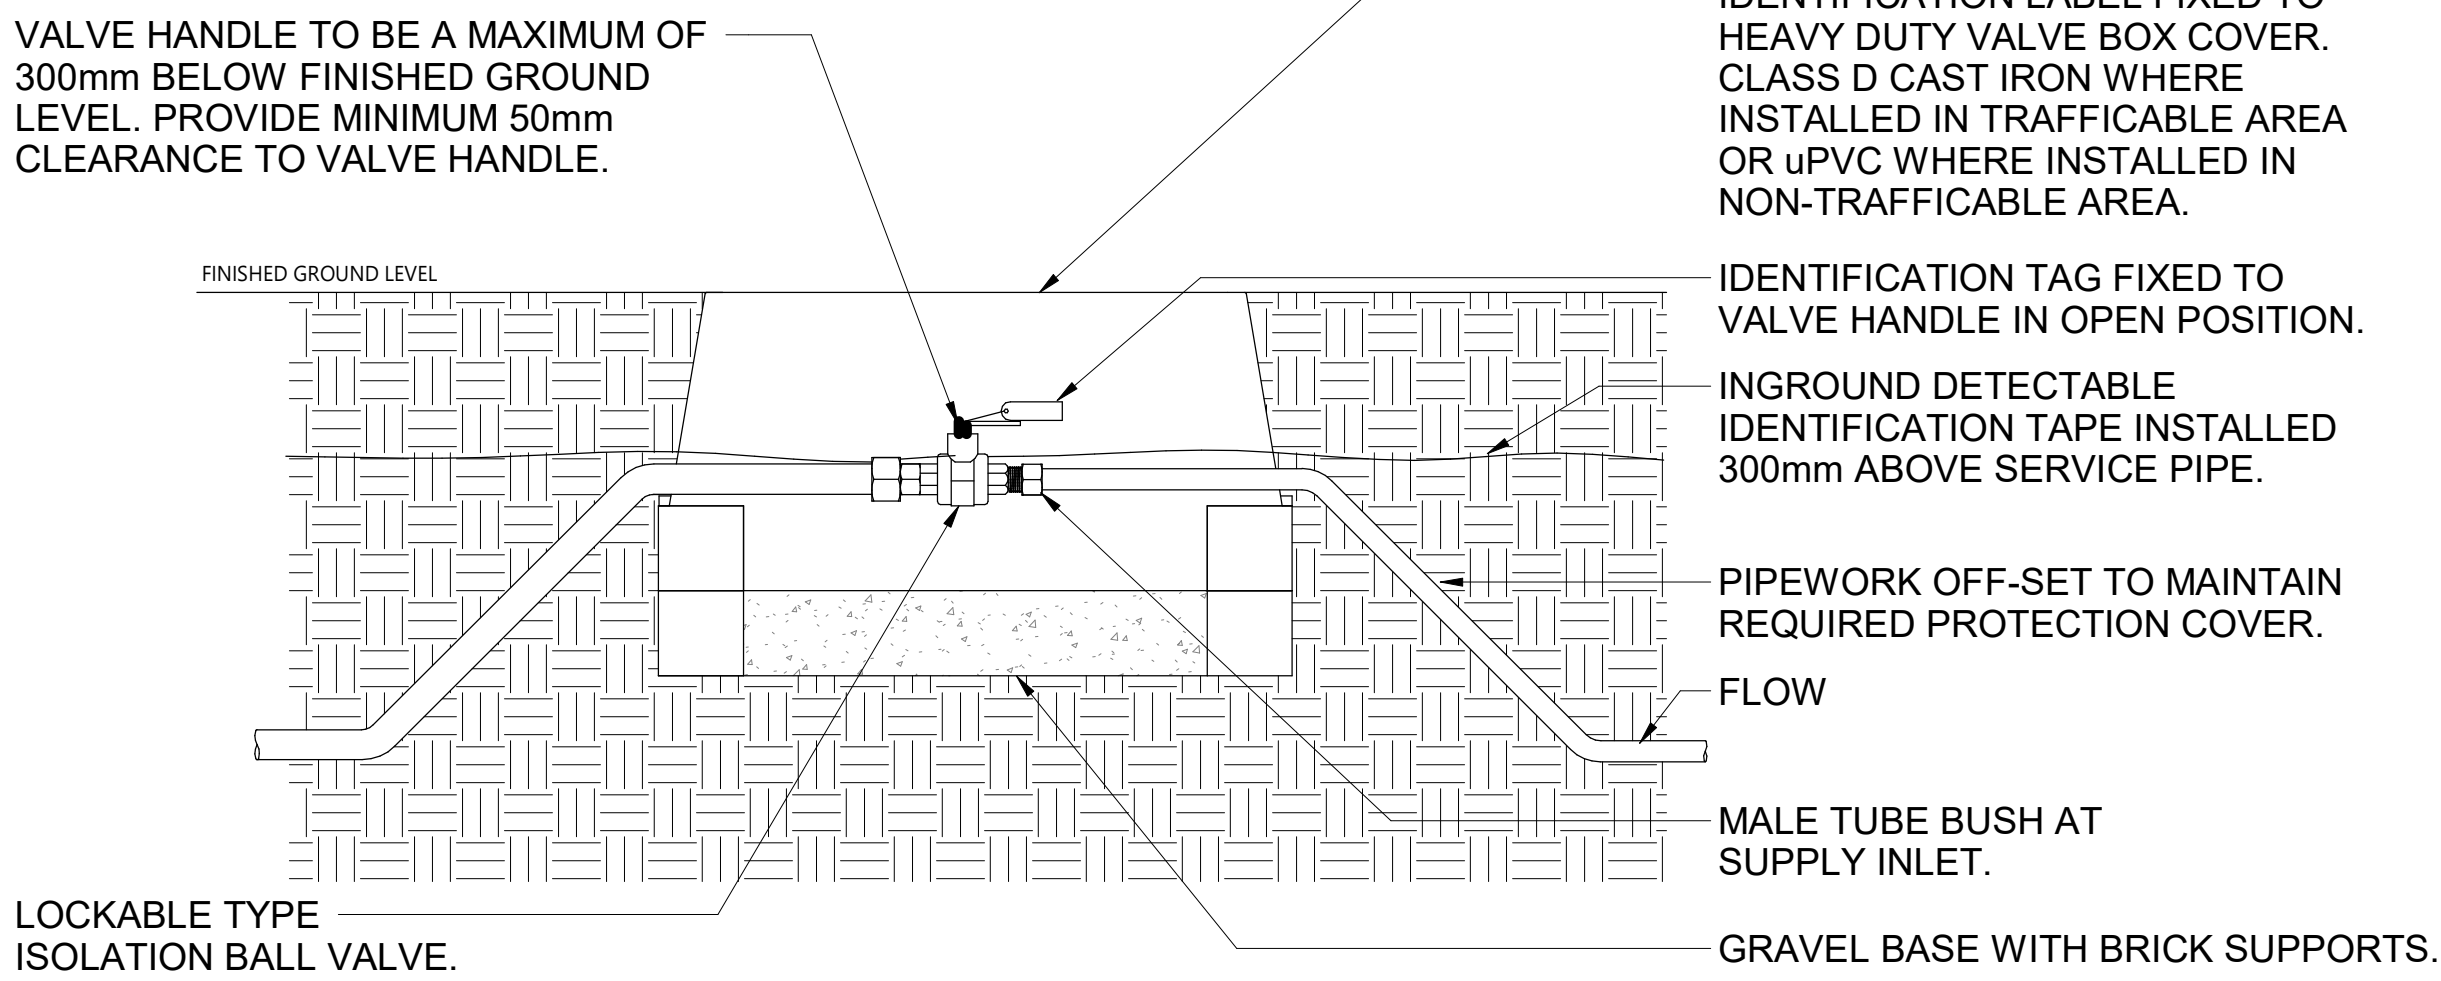


INGROUND ISOLATION VALVE BOX
NTS

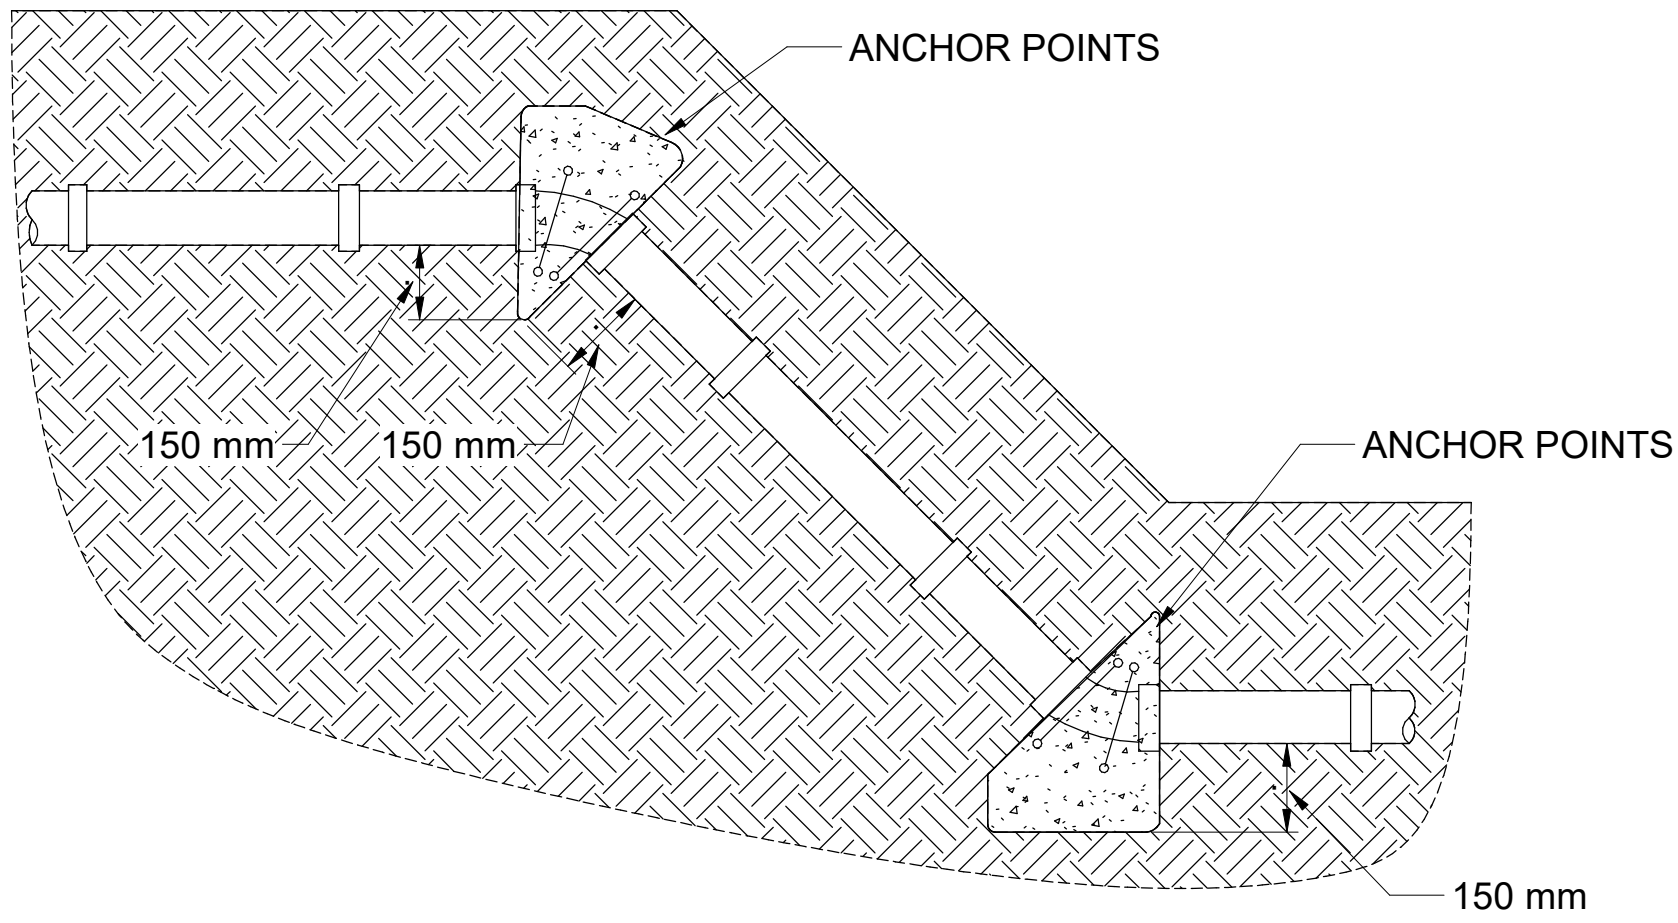


45° JUMP UP DETAIL
NTS

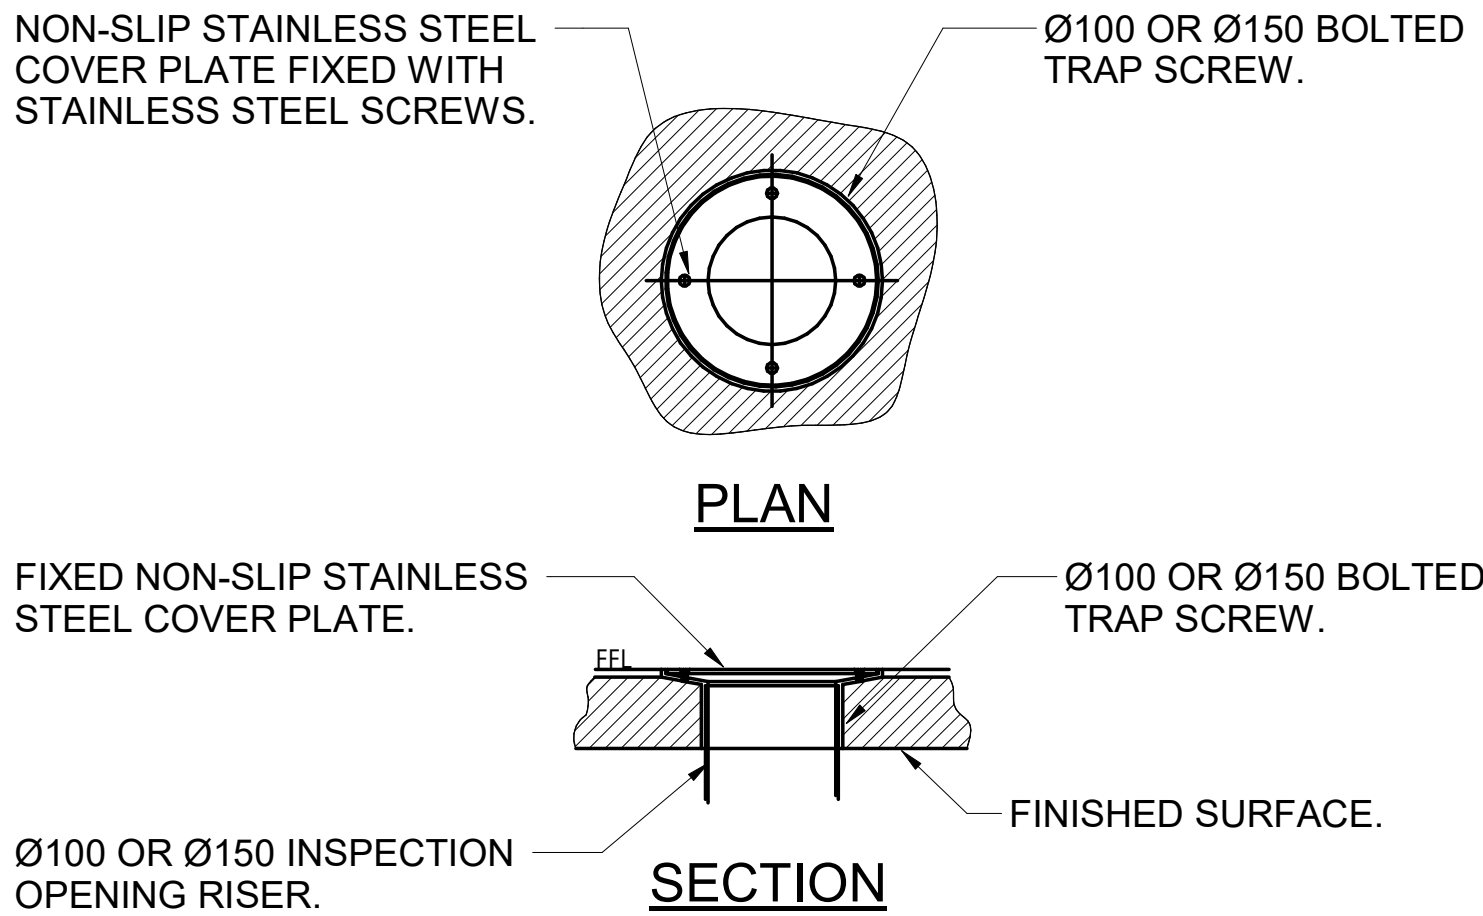


INSPECTION OPENING - NON-SLIP INTERNAL
NTS

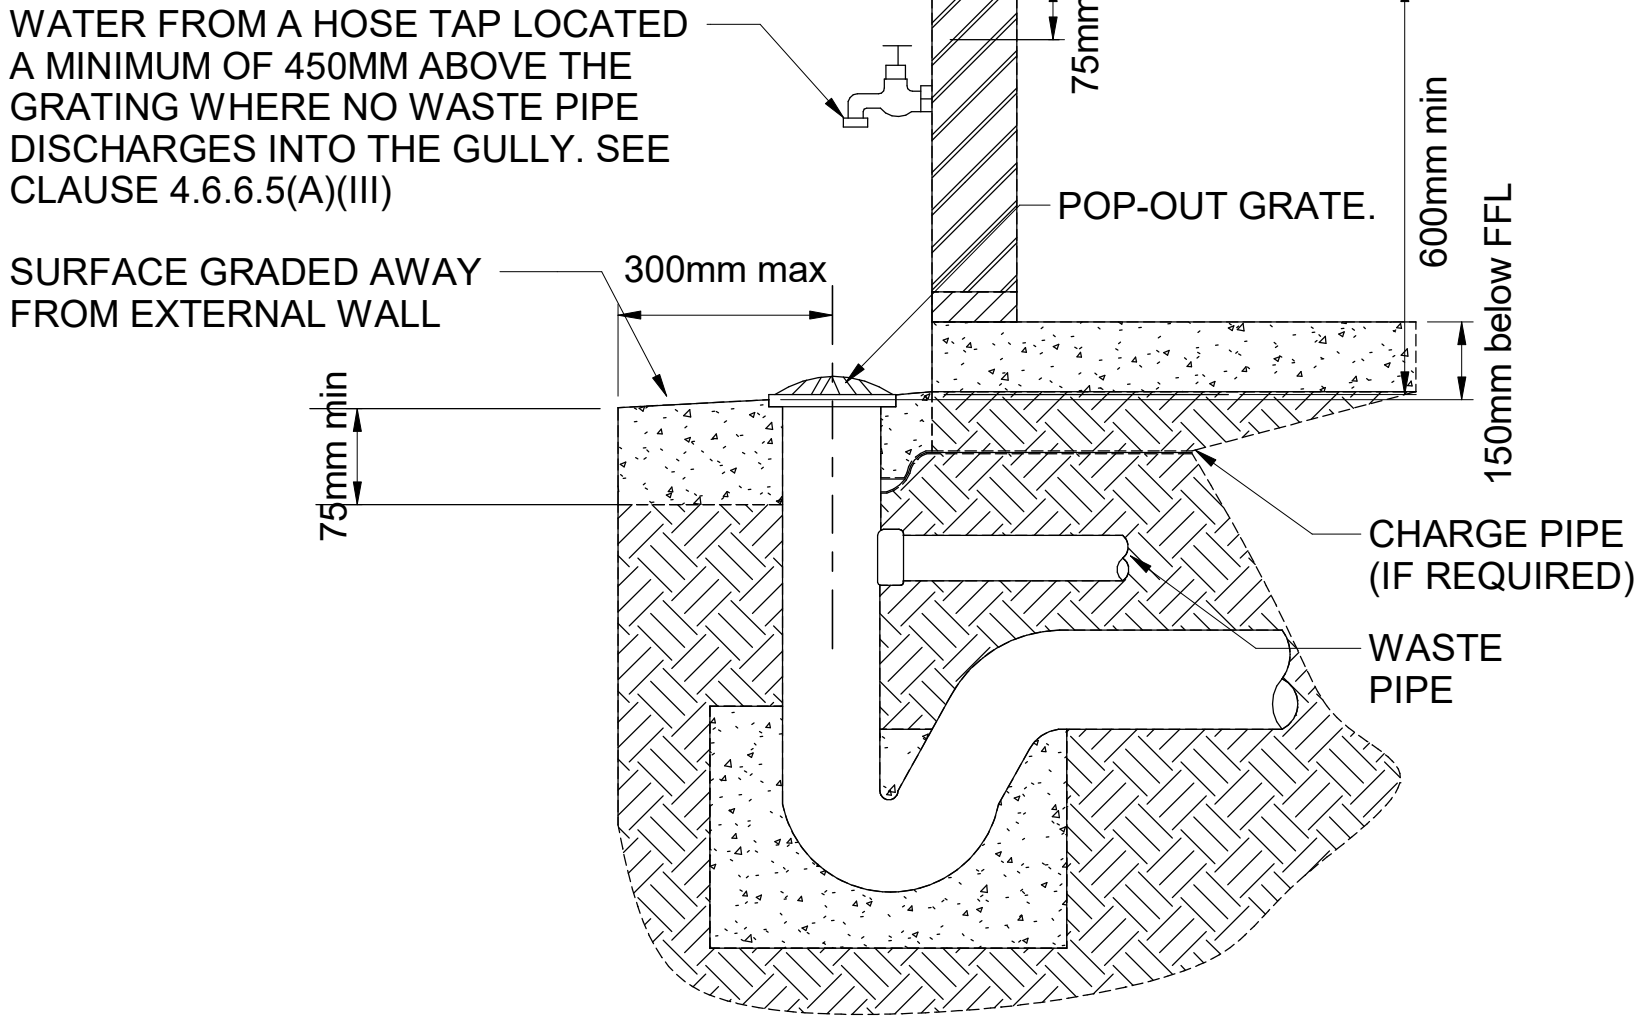

OVERFLOW RELIEF GULLY
NTS

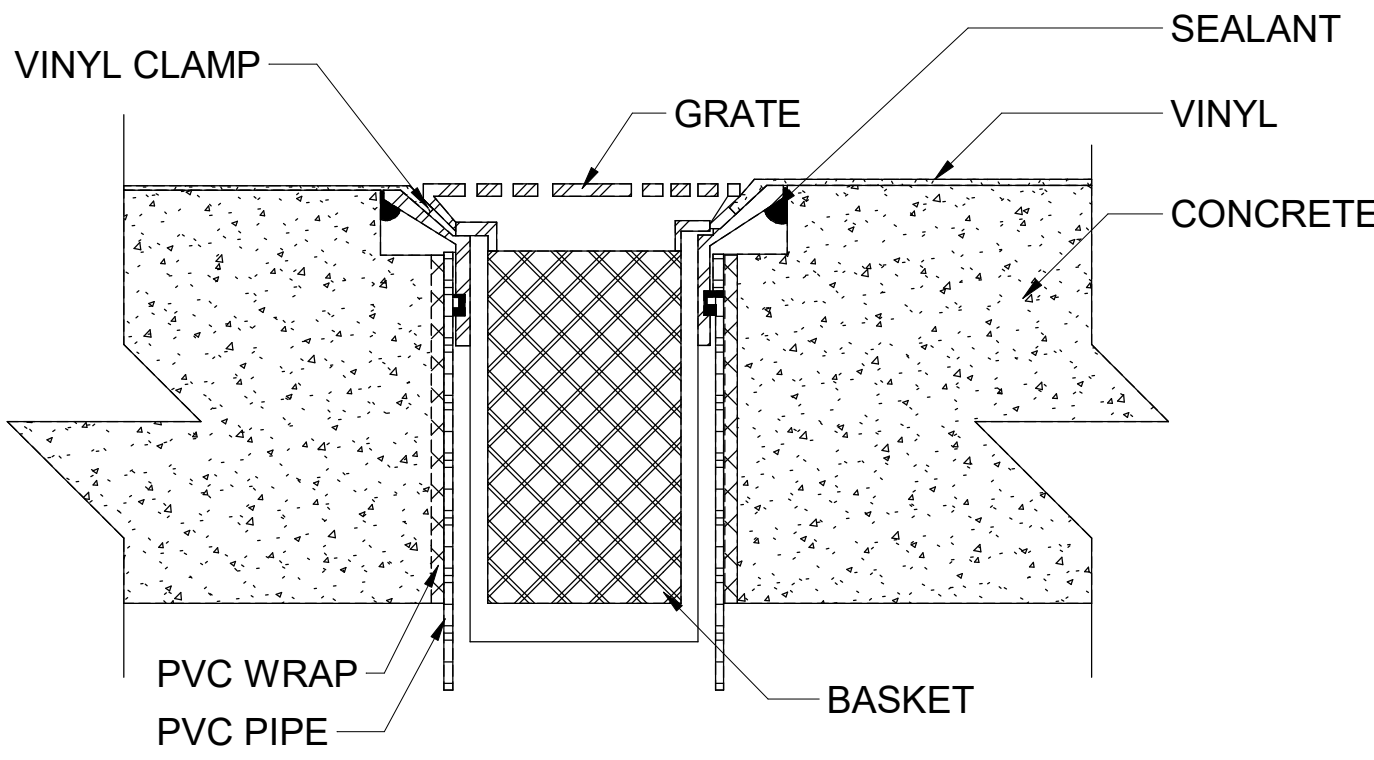

FLOOR/ BASKET WASTE DETAIL
NTS

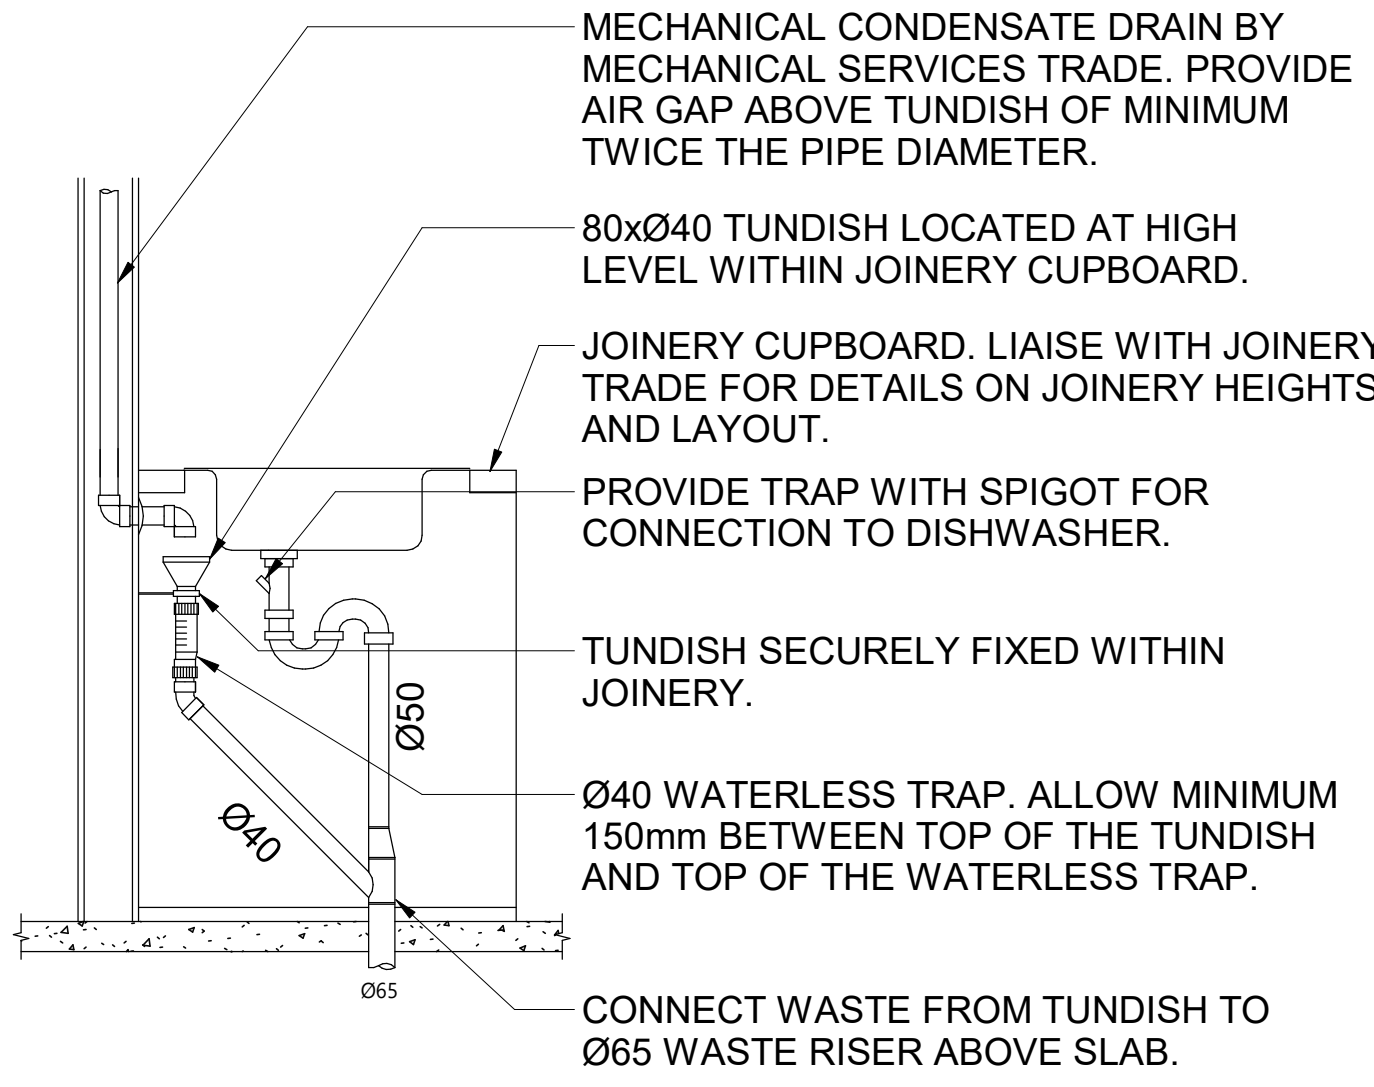

UNDERBENCH TUNDISH FOR A/C DISCHARGE
NTS

FOR TENDER

ALL DIMENSIONS SHOWN IN MM. DO NOT SCALE FROM DRAWINGS.
DIMENSIONS TAKE PRECEDENCE. IF IN DOUBT REFER TO HK SOLUTIONS.

T1	ISSUE FOR TENDER	17.06.2026	MC	HKS
REV.	DESCRIPTION	DATE	INT.	COMPANY
	REVISIONS			



ENGINEERING
PROJECT MANAGEMENT
DARWIN, GEELONG,
CAIRNS, TOWNSVILLE,
PERTH, BALLARAT
admin@hksolutions.com.au
www.hksolutions.com.au

Conditions of use. This document may only be used by
Harris Kmon Solutions clients for the purpose for which
it was prepared and must not be used by any other
person or for any other purpose.

SPORTS

DRAWN	AL
CHECKED	MC
DESIGNED	MC
CHECKED	LM
APPROVED	
THIS DRAWING MUST NOT BE USED FOR CONSTRUCTION UNLESS SIGNED AS APPROVED	

STAGE 1
ROCKHAMPTON SPORTS PRECINCT - PUBLIC AMENITIES BLOCK
554-700 YAAMBA ROAD, NORMAN GARDEN - 4701
DETAILS

PAGE No	PROJECT No - DRAWING No	DISCIPLINE	REV.	SHEET SIZE
10 of 06	25015-H-PAM-300	HYDRAULIC	T1	A1

DRAWINGS TO BE PRINTED IN COLOUR