
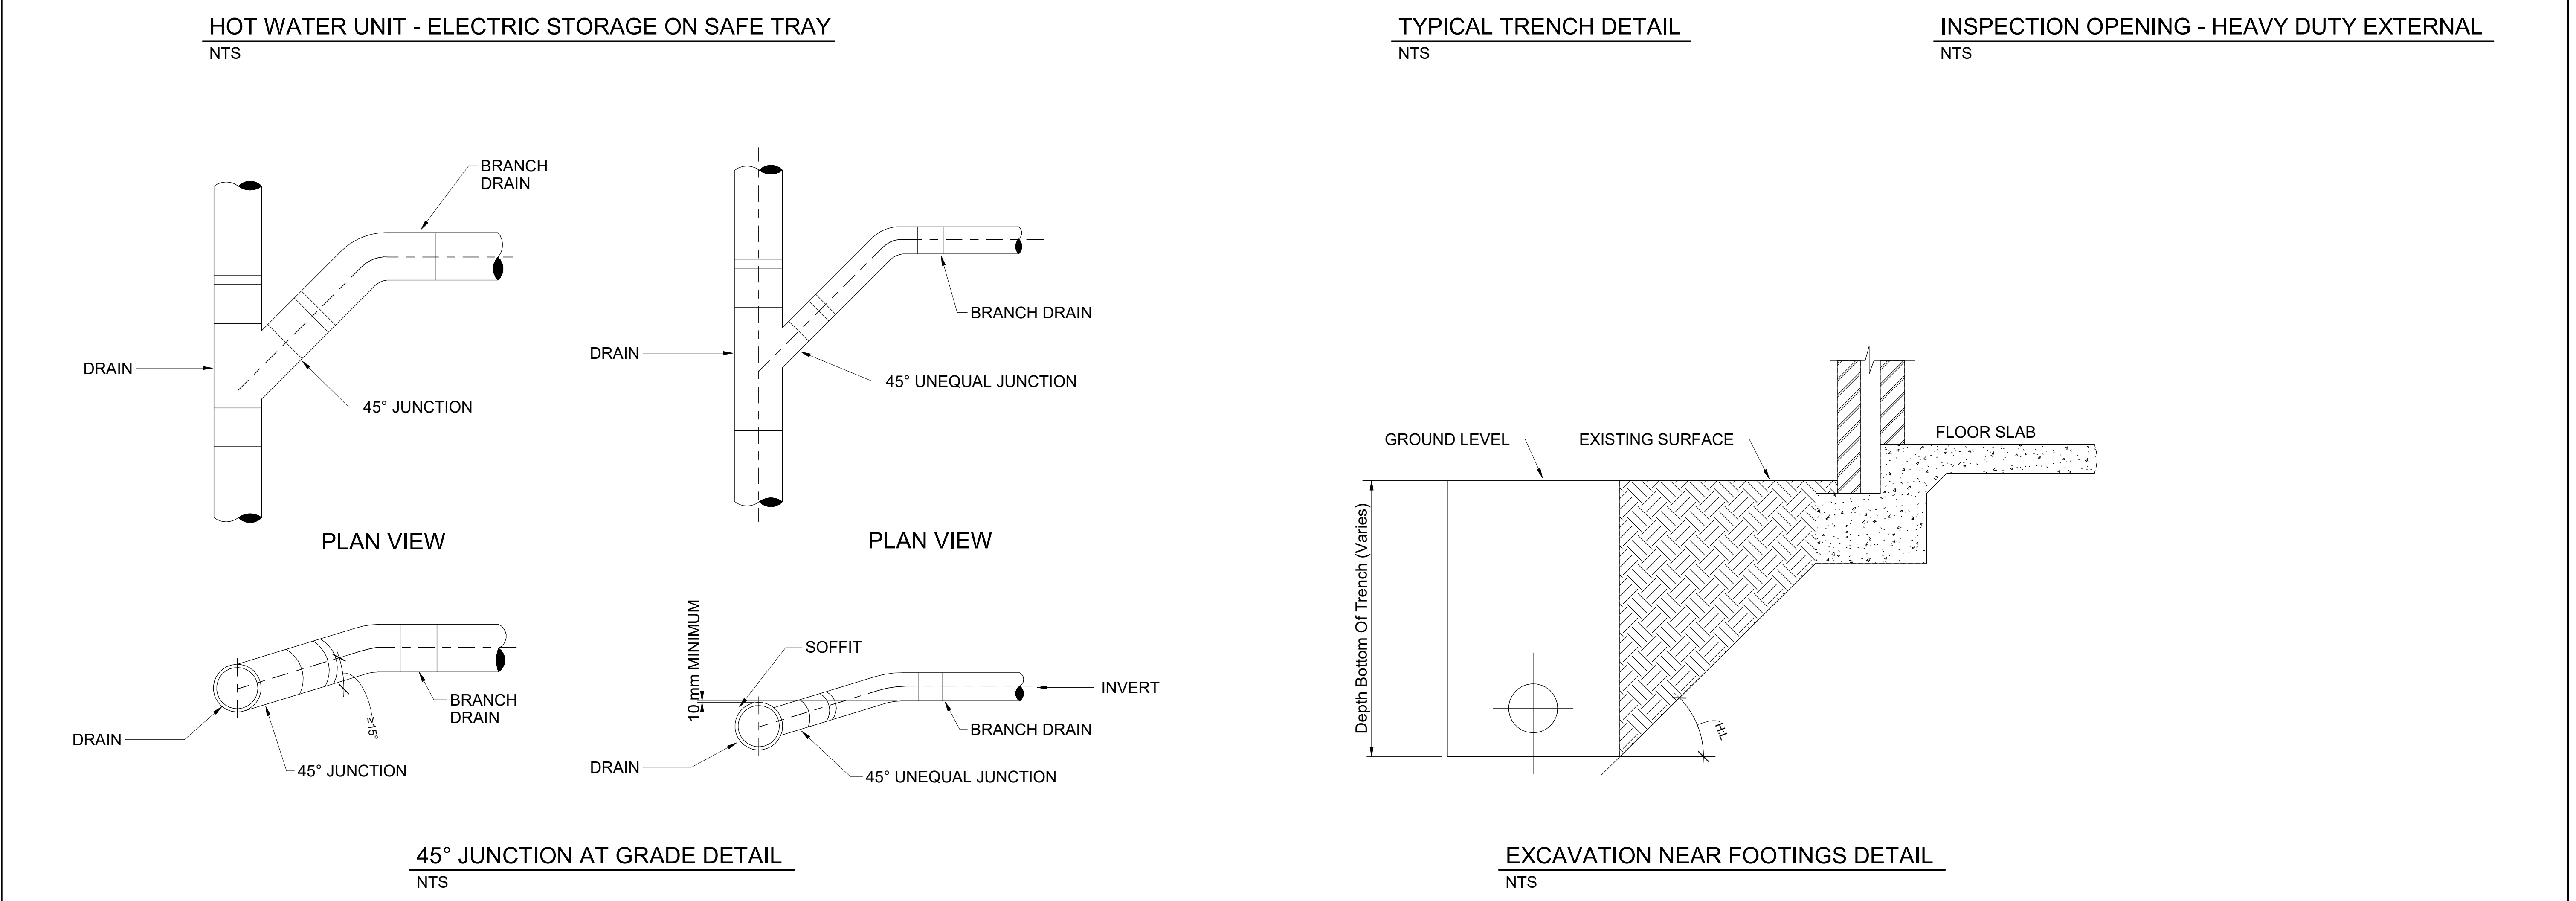


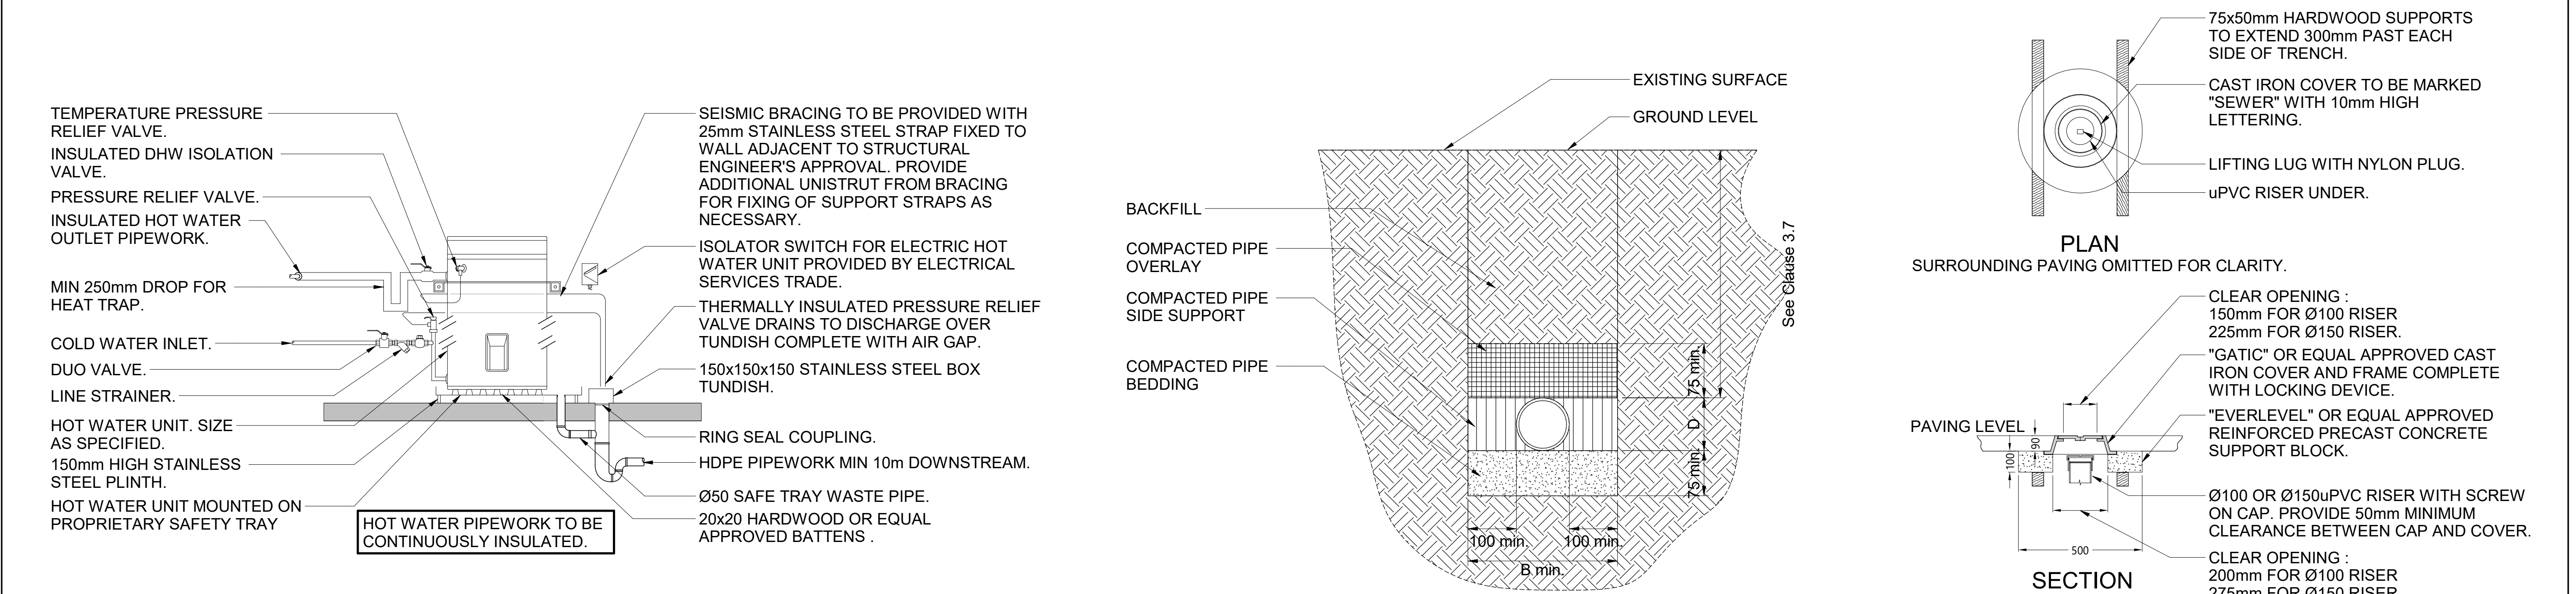

ALL DIMENSIONS SHOWN IN MM. DO NOT SCALE FROM DRAWINGS.
DIMENSIONS TAKE PRECEDENCE. IF IN DOUBT REFER TO HK SOLUTIONS.

T1	ISSUE FOR TENDER		17.06.2026	MC	HKS	 ENGINEERING PROJECT MANAGEMENT DARWIN, GEELONG, CAIRNS, TOWNSVILLE, PERTH, BALLARAT admin@hksolutions.com.au www.hksolutions.com.au
	REV.	DESCRIPTION	DATE	INT.	COMPANY	Conditions of use. This document may only be used by Harris Kmon Solutions clients for the purpose for which it was prepared and must not be used by any other person or for any other purpose.
REVISIONS						

SPORTS

DRAWN	AL
CHECKED	MC
DESIGNED	MC
CHECKED	LM
APPROVED	

THIS DRAWING MUST NOT BE USED FOR CONSTRUCTION UNLESS SIGNED AS APPROVED

STAGE 1
ROCKHAMPTON SPORTS PRECINCT - PUBLIC AMENITIES BLOCK
554-700 YAAMBA ROAD, NORMAN GARDEN - 4701
DETAILS

PAGE No	PROJECT No - DRAWING No	DISCIPLINE	REV.	SHEET SIZE
10 of 06	25015-H-PAM-301	HYDRAULIC	T1	A1

FOR TENDER

DRAWINGS TO BE PRINTED IN COLOUR