


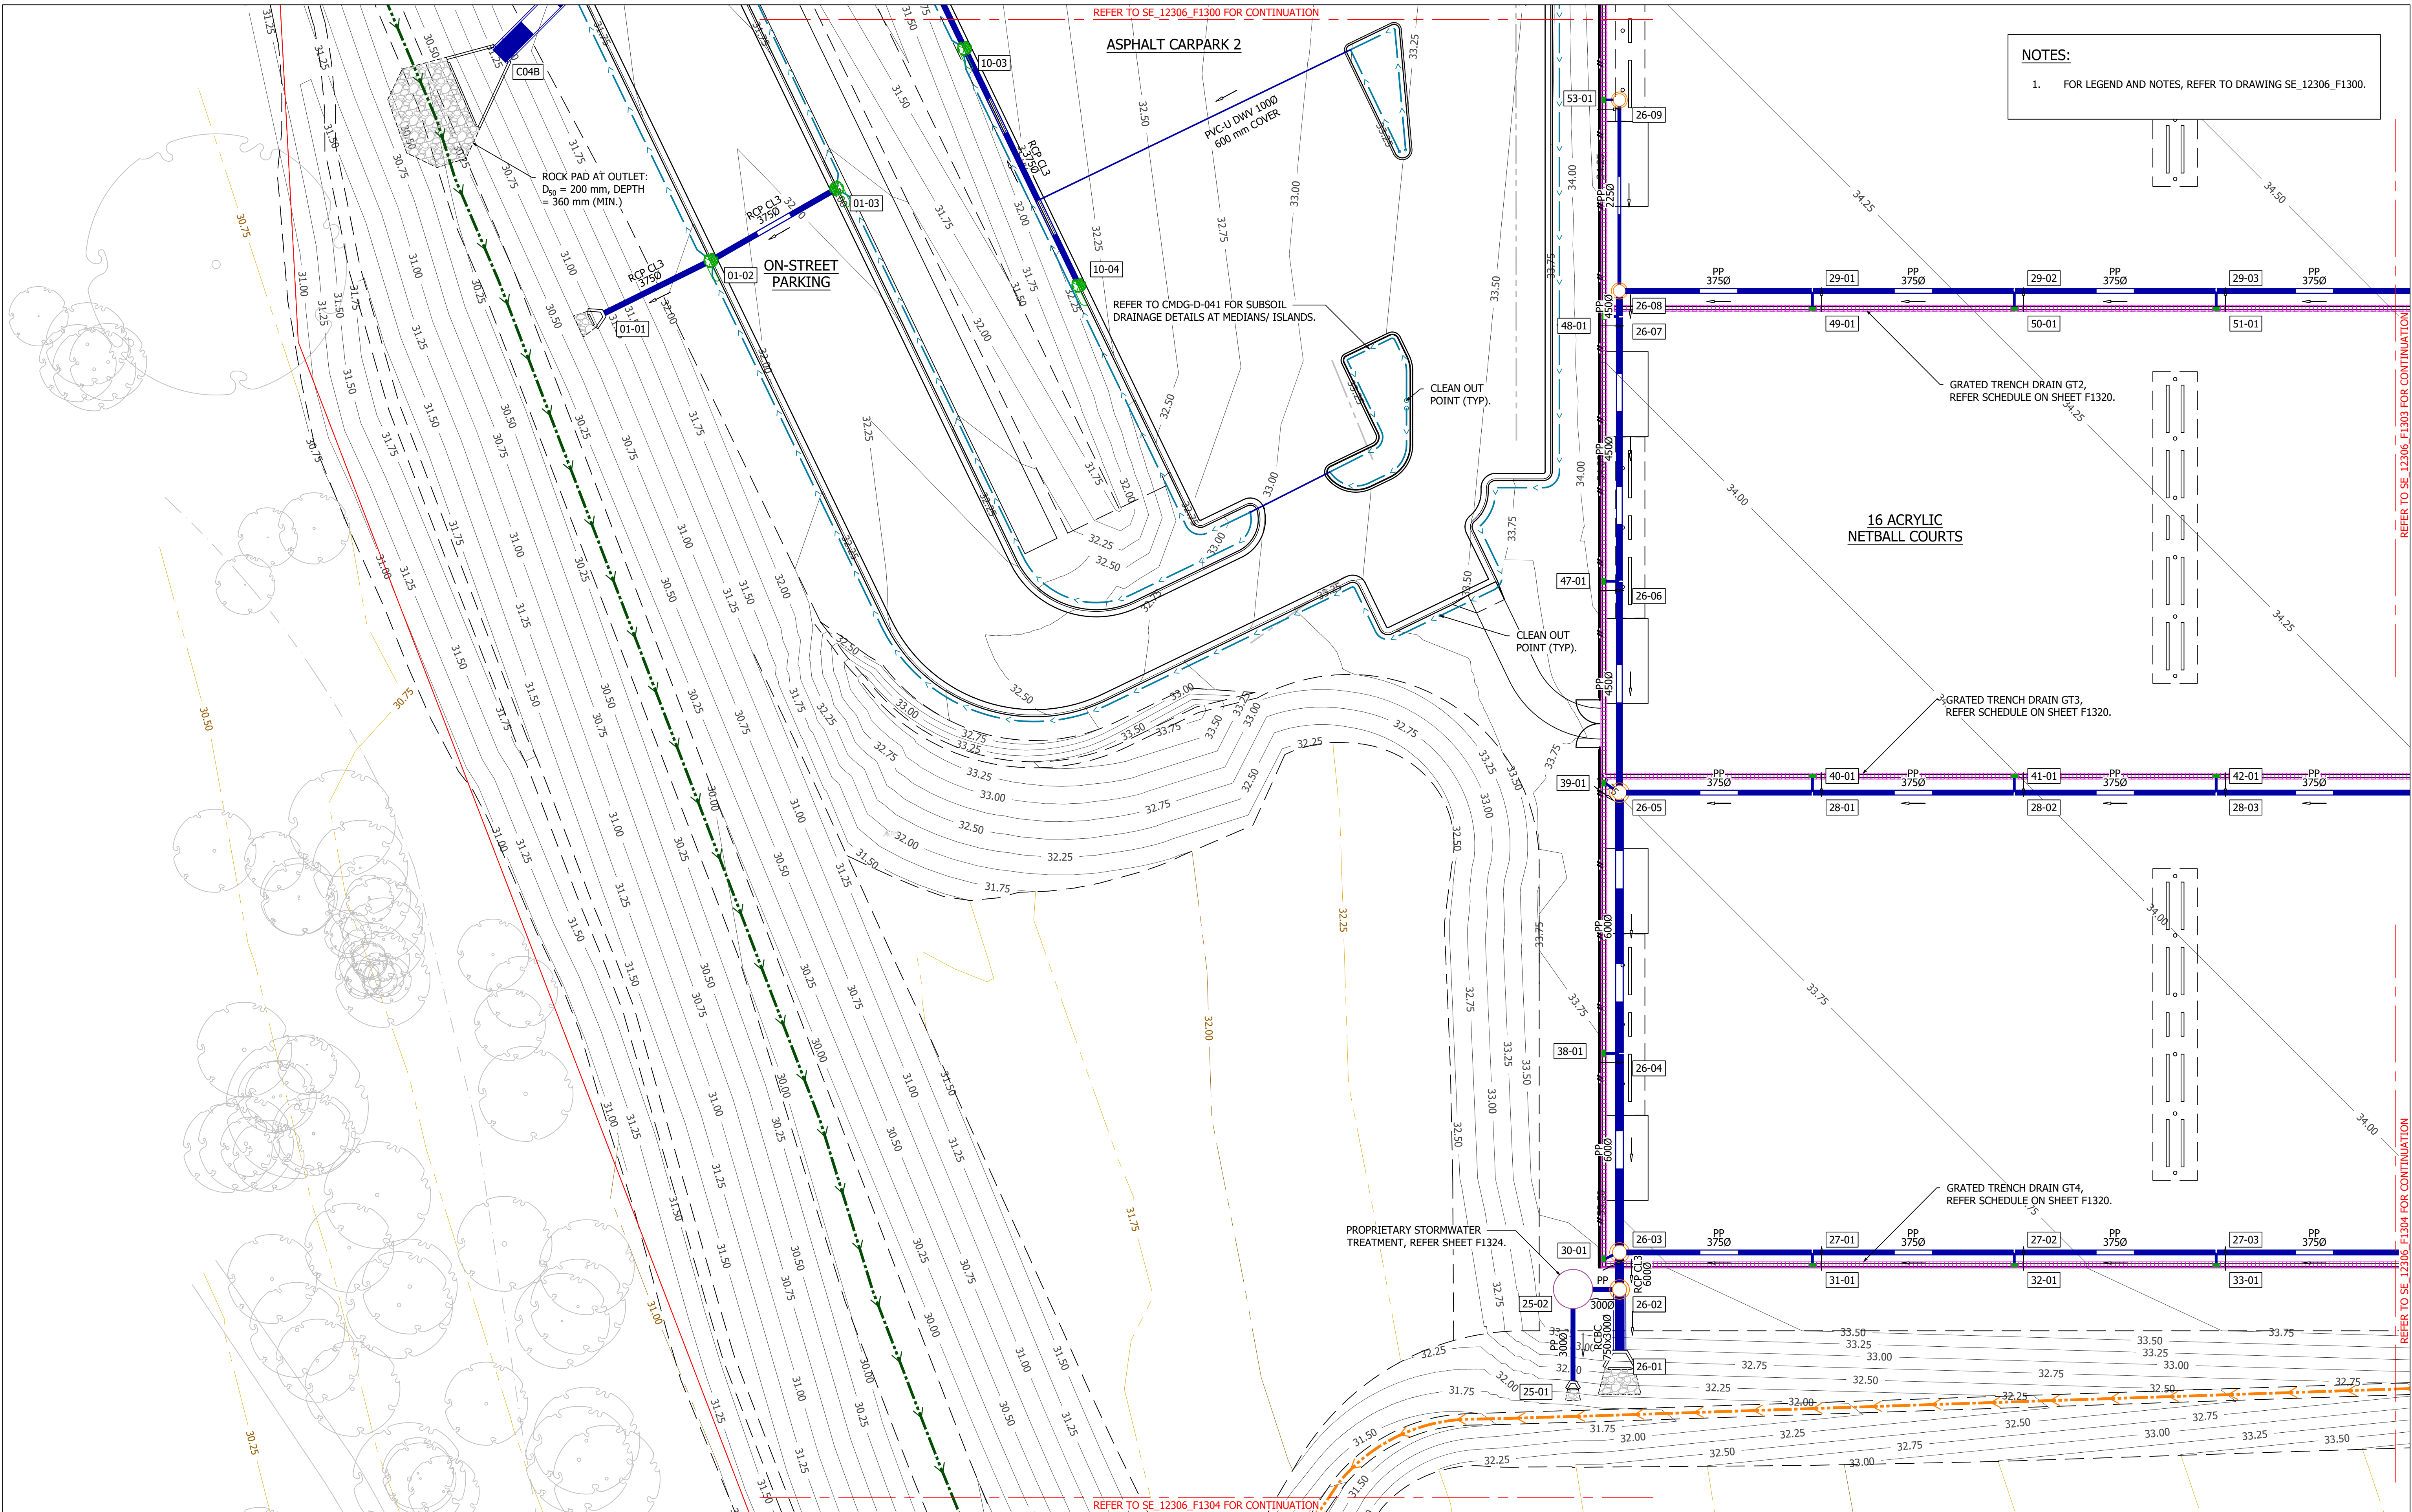

NOTES:
1. FOR LEGEND AND NOTES, REFER TO DRAWING SE_12306_F1300.

WARNING
BEWARE OF UNDERGROUND SERVICES
THE LOCATION OF UNDERGROUND SERVICES ARE APPROXIMATE ONLY. IT IS THE RESPONSIBILITY OF THE CONTRACTOR TO PROVE THEIR EXACT POSITION ON SITE. NO GUARANTEE IS GIVEN THAT ALL EXISTING SERVICES ARE SHOWN.

WARNING
OVERHEAD ELECTRICITY IN VICINITY OF WORKS
NOT FOR CONSTRUCTION



SPORTENG™

T1	17/06/26	TPC	JZV	JDH	ISSUE FOR TENDER
Issue	Date	By	Chkd	Appd	Description

Job Title
**ROCKHAMPTON
NETBALL CENTRE**

Drawing Title
**STORMWATER DRAINAGE
LAYOUT PLAN
SHEET 3**

01m 5m 10m 15m 20m
SCALE 1:250 @ A1
Discipline
CIVIL AND FIELD OF PLAY
Drawing Status
ISSUE FOR TENDER
Drawing Number
SE_12306_F1302
Issue
T1