


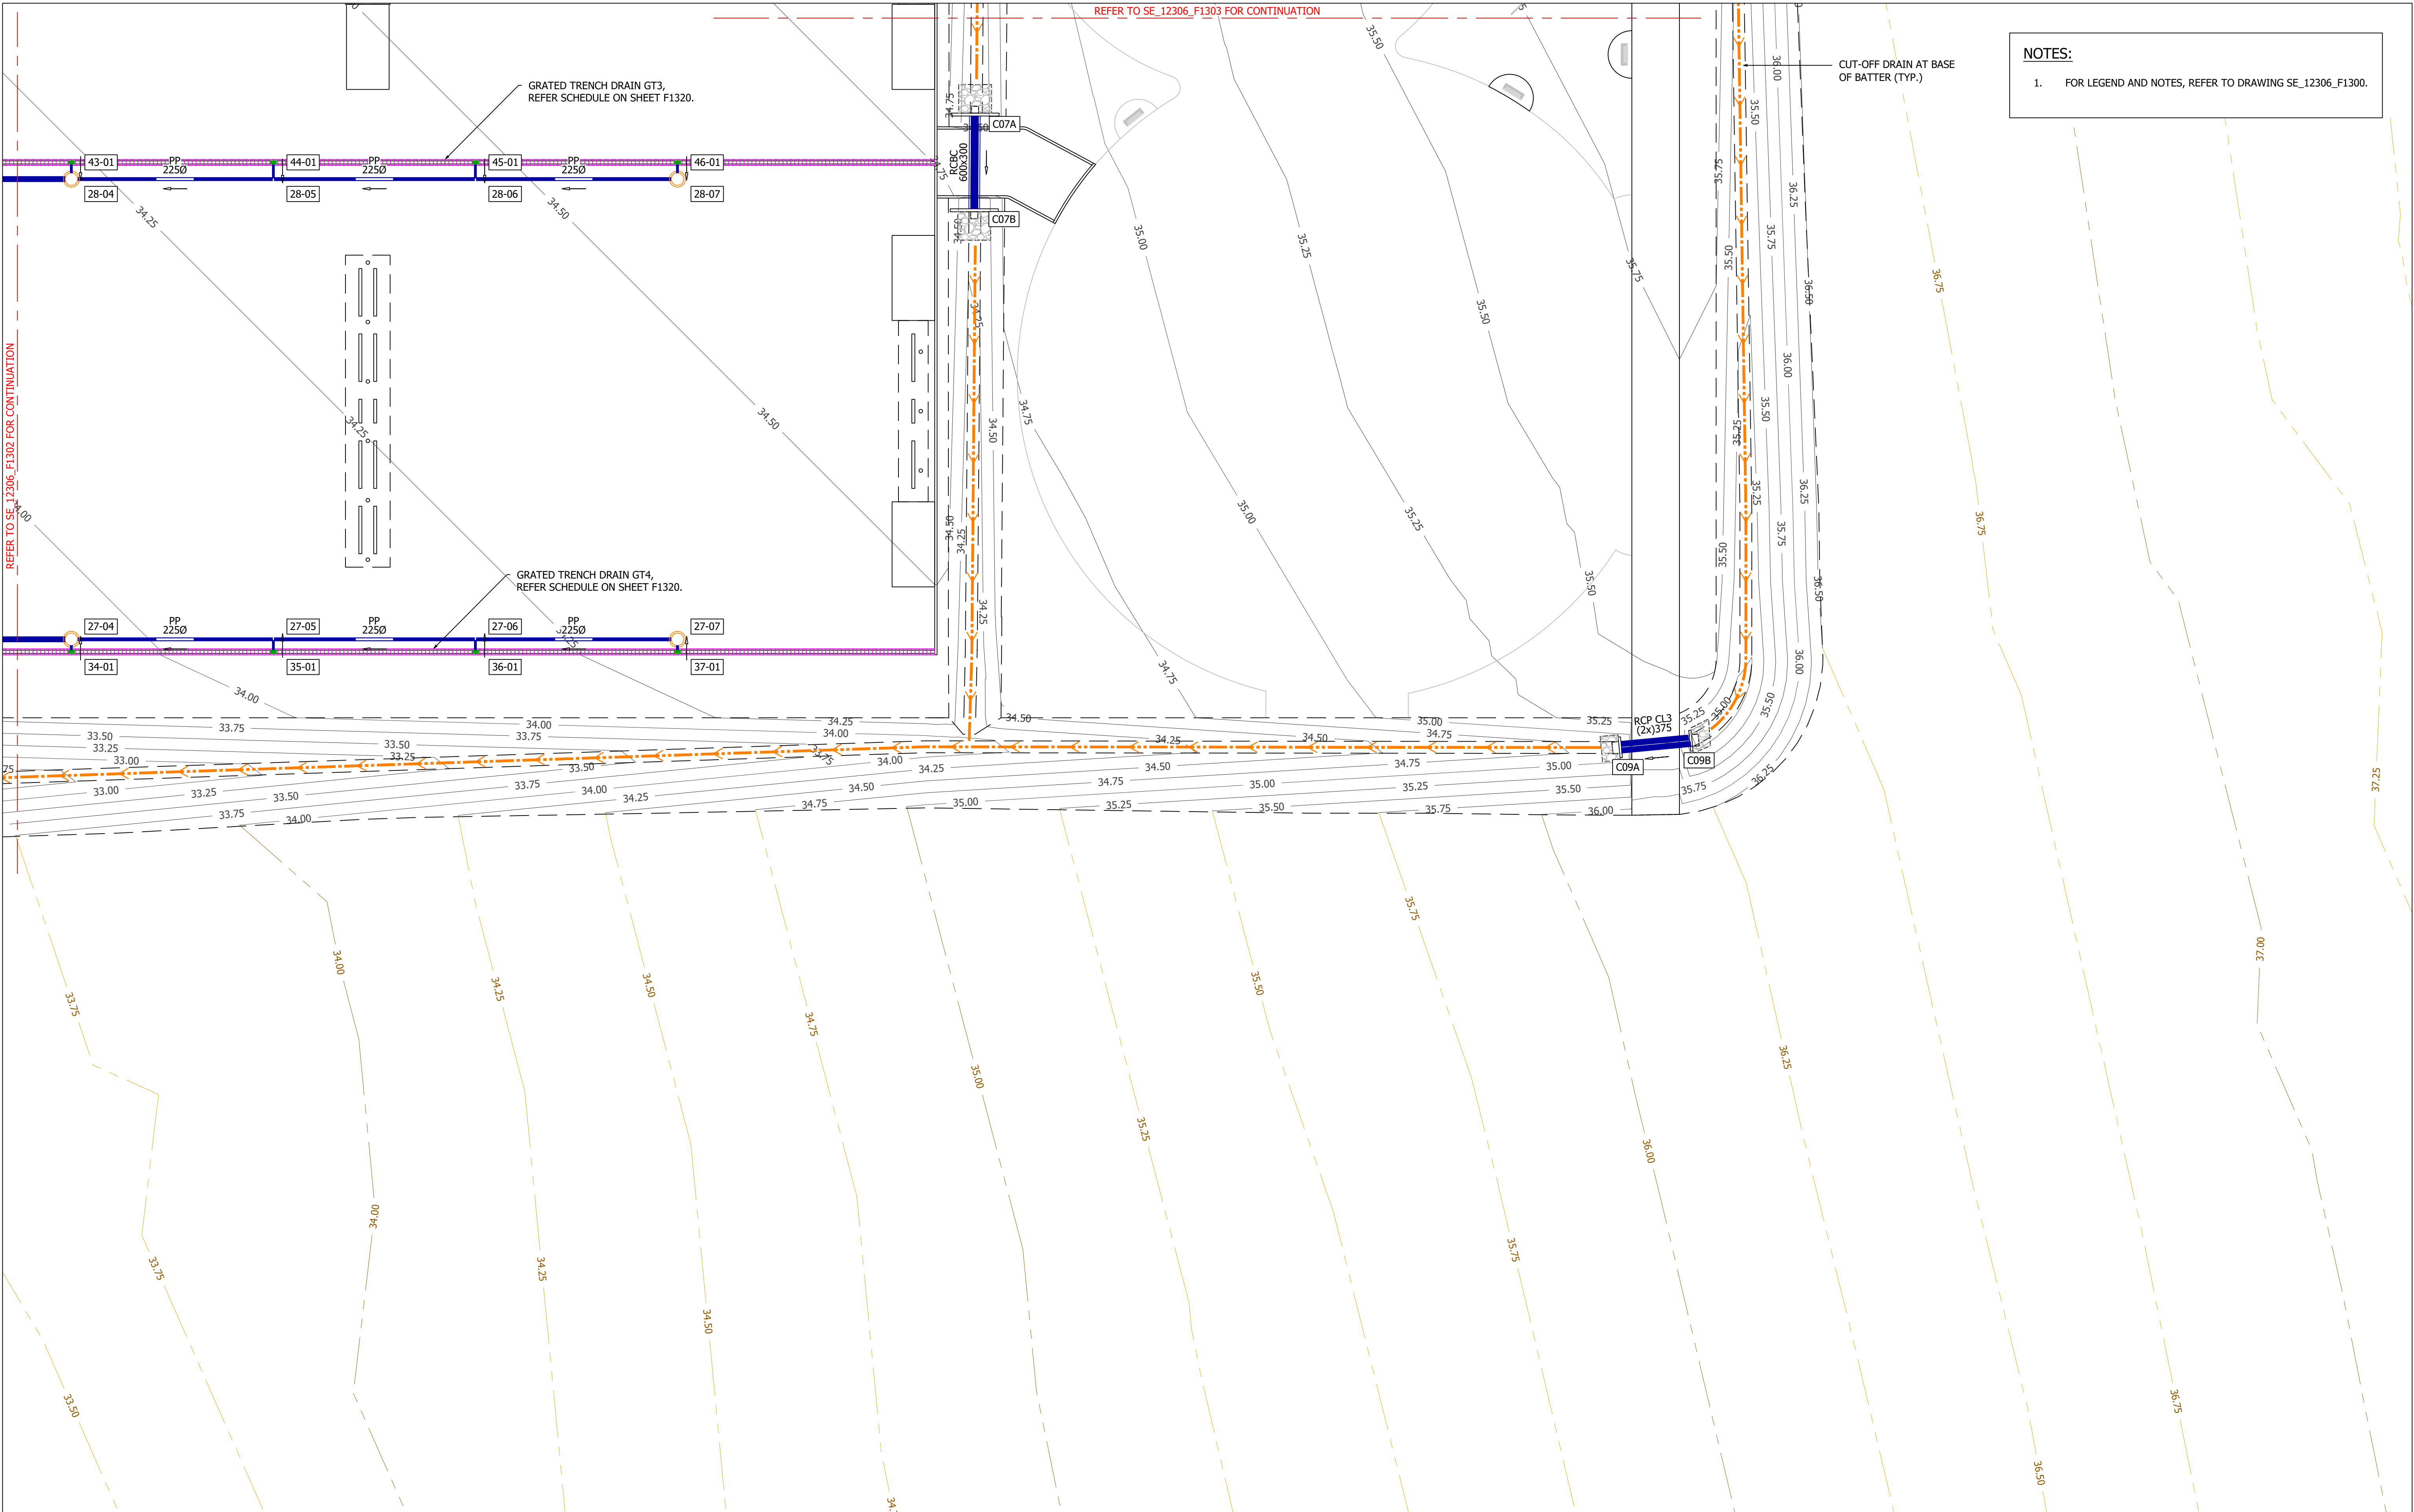

WARNING
BEWARE OF UNDERGROUND SERVICES
THE LOCATION OF UNDERGROUND SERVICES ARE APPROXIMATE ONLY. IT IS THE RESPONSIBILITY OF THE CONTRACTOR TO PROVE THEIR EXACT POSITION ON SITE. NO GUARANTEE IS GIVEN THAT ALL EXISTING SERVICES ARE SHOWN.

WARNING
OVERHEAD ELECTRICITY IN VICINITY OF WORKS

NOT FOR CONSTRUCTION



T1	17/06/26	TPC	JZV	JDH	ISSUE FOR TENDER
Issue	Date	By	Chkd	Appd	Description

Job Title
**ROCKHAMPTON
NETBALL CENTRE**

Drawing Title
**STORMWATER DRAINAGE
LAYOUT PLAN
SHEET 5**

01m 5m 10m 15m 20m

SCALE 1:250 @ A1

Discipline
CIVIL AND FIELD OF PLAY

Drawing Status
ISSUE FOR TENDER

Drawing Number SE_12306_F1304	Issue T1
---	--------------------