

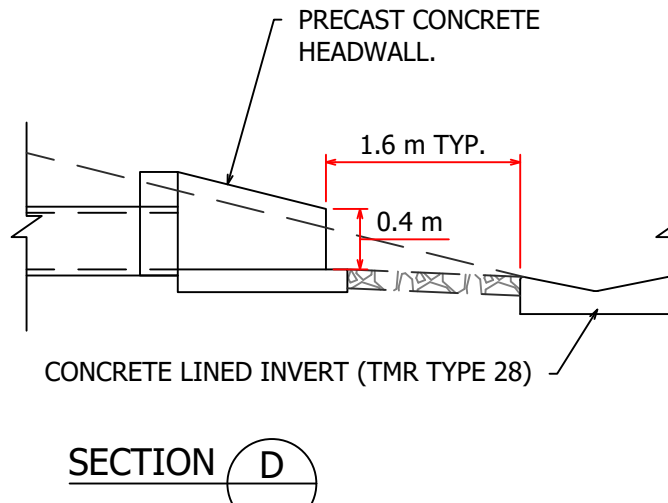
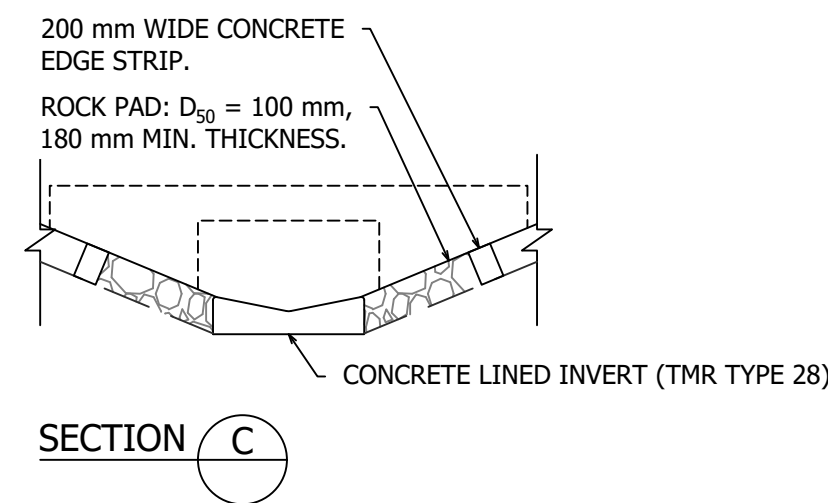
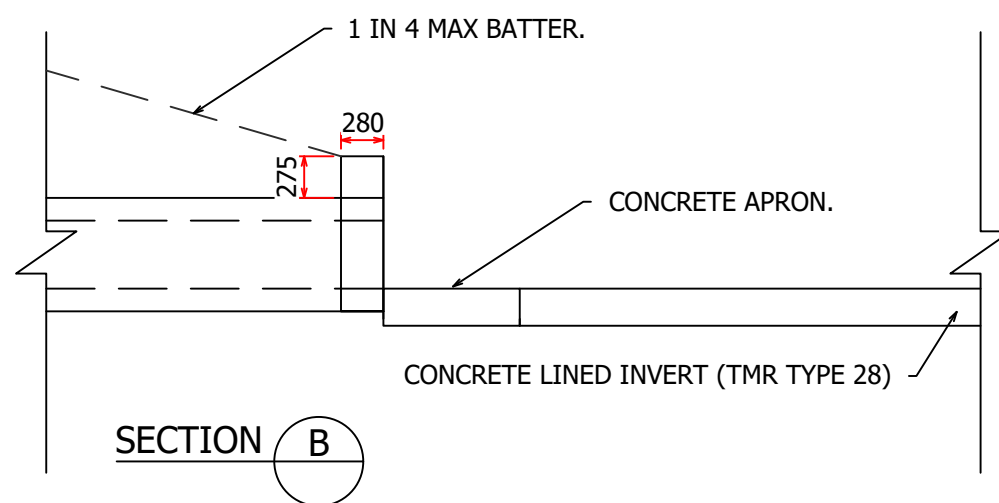
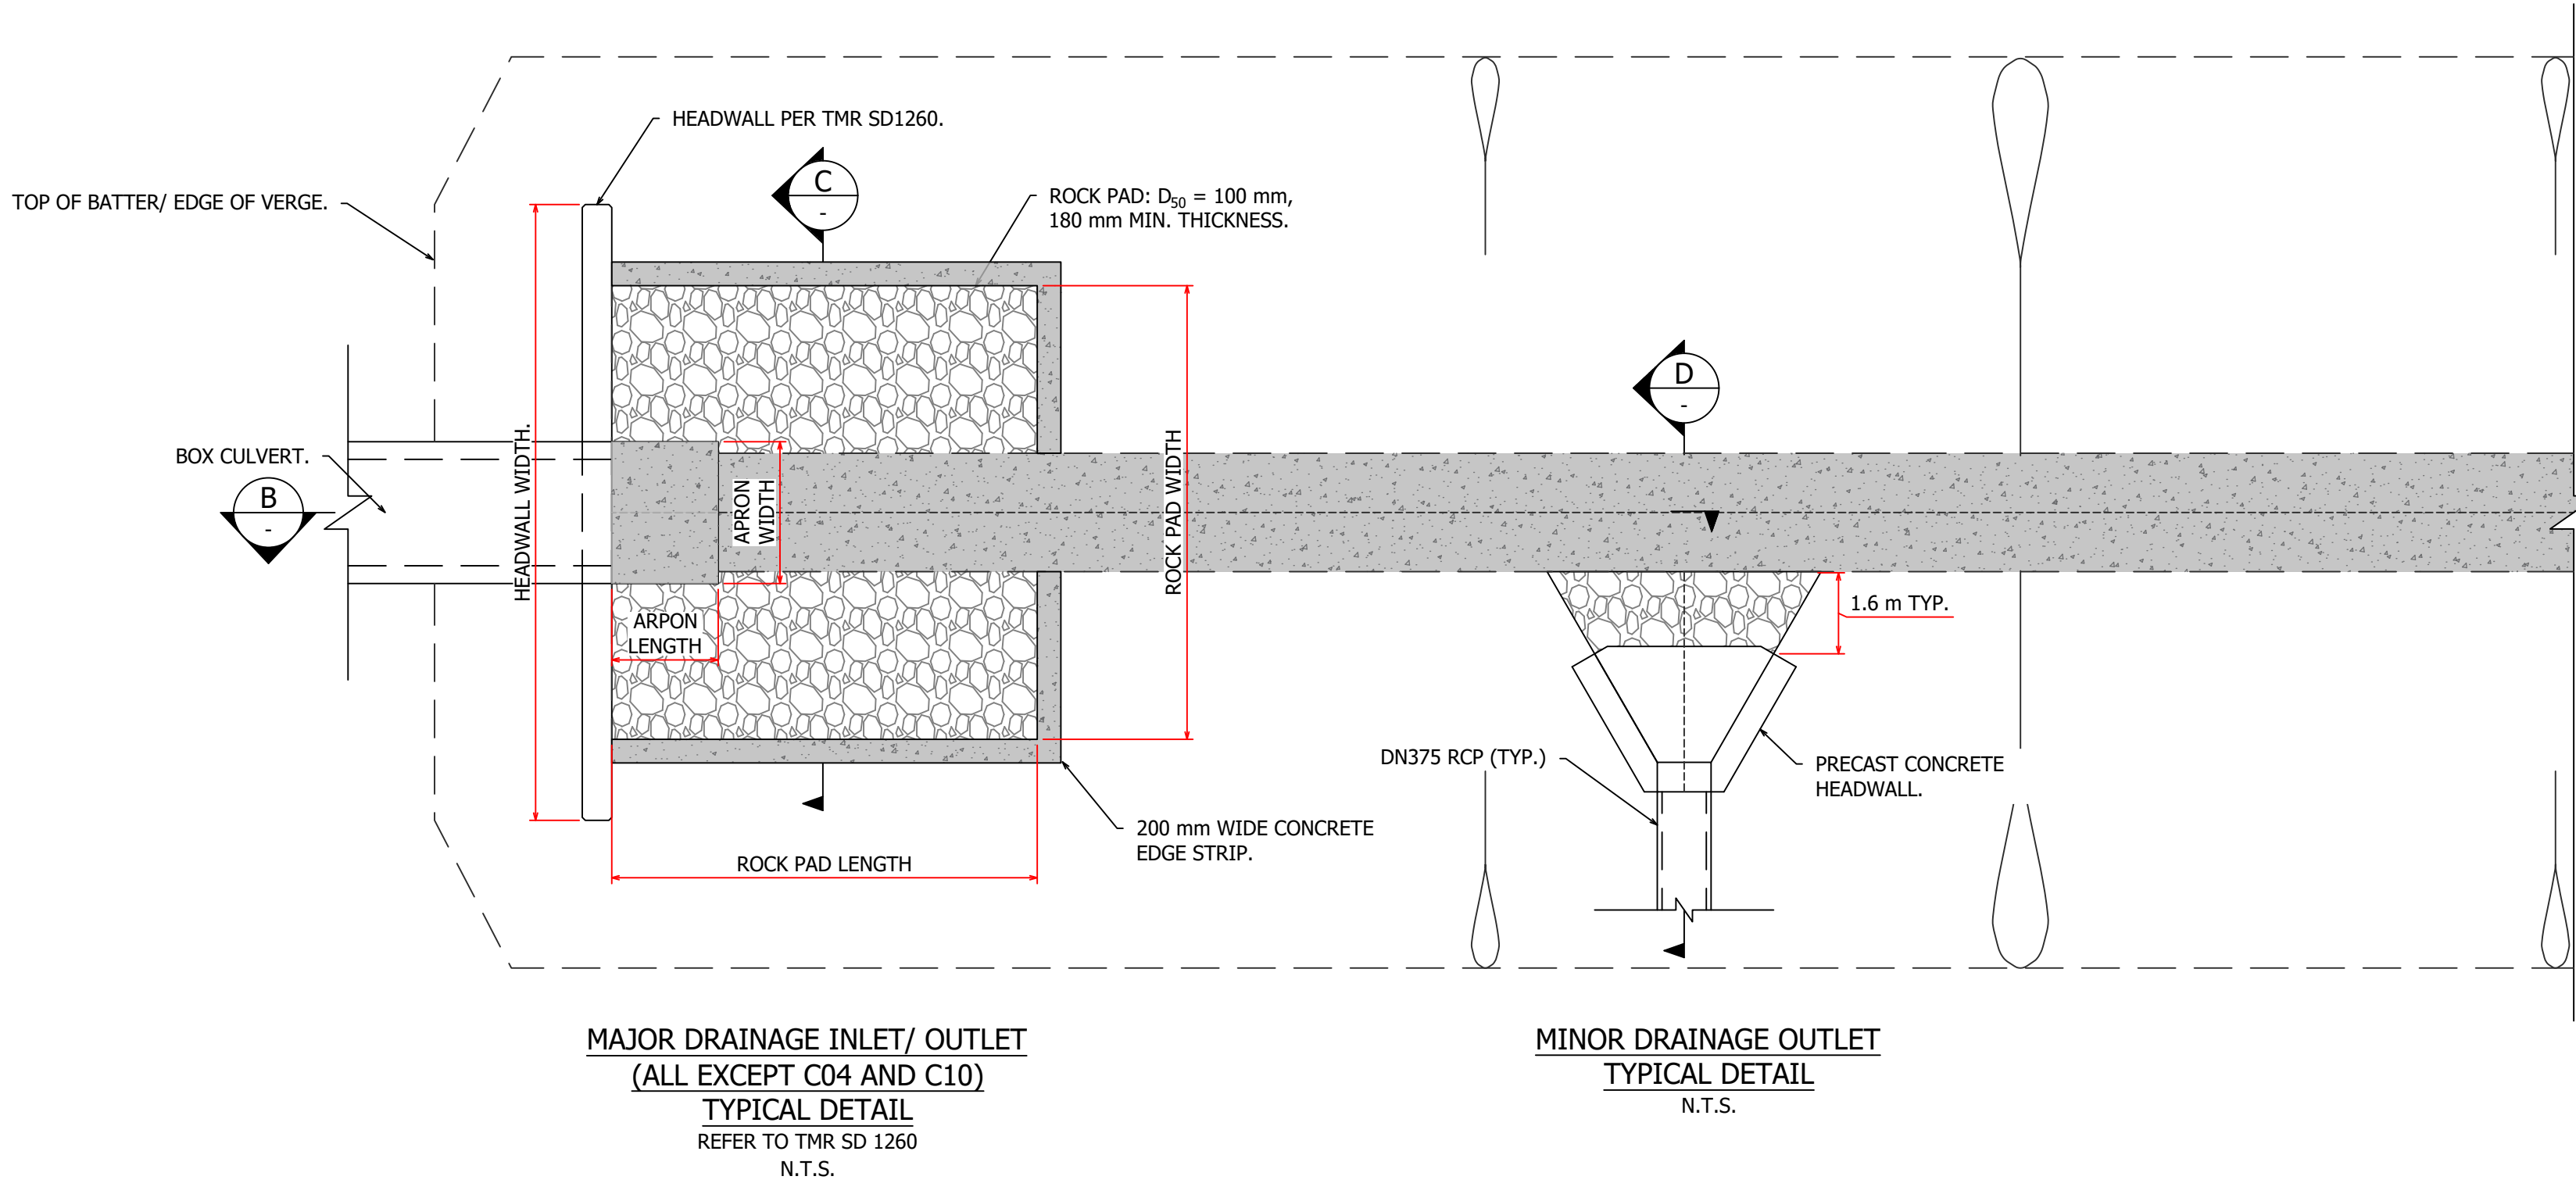


MAJOR DRAINAGE CULVERT INLET/OUTLET DIMENSIONS				
ID	RCBC	W1	W2	SKEW ANGLE
C04A	1500 x 600	3.84	2.86	22
C04B	1500 x 600	5.85	4.37	0
C10A	2700 x 1200	7.95	7.95	0
C10B	2700 x 1200	7.95	7.95	0

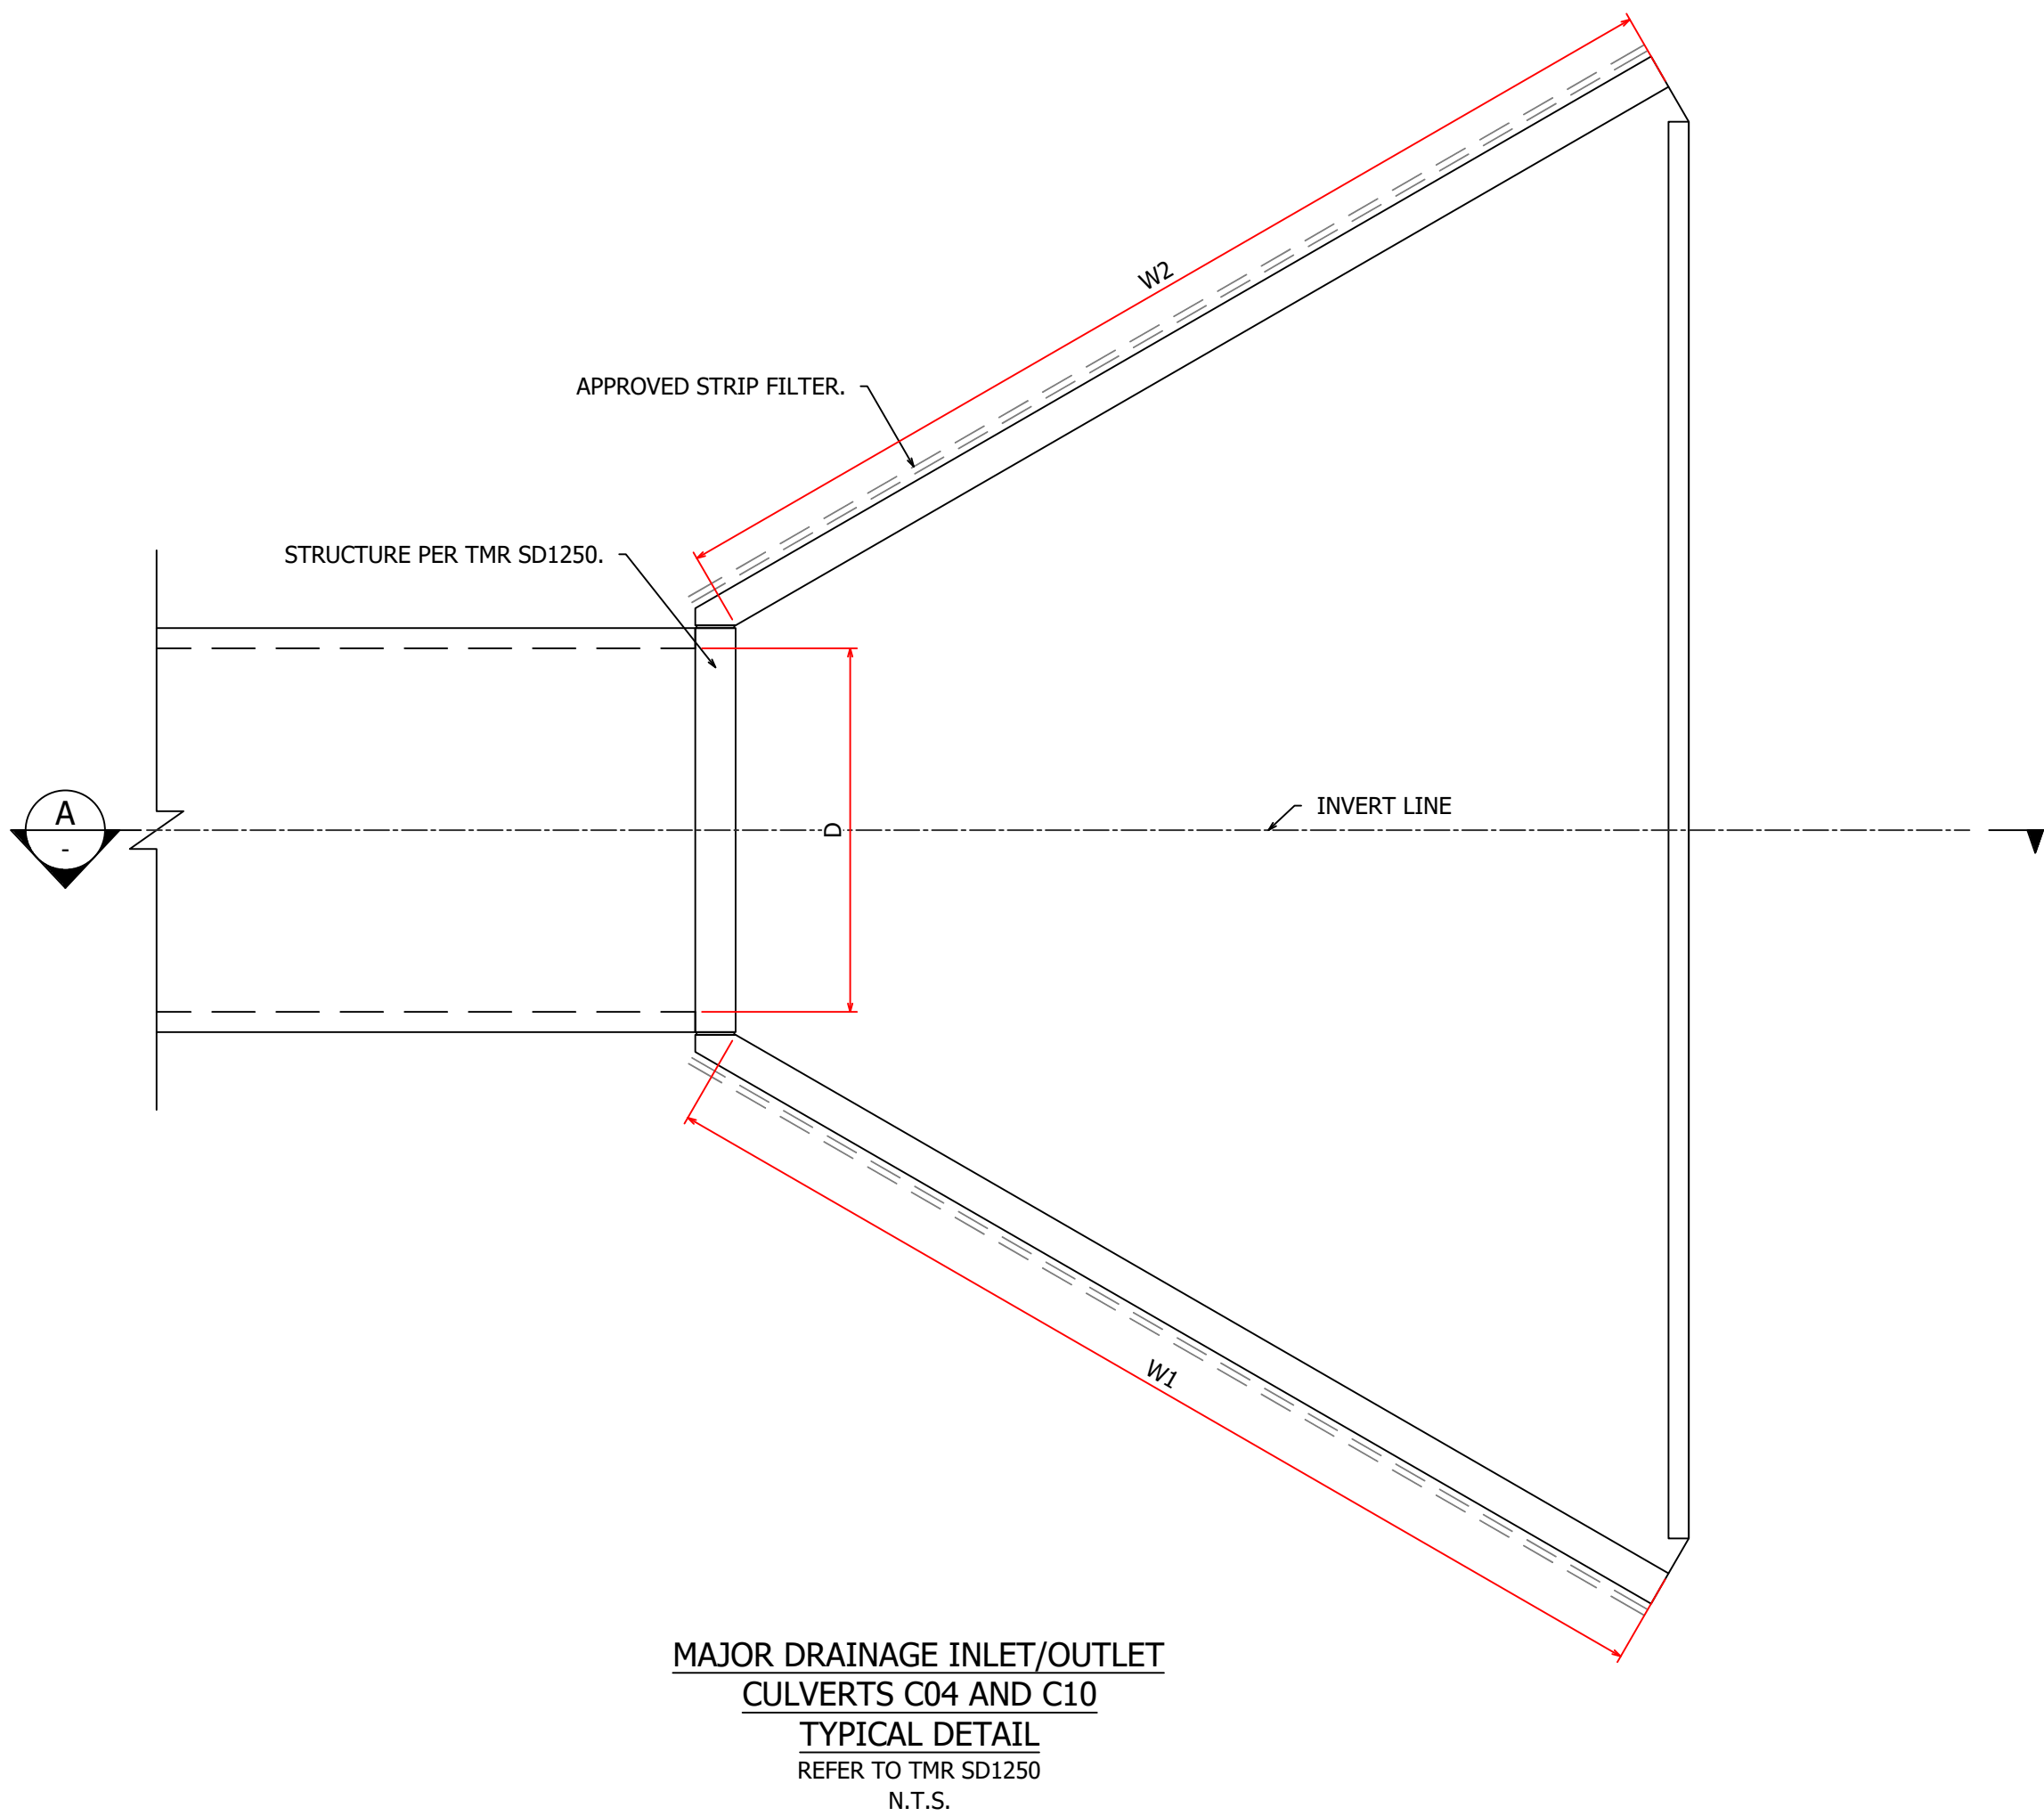

MAJOR DRAINAGE CULVERT INLET/OUTLET DIMENSIONS						
ID	RCBC	HEADWALL WIDTH	APRON WIDTH	APRON LENGTH	ROCK PAD WIDTH	ROCK PAD LENGTH
C01A	900 x 450	4.050	0.675	1.000	3.840	3.600
C01B	900 x 450	4.050	0.675	1.000	3.840	3.600
C02A	900 x 450	4.050	0.675	1.000	3.840	3.600
C02B	900 x 450	4.050	0.675	1.000	3.840	3.600
C03A	1200 x 600	5.400	0.900	1.200	5.880	7.200
C03B	1200 x 600	5.400	0.900	1.200	5.840	7.200
C05A	600 x 300	2.700	0.575	1.000	2.760	2.400
C05B	600 x 300	2.700	0.575	1.000	2.760	2.400
C06A	600 x 300	2.700	0.575	1.000	2.760	2.400
C06B	600 x 300	2.700	0.575	1.000	2.760	2.400
C07A	600 x 300	2.700	0.575	1.000	2.760	2.400
C07B	600 x 300	2.700	0.575	1.000	2.760	2.400
C08A	600 x 300	2.700	0.575	1.000	2.760	2.400
C08B	600 x 300	2.700	0.575	1.000	2.760	2.400

NOT FOR CONSTRUCTION

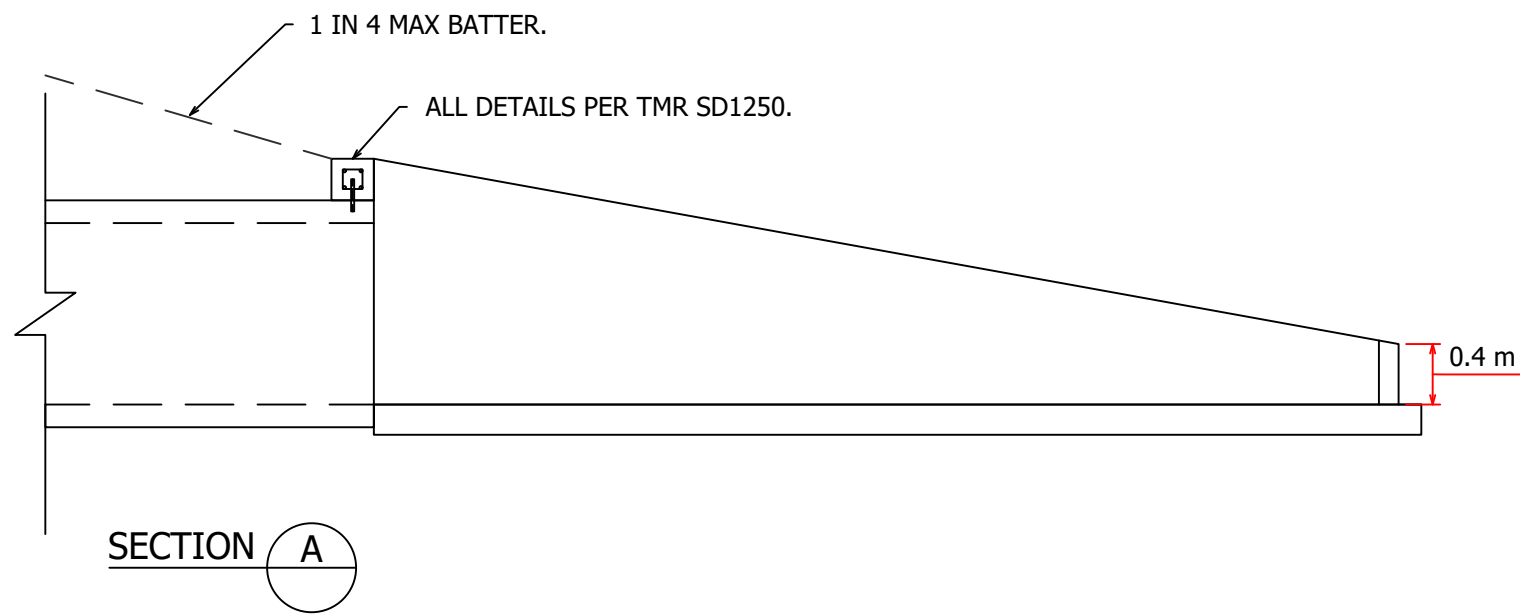

T1	17/06/26	TPC	JZV	JDH	ISSUE FOR TENDER
Issue	Date	By	Chkd	Appd	Description

Job Title
ROCKHAMPTON
NETBALL CENTRE

Drawing Title
STORMWATER DRAINAGE
DETAILS
SHEET 2

Discipline
CIVIL AND FIELD OF PLAY
Drawing Status
ISSUE FOR TENDER
Drawing Number
SE_12306_F1321

Issue
T1