




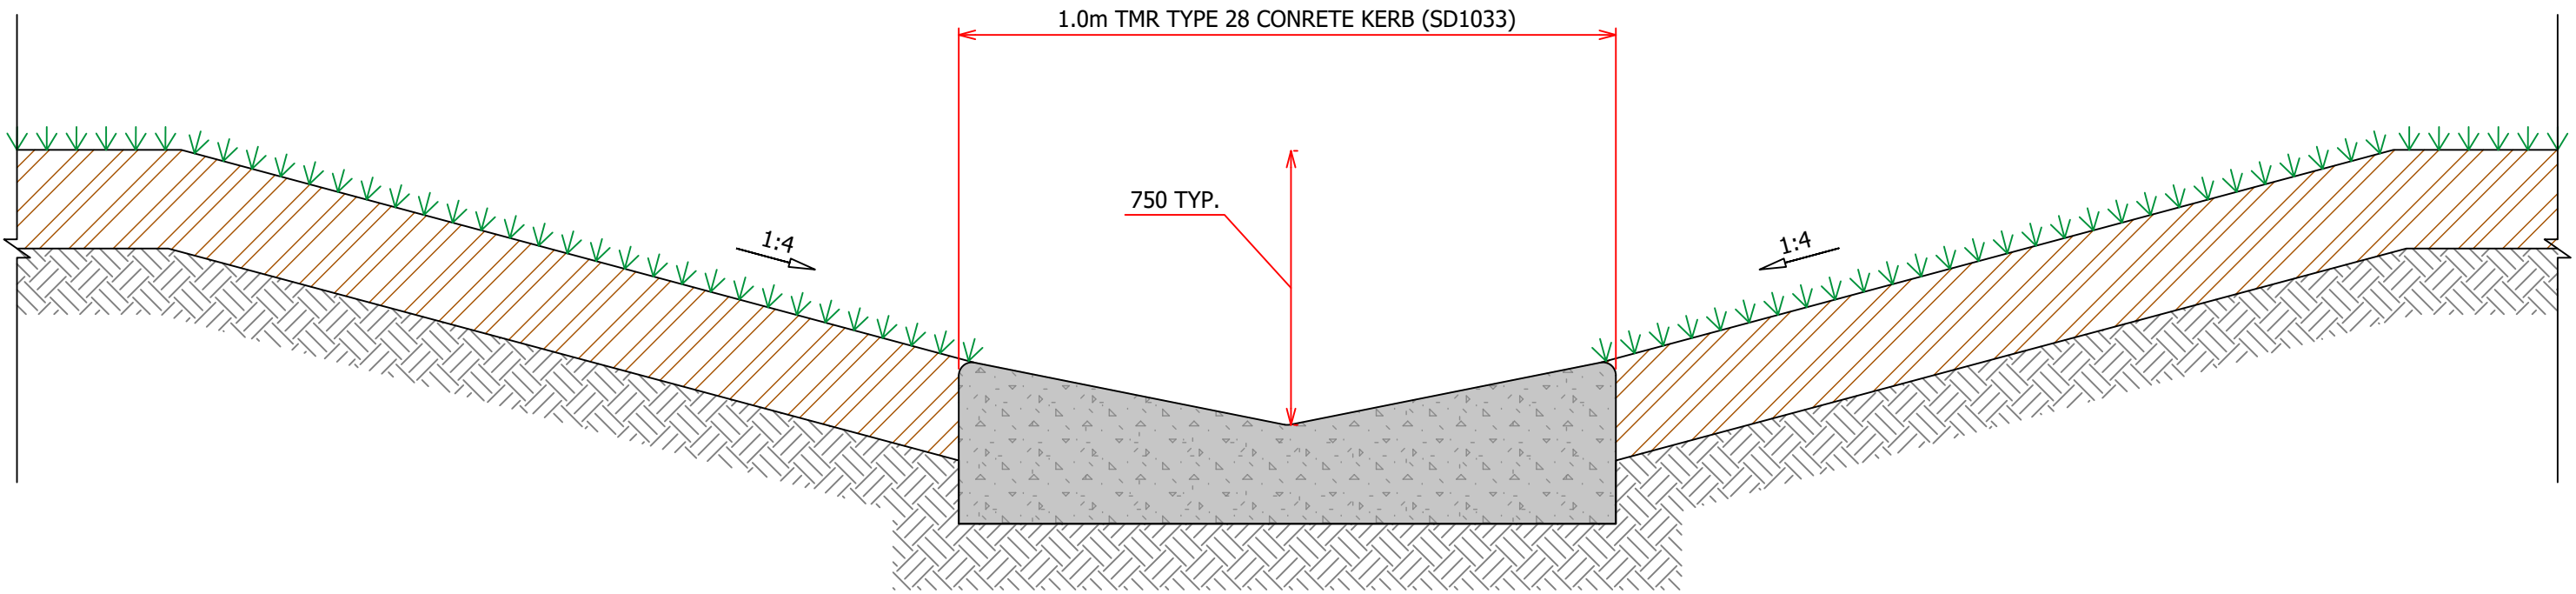

GRASSED SWALE WITH SPOON DRAIN
TYPICAL DETAIL
N.T.S

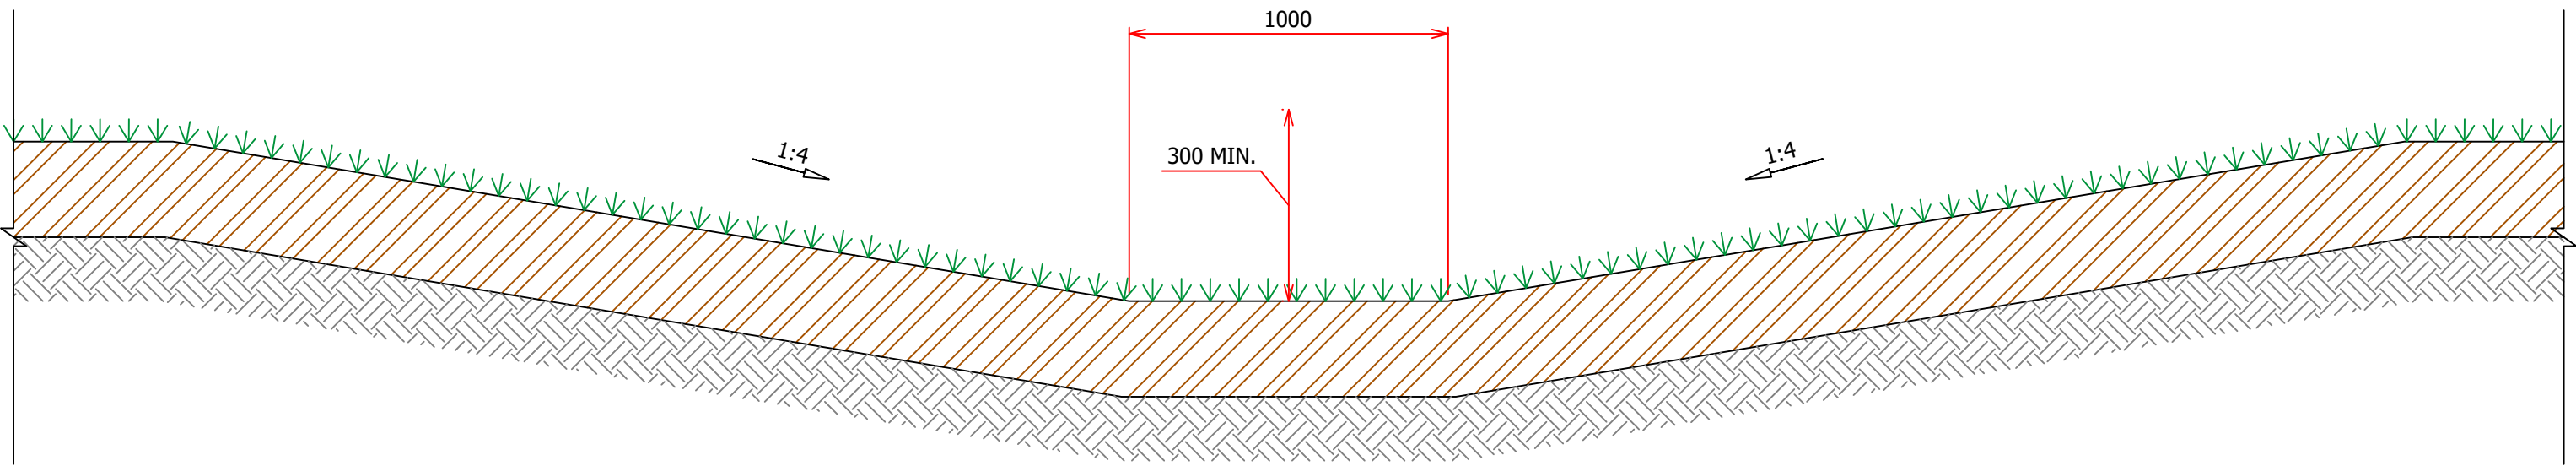

GRASSED SWALE TYPICAL DETAIL
N.T.S

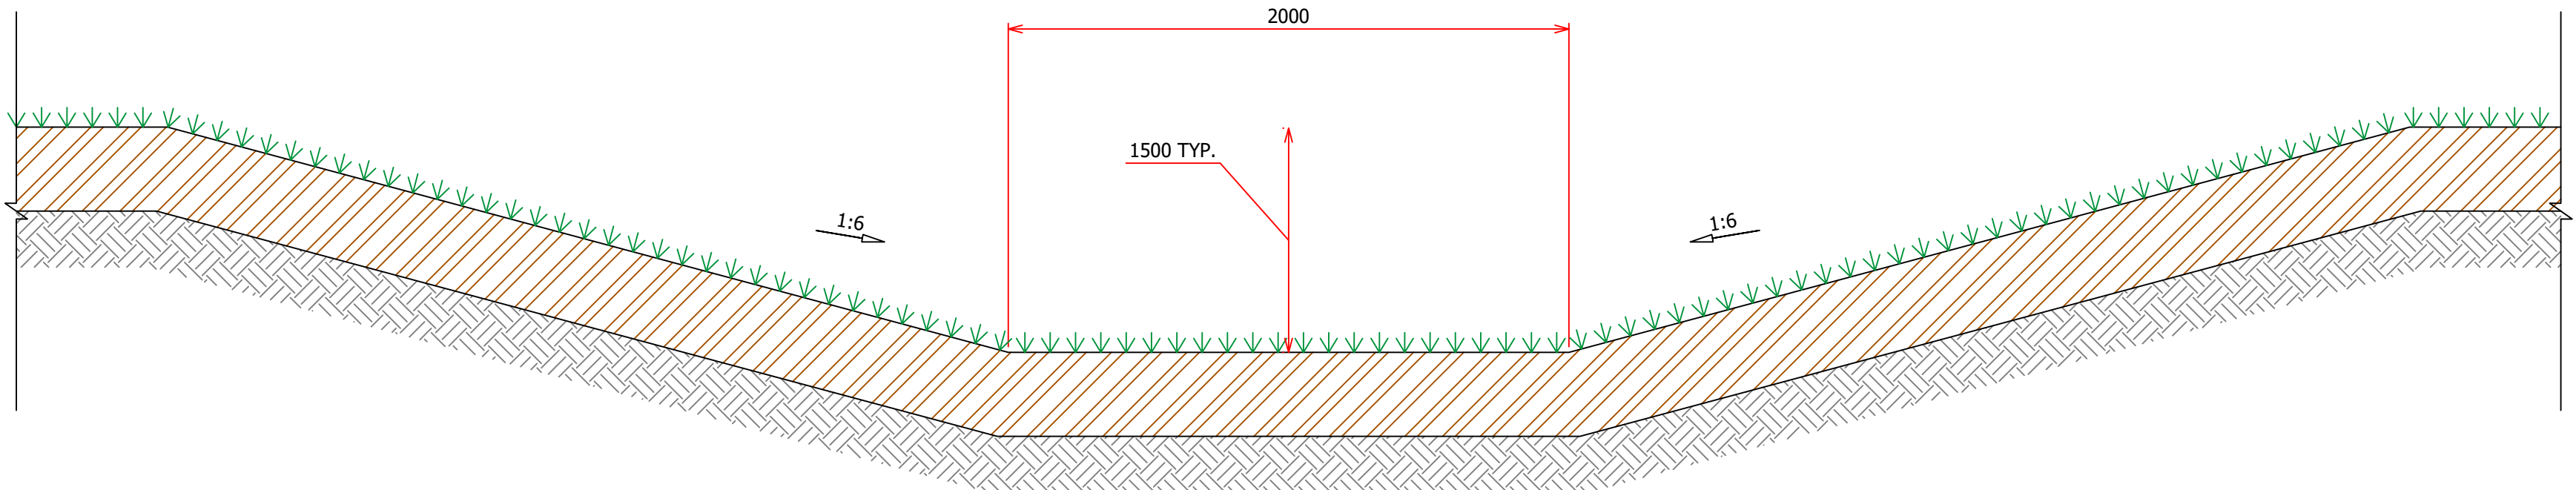

VEGETATED SWALE TYPICAL DETAIL
N.T.S

NOT FOR CONSTRUCTION



SPORTENG™

T1	17/06/26	TPC	JZV	JDH	ISSUE FOR TENDER
Issue	Date	By	Chkd	Appd	Description

Job Title
ROCKHAMPTON
NETBALL CENTRE

Drawing Title
STORMWATER DRAINAGE
DETAILS
SHEET 3

Discipline	CIVIL AND FIELD OF PLAY
Drawing Status	ISSUE FOR TENDER
Drawing Number	SE_12306_F1322
Issue	T1