




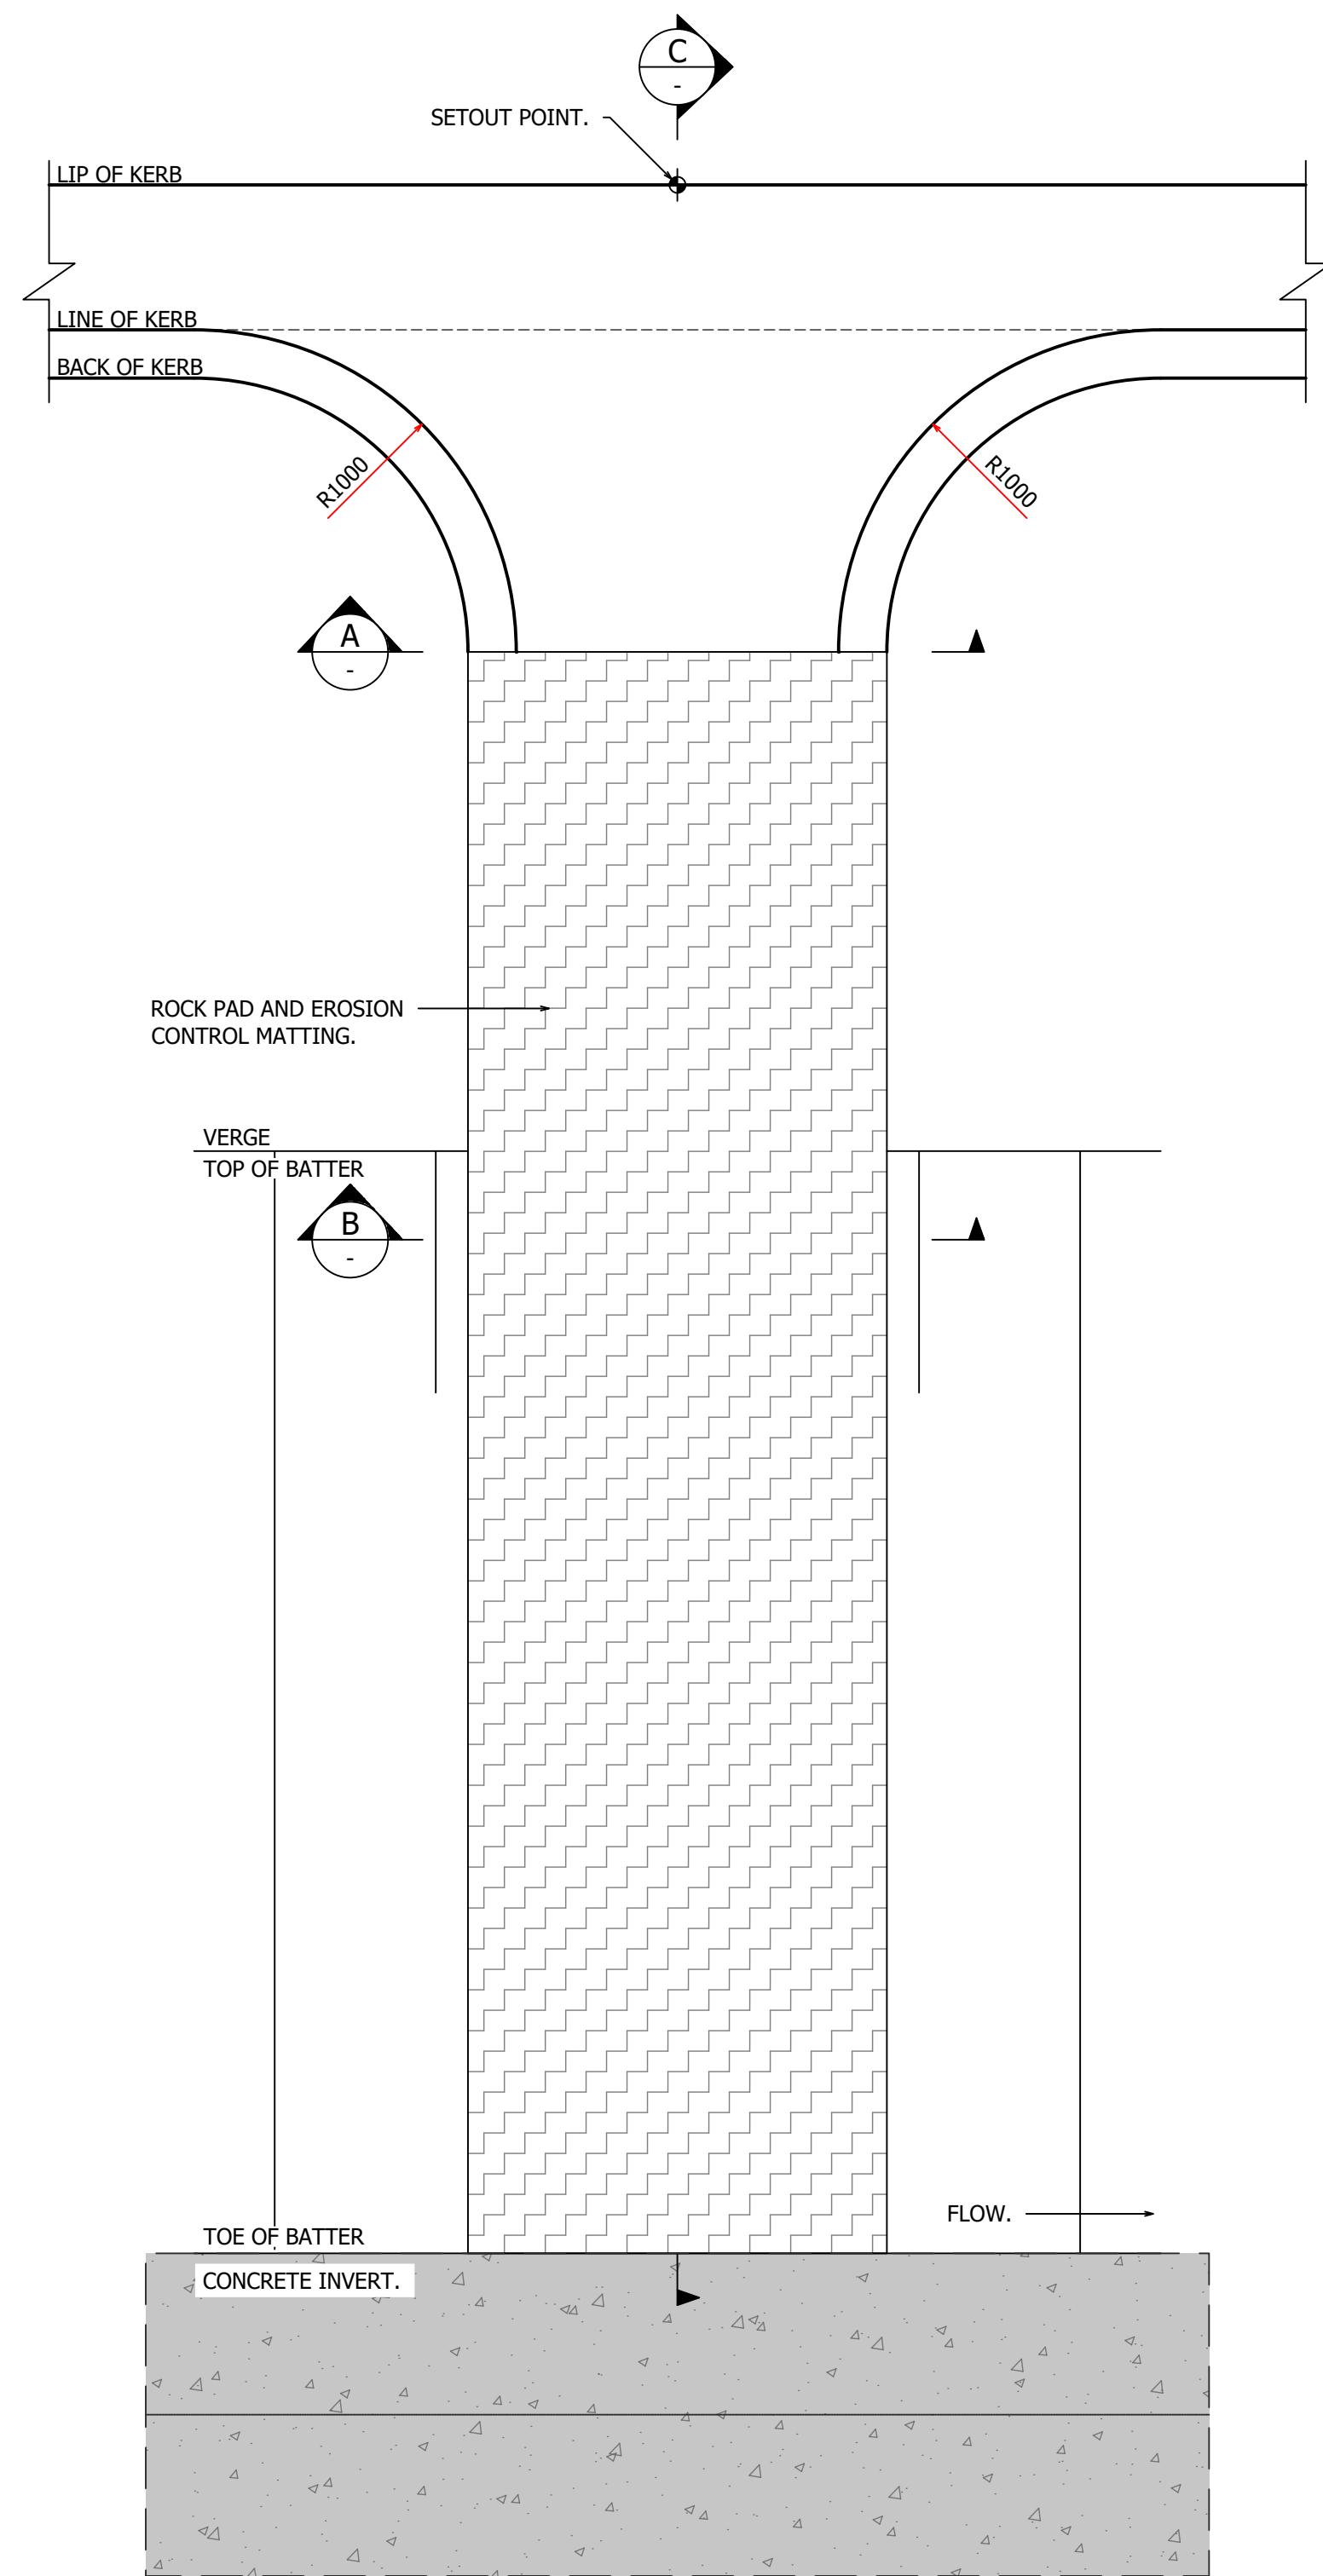


KERB OUTLET TYPICAL DETAIL PLAN
N.T.S.

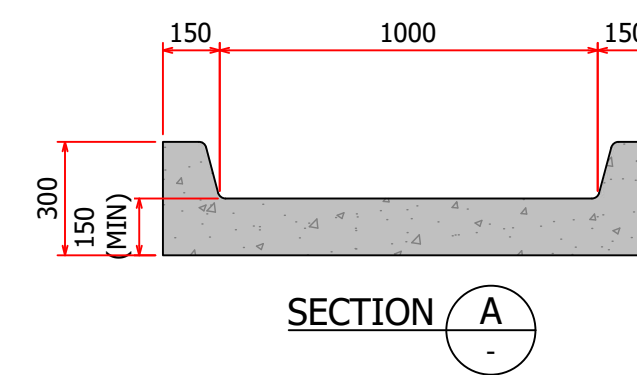

SECTION A

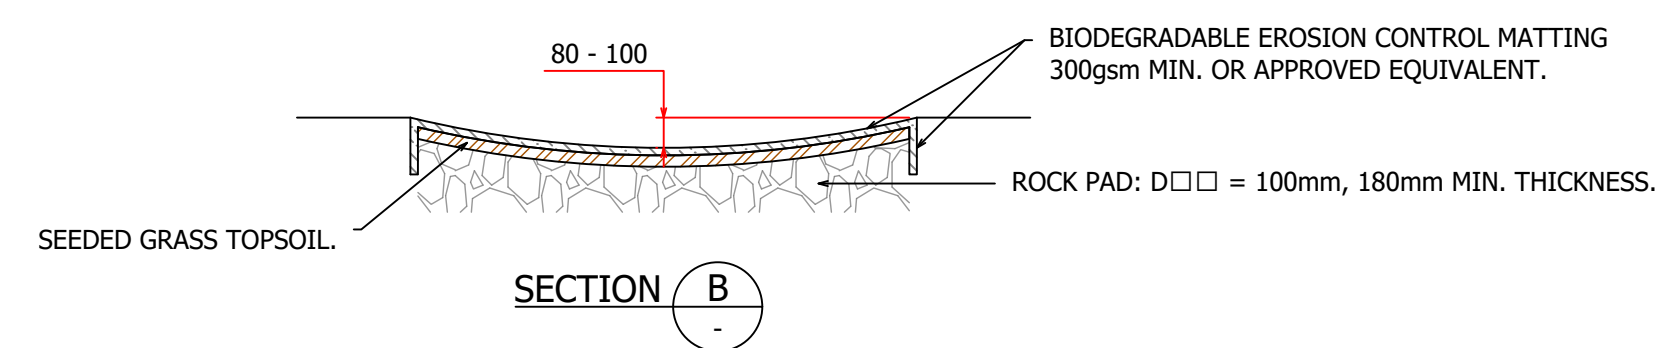

SECTION B

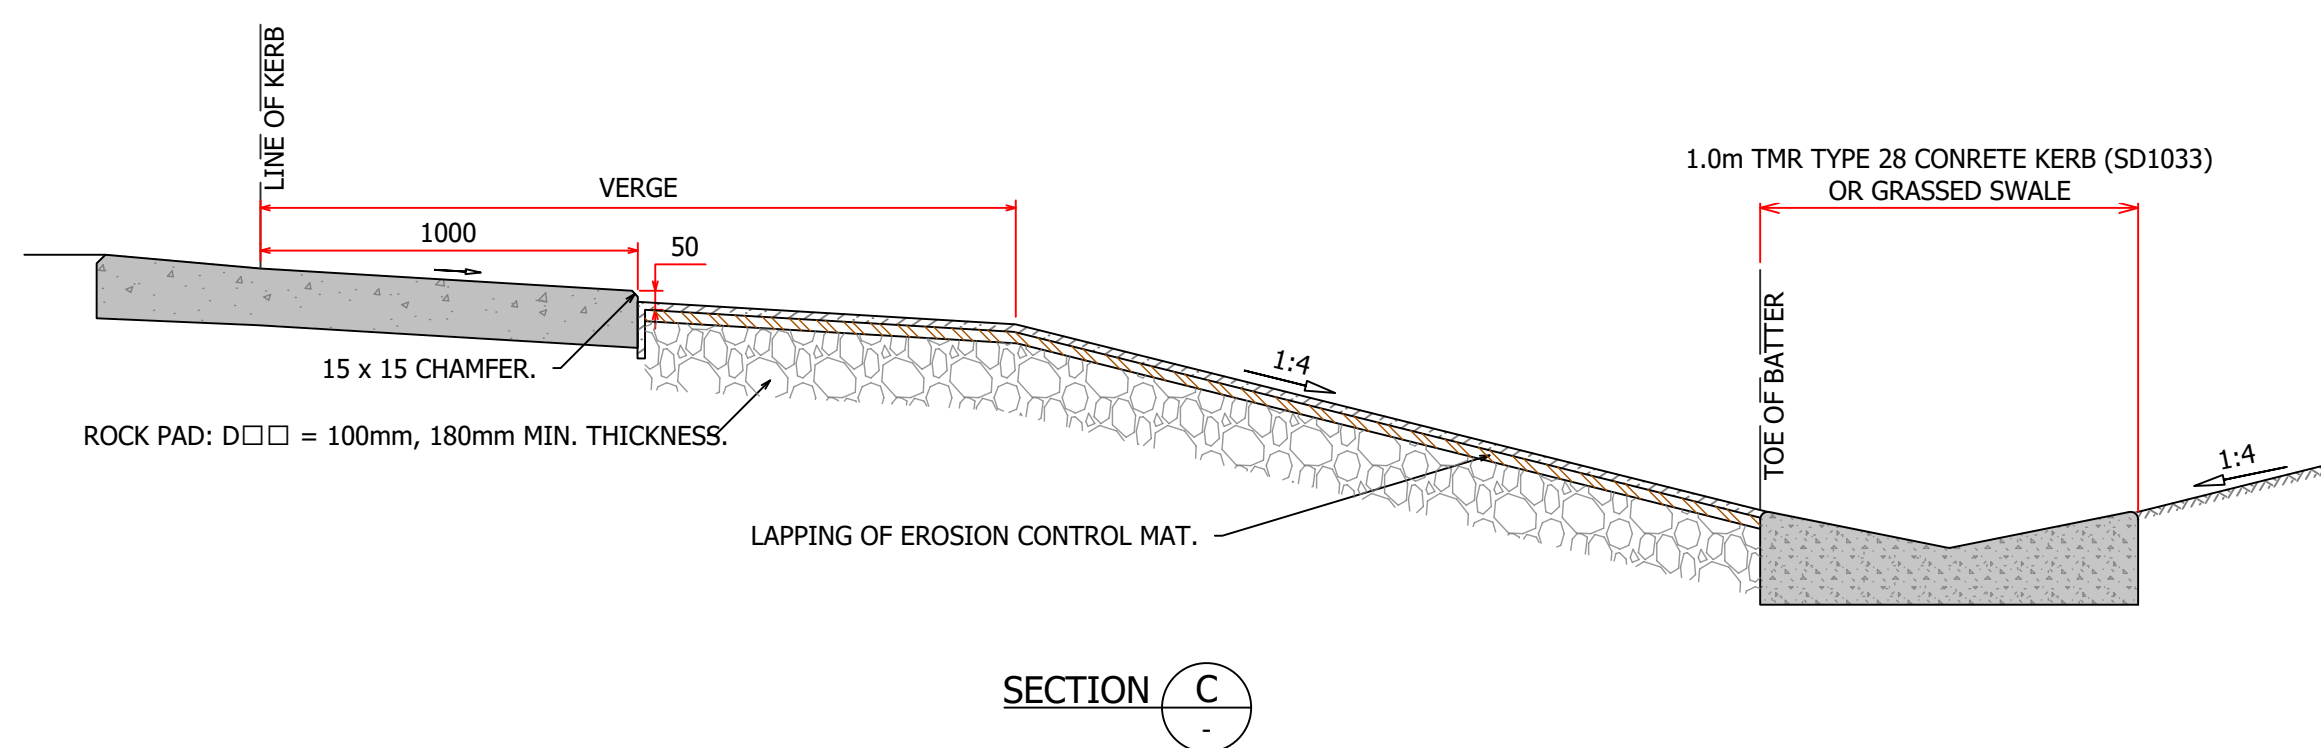

SECTION C

NOT FOR CONSTRUCTION



SPORTENG™

T1	17/06/26	TPC	JZV	JDH	ISSUE FOR TENDER
Issue	Date	By	Chkd	Appd	Description

Job Title
ROCKHAMPTON
NETBALL CENTRE

Drawing Title
STORMWATER DRAINAGE
DETAILS
SHEET 5

Discipline
CIVIL AND FIELD OF PLAY
Drawing Status
ISSUE FOR TENDER
Drawing Number
SE_12306_F1325
Issue
T1