


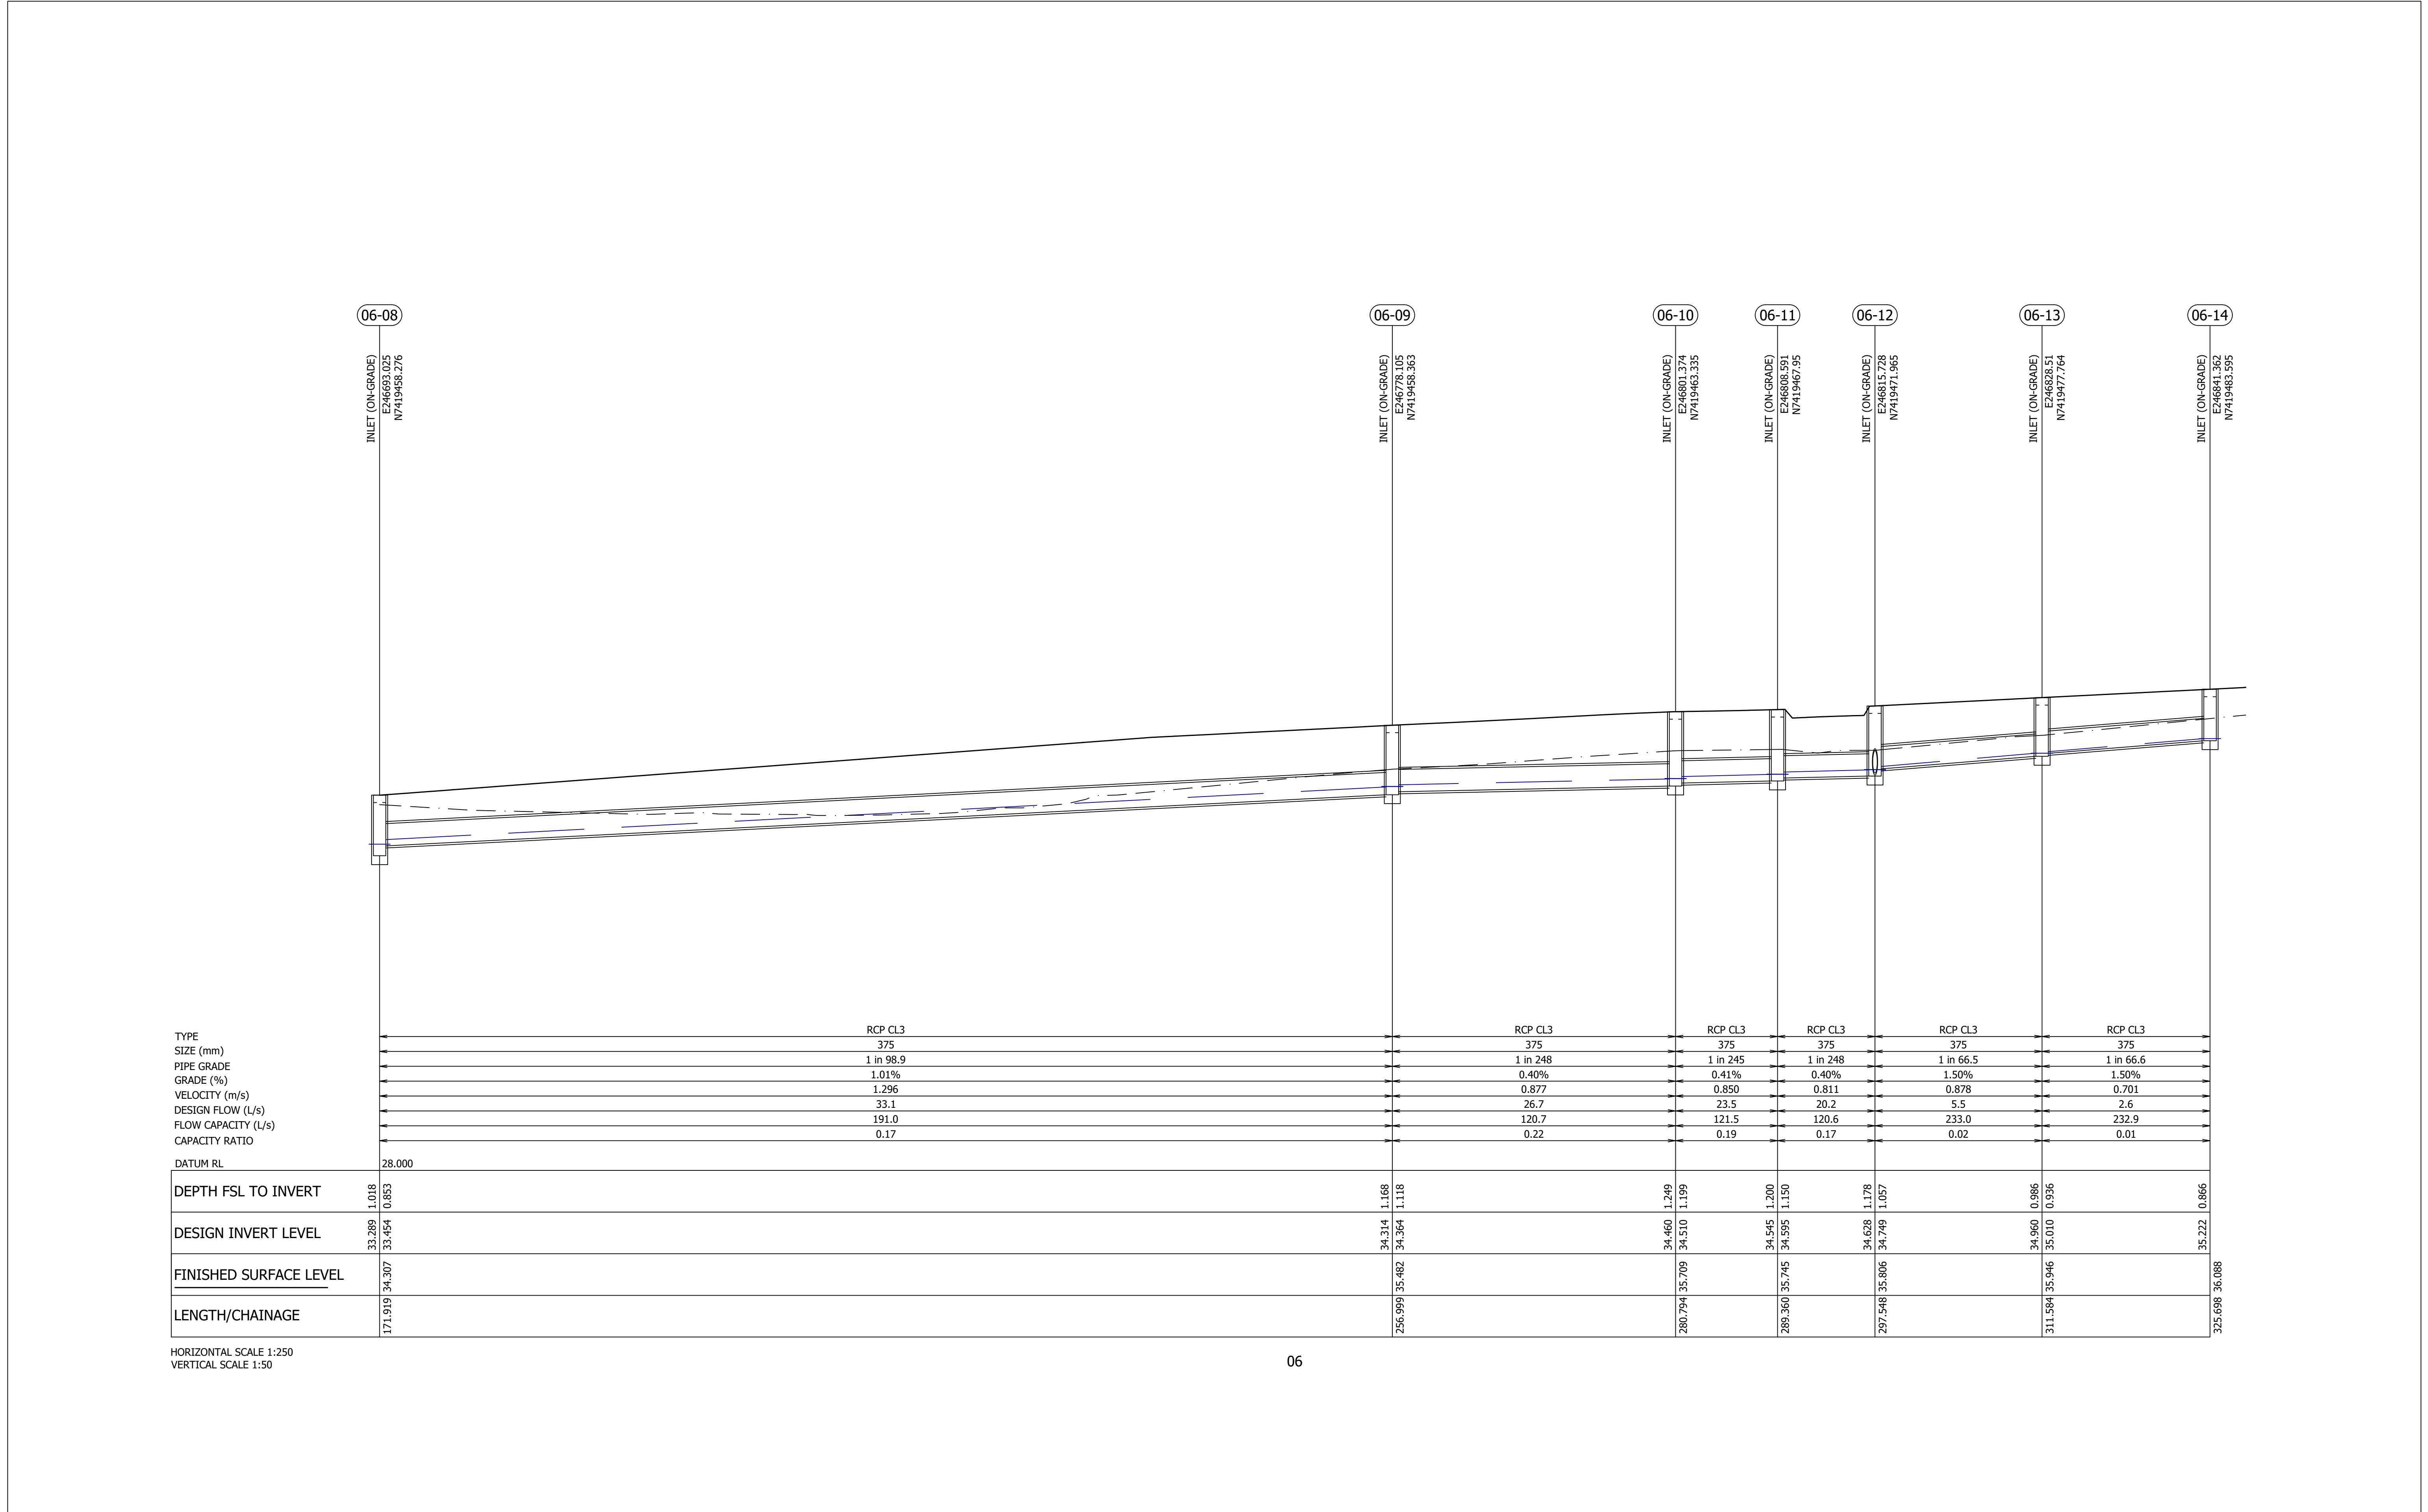

TYPE
SIZE (mm)
PIPE GRADE
GRADE (%)
VELOCITY (m/s)
DESIGN FLOW (L/s)
FLOW CAPACITY (L/s)
CAPACITY RATIO

DATUM RL

DEPTH FSL TO INVERT

DESIGN INVERT LEVEL

FINISHED SURFACE LEVEL

LENGTH/CHAINAGE

HORIZONTAL SCALE 1:250
VERTICAL SCALE 1:50

NOT FOR CONSTRUCTION



T1	17/06/26	TPC	JZV	JDH	ISSUE FOR TENDER
Issue	Date	By	Chkd	Appd	Description

Job Title
ROCKHAMPTON
NETBALL CENTRE

Drawing Title
STORMWATER DRAINAGE
LONG SECTIONS
SHEET 3

Discipline
CIVIL AND FIELD OF PLAY

Drawing Status
ISSUE FOR TENDER

Drawing Number
SE_12306_F1352

Issue
T1