


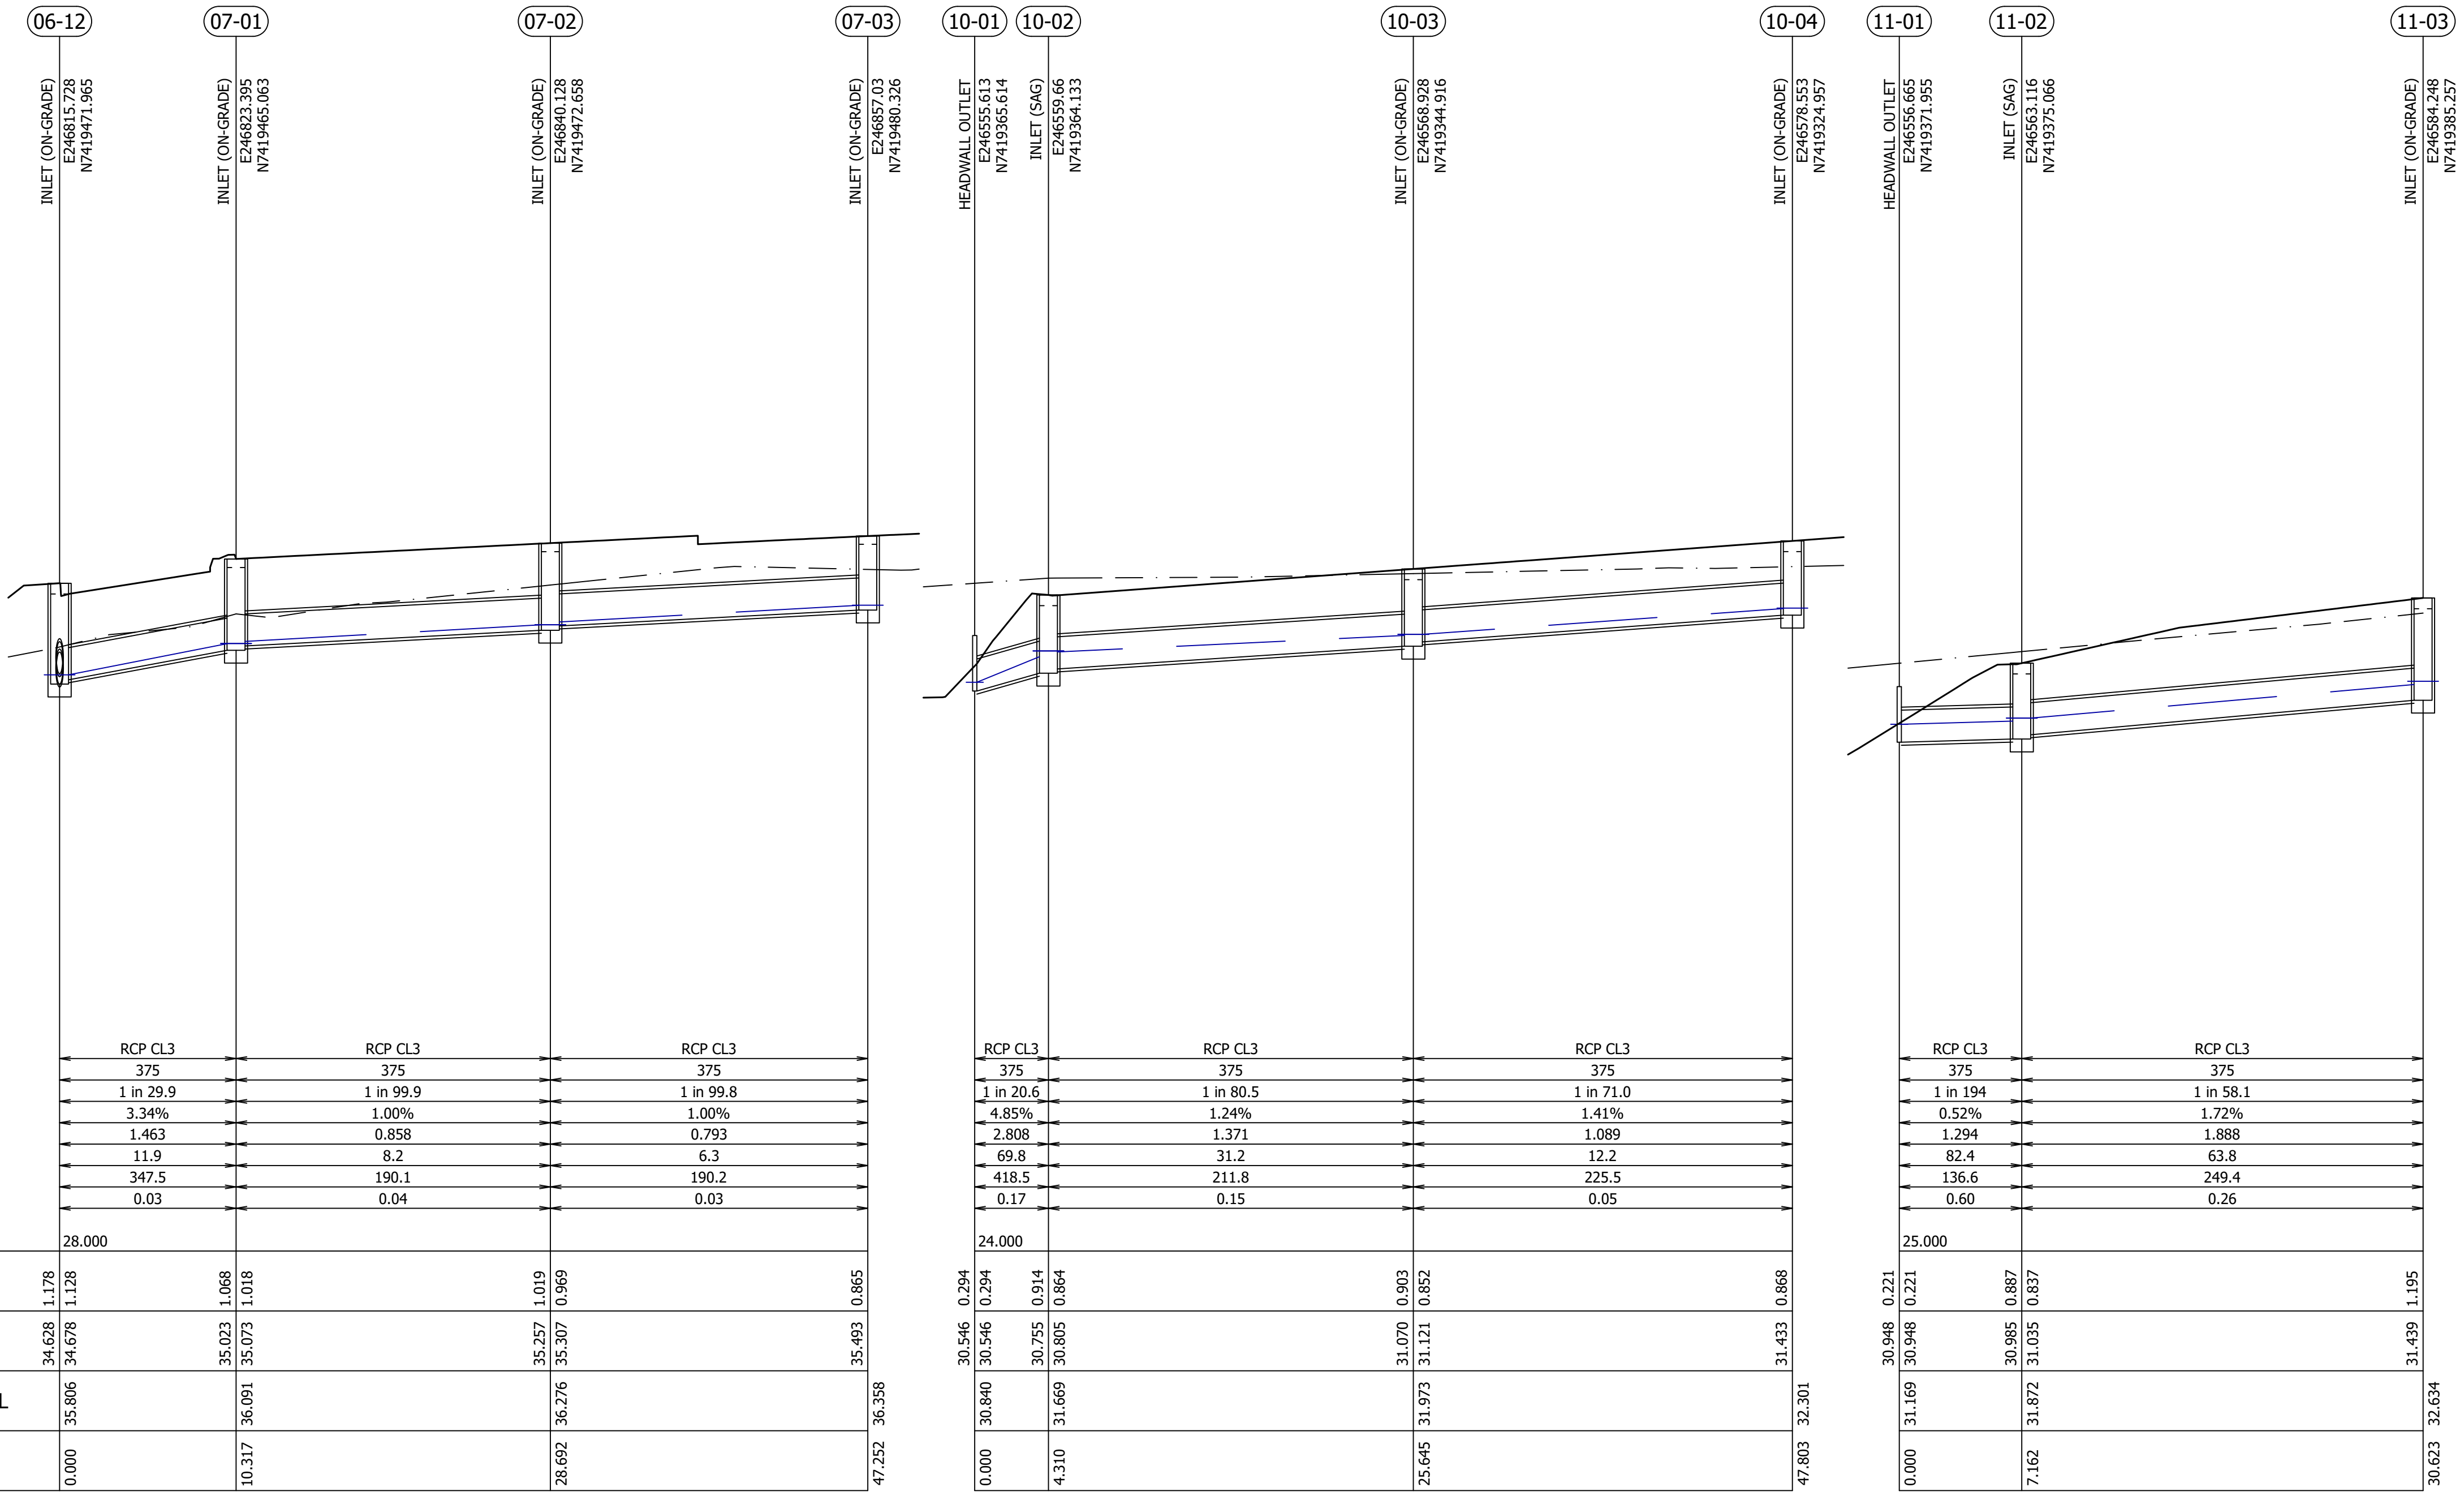

TYPE
SIZE (mm)
PIPE GRADE
GRADE (%)
VELOCITY (m/s)
DESIGN FLOW (L/s)
FLOW CAPACITY (L/s)
CAPACITY RATIO

DATUM RL	28.000				
DEPTH FSL TO INVERT	1.178	1.128	1.068	1.018	0.865
DESIGN INVERT LEVEL	34.628	34.678	35.023	35.073	35.493
FINISHED SURFACE LEVEL	35.806	36.091	36.091	36.276	36.358
LENGTH/CHAINAGE	0.000	10.317	28.692		47.252

DATUM RL	24.000				
DEPTH FSL TO INVERT	0.294	0.294	0.914	0.852	0.868
DESIGN INVERT LEVEL	30.546	30.546	30.755	31.121	31.433
FINISHED SURFACE LEVEL	30.840	30.755	31.669	31.973	32.301
LENGTH/CHAINAGE	0.000	4.310	25.645		47.803

DATUM RL	25.000				
DEPTH FSL TO INVERT	0.221	0.221	0.887	0.837	1.195
DESIGN INVERT LEVEL	30.948	30.948	30.985	31.035	31.439
FINISHED SURFACE LEVEL	31.169	31.872	31.872		32.634
LENGTH/CHAINAGE	0.000	7.162			30.623

HORIZONTAL SCALE 1:250
VERTICAL SCALE 1:50

07

10

11

NOT FOR CONSTRUCTION



T1	17/06/26	TPC	JZV	JDH	ISSUE FOR TENDER
Issue	Date	By	Chkd	Appd	Description

Job Title
ROCKHAMPTON
NETBALL CENTRE

Drawing Title
STORMWATER DRAINAGE
LONG SECTIONS
SHEET 4

Discipline	CIVIL AND FIELD OF PLAY
Drawing Status	ISSUE FOR TENDER
Drawing Number	SE_12306_F1353
Issue	T1