


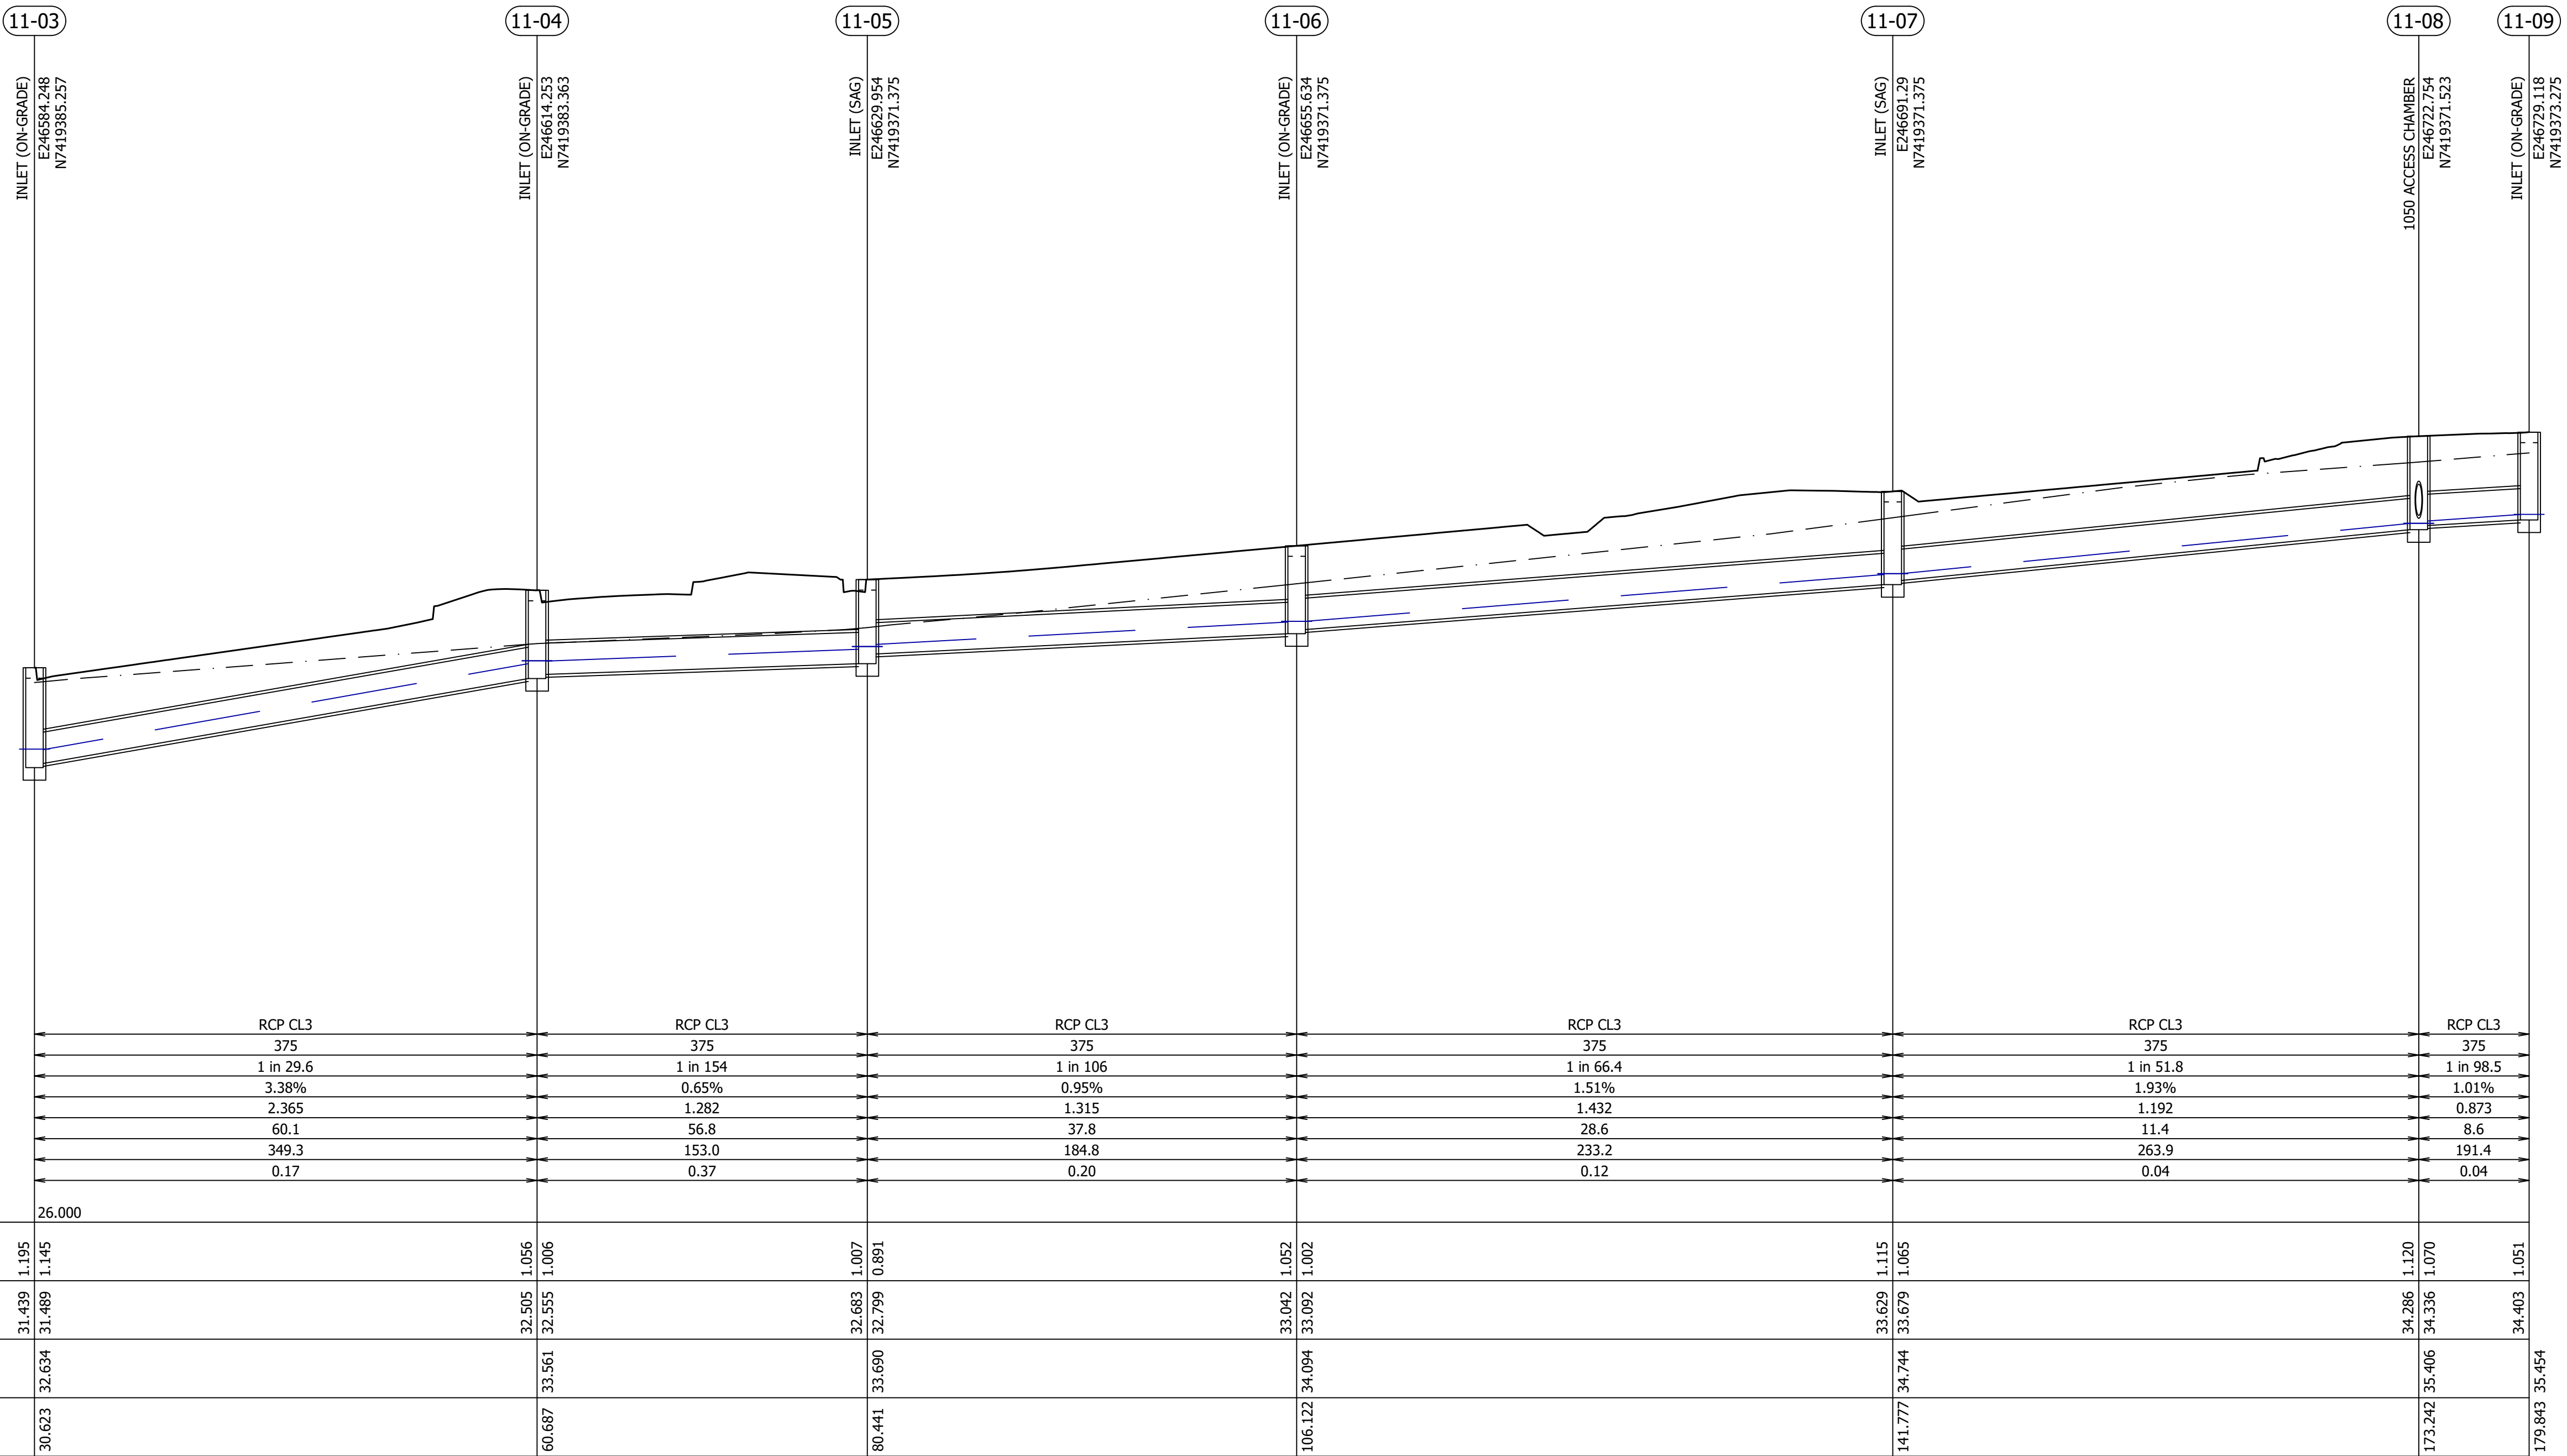

HORIZONTAL SCALE 1:250
VERTICAL SCALE 1:50

NOT FOR CONSTRUCTION



T1	17/06/26	TPC	JZV	JDH	ISSUE FOR TENDER
Issue	Date	By	Chkd	Appd	Description

Job Title
ROCKHAMPTON
NETBALL CENTRE

Drawing Title
STORMWATER DRAINAGE
LONG SECTIONS
SHEET 5

Discipline CIVIL AND FIELD OF PLAY
Drawing Status ISSUE FOR TENDER
Drawing Number SE_12306_F1354
Issue T1