

TYPE
SIZE (mm)
PIPE GRADE
GRADE (%)
VELOCITY (m/s)
DESIGN FLOW (L/s)
FLOW CAPACITY (L/s)
CAPACITY RATIO

DATUM RL


DEPTH FSL TO INVERT

DESIGN INVERT LEVEL

FINISHED SURFACE LEVEL

LENGTH/CHAINAGE

HORIZONTAL SCALE 1:250
VERTICAL SCALE 1:50

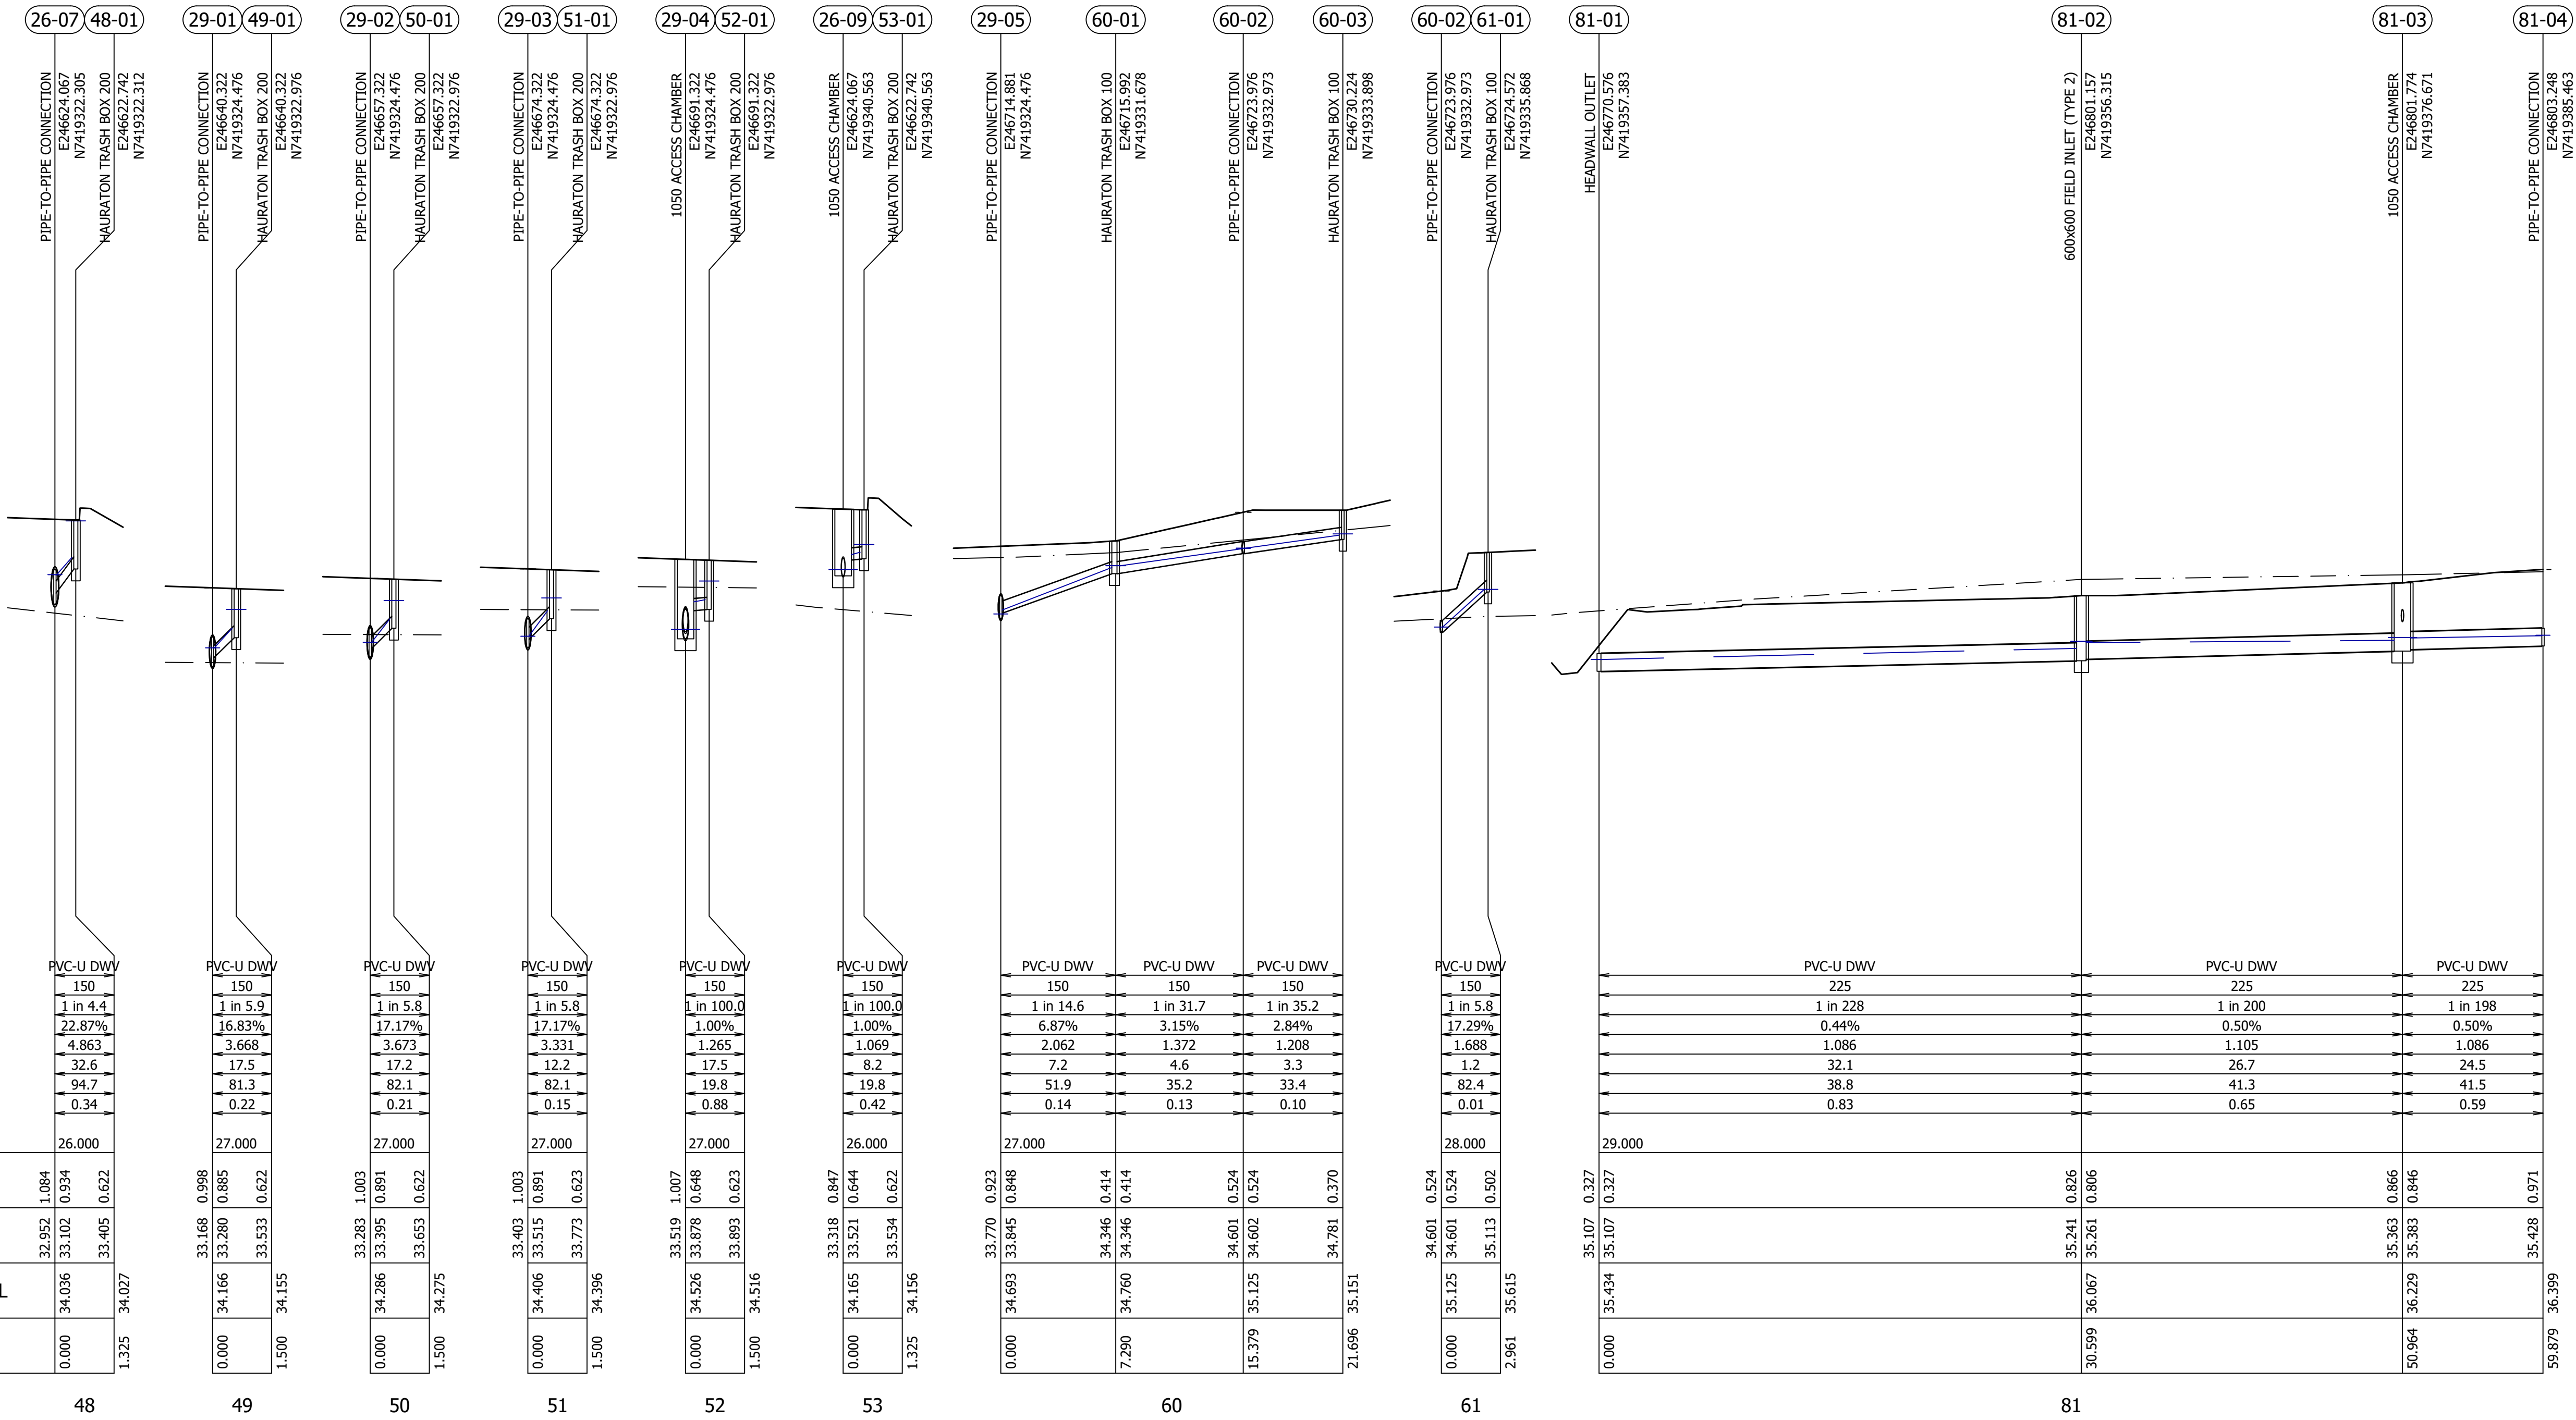

NOT FOR CONSTRUCTION



SPORTENG™

T1 17/06/26 TPC JZV JDH ISSUE FOR TENDER
Issue Date By Chkd Appd Description

Job Title
ROCKHAMPTON
NETBALL CENTRE

Drawing Title
STORMWATER DRAINAGE
LONG SECTIONS
SHEET 11

Discipline
CIVIL AND FIELD OF PLAY
Drawing Status
ISSUE FOR TENDER
Drawing Number
SE_12306_F1360
Issue
T1