


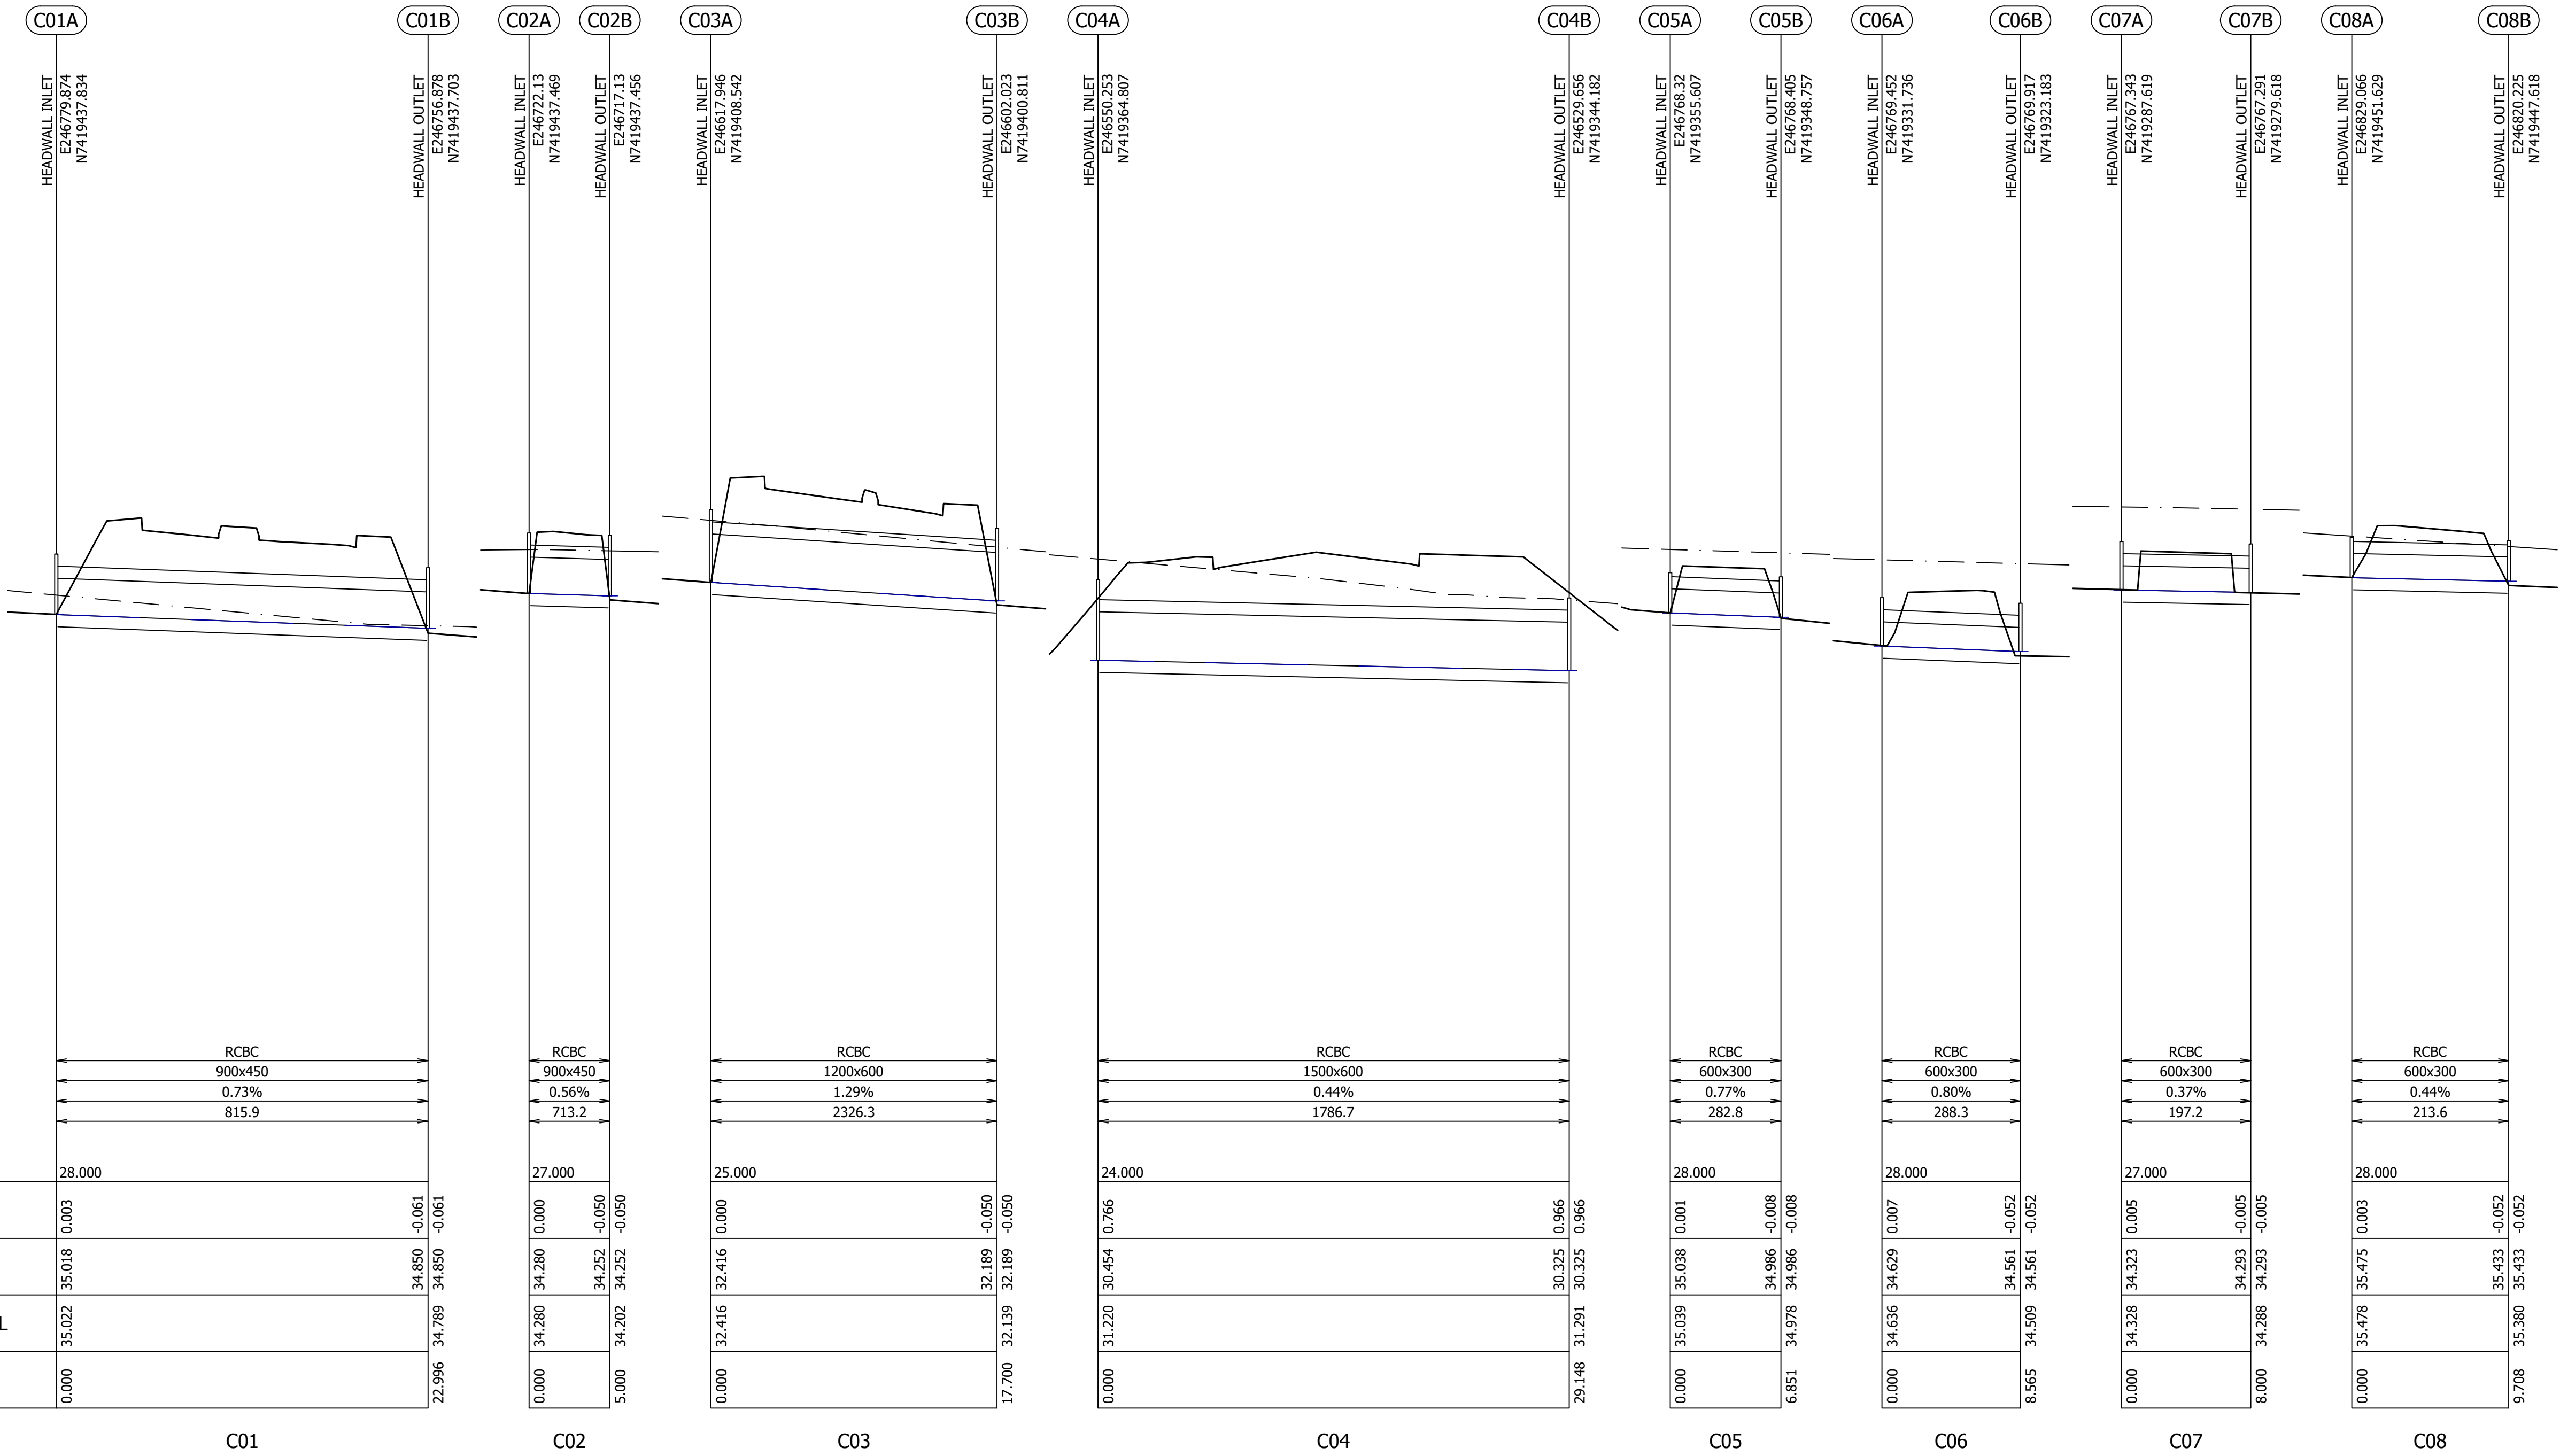

TYPE
SIZE (mm)
GRADE (%)
FLOW CAPACITY (L/s)

DATUM RL

DEPTH FSL TO INVERT

DESIGN INVERT LEVEL

FINISHED SURFACE LEVEL

LENGTH/CHAINAGE

C01

C02

C03

C04

C05

C06

C07

C08

NOT FOR CONSTRUCTION



SPORTENG™

T1	17/06/26	TPC	JZV	JDH	ISSUE FOR TENDER
Issue	Date	By	Chkd	Appd	Description

Job Title
ROCKHAMPTON
NETBALL CENTRE

Drawing Title
STORMWATER DRAINAGE
LONG SECTIONS
SHEET 14

Discipline
CIVIL AND FIELD OF PLAY
Drawing Status
ISSUE FOR TENDER
Drawing Number
SE_12306_F1362

Issue
T1