


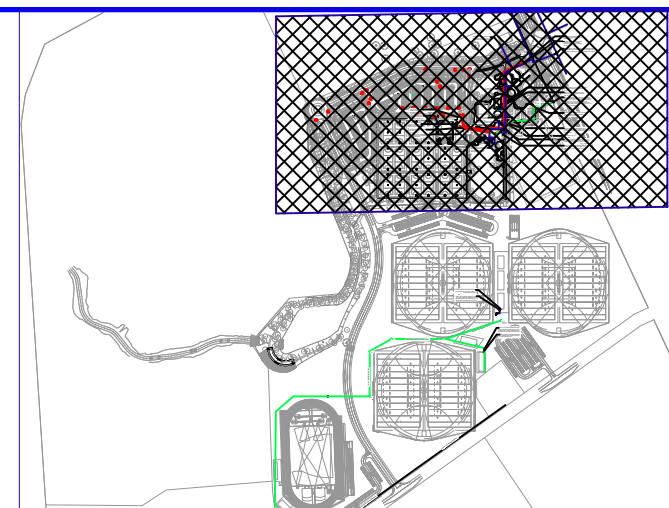

N

WATER TO CONNECT UP TO NEW HOUSES ESTATE TO THE NORTH OF THE SITE AT A FUTURE POINT

020mm COLD WATER COMPLETE WITH ISOLATING VALVE CAPPED FOR FUTURE CONNECTION TO MAINTENANCE BUILDING.

EXISTING AUTHORITY 0250 MPVC COLD WATER

EXISTING AUTHORITY 0250 MPVC COLD WATER

4m x 2m SLAB FOR WATER METERS COMPLETE WITH BOLLARDS TO PROTECT METER ASSEMBLY

PROPOSED Ø100mm FIRE WATER METER ASSEMBLY AND Ø100 COLD WATER ASSEMBLY AUTHORITY'S REQUIREMENTS AND APPROVAL

PROPOSED Ø200mm COLD WATER TAPPING FOR FIRE AND GENERAL TO AUTHORITY'S WATER MAIN LOCATED EAST OF NORMAN ROAD TO ROCKHAMPTON REGIONAL COUNCIL REQUIREMENTS AND APPROVAL

SL. 36.490
IL. 34.805

Ø100 FS INGROUND
Ø100 CW INGROUND

Ø100 SEWER RAISING MAIN

MH-1
RL. 37.800
IL. 35.716

IL. 35.433

NEW Ø150 UPVC SEWER @ 1:100 FALL

Ø100mm SEWER FOR TO PUBLIC TOILETS BUILDING FOR CONTINUATION REFER TO DRAWING NOS. 25015-H-PAM-100

Ø25mm COLD WATER CAPPED FOR FUTURE CONNECTION TO PUBLIC AMENITIES BUILDING

Ø150 SEWER PROPERTY SEWER CONNECTION IN GROUND, ALLOW TO EXTEND AND CONNECT INTO EXISTING SEWER PIT (MH) TO LOCAL AUTHORITY'S REQUIREMENTS AND APPROVAL. FINAL AND EXACT LOCATION TO BE CONFIRMED AND DETERMINED ON SITE. CONTRACTOR TO ALLOW FOR SITE CONNECTION. SUBMIT APPLICATION FOR APPROVAL PAY FEES AND CHARGES AS REQUIRED.

PROPOSED SEWER RAISING MAIN TO BE CONNECTED TO SITE SEWER RETICULATION LOCATION TO BE CONFIRMED AND COORDINATED

FOR DETAIL DRAWINGS H-NBC-102 AND H-NBC-202 FOR MORE DETAILS.

PROPOSED VANDAL PROOF GARDEN TAP COMPLETE TO STAND 600mm ABOVE FSL.

Ø100mm SEWER FOR TO NETBALL CLUB HOUSE BUILDING FOR CONTINUATION REFER TO DRAWING NOS. 25015-H-NBC-102

FOR CONTINUATION REFER TO DRAWING H-NBC-102 FOR FURTHER DETAILS

Ø32mm COLD WATER CAPPED FOR FUTURE CONNECTION TO NETBALL CLUB HOUSE BUILDING

I.L. 35.061

I.L. 34.610

SMS-1
RL. 35.700
IL. 34.556

NEW Ø100 UPVC SEWER @ 1:60 FALL

SMS-2
RL. 35.700
IL. 33.783

Ø100 FS INGROUND
Ø100 CW INGROUND
REFER TO DRAWING H300 FOR THE TRENCH DETAIL

I.L. 33.380

I.L. 34.603

Ø100 SEWER RAISING MAIN

Ø100 SEWER RAISING MAIN

PROPOSED SEWER PUMP AND CHAMBER (PIT) IN GROUND, QMAX FORTIS 3200 PUMPELL OR EQUALLY APPROVED. REFER TO DETAILS QCPS32VC/A01 & A02 FOR FURTHER DETAILS.

R/L TO BE SET AS THE FSL.

Ø100mm COLD WATER COMPLETE WITH ISOLATING AND CHECK METER VALVE CAPPED FOR FUTURE CONNECTION TO HIGH PERFORMANCE CENTER BUILDING AMENITIES

Ø100mm COLD WATER POINT FOR IRRIGATION TO TAKE OFF FROM ISOLATION VALVE AND CHECK VALVE COMPLETE WITH E TYPE FLANGE CAPPED ABOVE GROUND.

Ø20 TO CONNECT TO PILLAR SUPPLY. REFER TO ARCHITECTURAL DRAWINGS AND FIXTURE SCHEDULE FOR FURTHER DETAILS. (TYPICAL)

FOR CONTINUATION REFER TO DRAWING H004

ALL DIMENSIONS SHOWN IN MM DO NOT SCALE FROM DRAWINGS. DIMENSIONS TAKE PRECEDENCE IF IN DOUBT REFER TO HK SOLUTIONS

SCALE 1:500 @A1

TENDER ISSUE

FOR CONTINUATION LN REFER TO DRAWING H004

TENDER ISSUE

T1		ISSUE FOR TENDER	17.06.2026	MC	HKS	 ENGINEERING PROJECT MANAGEMENT DARWIN. GEELONG. CAIRNS. TOWNSVILLE. PERTH. BALLARAT admin@hksolutions.com.au www.hksolutions.com.au
REV.	DESCRIPTION		DATE	INIT.	COMPANY	
Conditions of use. This document may only be used by Harris Kmon Solutions clients for the purpose for which it was prepared and must not be used by any other person or for any other purpose.						
REVISIONS						

DRAWN	MC	CITY OF ROCKHAMPTON
CHECKED	AB	ROCKHAMPTON SPORTS PRECINCT
DESIGNED	MC	554-700 YAAMBA ROAD NORMAN GARDENS
CHECKED	AB	
APPROVED		HYDRAULIC SERVICE
Date Approved		STAGE 1 SITE RETICULATION
THIS DRAWING MUST NOT BE USED FOR CONSTRUCTION UNLESS SIGNED AS APPROVED		
PAGE No	PROJECT No	DRAWING No
3 OF 4	25015 - H003	
DISCIPLINE		REV.
HYDRAULIC		T1
SHEET SIZE		A1