




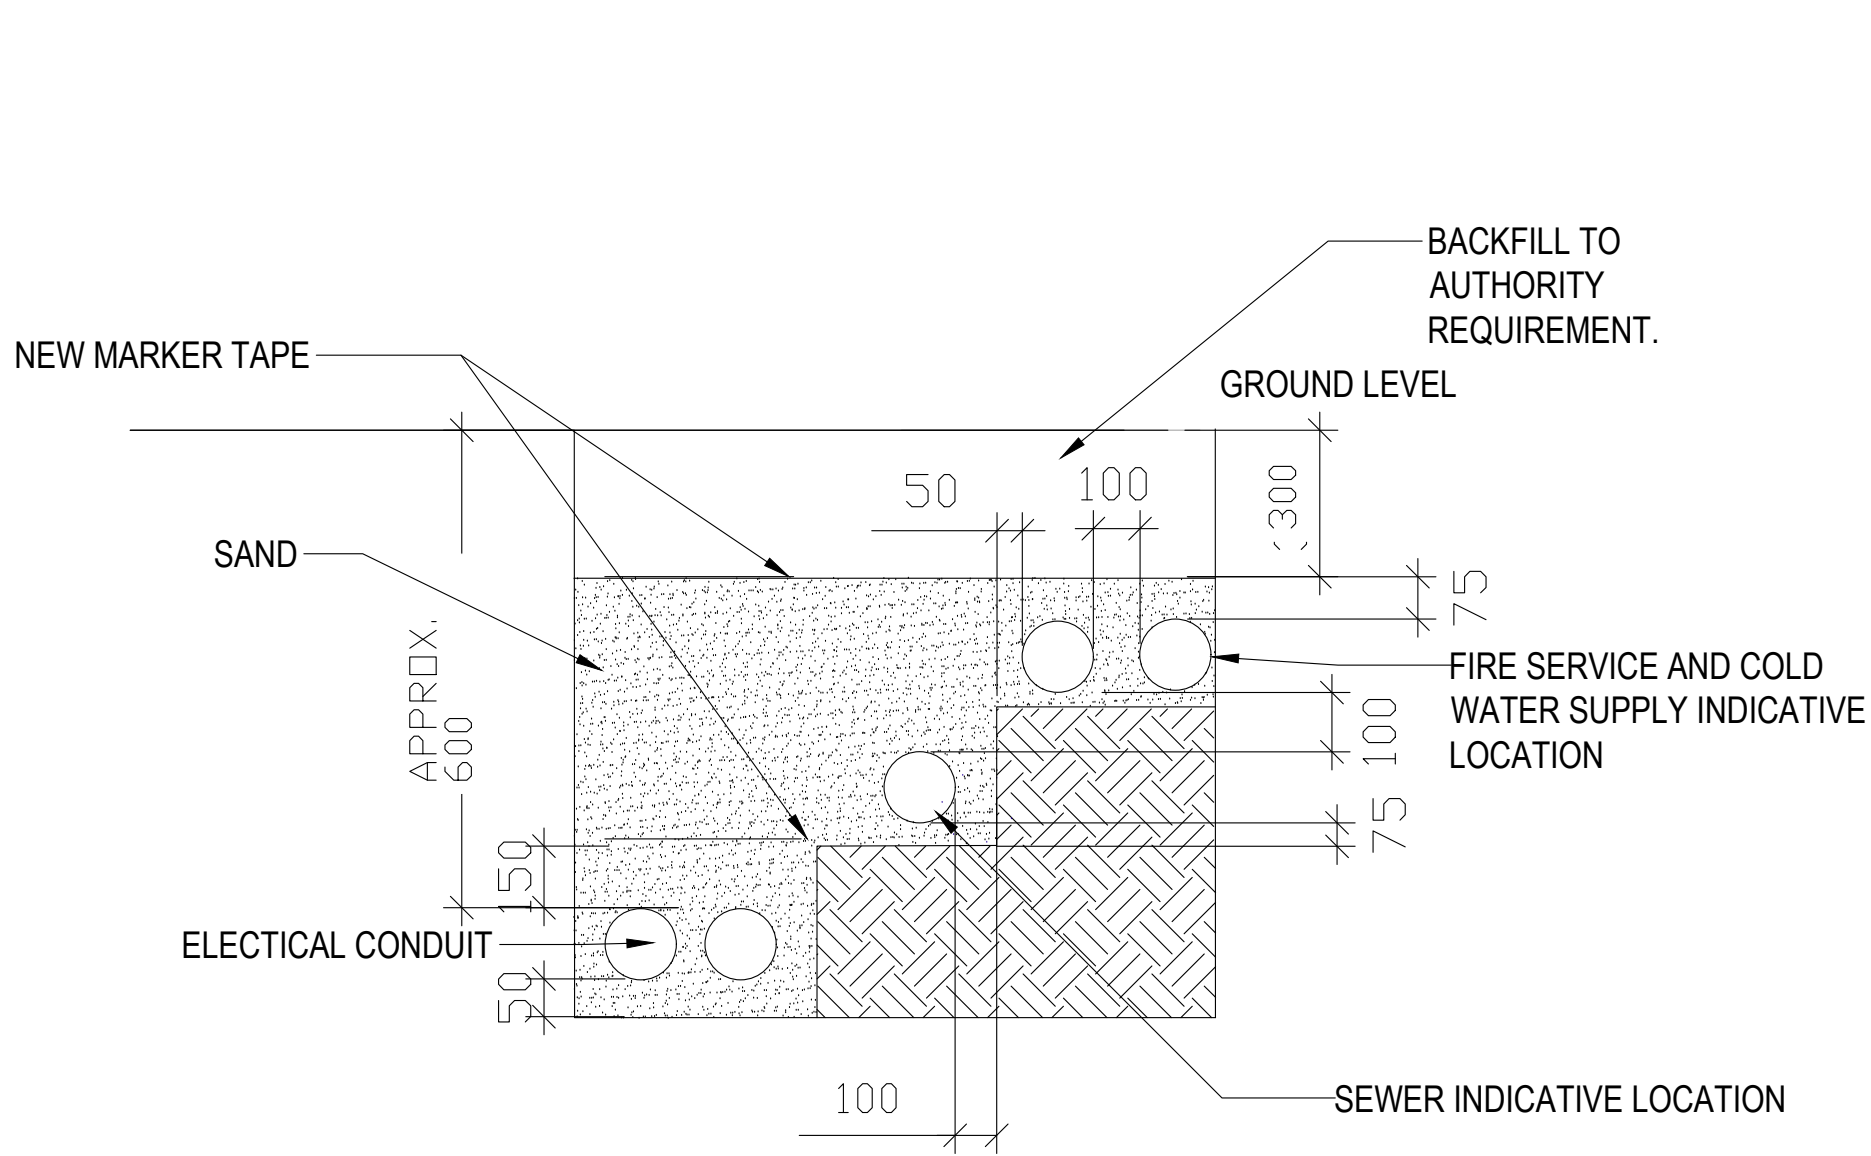


SHARED TRENCH DETAIL
NOT TO SCALE

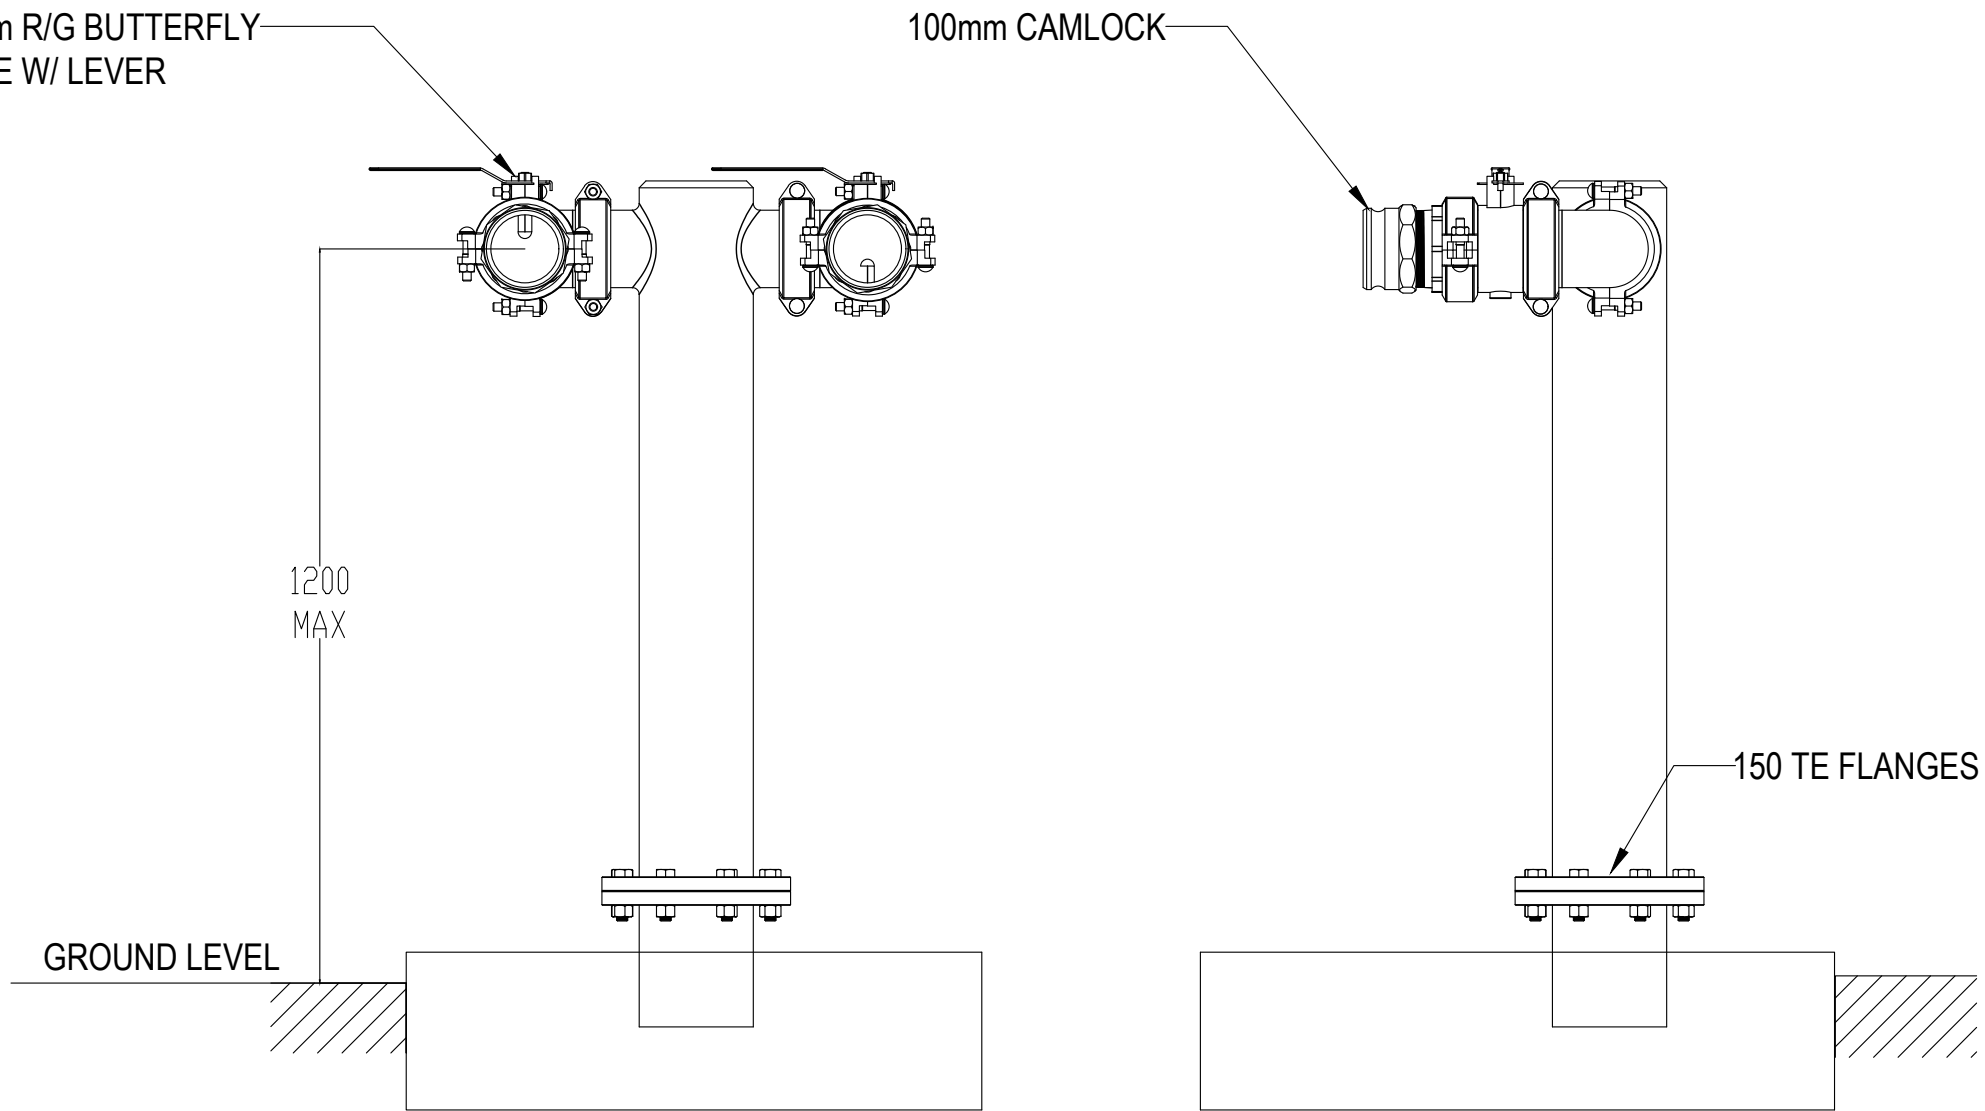


FIRE HYDRANT DETAIL
NOT TO SCALE

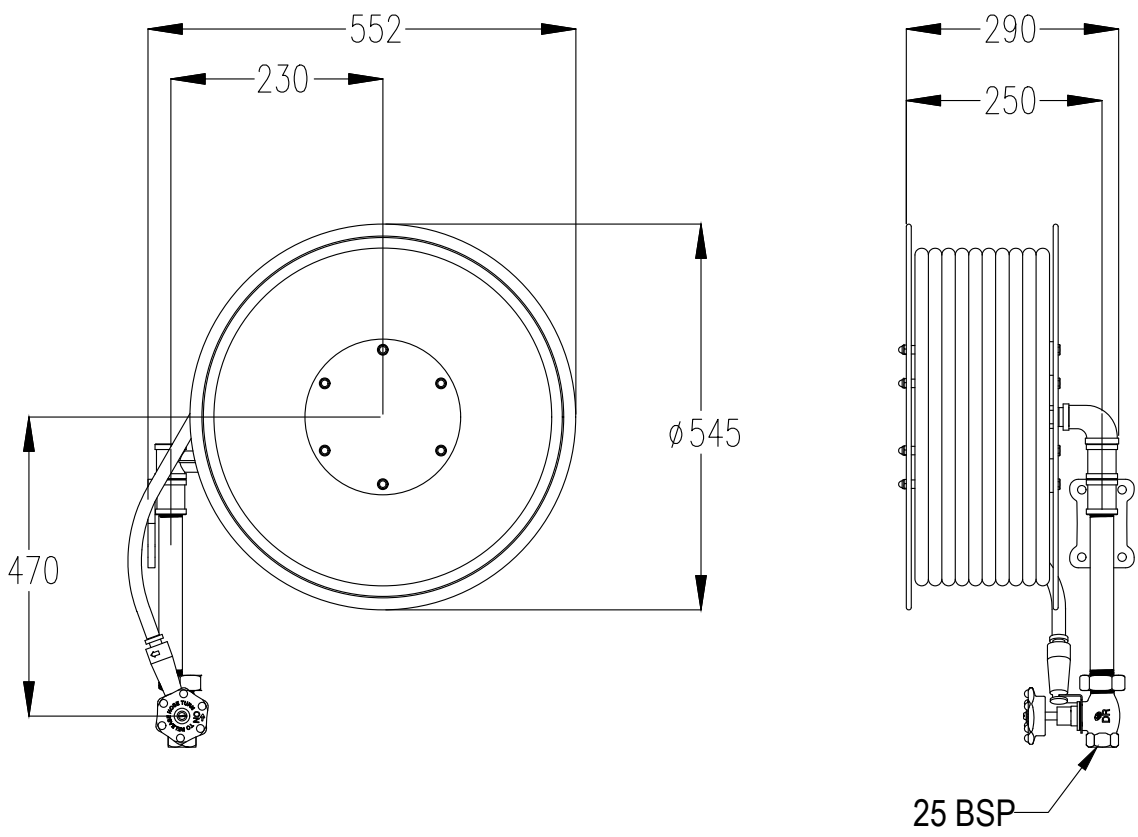

FIRE HOSE REEL DETAIL
NOT TO SCALE

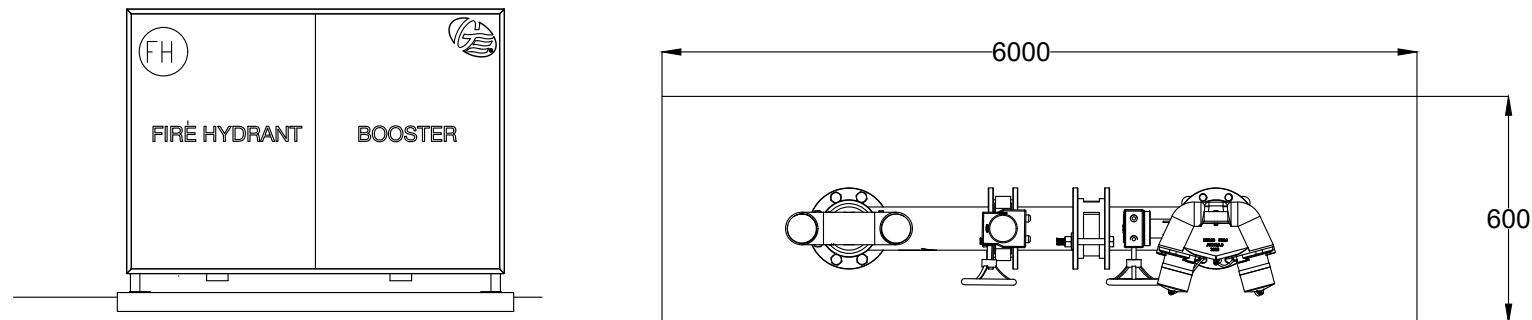

FRONT VIEW

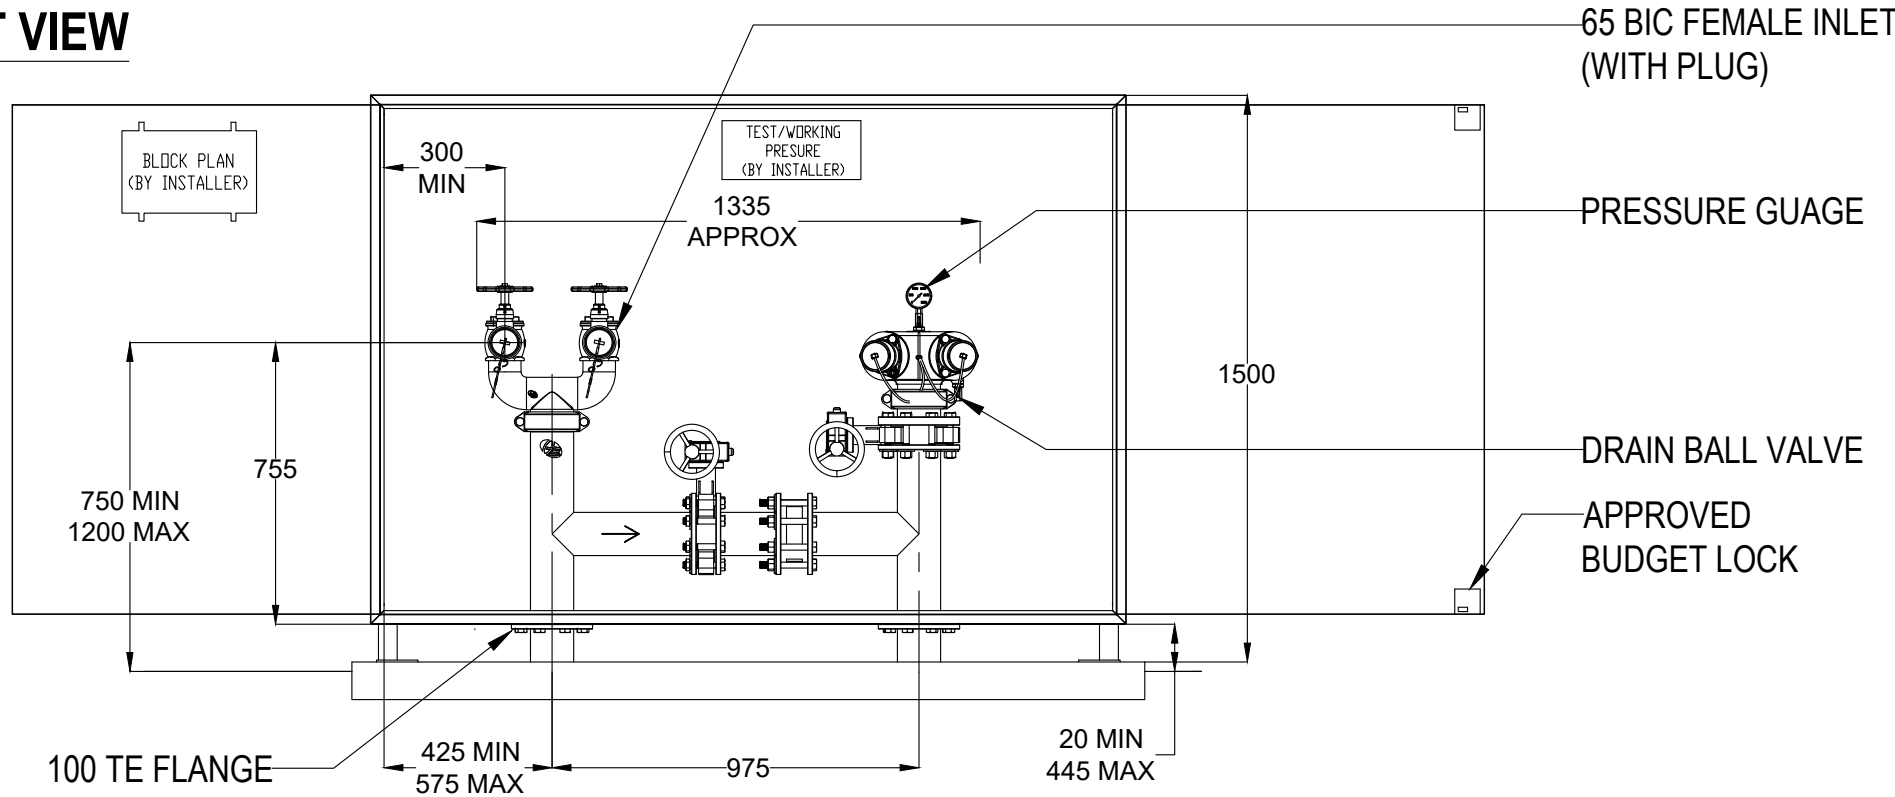

H DESIGN BOOSTER CABINET DETAIL
NOT TO SCALE

ALL DIMENSIONS SHOWN IN MM. DO NOT SCALE FROM DRAWINGS. DIMENSIONS TAKE PRECEDENCE. IF IN DOUBT REFER TO HK SOLUTIONS.

TENDER ISSUE



ENGINEERING
PROJECT MANAGEMENT
DARWIN. GEELONG.
CAIRNS. TOWNSVILLE.
PERTH. **BALLARAT**
admin@hksolutions.com.au
www.hksolutions.com.au

Conditions of use. This document may only be used by Harris Kmon Solutions clients for the purpose for which it was prepared and must not be used by any other person or for any other purpose.

DRAWN MC
CHECKED AB
DESIGNED MC
CHECKED AB
APPROVED ##
Date Approved ##
THIS DRAWING MUST NOT BE
USED FOR CONSTRUCTION
UNLESS SIGNED AS
APPROVED

CITY OF ROCKHAMPTON
ROCKHAMPTON SPORTS PRECINCT
554-700 YAAMBA ROAD NORMAN GARDENS
**HYDRAULIC SERVICES
DETAILS**

PAGE No	PROJECT No	DRAWING No	DISCIPLINE	REV.	SHEET SIZE
4 OF 4	25015 - H300		HYDRAULIC	T1	A1