


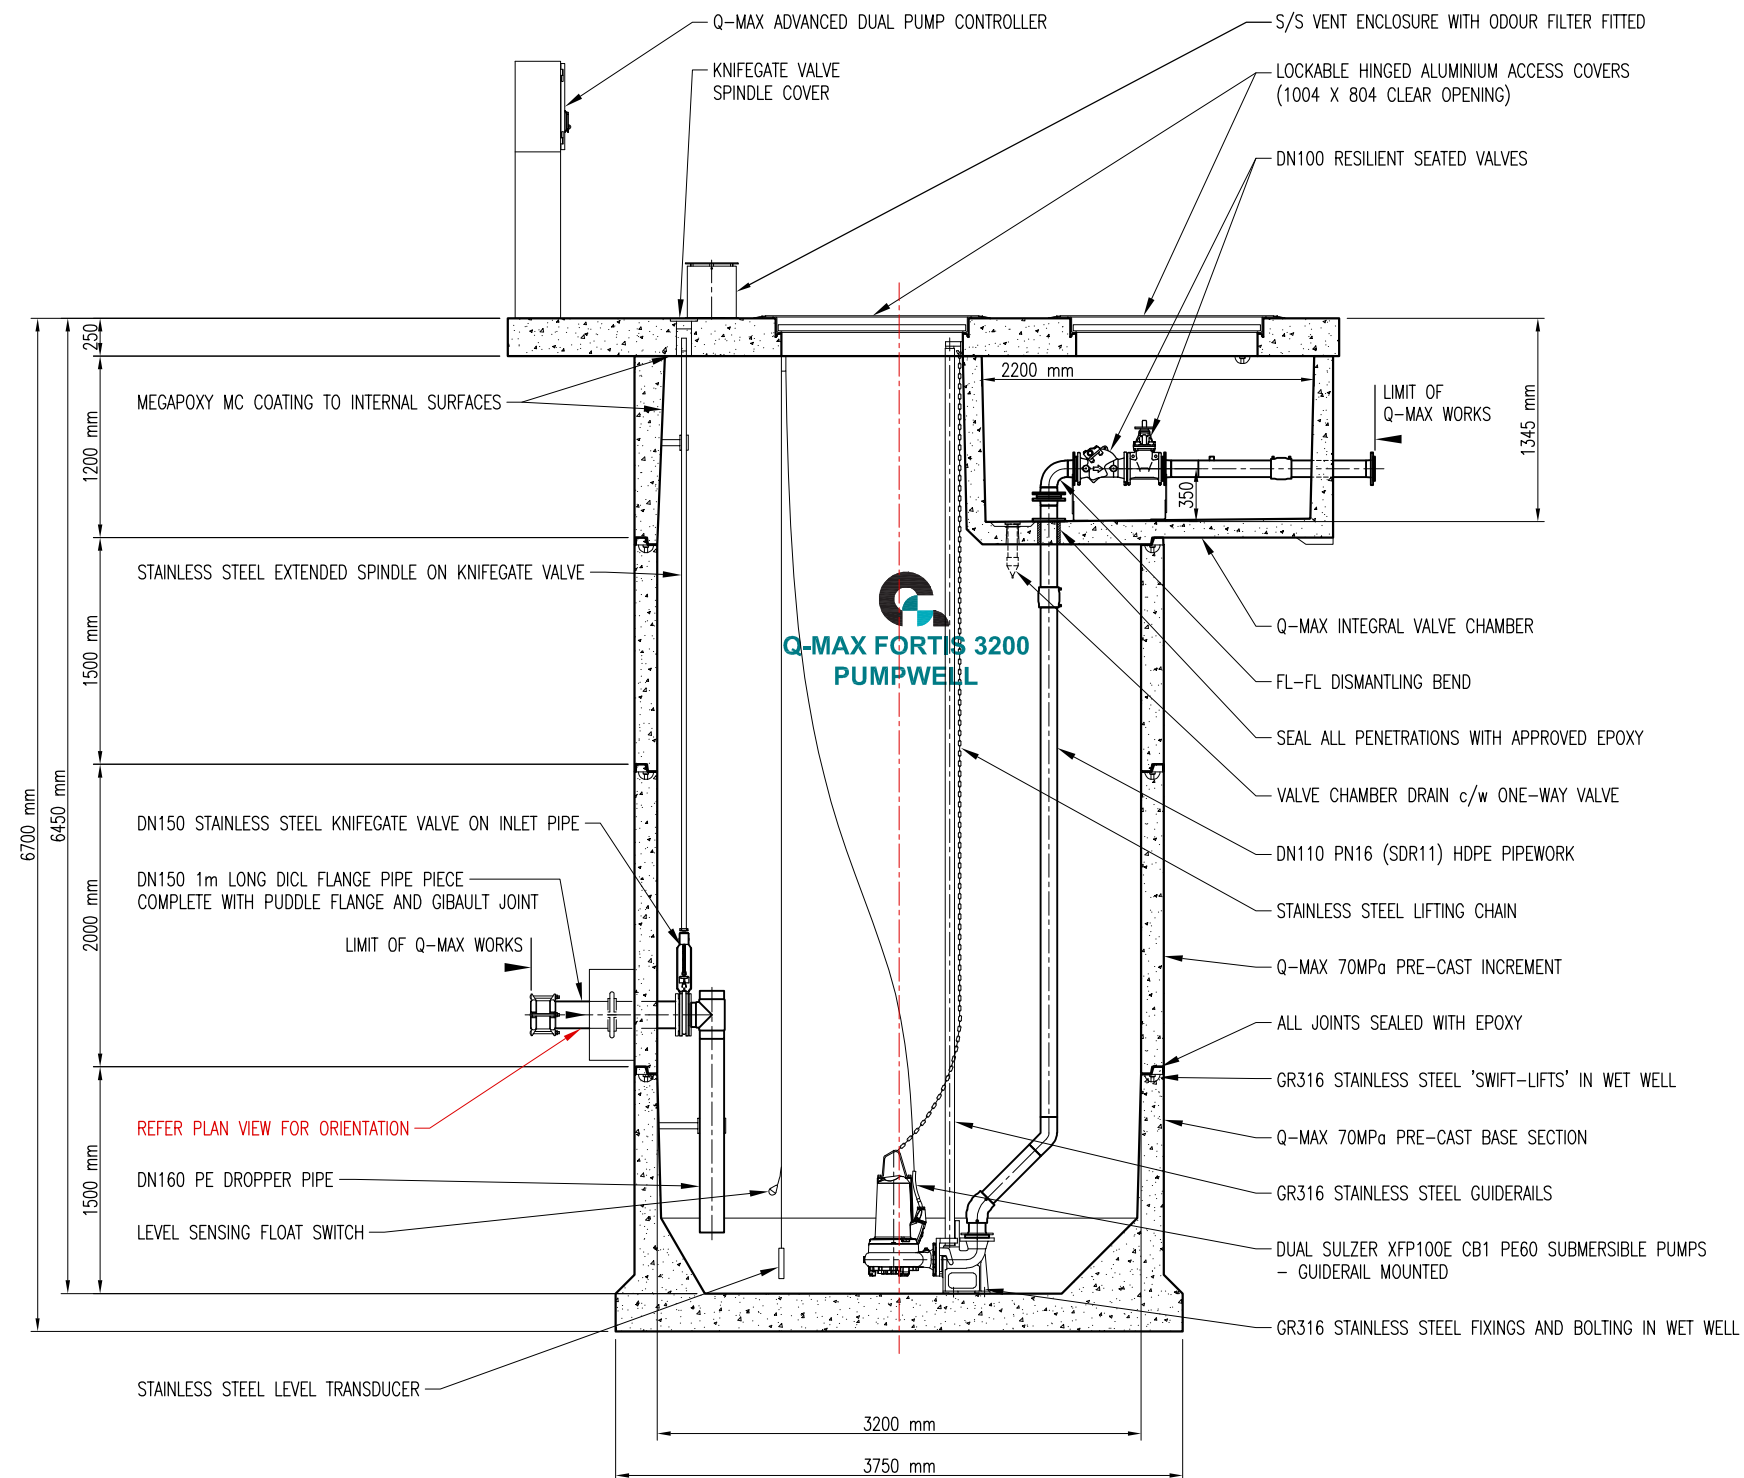

SECTIONAL ELEVATION
SCALE: 1 : 50 @ A3

Copyright of this design shown hereon is retained by Q-MAX PUMPING SYSTEMS
Reproduction of any kind not permitted unless prior authorisation is given in writing from Q-MAX PUMPING SYSTEMS
Figured dimensions to be used in preference to scaling.
Any dimensional or drawing discrepancy to be referred to the Q-MAX Project Manager Prior to the commencement of work.

Rev	Description	Date
A	For Approval	27.03.24

Status
FOR APPROVAL

QMAX PUMPING SYSTEMS
P O BOX 6006
72 HIGH STREET
QUEANBEYAN NSW 2620
P 02 6128 1000 F 02 6128 1055
E SALES@QMAXPUMPING.COM.AU
WWW.QMAXPUMPING.COM.AU
DESIGNED FOR PERFORMANCE.
BASED ON EXPERIENCE.

Client
-

Project
SAMPLE SEWER PUMP STATION

Drawn	S. SHOKRAVI	Date	27.03.2024
Designed	D. PRIDHAM		
Checked	P. PRIDHAM	Size	A3

Title
Q-MAX FORTIS 3200 PUMP STATION GENERAL LAYOUT (SECTIONAL ELEVATION)

Scale	1 : 50	Rev	A
-------	--------	-----	---

Drg No. **QCPS32VC/A02**