


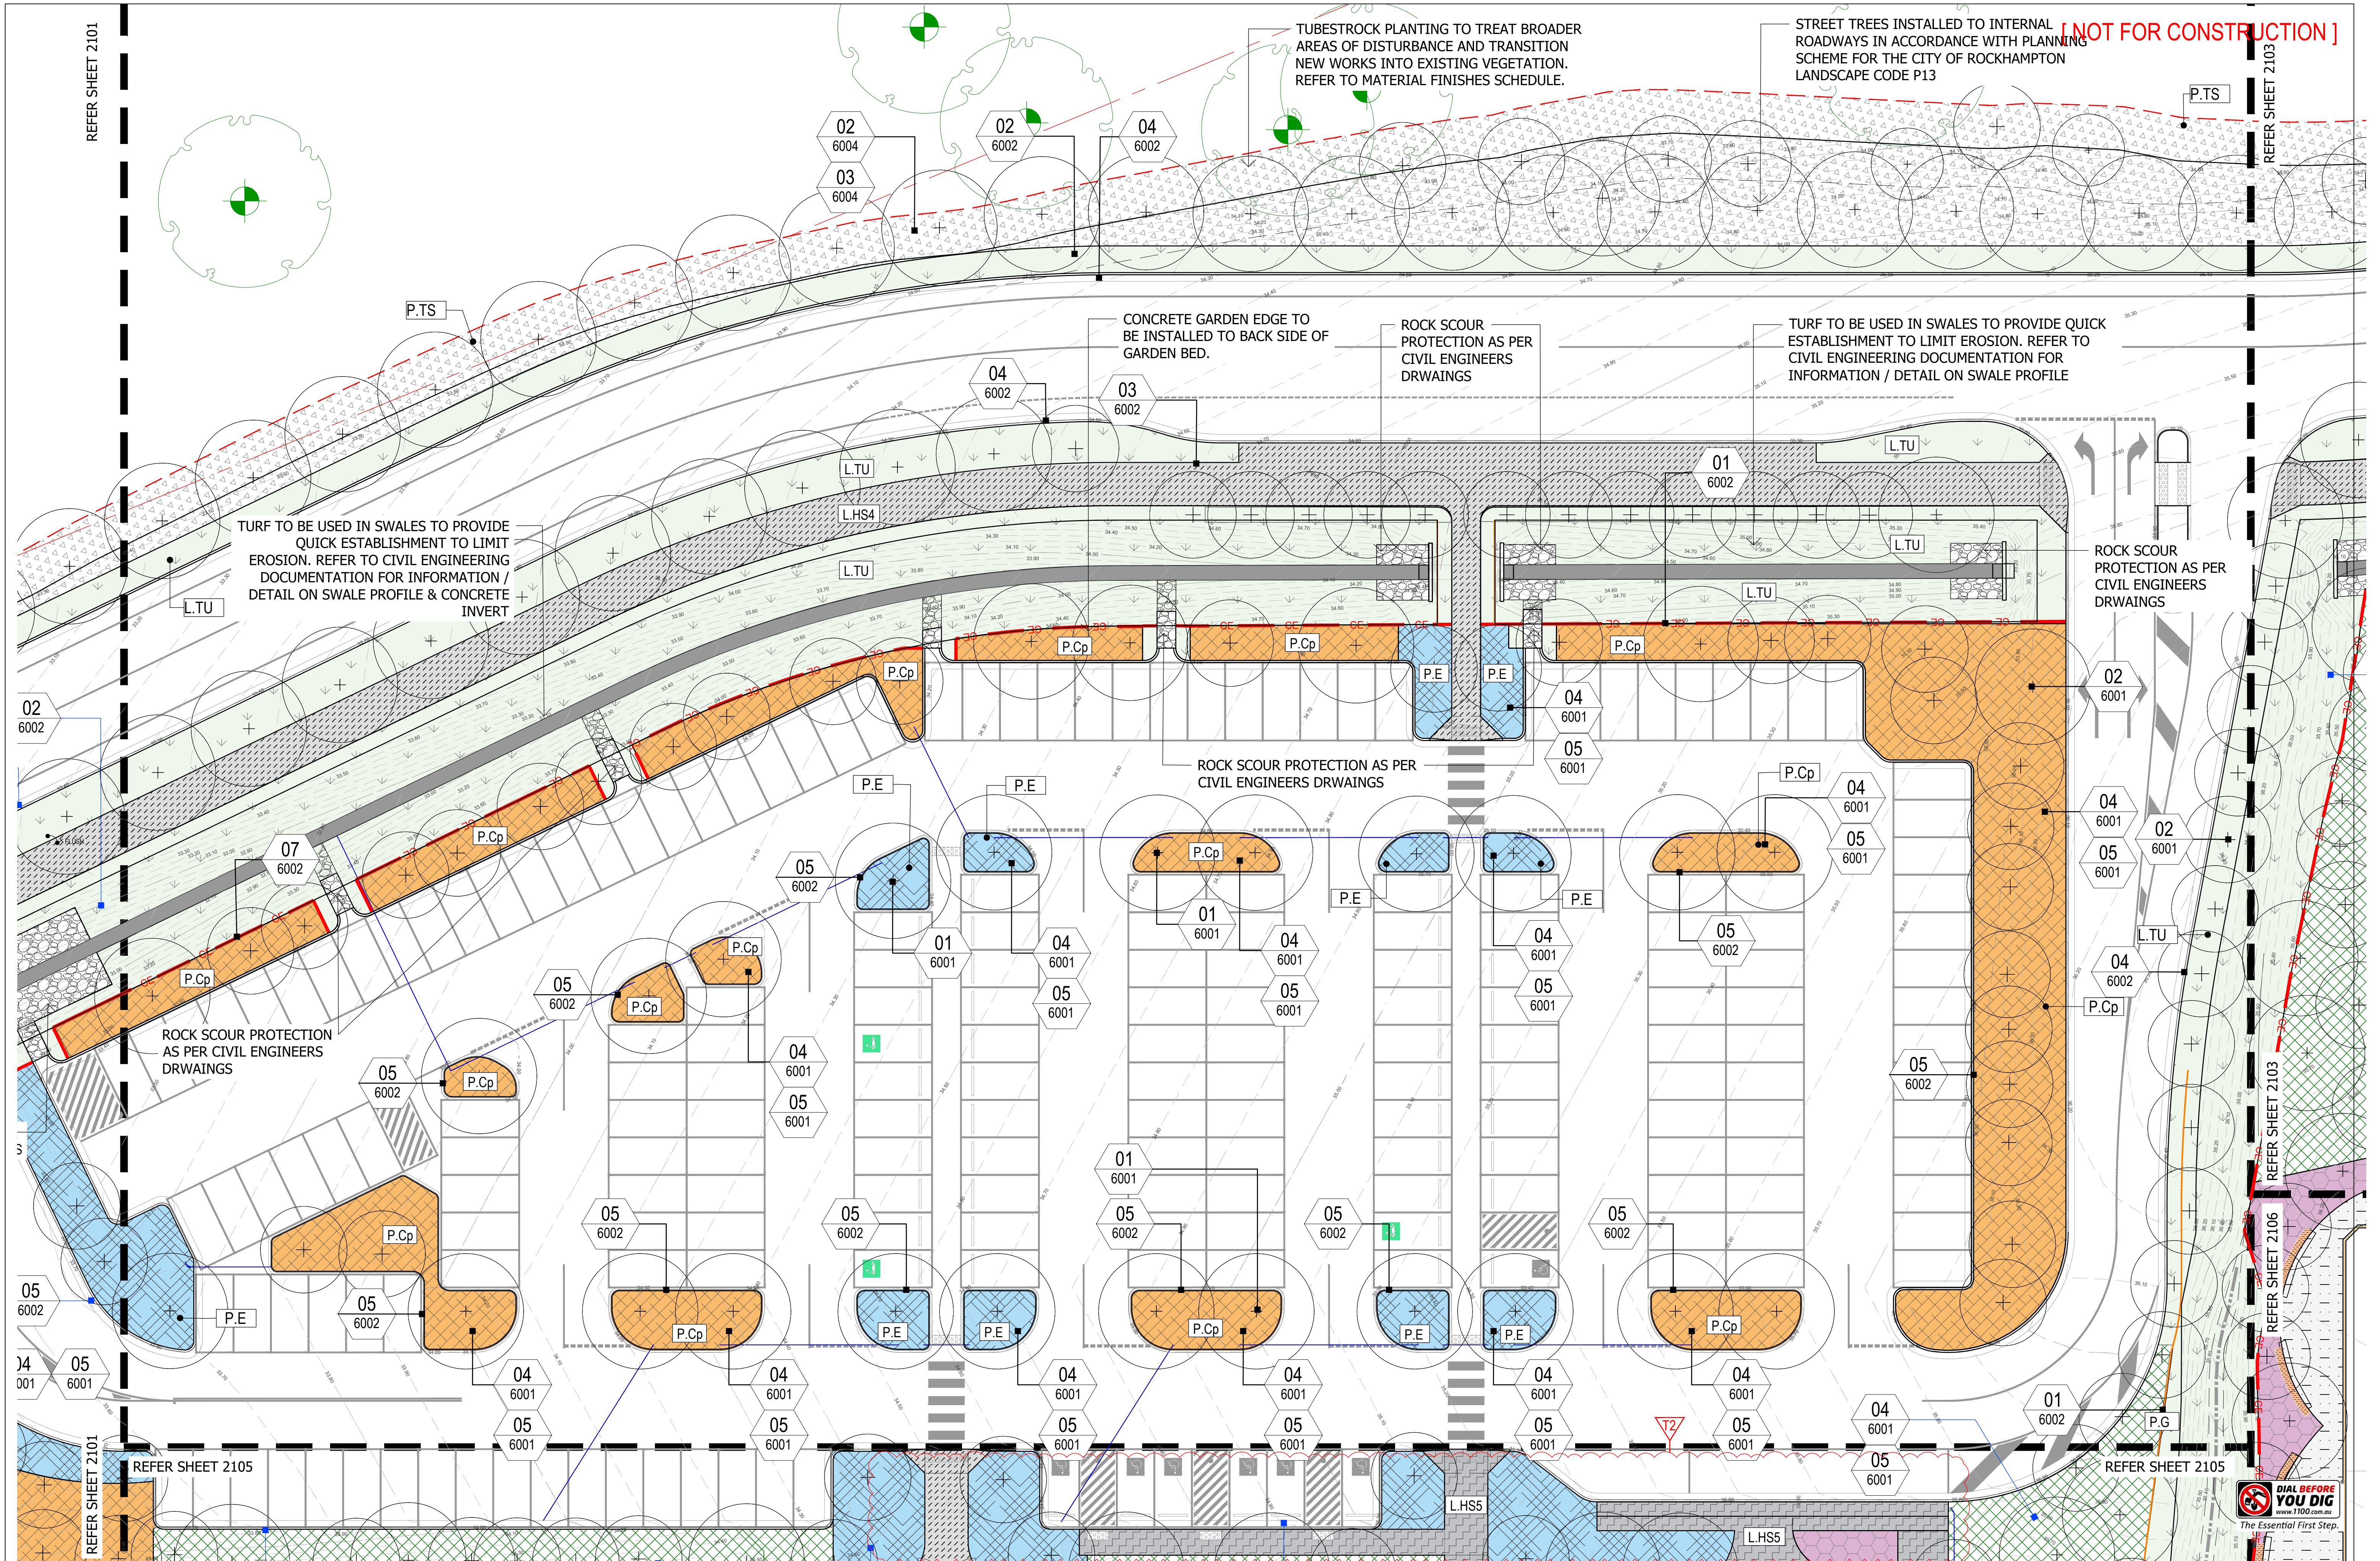

[NOT FOR CONSTRUCTION]

REV	DESCRIPTION	AUTH	CHK	DATE	- These designs and plans are the copyright of MODE DESIGN Corp. Pty Ltd and cannot be reproduced without written permission. - Verify all dimensions on site prior to commencement of work. DO NOT scale off these drawings. - Report any discrepancies to MODE before carrying out any work. - Where service locations are shown on the drawings they are indicative only. The exact location of existing services is to be confirmed on site by the contractor prior to commencement of work. Dial Before You Dig - Ph 1100. Refer to Service Engineer's drawings for the location of all proposed services.	SCALE 1:200 0m 2 4 6 8 10	NORTH 	CLIENT 	CONSULTANTS 	BRISBANE Turbal and Yuggera Country 826 Ann St Fortitude Valley QLD 4006 T +61 7 3253 9900 bne@modedesign.com.au ABN: 65 112 807 931	PROJECT Rockhampton Sports Precinct Stage 1 544-700 Yaamba Rd, Norman Gardens, QLD This project is located on Durumbal Land	DRAWING TITLE SURFACE FINISHES PLAN 02	PROJECT STAGE ISSUE FOR TENDER			
T1	ISSUE FOR TENDER	CE	AW	18.06.2026									MODE PROJECT No 24523	STAGE IFT	DRAWING No LD-2102	REVISION T2
T2	ISSUE FOR TENDER - RESPONSES TO TC011	LM	CE	14.07.2026												