




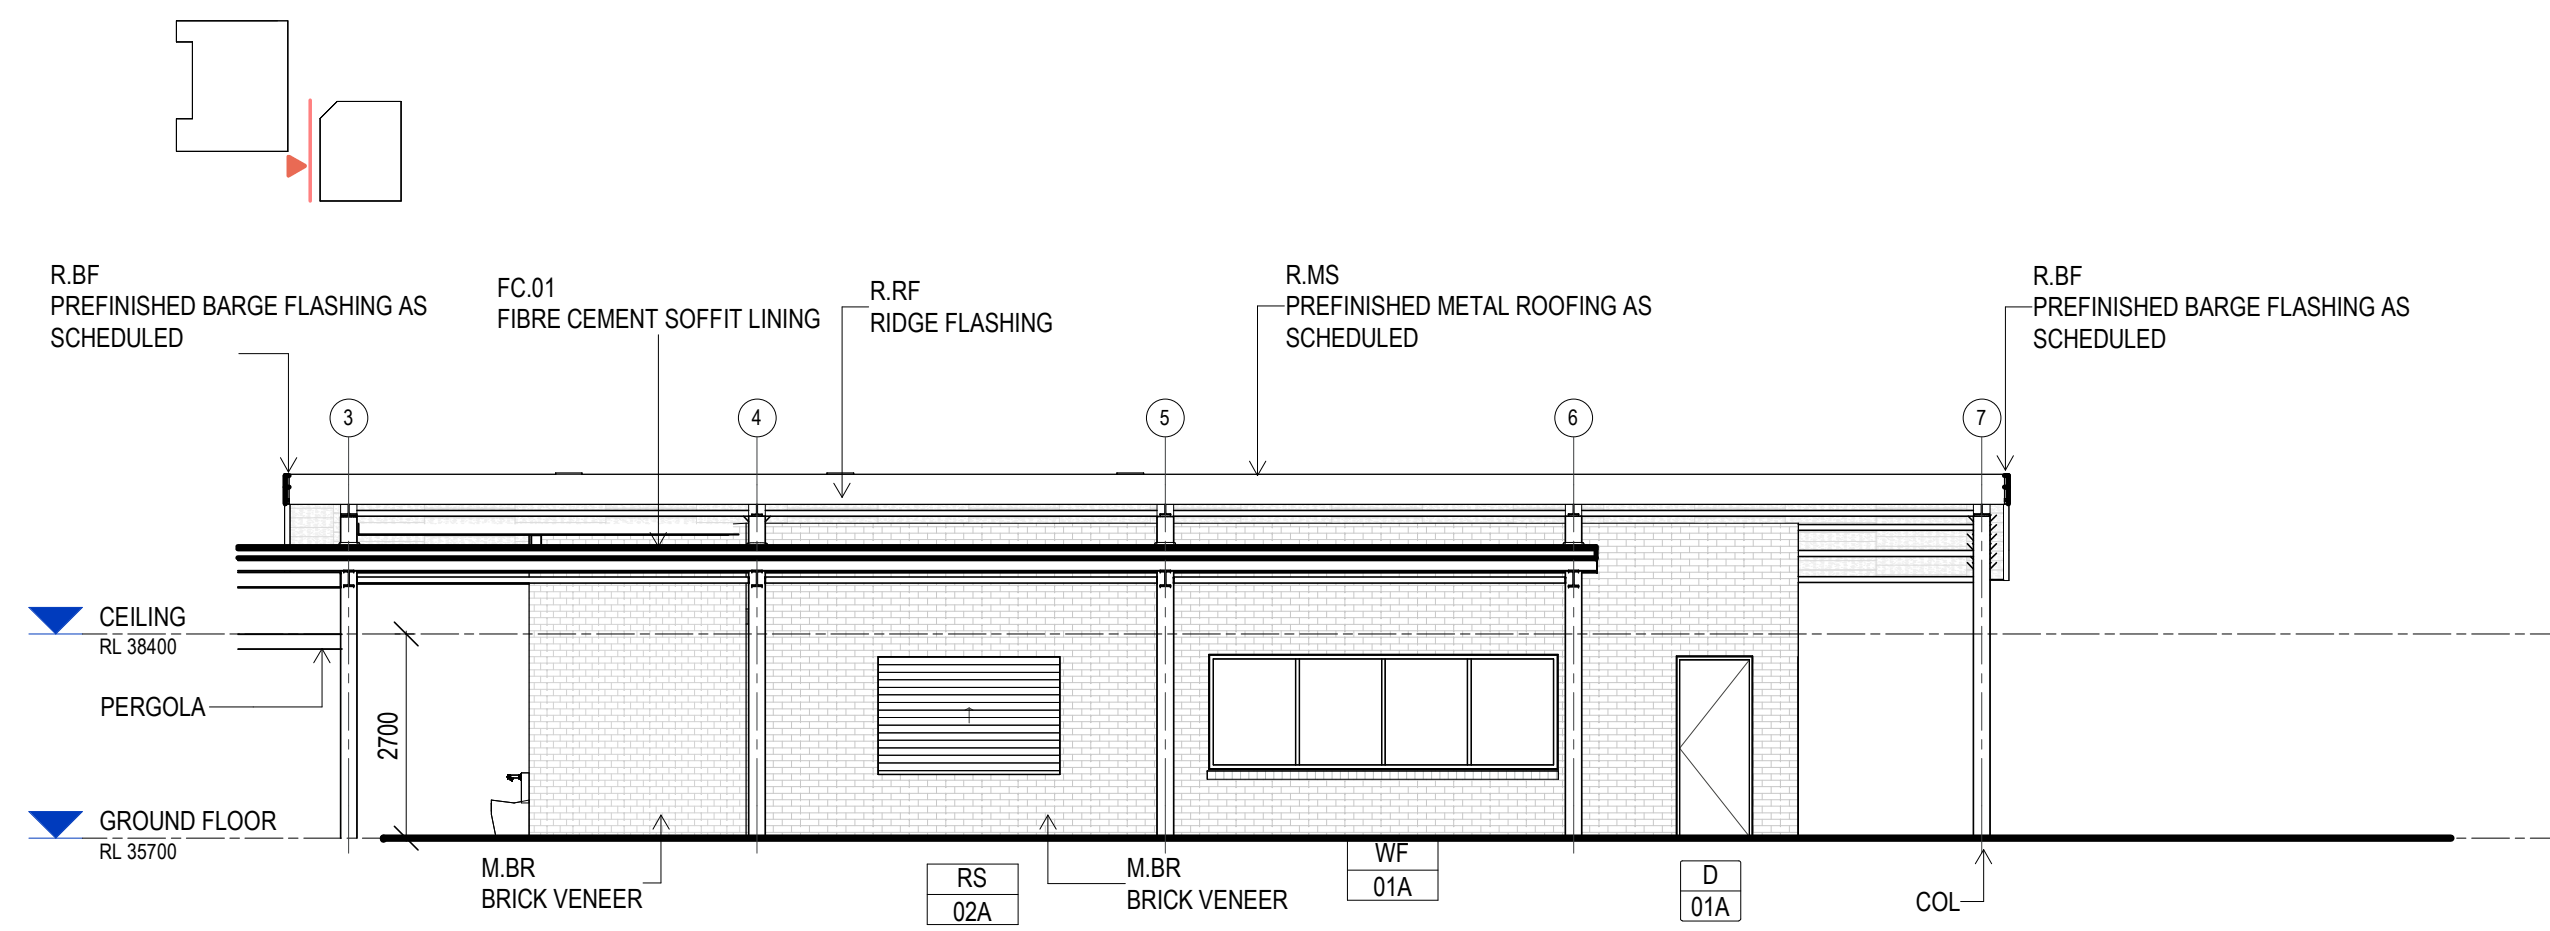


1 ELEVATION WEST
Scale: 1 : 100

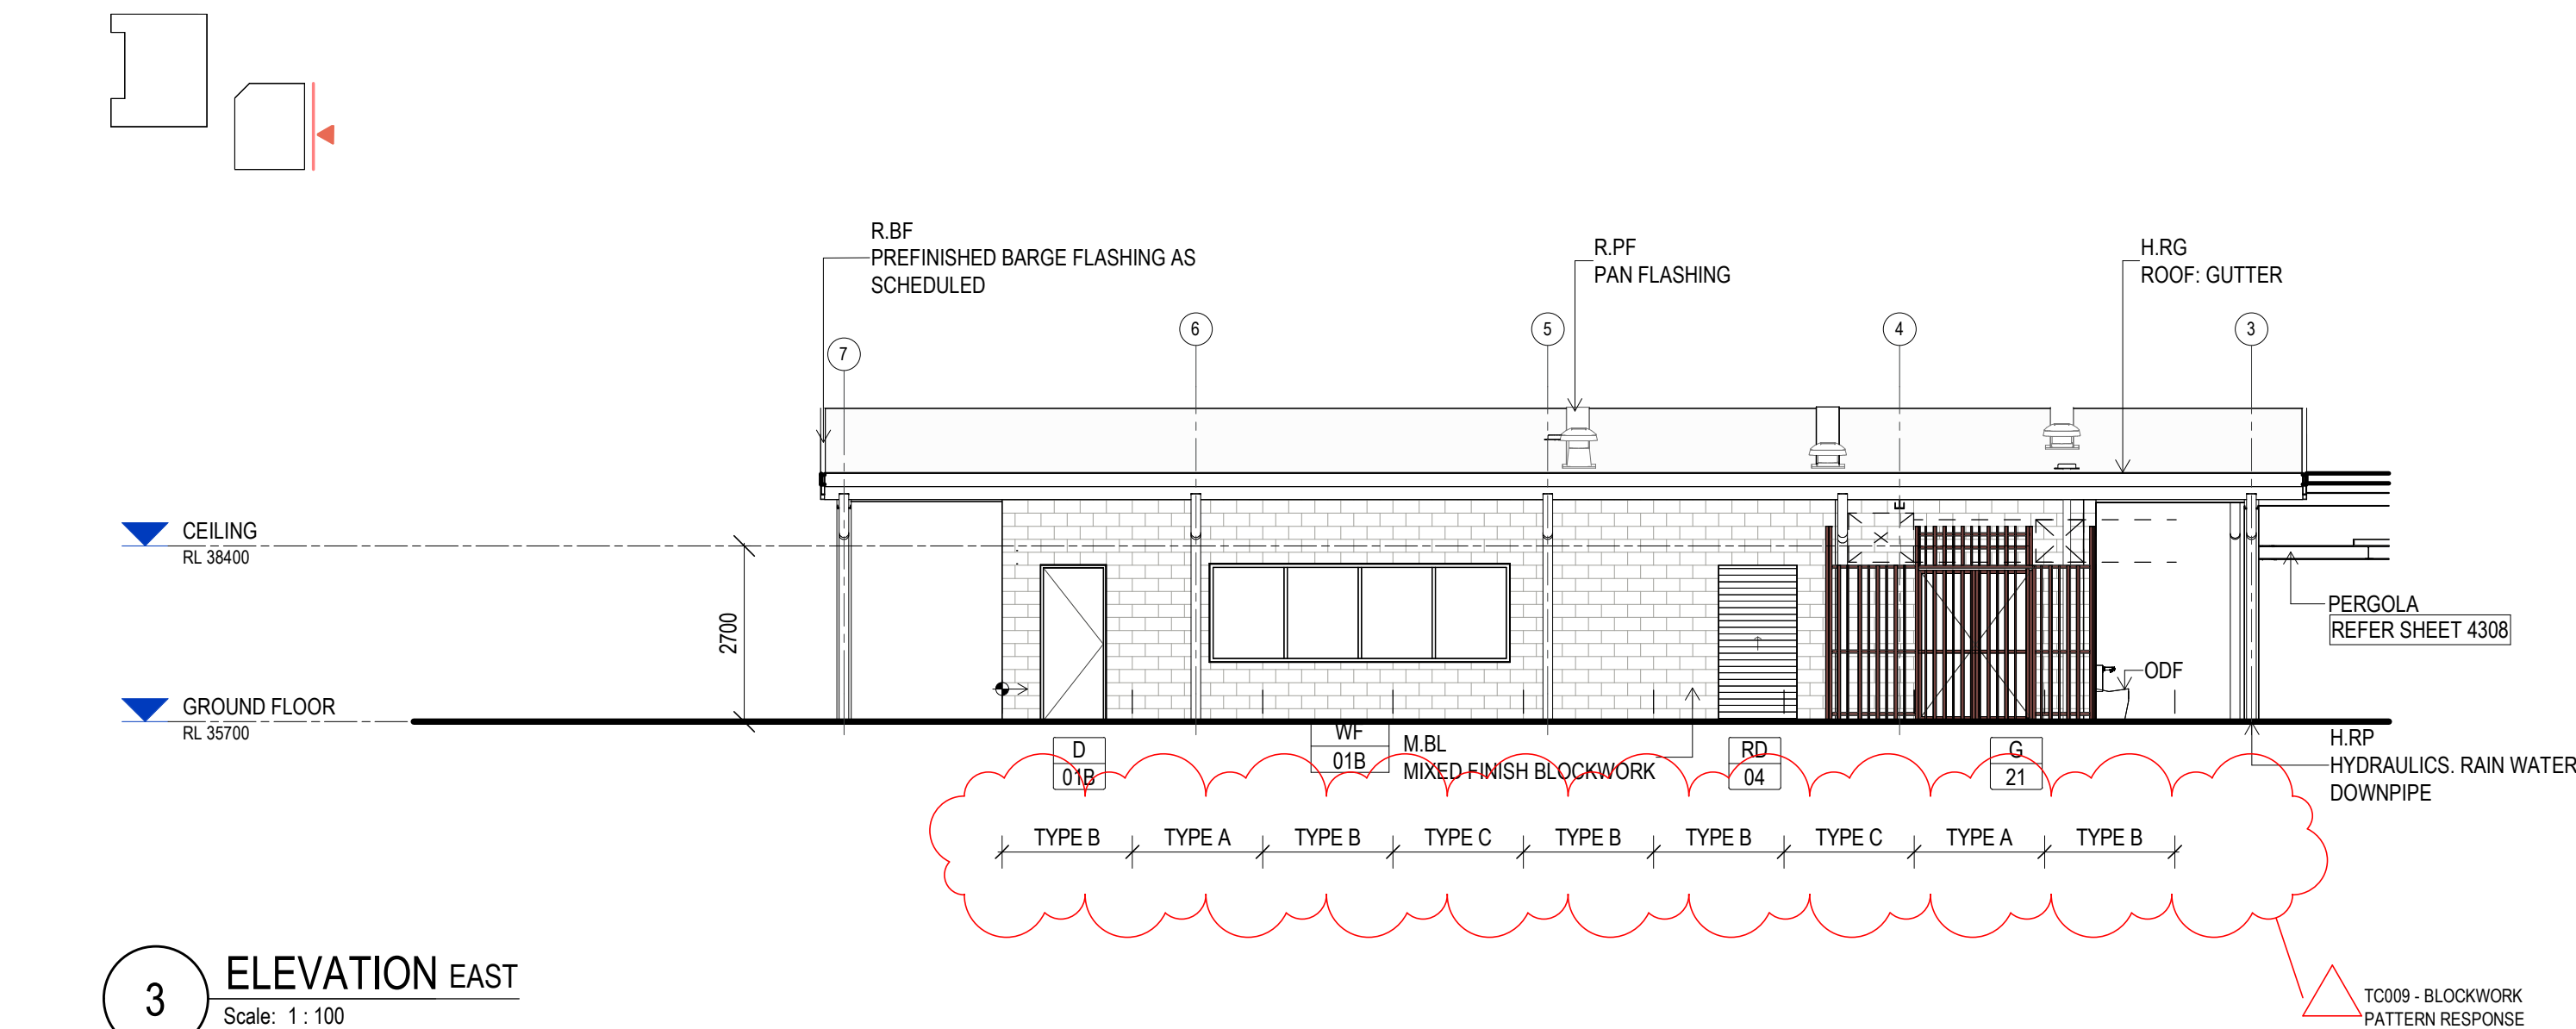


3 ELEVATION EAST
Scale: 1 : 100

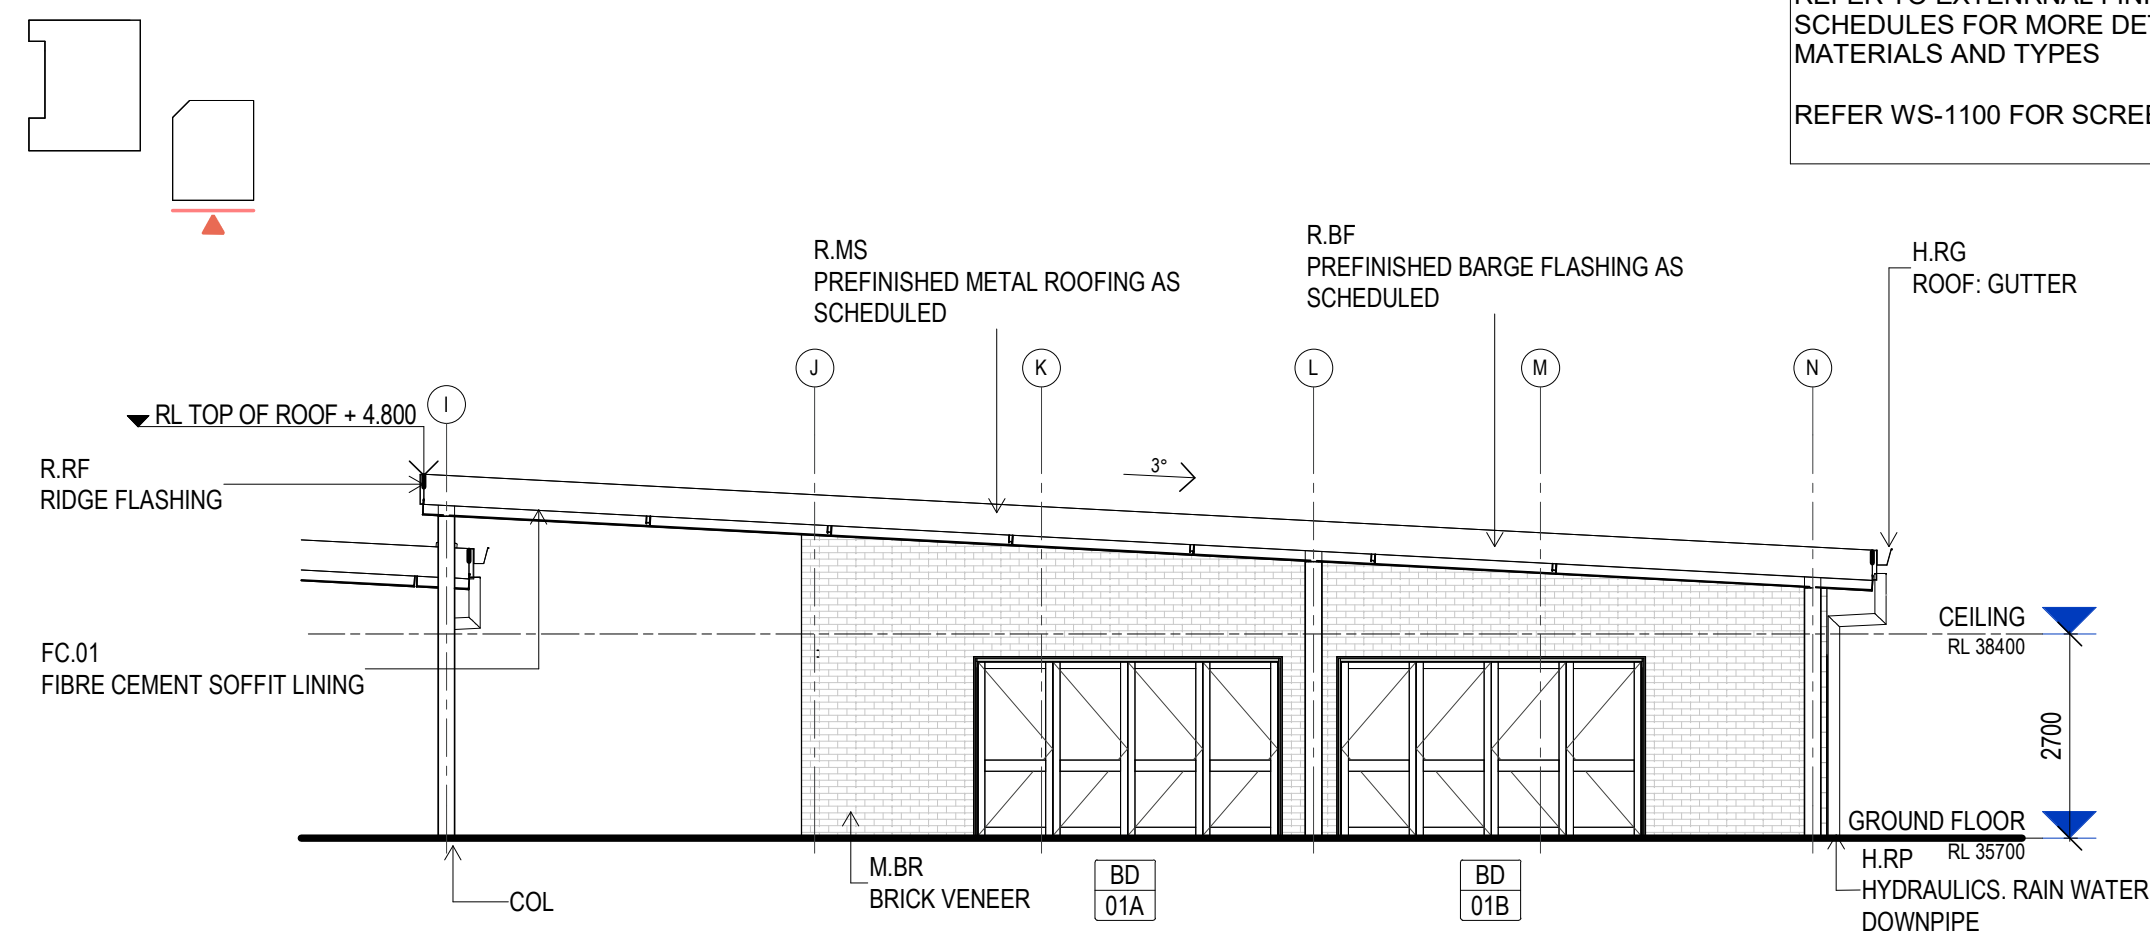


2 ELEVATION SOUTH
Scale: 1 : 100

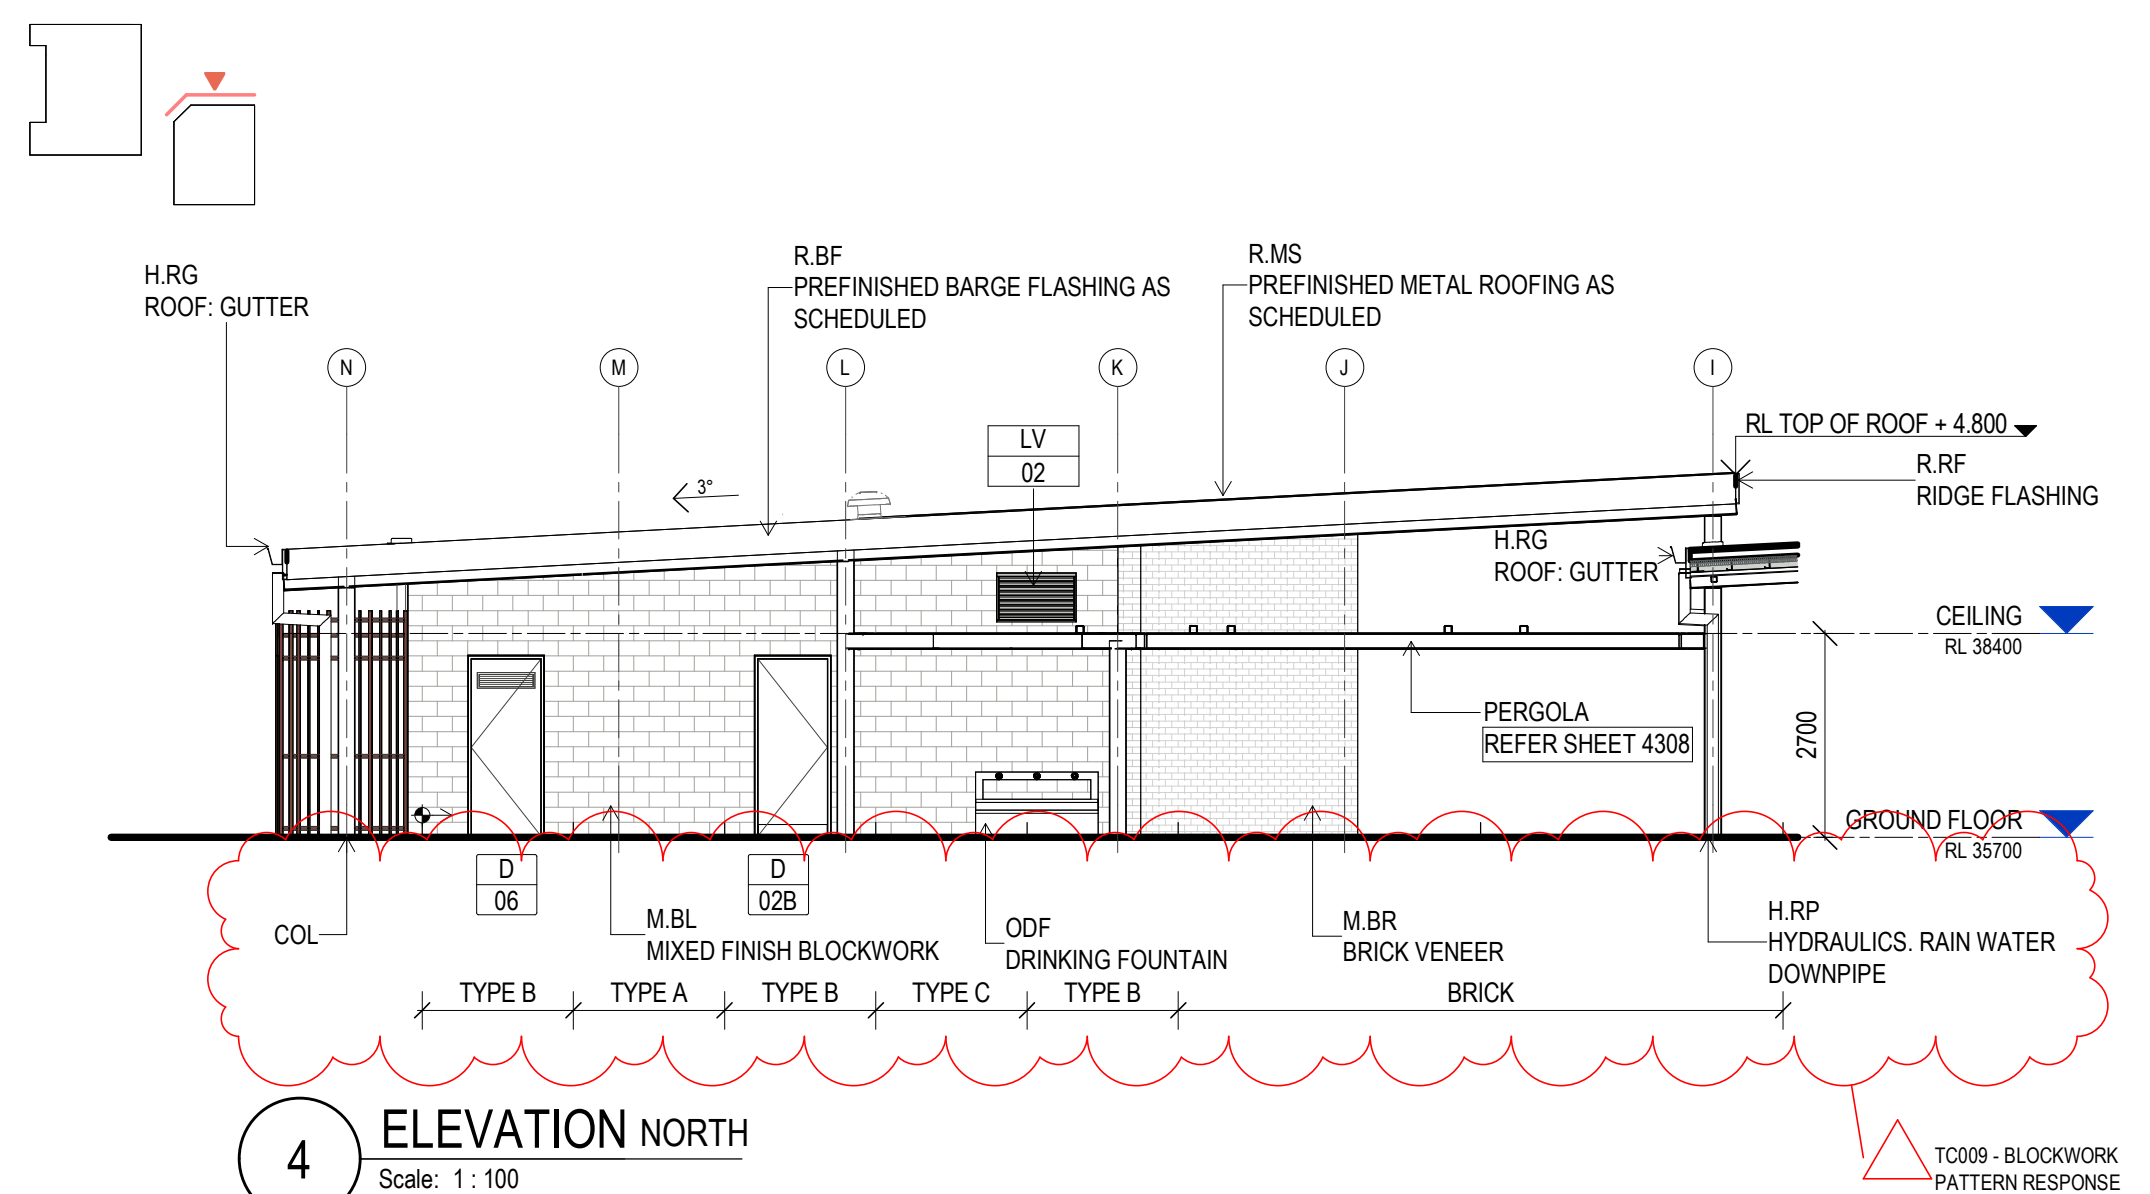


4 ELEVATION NORTH
Scale: 1 : 100

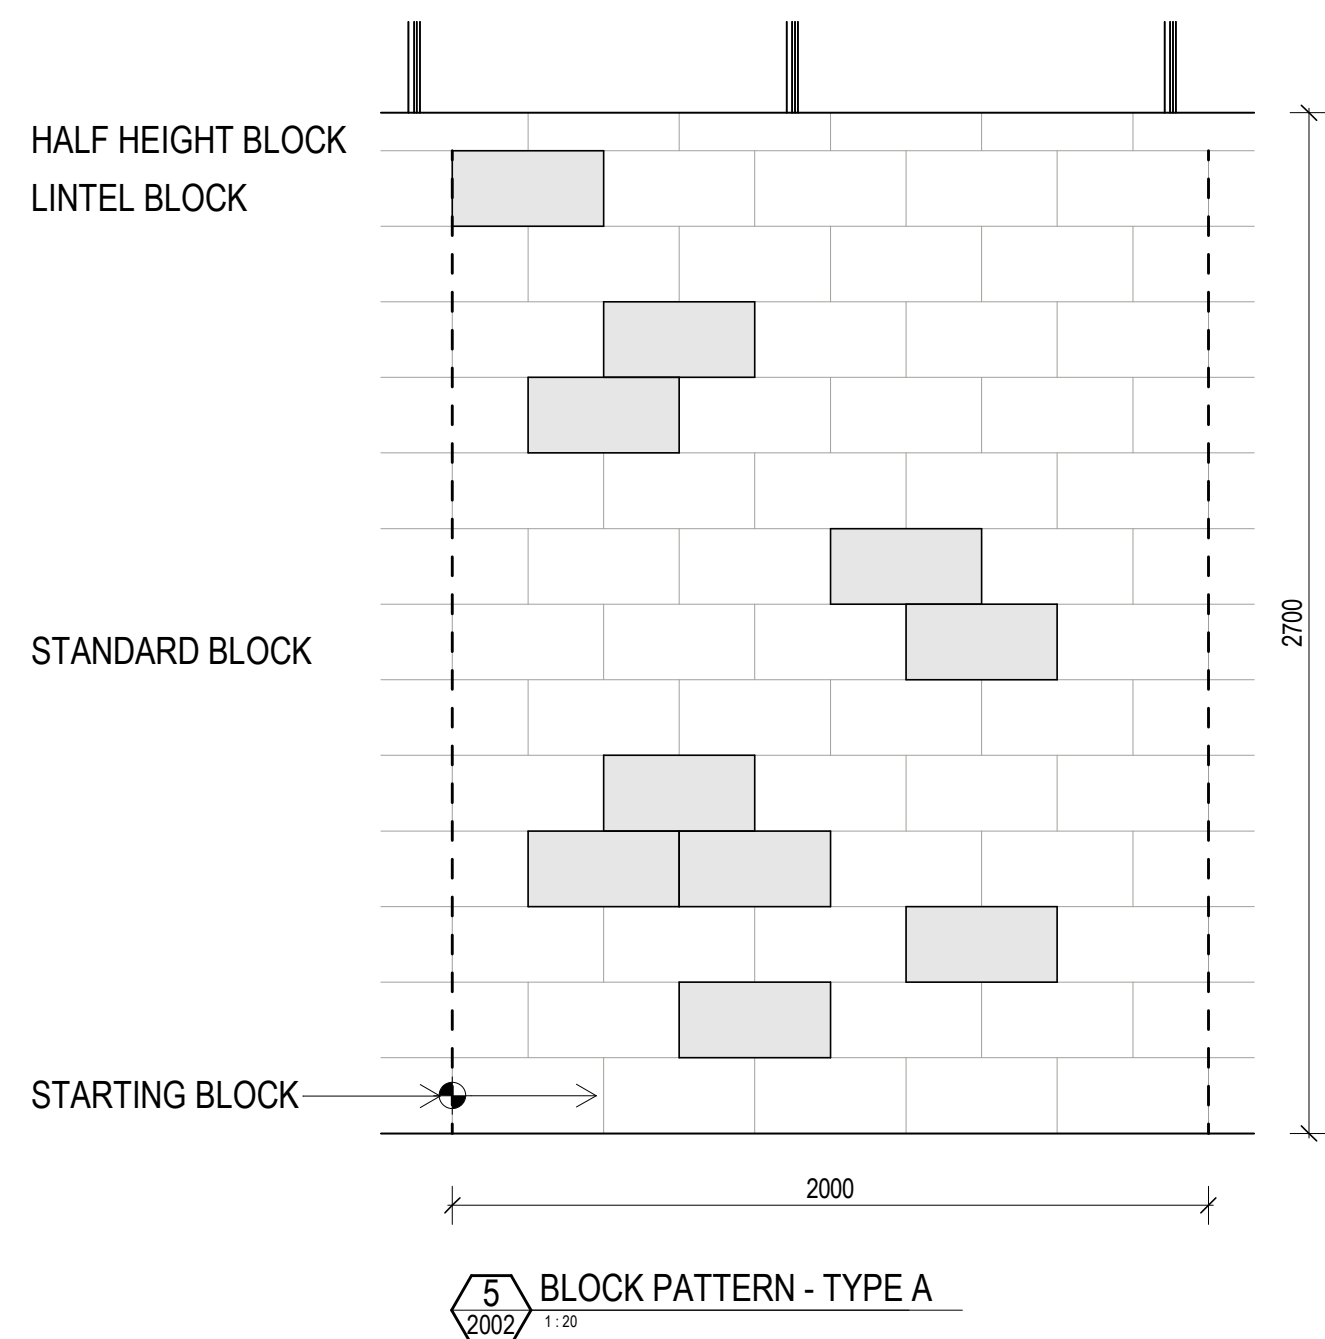

5 BLOCK PATTERN - TYPE A
2002 1:20

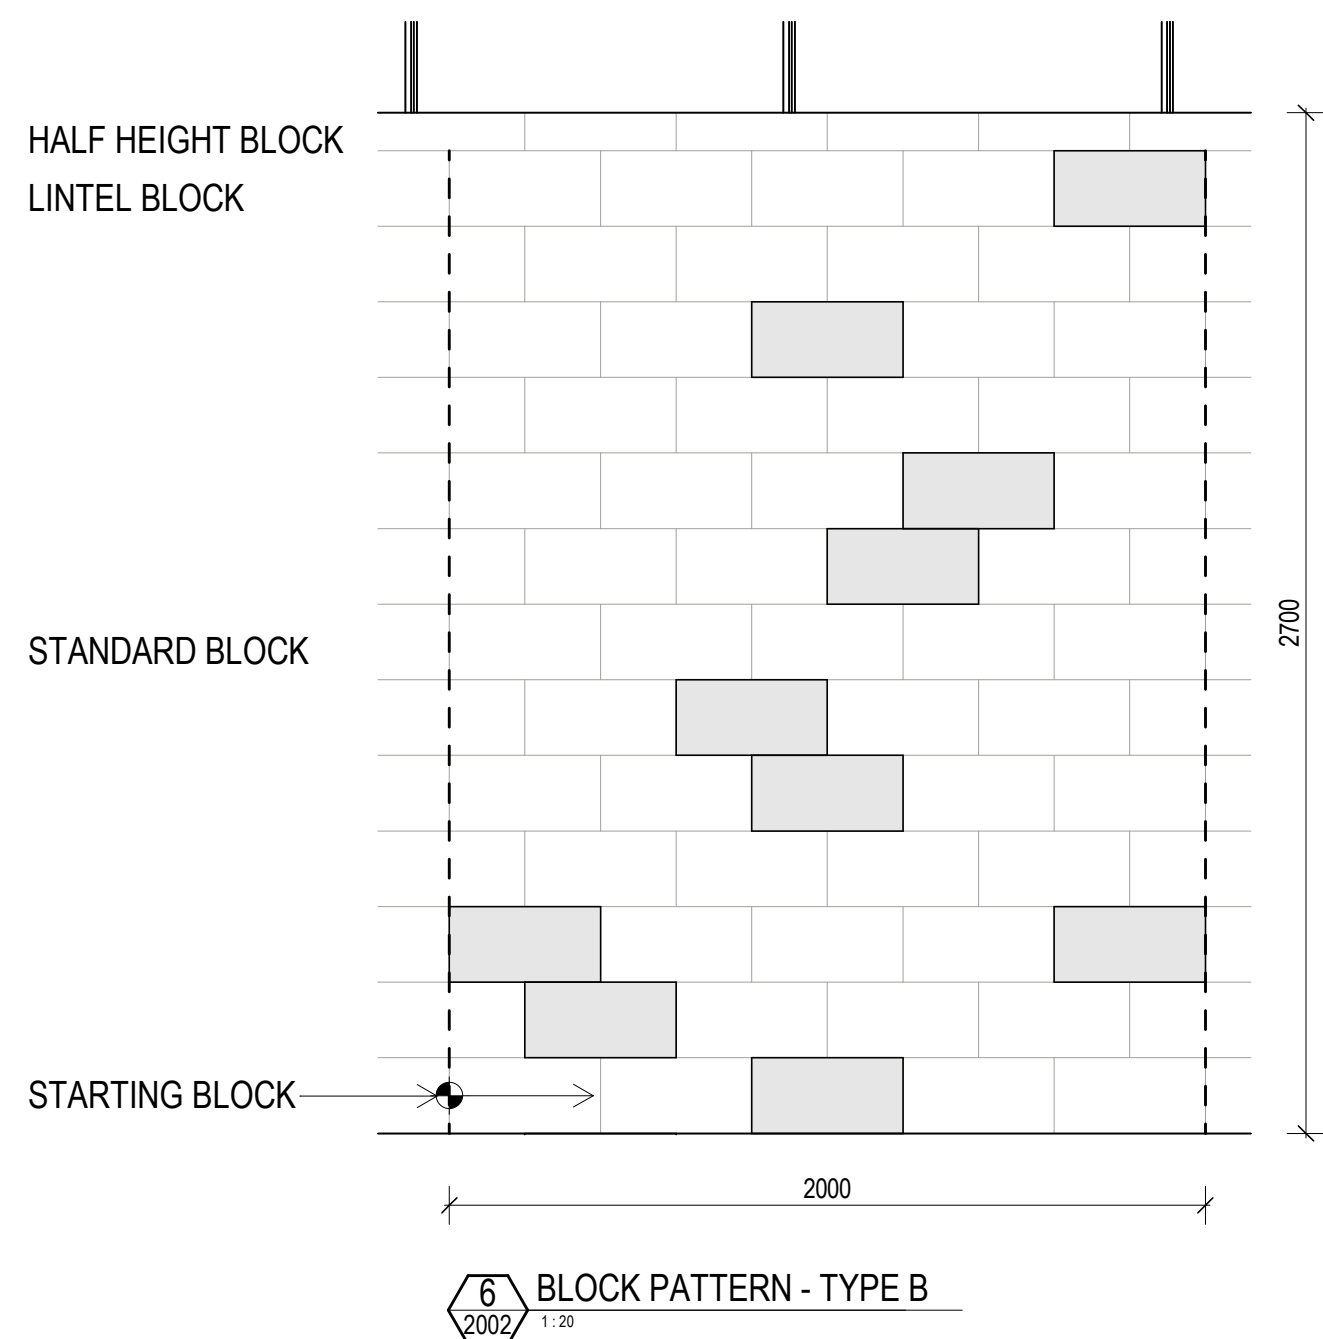

6 BLOCK PATTERN - TYPE B
2002 1:20

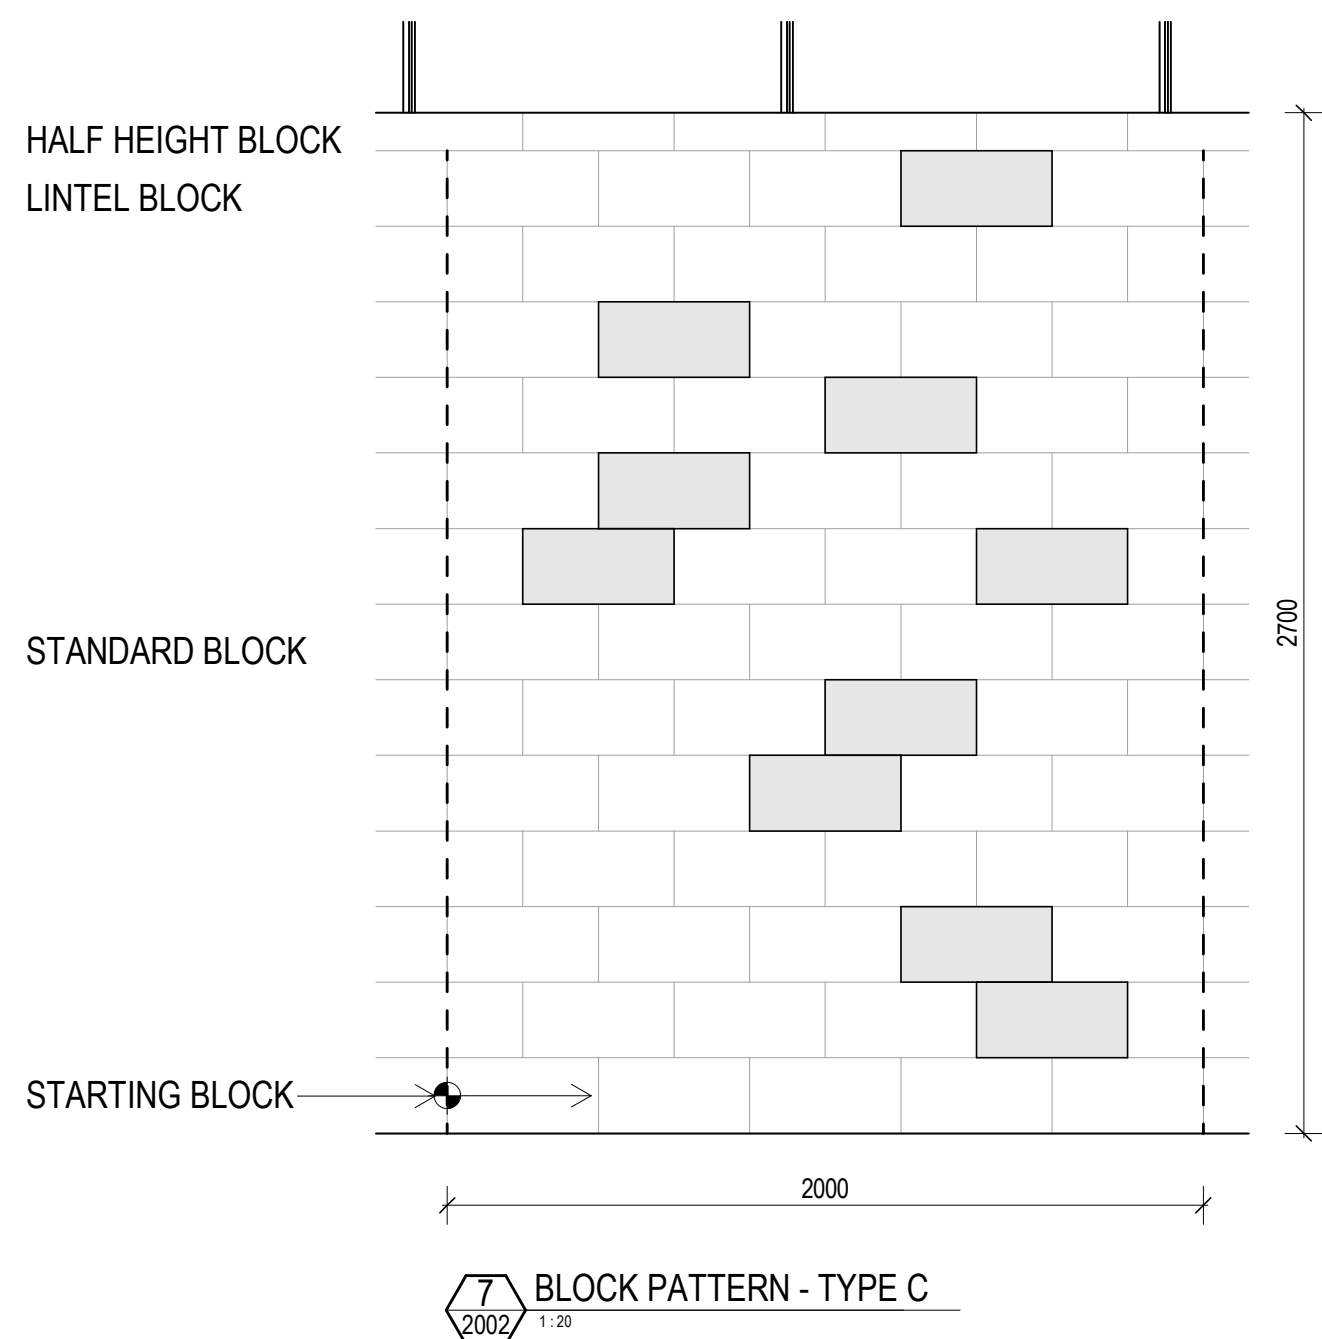

7 BLOCK PATTERN - TYPE C
2002 1:20

PATTERN STRATEGY:

PREDOMINANTLY HONED (OR STANDARD) FINISH BLOCKWORK WITH POLISHED FEATURE BLOCKS. PROVIDE A MAXIMUM OF 10 POLISHED BLOCKS PER 2.0 M WALL LENGTH, ARRANGED GENERALLY IN ACCORDANCE WITH PATTERN TYPES A, B AND C SHOWN. PATTERN MAY BE ADJUSTED AT CORNERS, WALL JUNCTIONS AND OPENINGS, WHERE HONED (OR STANDARD) BLOCKS SHALL CONTINUE AND THE PATTERN RECOMMENCED BEYOND THE INTERRUPTION.

LIGHT GREY HATCH DENOTES POLISHED BLOCKWORK; ALL UNSHADED BLOCKS DENOTE HONED (OR STANDARD) FINISH BLOCKWORK.

LIGHT GREY HATCH = POLISHED BLOCKWORK
NO HATCH = HONED (OR STANDARD) FINISH BLOCKWORK

POLISHED BLOCK SPEC : (SPECIFIED OR SIMILAR)
SUPPLIER : NATIONAL MASONRY
RANGE : POLISHED FACE
COLOR : PEARL GREY

SYMBOL DENOTES STARTING BLOCK SET-OUT POINT AND DIRECTION.

NOTE :
REFER TO EXTENRNAL FINISHES SCHEDULES FOR MORE DETAILS ON MATERIALS AND TYPES
REFER WS-1100 FOR SCREEN PATTERN

These designs and plans are the copyright of MODE DESIGN Corp. Pty Ltd and cannot be reproduced without written permission.
• Verify all dimensions on site prior to commencement of work.
• DO NOT scale off these drawings.
• Report any discrepancies to the architect before carrying out any work.

AMENDMENTS				
REV	DESCRIPTION	AUTH	CHK	DATE
T1	ISSUE FOR TENDER	DW	GB	18/06/26
T2	TENDER QUERY RESPONSE	DS	SM	13/07/2026

NOTE:
- REFER TO AR-NBC-0010 FOR CODE LIST.

NOM. REG. Architect: Rhonan O'Brien QLD 2350 NSW 7176 VIC 16182
TAS 1216 NZ 4712, Peter Bertram QLD 2333 WA 2143 NT AR1213

STATUS
ISSUED FOR TENDER

0m 1 2 3 4 5

BRISBANE
mode
Plaza Level, Mosaic
826 Ann St
Fortitude Valley QLD 4006
T +61 7 3253 9900
bne@modedesign.com.au
ABN: 65 112 807 931

Rockhampton
Regional Council

CLIENT
SPORTENG™

PROJECT
ROCKHAMPTON NETBALL CENTRE (STAGE 1) - NETBALL CLUBHOUSE
554-700 YAAMBA ROAD, NORMAN GARDEN - 4701
DRAWING TITLE
ELEVATIONS - SHEET 02

DRAWN DW	CHECKED SM
ISSUE 13/07/2026 12:39:16 PM As indicated	SCALE @ A1 As indicated
PROJECT No 24523	STAGE IFT
DRAWING No AR-NBC-2002	REVISION T2