

Diagram illustrating the construction details for a Double Rebate (Wrapping Wall). The diagram shows a cross-section of the wall and door assembly with the following dimensions and components:

- Dimensions:**
 - Top horizontal dimension: 40 (Grout fill) and 15 (Insulation).
 - Left vertical dimension: 15 (Grout fill) and 15 (Insulation).
 - Right vertical dimension: 15 (Grout fill).
- Construction Details:**
 - GROUT FILL DOOR FRAMES TO CONCRETE & BLOCK WALLS:** Indicated by arrows pointing to the top and side grout fills.
 - PROVIDE INSULATION TO FRAME WHERE WALL IS INSULATED:** Indicated by an arrow pointing to the insulation layer on the right side of the frame.
 - DOOR PANEL:** Indicated by an arrow pointing to the door panel.
 - DOUBLE REBATE (WRAPPING WALL):** The overall construction detail shown.

FINISHES

AN	ANODISED ALUMINIUM - CLEAR
GL	FRAMELESS GLASS
PT	PAINT
PC	POWDERCOAT
GALV	GALVANISED

NOTE :
REFER TO EXTERNAL FINISHES
SCHEDULES FOR MORE DETAILS
MATERIALS AND TYPES

The image contains two technical drawings of door panel elevations, labeled 'PANEL ELEVATION NON-GLASS DOOR' and 'PANEL ELEVATION GLASS DOOR'.

PANEL ELEVATION NON-GLASS DOOR: This drawing shows a rectangular door panel. Key dimensions and labels include:


- DOOR PANEL WIDTH** (top horizontal dimension)
- DOOR PANEL HEIGHT** (left vertical dimension)
- HEIGHT OF HANDLE** (1000, left vertical dimension)
- UNDERCUT (IF REQUIRED)** (left vertical dimension)
- GR** (Door Grille, located in the lower center)
- KP** (Kick Plate, located at the bottom)
- GR WIDTH** (bottom horizontal dimension for the grille)
- 250 KP HEIGHT** (vertical dimension for the kick plate)
- 300 GR HEIGHT** (vertical dimension for the grille)
- KICK PLATE (KP) WHERE SCHEDULED** (label pointing to the KP)
- DOOR GRILLE (GR) WHERE SCHEDULED** (label pointing to the GR)
- DOOR FRAME** (label pointing to the frame area)
- VISUAL INDICATORS (TYP)** (label pointing to the handle area)
- LATCH SIDE** (label at the bottom center)

PANEL ELEVATION GLASS DOOR: This drawing shows a rectangular door panel with a glass section. Key dimensions and labels include:

- DOOR PANEL WIDTH** (top horizontal dimension)
- 60** (width of the side glass sections)
- AL** (Aislamiento, top left corner label)
- GL** (Glass, top right corner label)
- 100** (height of the glass section)
- LATCH SIDE** (label at the bottom center)

TYPE	WINDOW CODE	OPERATION	WINDOW DIMENSIONS		SILL HEIGHT	CONSTRUCTION		COMMENTS
			FRAME WIDTH	FRAME HEIGHT		FRAME TYPE	FRAME FINISH	
WF	01A	FX	4620	1520	920	MF	PT	WINDOW: FIXED
WF	01B	FX	4620	1520	920	MF	PT	WINDOW: FIXED
RS	02A	R	2400	1555	845	MF	PT	ROLLER SHUTTER
RS	02B	R	2400	1555	845	AL	PC	ROLLER SHUTTER
WS	07	SL	3600	1500	920	MF	PT	WINDOW: SLIDING
WF	08A1	FX	810	1480	920	MF	PT	WINDOW: FIXED
WS	08A2	SL	3600	1500	920	MF	PT	WINDOW: SLIDING
WF	08A3	FX	810	1480	920	MF	PT	WINDOW: FIXED
WF	08B	FX	3520	1500	920	MF	PT	WINDOW: FIXED
WF	08C	FX	2575	1500	920	MF	PT	WINDOW: FIXED
WS	09A	SL	2720	1500	900	MF	PT	WINDOW: SLIDING
WF	09B	FX	3620	1500	920	MF	PT	WINDOW: FIXED
WF	12	FX	810	1480	920	MF	PT	WINDOW: FIXED

TYPE	LOUVER NUMBER	LOUVER DIMENSIONS				COMMENTS
		FRAME WIDTH	FRAME HEIGHT	HEAD HEIGHT	SILL HEIGHT	
LV	02	1050	650	3500	2850	LOUVER. REFER MECHANICAL DRAWINGS FOR SPECIFICATIONS

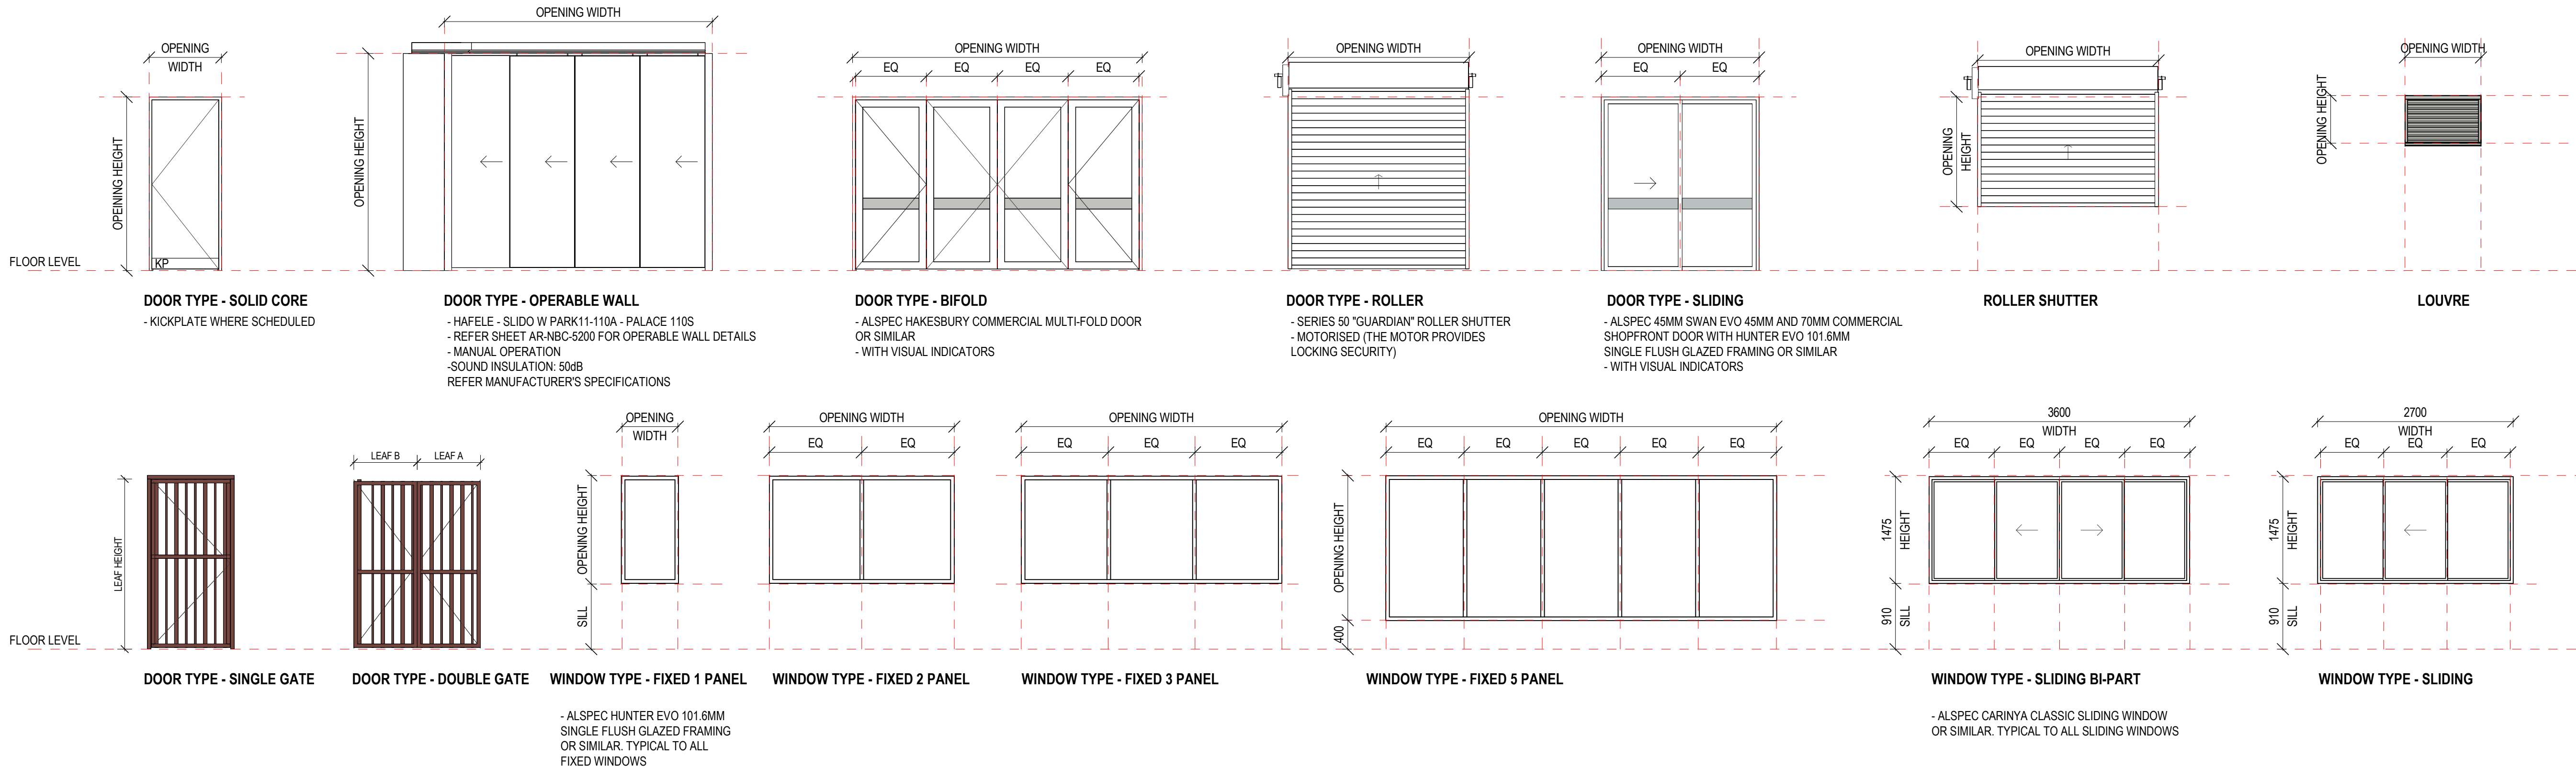

mode

BRISBANE

*Plaza Level, Mosaic
826 Ann St
Fortitude Valley QLD 4006
T +61 7 3253 9900
bne@modedesign.com.au
ABN: 65 112 807 931*



CLIENT

SPORTENG™

PROJECT
**ROCKHAMPTON NETBALL
CENTRE (STAGE 1) -
NETBALL CLUBHOUSE**
554-700 YAAMBA ROAD, NORMAN GARDEN - 4701

DRAWING TITLE
DOOR & WINDOW
SCHEDULES

DRAWN DW		CHECKED SM	
ISSUE 13/07/2026 3:51:11 PM		SCALE @ A1 As indicated	
PROJECT No 24523	STAGE IFT	DRAWING No AR-NBC-5102	REVISION T2