




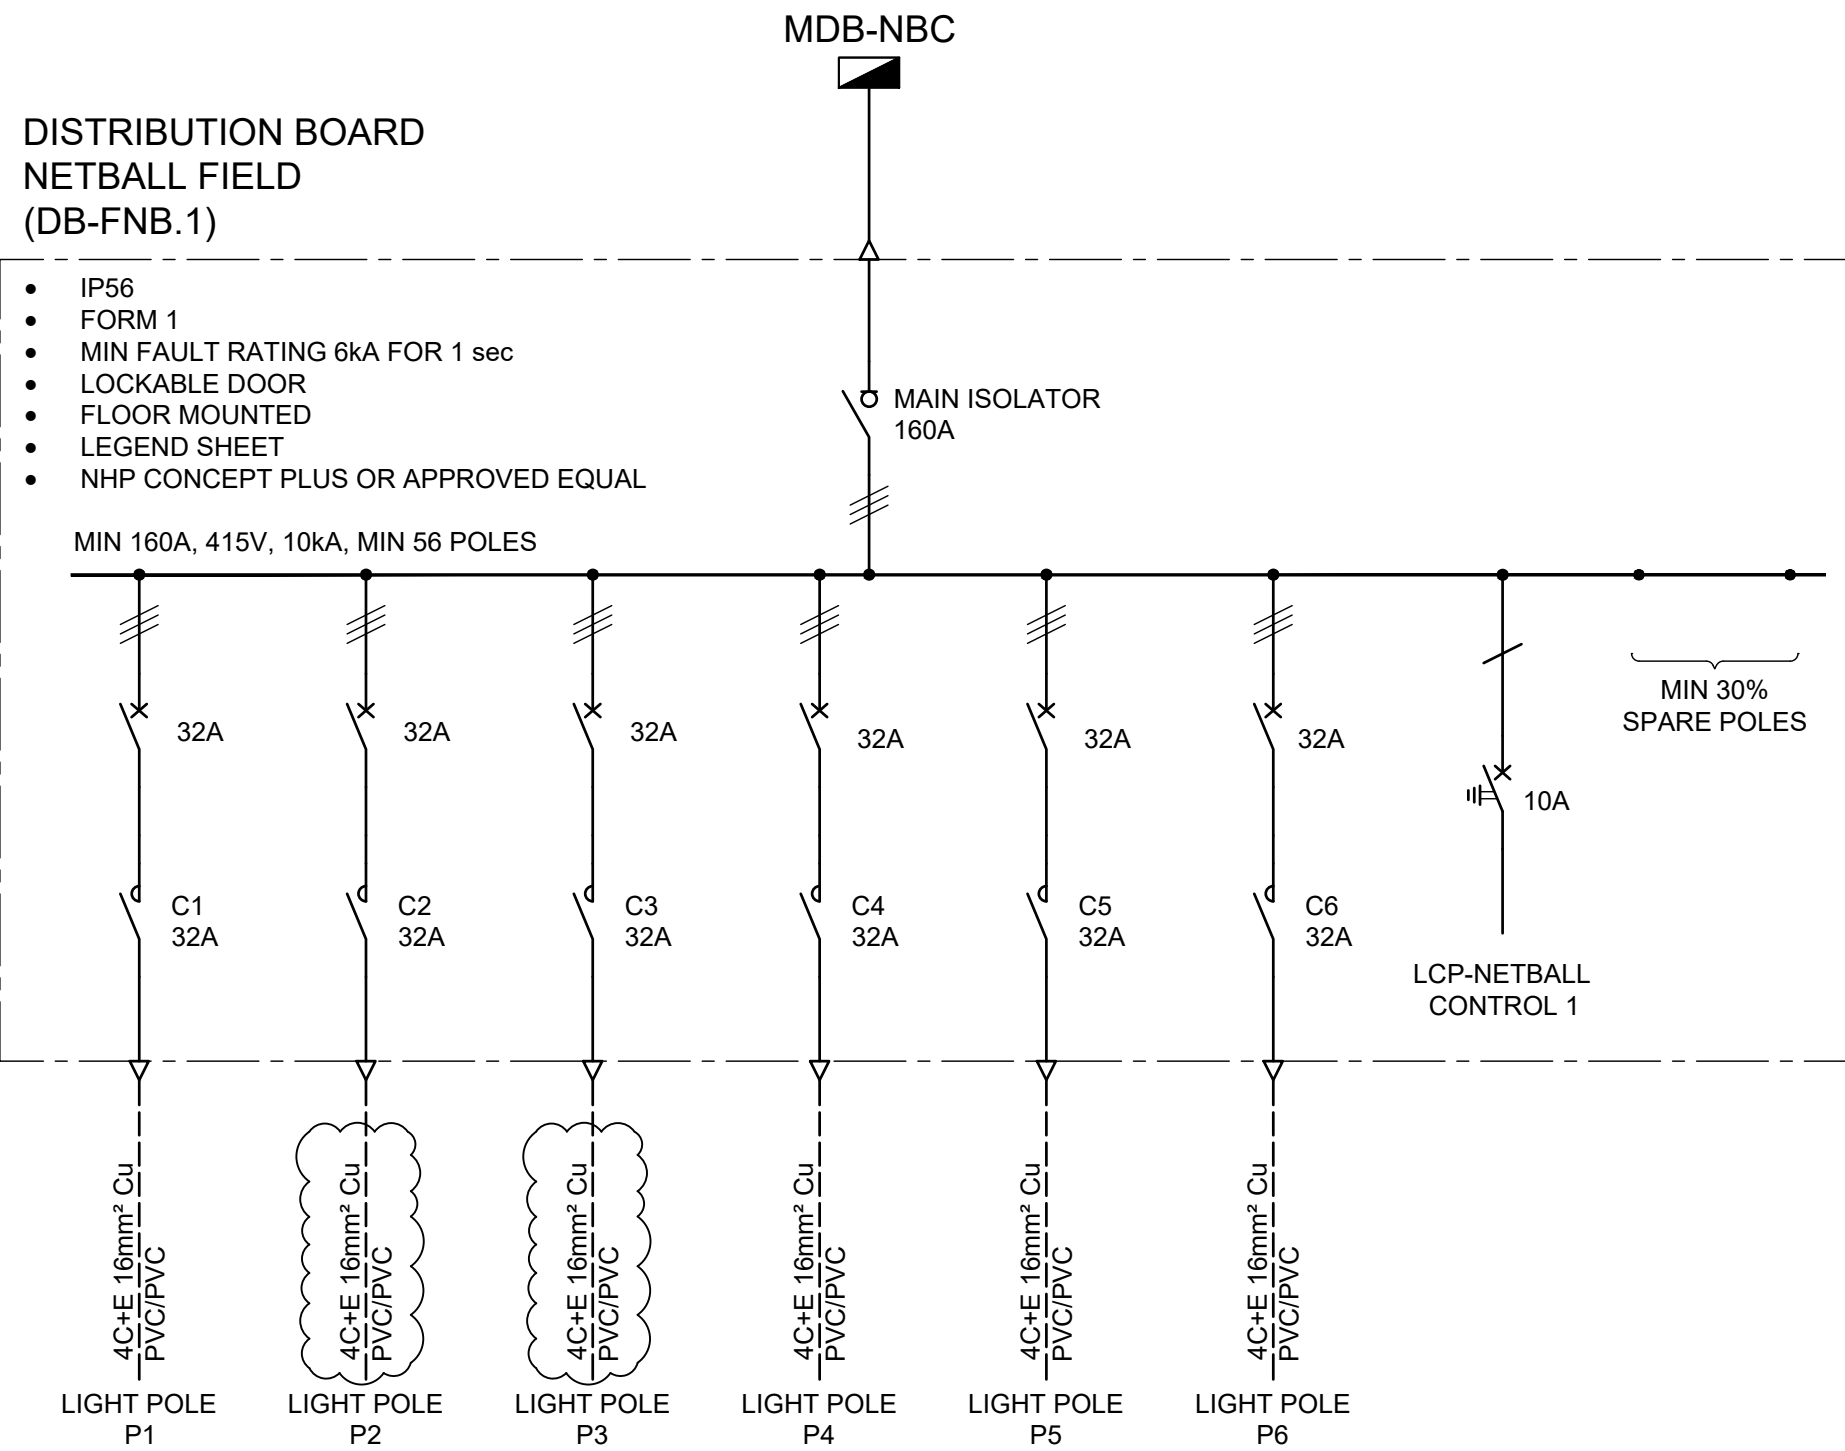


**NETBALL FIELD DISTRIBUTION
BOARD SLD (DB-FNB.1)**
NTS

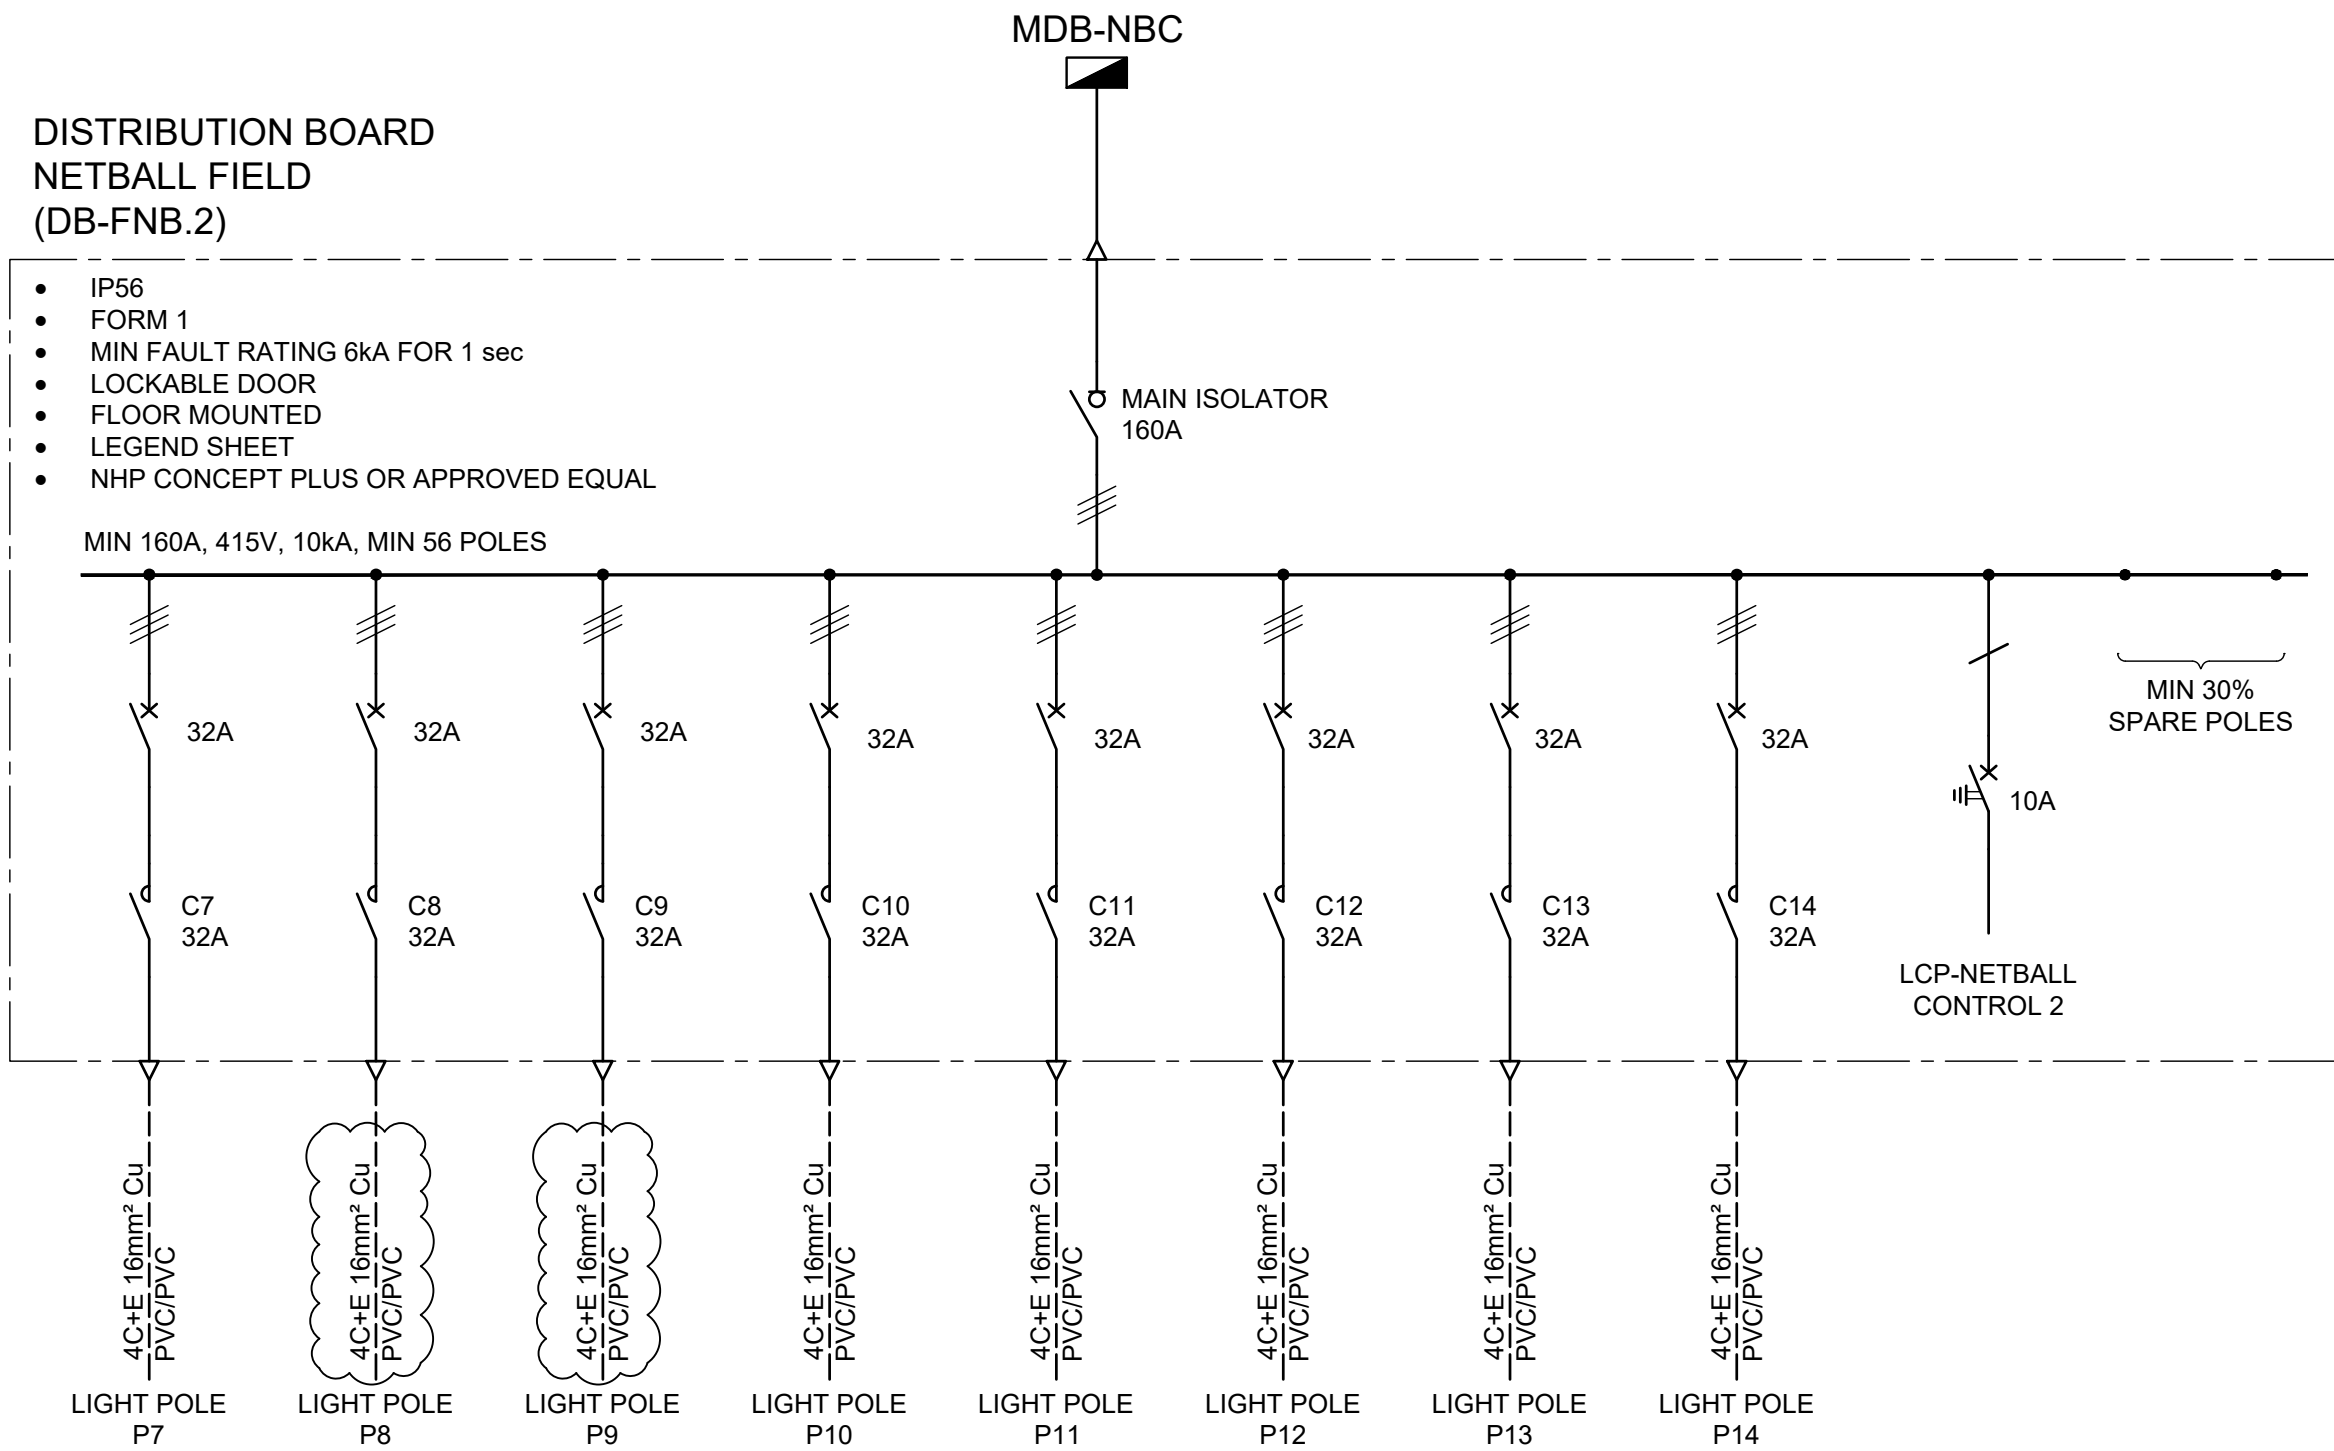

**NETBALL FIELD DISTRIBUTION
BOARD SLD (DB-FNB.2)**
NTS

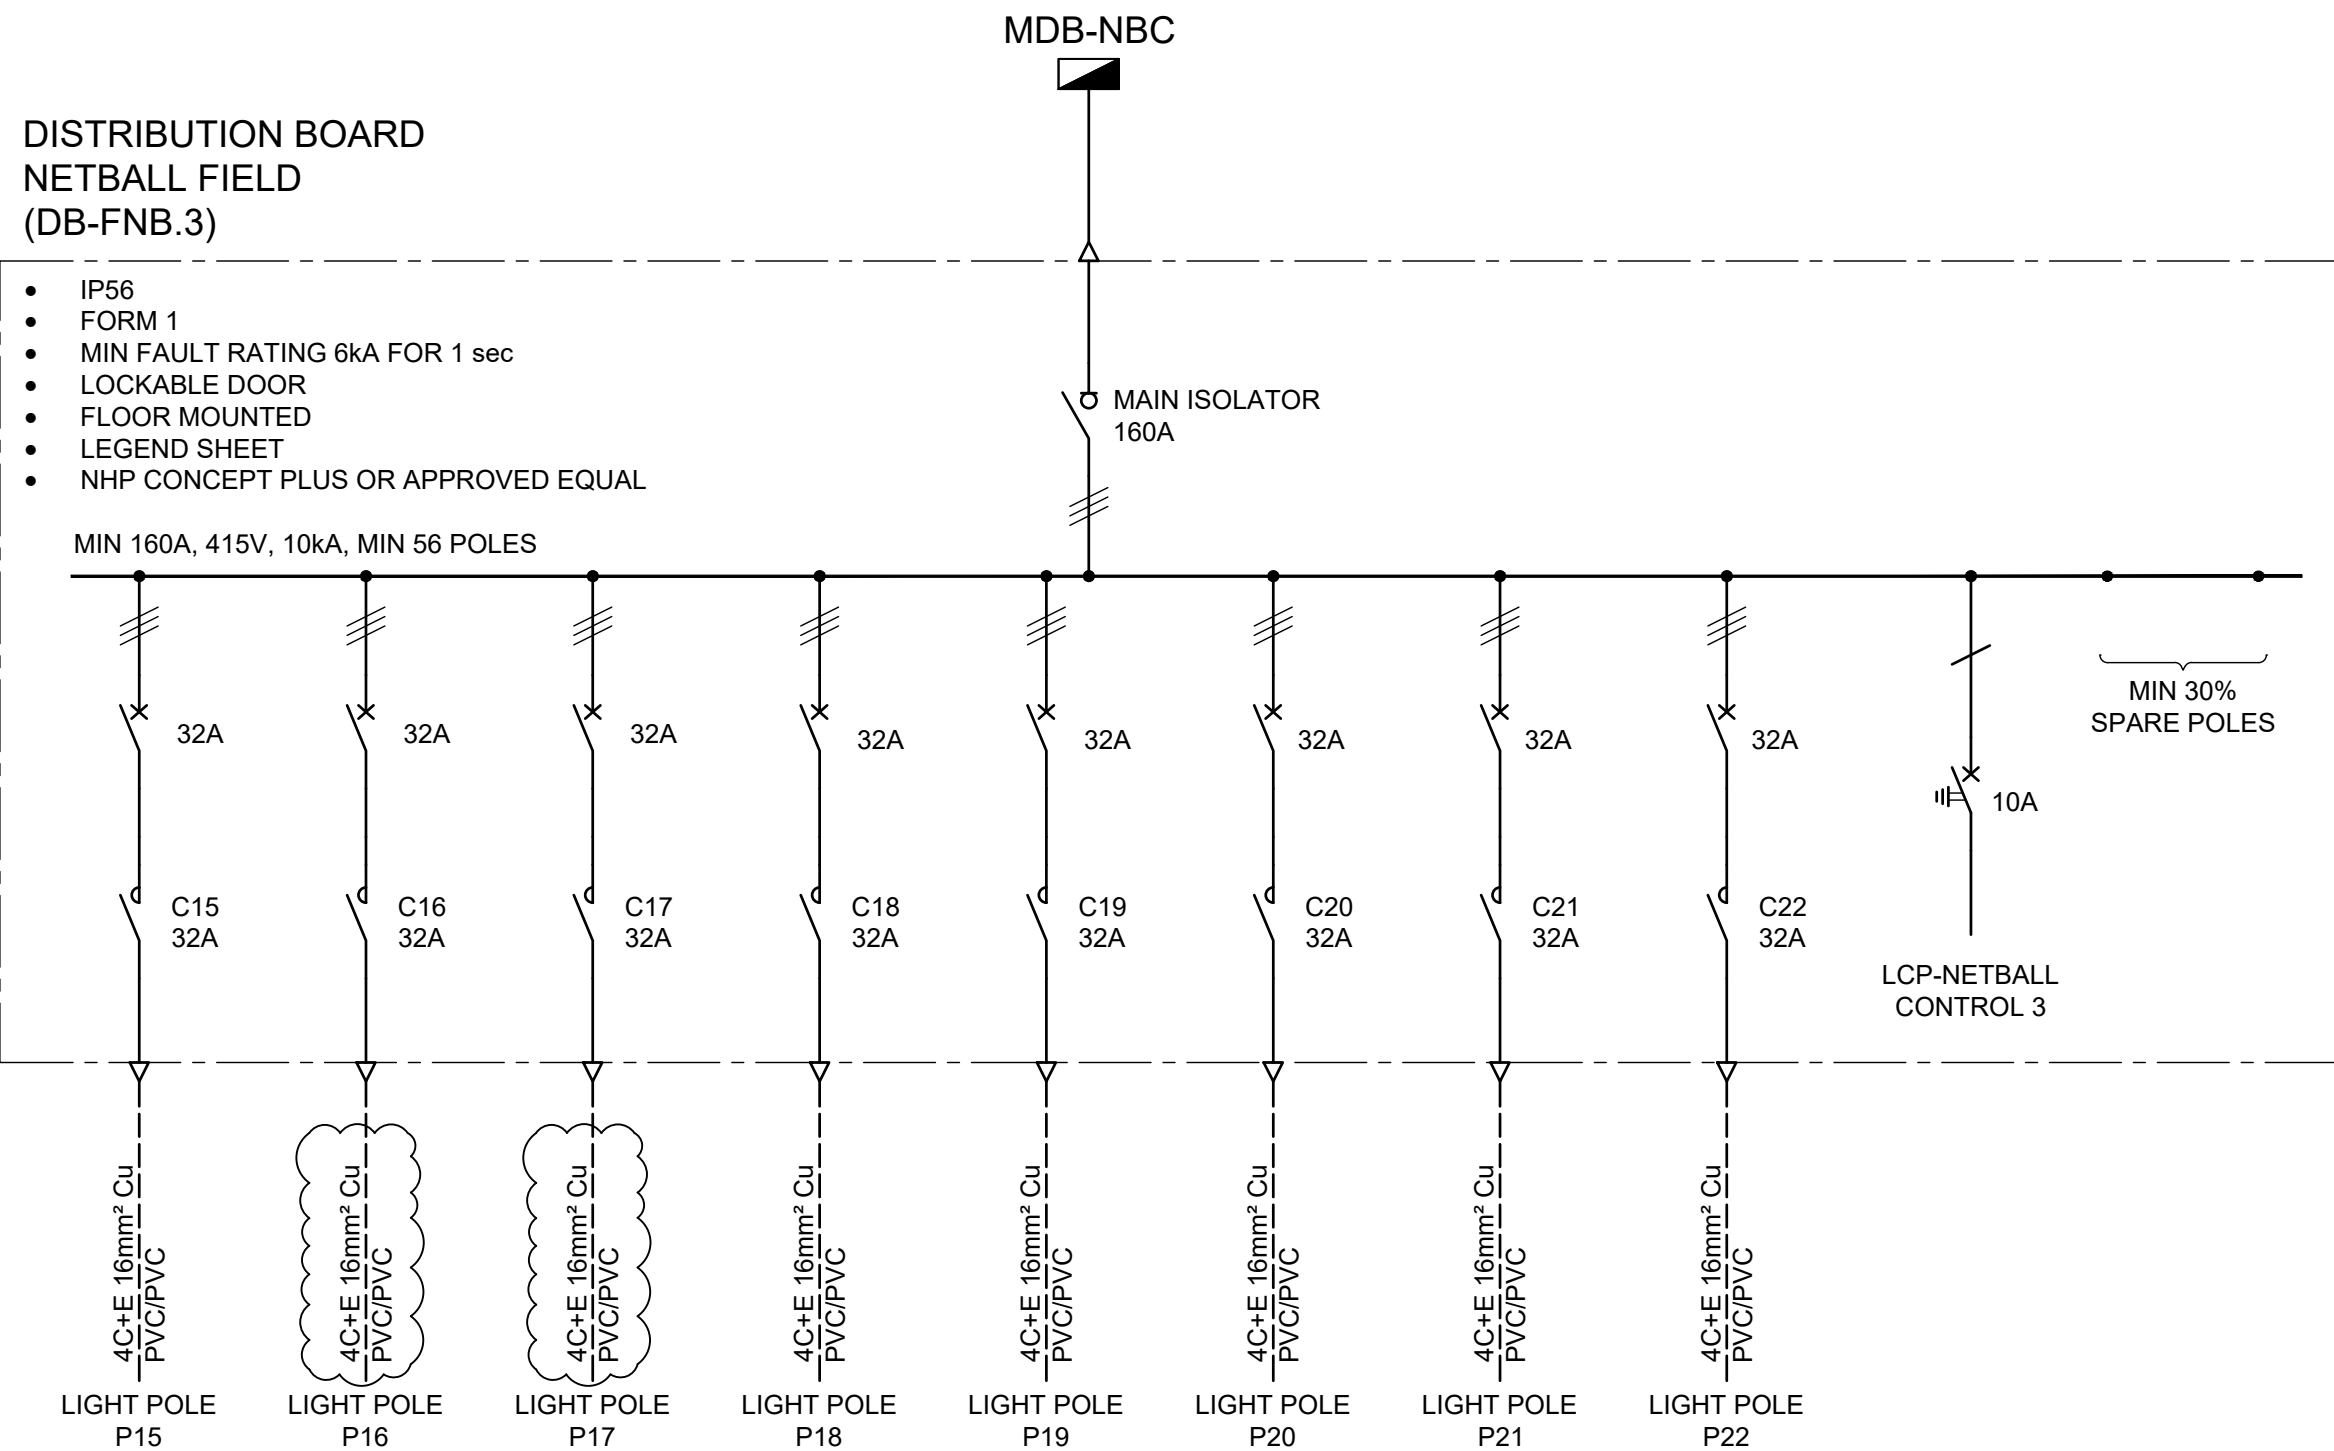

**NETBALL FIELD DISTRIBUTION
BOARD SLD (DB-FNB.3)**
NTS

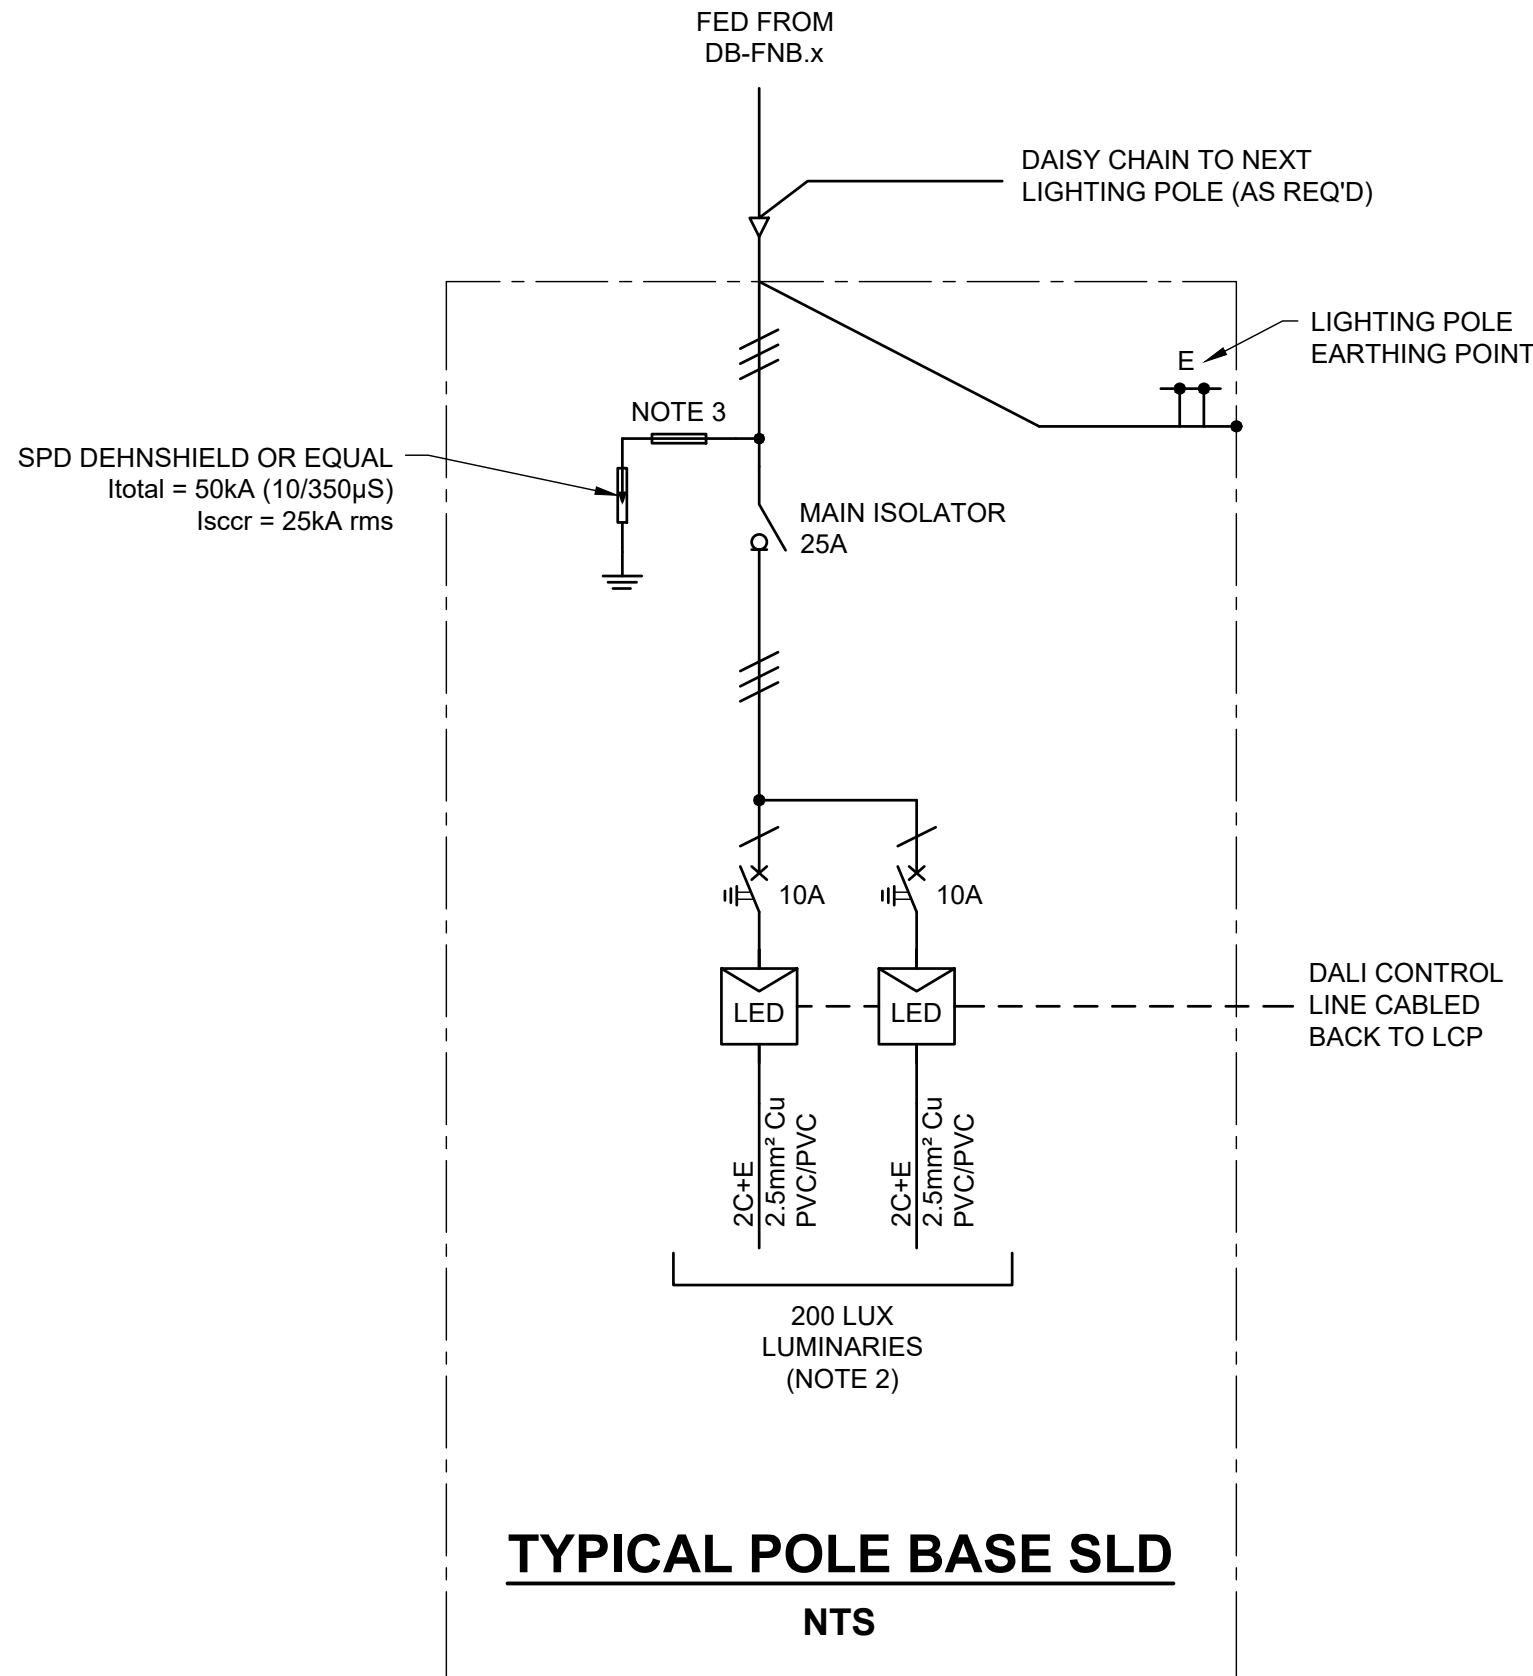

LIGHTING POLE NOTES:

1. LIGHTING CONTROL PANEL LABELS ARE TO BE WHITE TRAFFOLYTE WITH BLACK LETTERING.
2. ALL LUMINARIES SHALL BE FITTED WITH PROPRIETARY THERMAL PROTECTION AND WIRED TO REMOTE DRIVER.
3. SPD FUSE TO BE gG TYPE AND SIZED TO MANUFACTURERS REQUIREMENTS.

ALL DIMENSIONS SHOWN IN MM. DO NOT SCALE FROM DRAWINGS.
DIMENSIONS TAKE PRECEDENCE. IF IN DOUBT REFER TO HK SOLUTIONS.

FOR TENDER

T2	UPDATED ISSUE FOR TENDER	10/07/26	AF	HKS	ENGINEERING PROJECT MANAGEMENT DARWIN. GEELONG. CAIRNS. TOWNSVILLE. PERTH. BALLARAT admin@hksolutions.com.au www.hksolutions.com.au
T1	ISSUE FOR TENDER	17/06/26	AF	HKS	
REV.	DESCRIPTION	DATE	INIT.	COMPANY	Conditions of use. This document may only be used by Harris Kmon Solutions clients for the purpose for which it was prepared and must not be used by any other person or for any other purpose.
REVISIONS					

SPORTENG™

DRAWN	AF
CHECKED	ABM
DESIGNED	AF
CHECKED	--
APPROVED	--
Date Approved	--
THIS DRAWING MUST NOT BE USED FOR CONSTRUCTION UNLESS SIGNED AS APPROVED	

STAGE 1
ROCKHAMPTON NETBALL CENTRE - SITE LAYOUT
554-700 YAAMBA ROAD, NORMAN GARDEN - 4701
NETBALL LIGHTING SLD & SCHEMATICS

PAGE No	PROJECT No - DRAWING No	DISCIPLINE	REV.	SHEET SIZE
12 OF 16	25015 -E-SITE-304	ELECTRICAL	T2	A1